


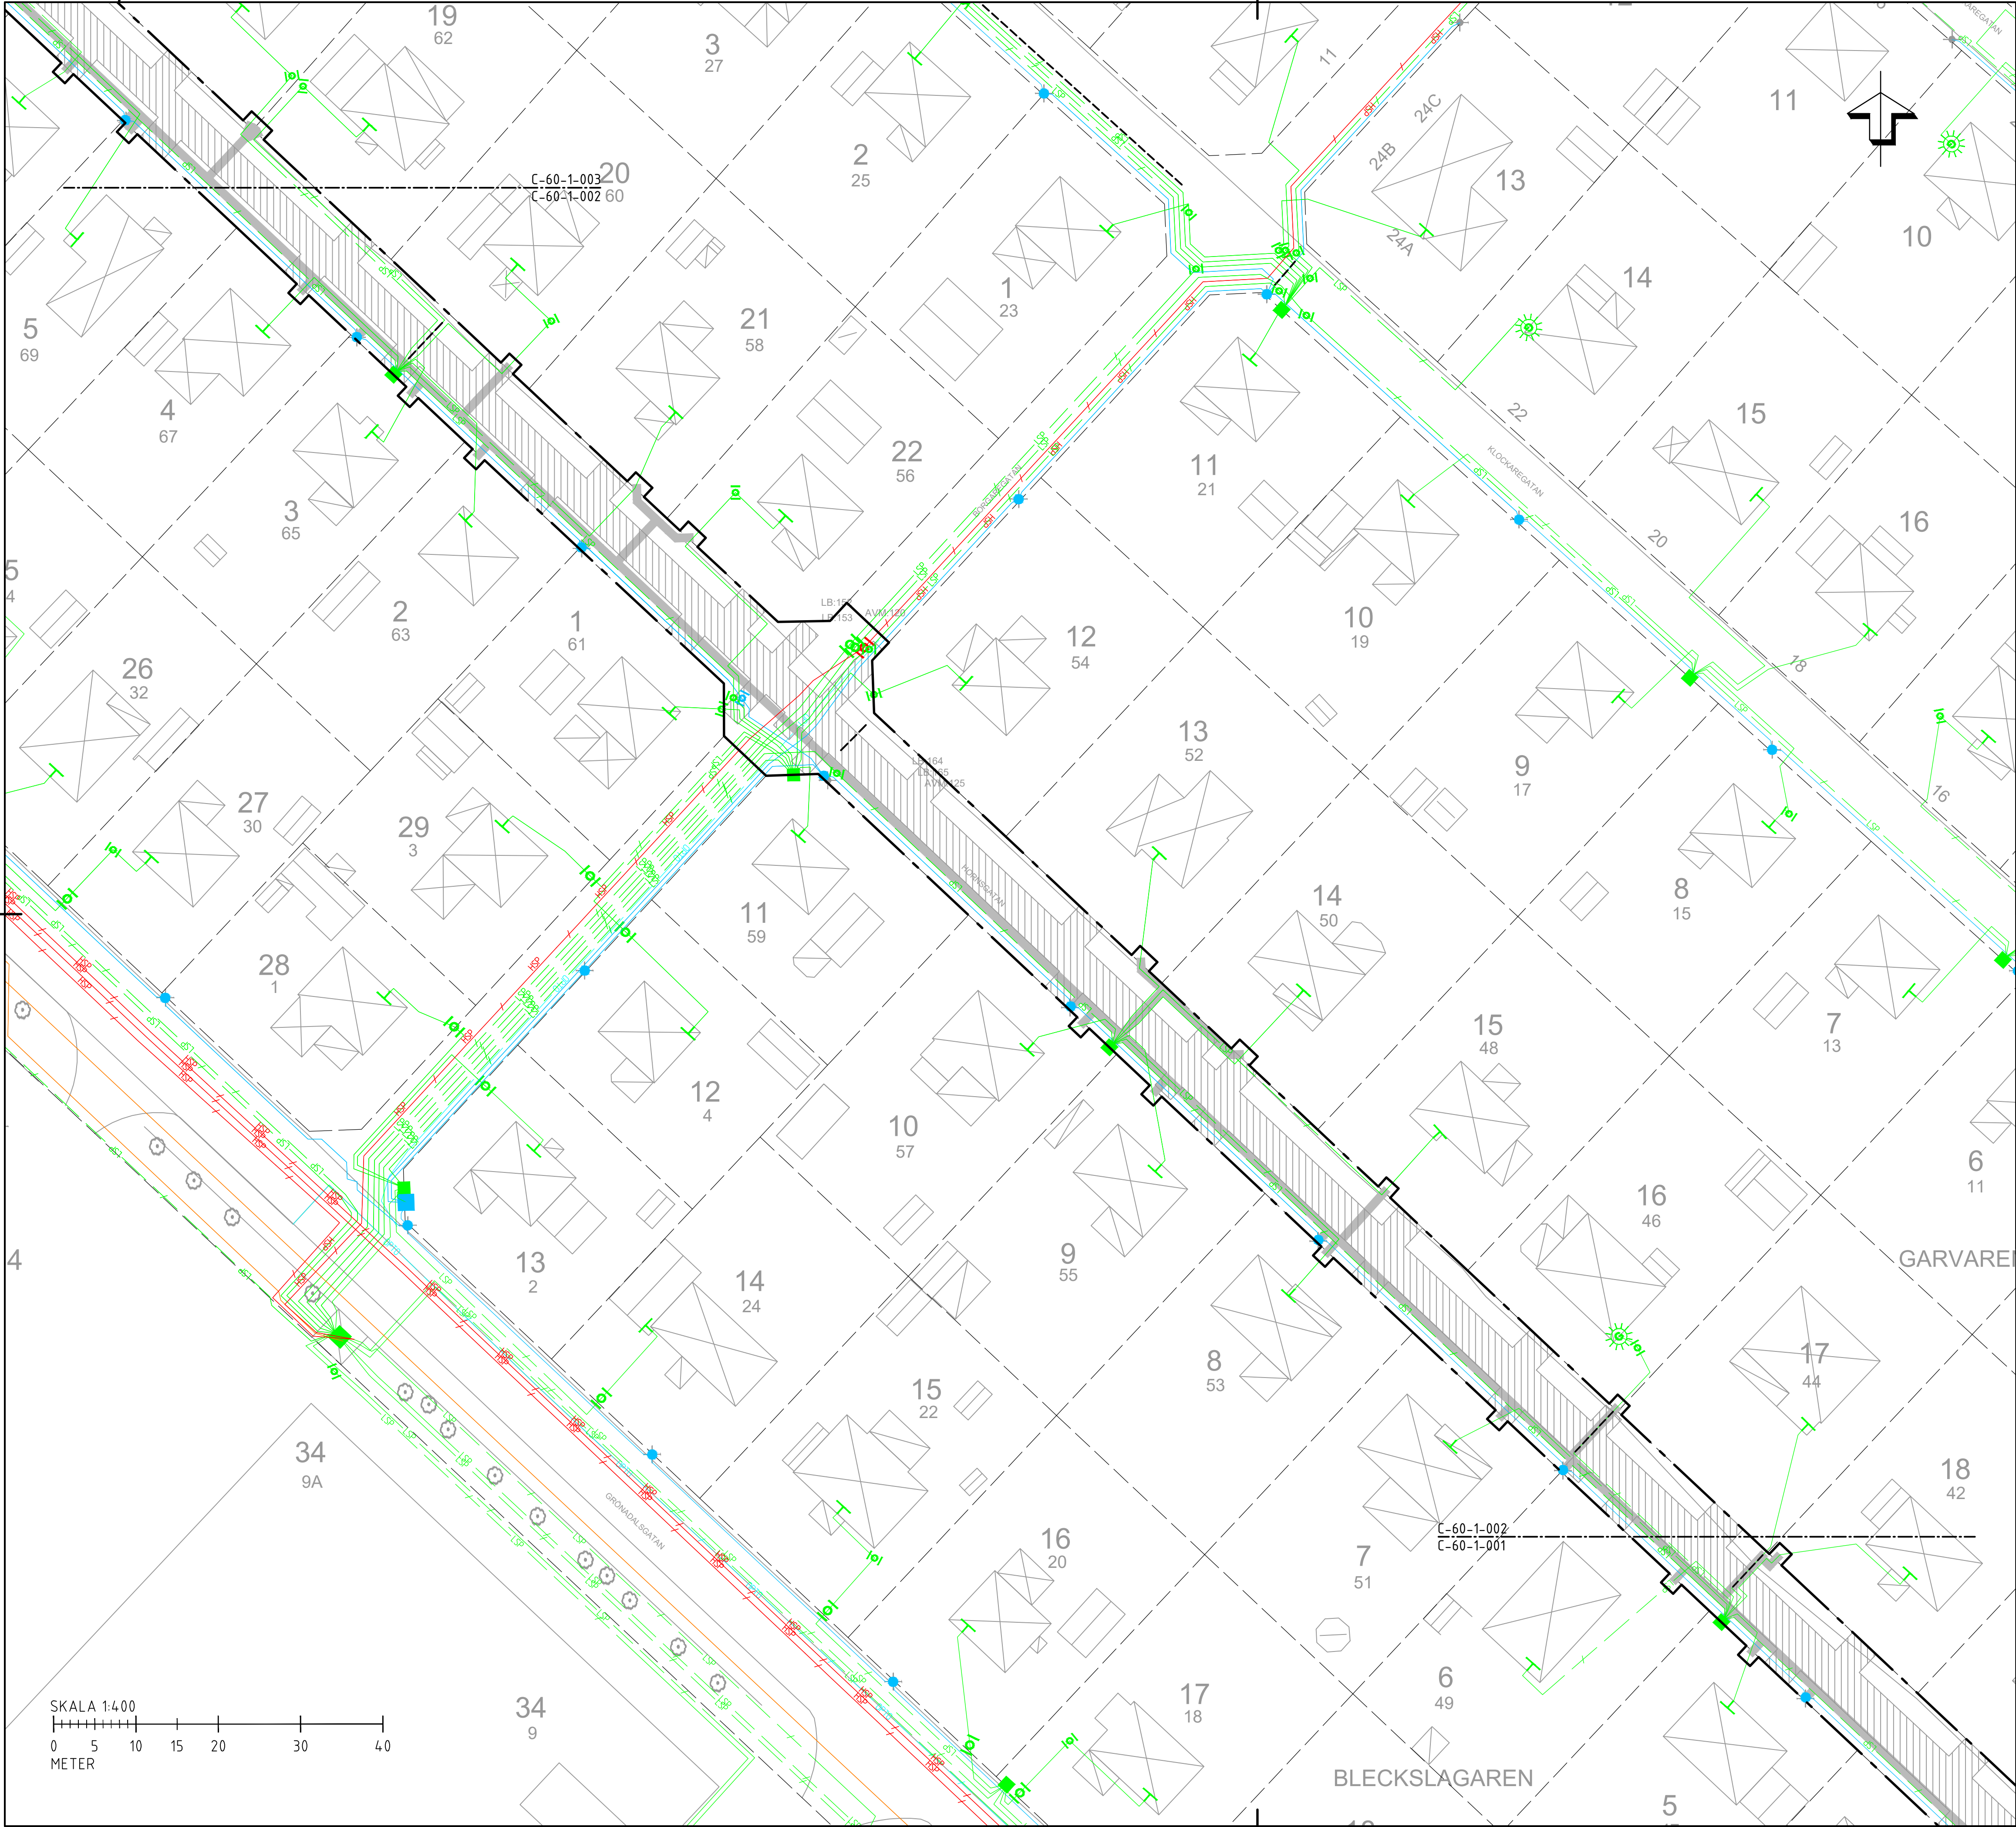


TECKENFÖRKLARING

- Bef. Belysningskabel
- Bef. Lågspänningskabel
- Bef. Högspänningskabel
- Bef. Optokabel
- Bef. Telekabel
- Bef. Skydds rör
- Fastighetsgräns
- Ny VA-schakt
- Ny el-schakt
- Arbetsområdesgräns

KOORDINATSYSTEM

PLAN: SWEREF 991630
HÖJD: RH2000

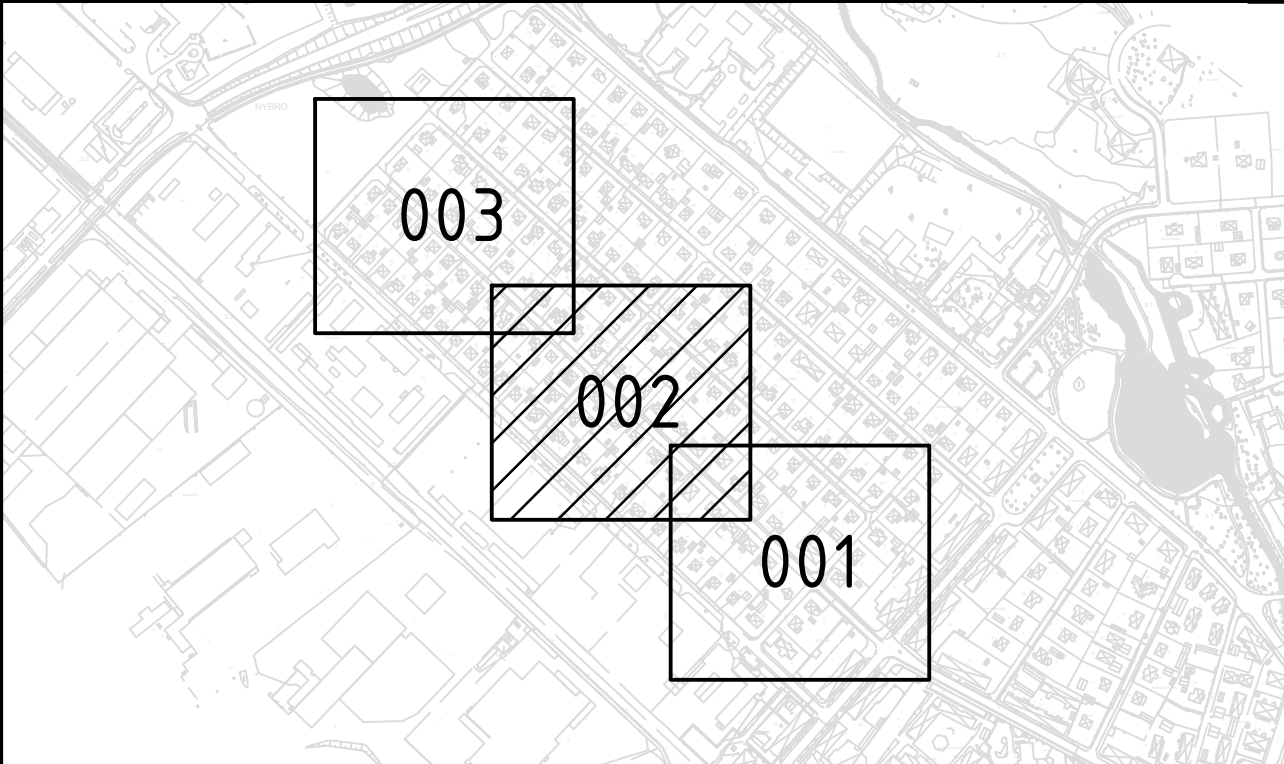

BET	ANT	ÄNDRINGEN AVSER	SIGN	DATUM
FÖRFRÅGNINGSUNDERLAG				
HORNSGATAN NYBRO				
 NYBRO ENERGI <i>ditt lokala energibolag</i>				
PROJEKT BYGGAREN				
UPPDRAG NR 8524.006	RITAD AV I. PÅLSSON TEL:		HANDLÄGGARE J. WIJK TEL:	
DATUM 2025-02-10	ANSVARIG J. WIJK			
SANERING AV VA-LEDNINAGR SAMT EL- OCH BELYSNINGSKABLAR BEFINTLIGA KABLAR PLAN				
SKALA (A1/A3) 1:400	NUMMER C-60-1-002			I BET