


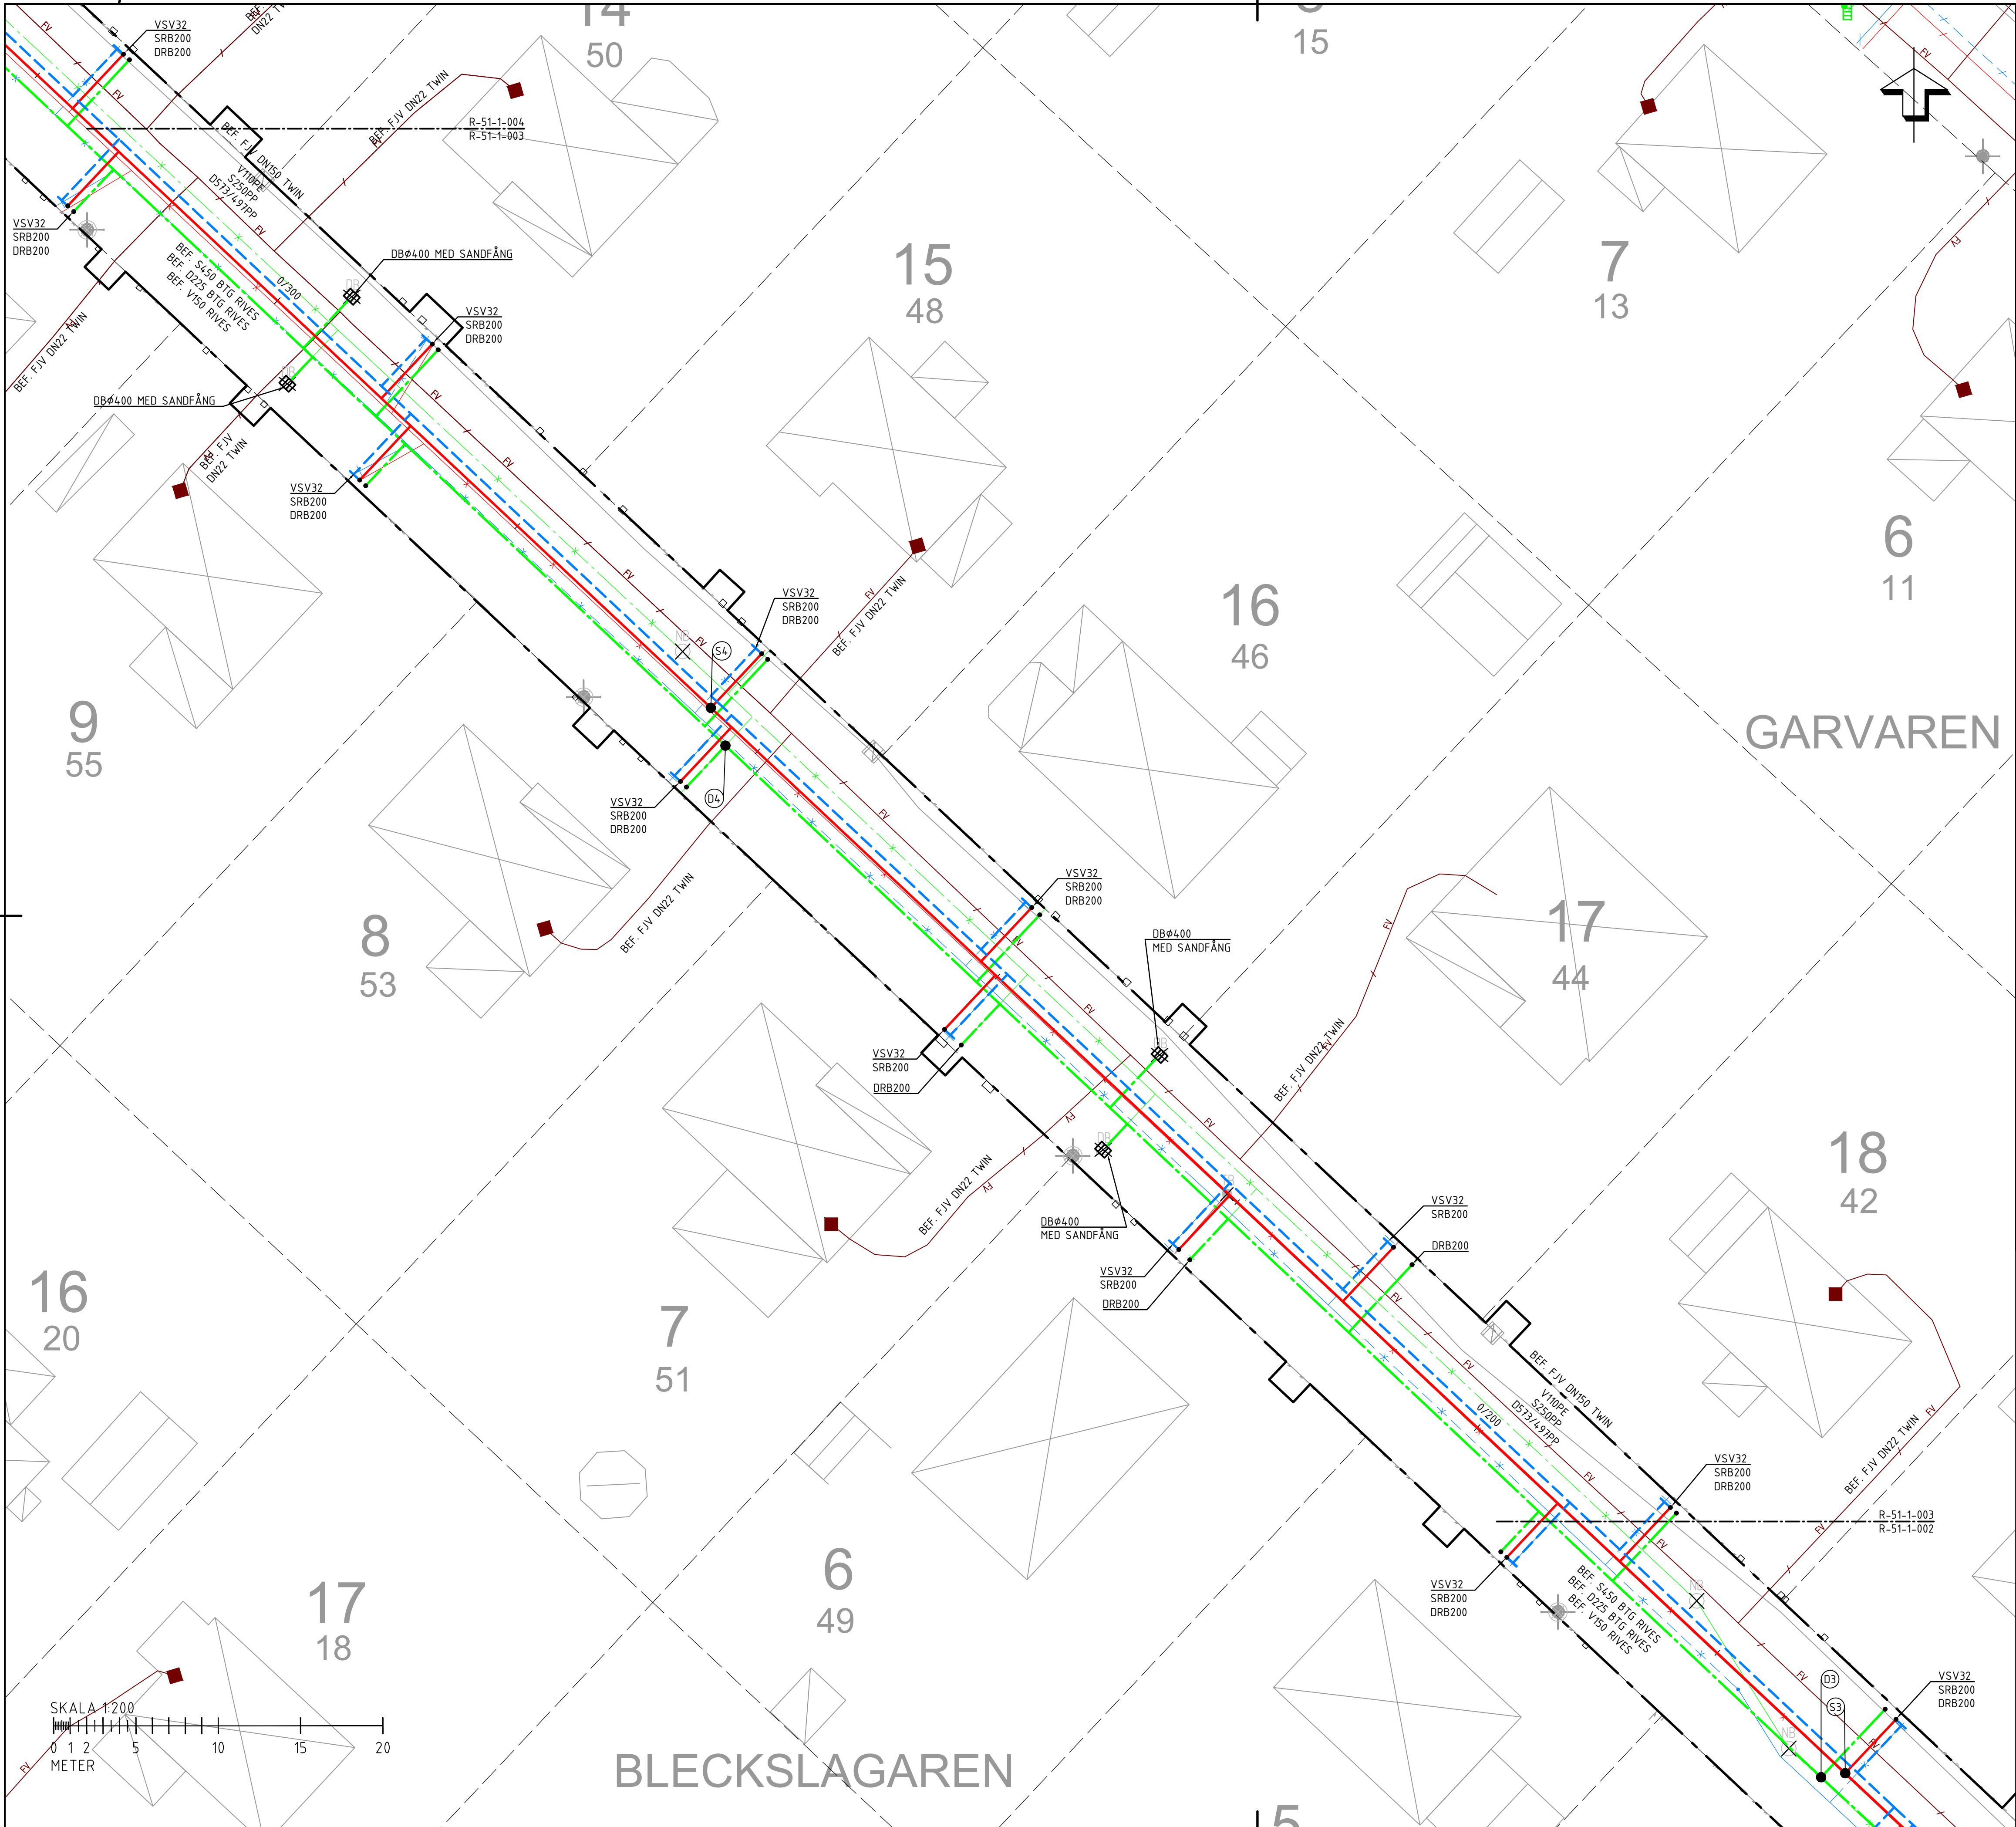

TECKENFÖRKLARING


- BEF. DAGVATTENLEDNING UTGÅR/RIVES
- BEF. SPILLV. LEDNING UTGÅR/RIVES
- BEF. VATTENLEDNING UTGÅR/RIVES
- BEF. DAGVATTENLEDNING
- BEF. SPILLVATTENLEDNING
- BEF. VATTENLEDNING
- BEF. FJÄRRVÄRMELEDNING
- FASTIGHETSGRÄNS
- NY DAGVATTENLEDNING
- NY SPILLVATTENLEDNING
- NY VATTENLEDNING
- ARBETSOMRÅDESGRÄNS
- KONNEKTIONSLINJE
- BEF. ELSKÅP
- BEF. BRUNN
- BEF. BRUNN RIVES
- BEF. BRANDPOST
- BEF. BRANDPOST RIVES
- NY BRANDPOST
- NY AVSTÄNGNINGSVENTIL VATTEN
- NY NEDSTIGNINGSBRUNN
- NY TILLSYNSBRUNN/SADELBRUNN
- NY RENSBRUNN Ø200
- NY PROPPNING
- NY DAGVATTENBRUNN, GALLERBETÄCKNING

ANMÄRKNING

SERVISLEDNING UTANFÖR FASTIGHETSGRÄNS FÖR VATTEN SKA VARA DIM32 PE100 RC SDR11, SPILLVATTEN DIM110 PVC SN8 OCH DAGVATTEN DIM160 PVC SN8. NYA RENSBUNNAR OCH VENTILER PLACERAS 0.5M UTANFÖR FASTIGHETSGRÄNS.

KOORDINATSYSTEM

PLAN: SWREF 991630
HÖJD: RH2000

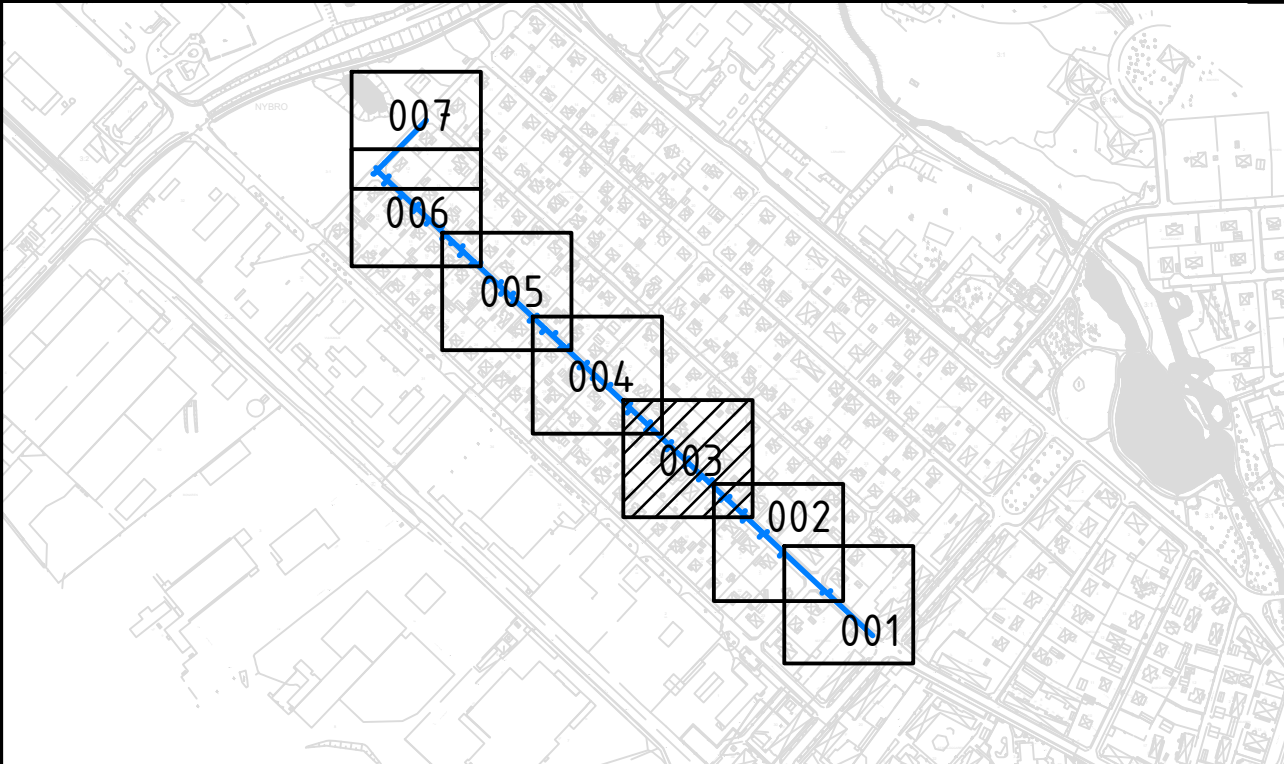

BET	ANT	ÄNDRINGEN AVSER	SIGN	DATUM
FÖRFRÅGNINGSUNDERLAG				
HORNSGATAN NYBRO				
 NYBRO ENERGI <i>ditt lokala energibolag</i>				
PROJEKT BYGGAREN				
UPPDRAG NR 8524006	RITAD AV I. P/H. K		HANDLÄGGARE J. WIJK	
DATUM 2025-02-10	ANSVARIG J. WIJK		TEL:	
SANERING AV VA-LEDNINGAR SAMT EL- OCH BELYSNINGSKABLAR				
PLAN				
SKALA (A1/A3) 1:200	NUMMER R-51-1-003		I BET	