
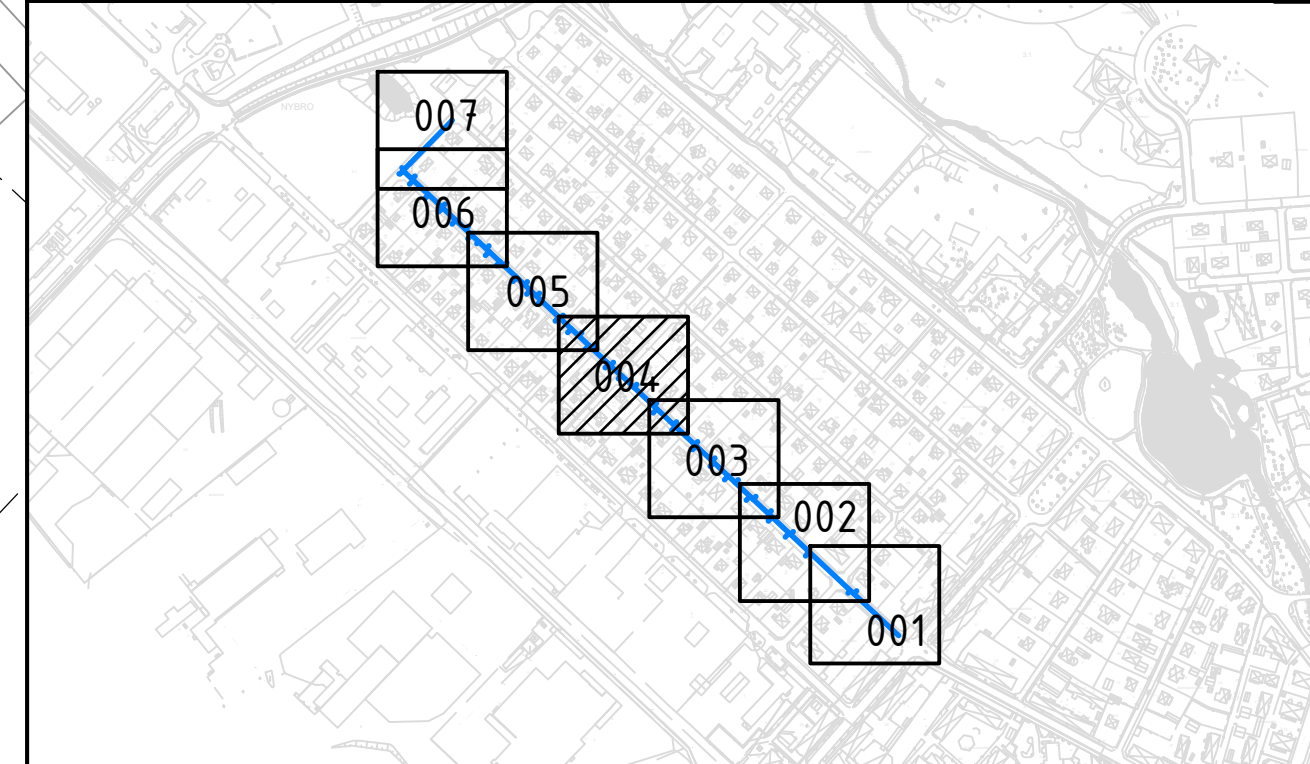


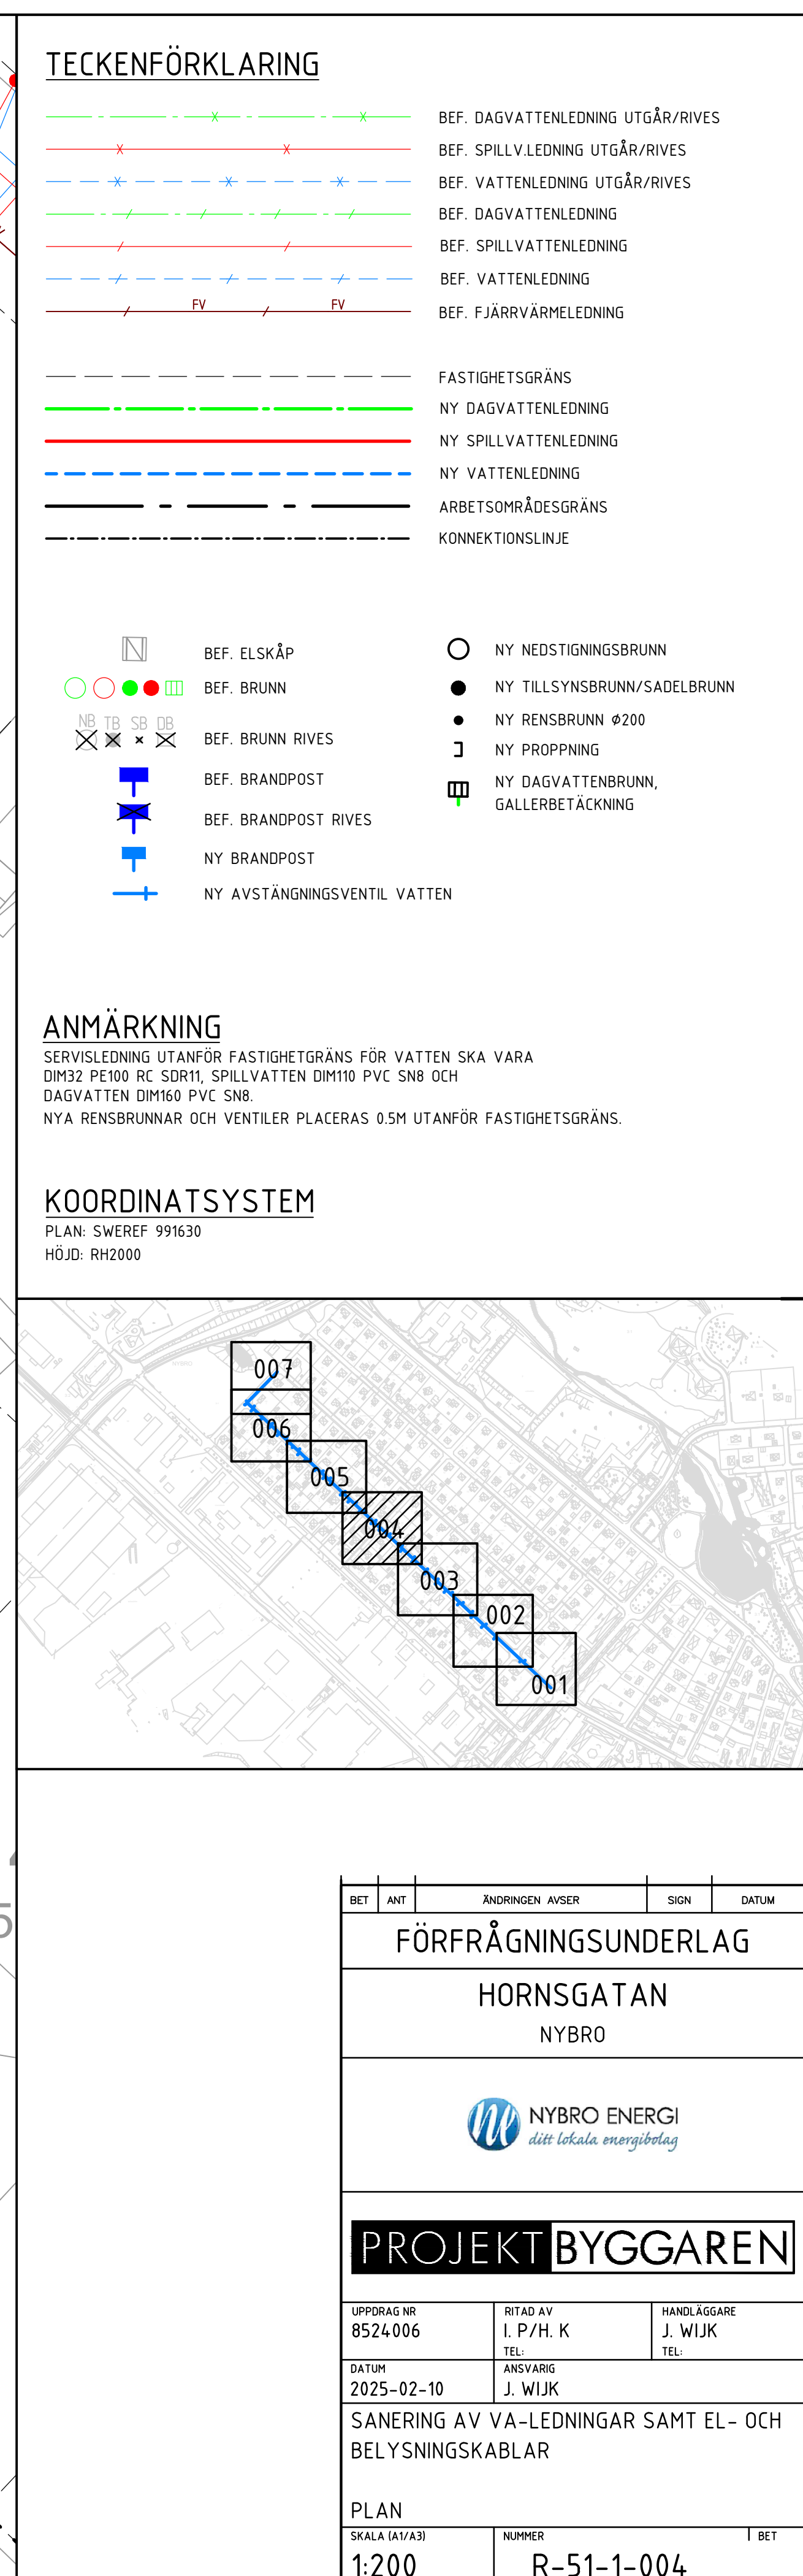

BET	ANT	ÄNDRINGEN AVSER	SIGN	DATUM
FÖRFRÅGNINGSUNDERLAG				
HORNSGATAN				
NYBRO				
 NYBRO ENERGI <i>ditt lokala energibolag</i>				
PROJEKT BYGGGAREN				
UPPDRAG NR 8524-006		RITAD AV I. P/H. K		HANDLÄGGARE J. WIJK
DATUM 2025-02-10		ANSVARIG J. WIJK		TEL:
SANERING AV VA-LEDNINGAR SAMT EL- OCH BELYSNINGSKABLAR				
PLAN				
SKALA (A1/A3)		NUMMER		BET
1:200		R-51-1-004		