


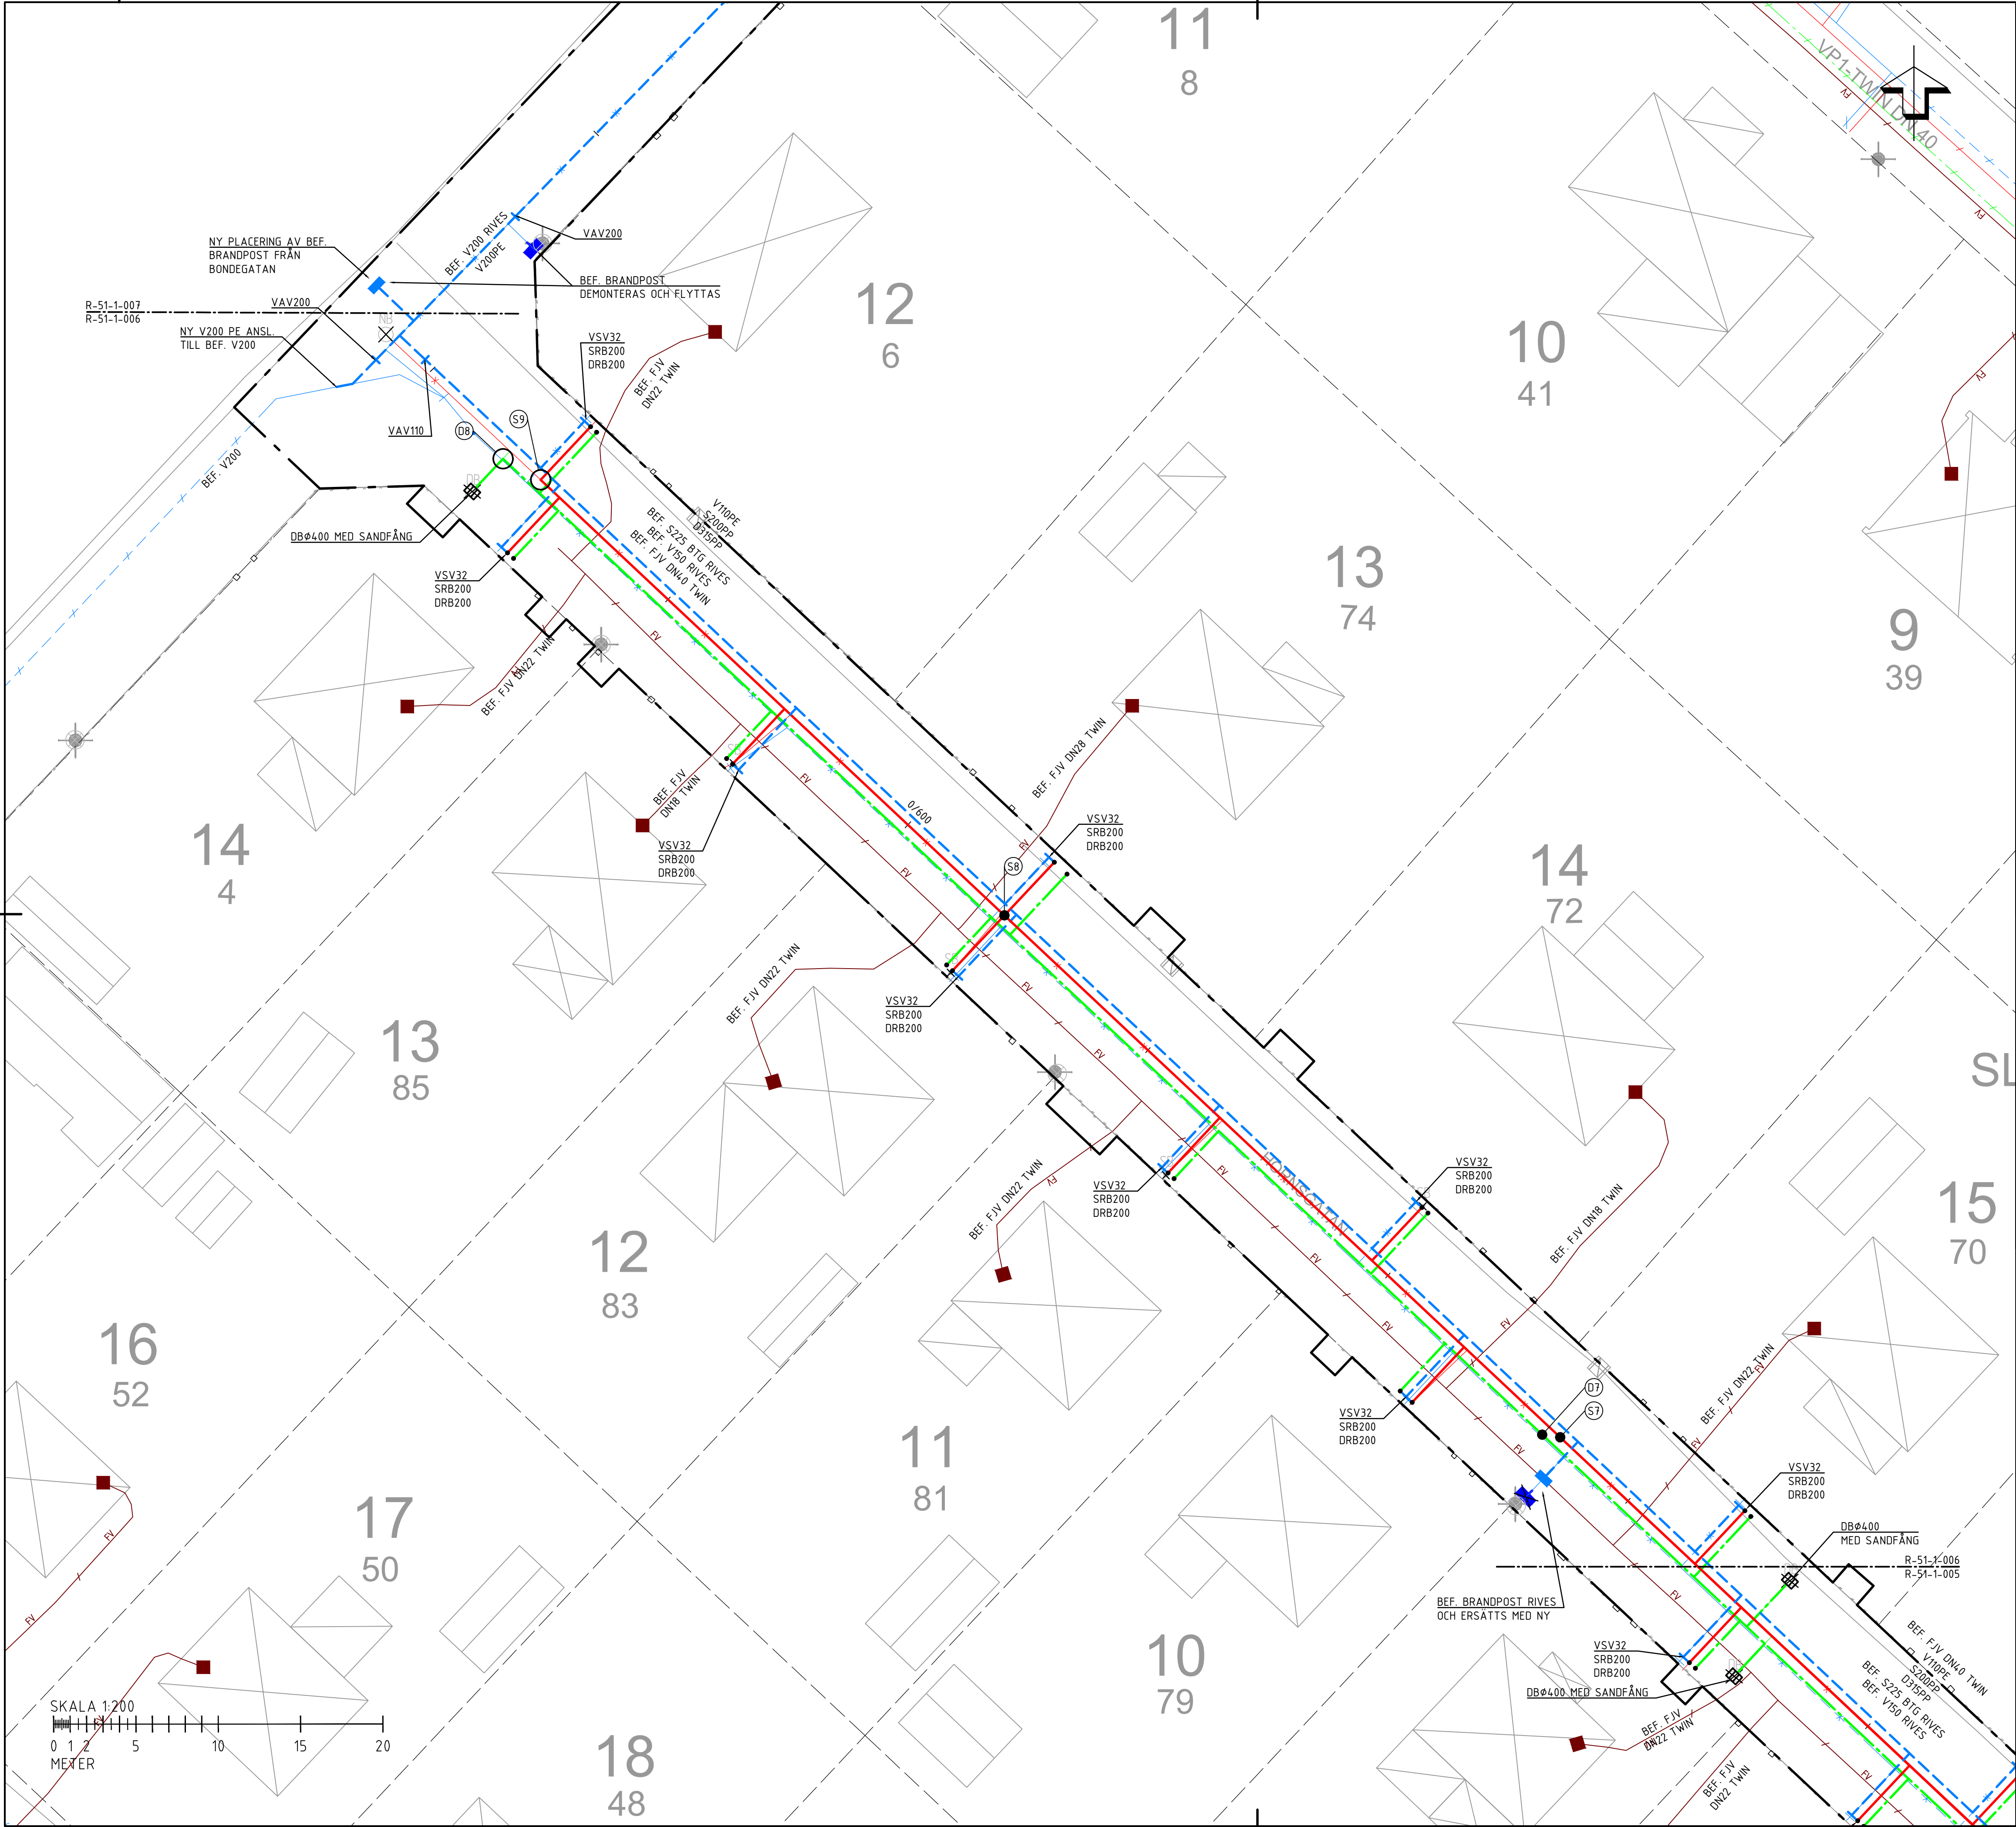

TECKENFÖRKLARING

	BEF. DAGVATTENLEDNING UTGÅR/RIVES
	BEF. SPILLV.LEDNING UTGÅR/RIVES
	BEF. VATTENLEDNING UTGÅR/RIVES
	BEF. DAGVATTENLEDNING
	BEF. SPILLVATTENLEDNING
	BEF. VATTENLEDNING
	BEF. FJÄRRVÄRMELEDNING
	FASTIGHETSGRÄNS
	NY DAGVATTENLEDNING
	NY SPILLVATTENLEDNING
	NY VATTENLEDNING
	ARBETSOMRÅDESGRÄNS
	KONNEKTIONSLINJE

	BEF. ELSKÅP		NY NEDSTIGNSBRUNN
	BEF. BRUNN		NY TILLSYNSBRUNN/SADELBRUNN
	BEF. BRUNN RIVES		NY RENSBRUNN Ø200
	BEF. BRUNN RIVES		NY PROPPNING
	BEF. BRANDPOST		NY DAGVATTENBRUNN, GALLERBETÄCKNING
	BEF. BRANDPOST RIVES		
	NY BRANDPOST		
	NY AVSTÄNGNINGSVENTIL VATTEN		

ANMÄRKNING

SERVISLEDNING UTANFÖR FASTIGHETGRÄNS FÖR VATTEN SKA VARA DIM32 PE100 RC SDR11, SPILLVATTEN DIM110 PVC SN8 OCH DAGVATTEN DIM160 PVC SN8.
NYA RENSBRUNNAR OCH VENTILER PLACERAS 0.5M UTANFÖR FASTIGHETSGRÄNS.

KOORDINATSYSTEM

PLAN: SWEREF 991630
HÖJD: RH2000

BET	ANT	ÄNDRINGEN AVSER	SIGN	DATUM
FÖRFRÅGNINGSUNDERLAG				
HORNSGATAN NYBRO				
NYBRO ENERGI ditt lokala energibolag				
PROJEKT BYGGAREN				
UPPDRAG NR 8524.006	RITAD AV I. P./H. K TEL:	HANDLÄGGARE J. WIJK TEL:		
DATUM 2025-02-10	ANSVARIG J. WIJK			
SANERING AV VA-LEDNINGAR SAMT EL- OCH BELYSNINGSKABLAR				
PLAN				
SKALA (A1/A3) 1:200	NUMMER R-51-1-006	I BET		