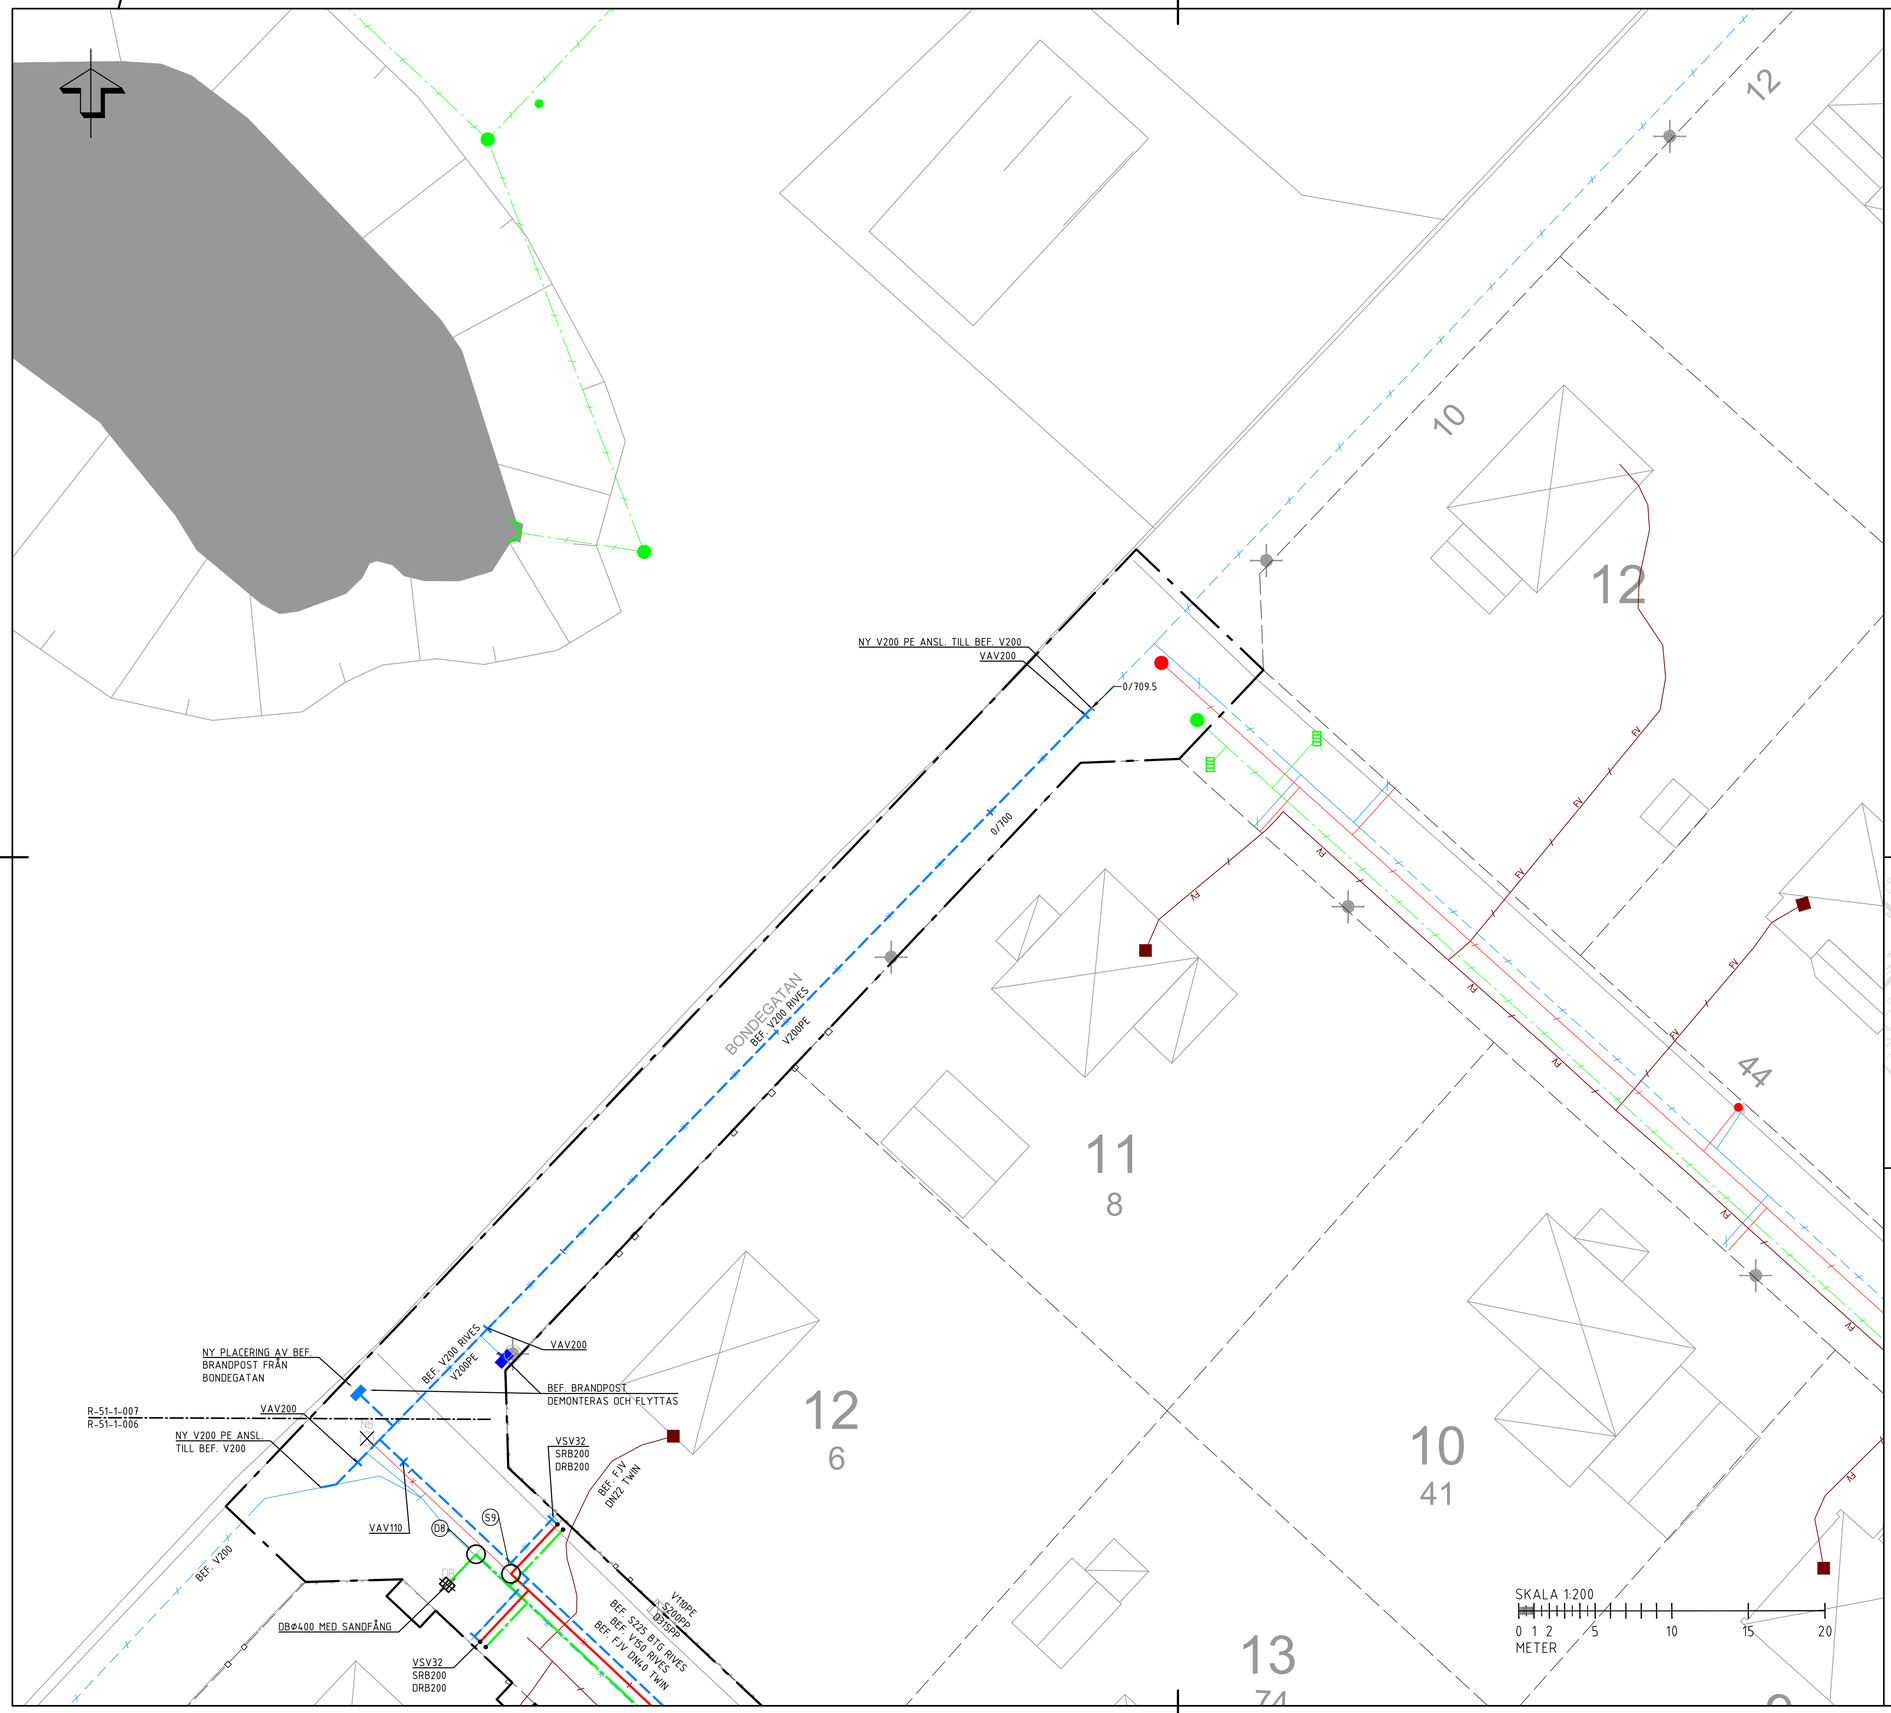

TECKENFÖRKLARING

- BEF. DAGVATTENLEDNING UTGÅR/RIVES
- BEF. SPILLV.LEDNING UTGÅR/RIVES
- BEF. VATTENLEDNING UTGÅR/RIVES
- BEF. DAGVATTENLEDNING
- BEF. SPILLVATTENLEDNING
- BEF. VATTENLEDNING
- BEF. FJÄRRVÄRMELEDNING
- FASTIGHETSGRÄNS
- NY DAGVATTENLEDNING
- NY SPILLVATTENLEDNING
- NY VATTENLEDNING
- ARBETSOMRÅDESGRÄNS
- KONNEKTIONSLINJE

- BEF. ELSKÅP
- BEF. BRUNN
- BEF. BRUNN RIVES
- BEF. BRANDPOST
- BEF. BRANDPOST RIVES
- NY BRANDPOST
- NY AVSTÄNGNINGSVENTIL VATTEN
- NY NEDSTIGNINGSBRUNN
- NY TILLSYNSBRUNN/SADELBRUNN
- NY RENSBRUNN Ø200
- NY PROPPNING
- NY DAGVATTENBRUNN, GALLERBETÄCKNING

ANMÄRKNING

SERVISLEDNING UTANFÖR FASTIGHETGRÄNS FÖR VATTEN SKA VARA DIM32 PE100 RC SDR11, SPILLVATTEN DIM110 PVC SN8 OCH DAGVATTEN DIM160 PVC SN8.
NYA RENSBRUNNAR OCH VENTILER PLACERAS 0.5M UTANFÖR FASTIGHETSGRÄNS.

KOORDINATSYSTEM

PLAN: SWEREF 991630
HÖJD: RH2000

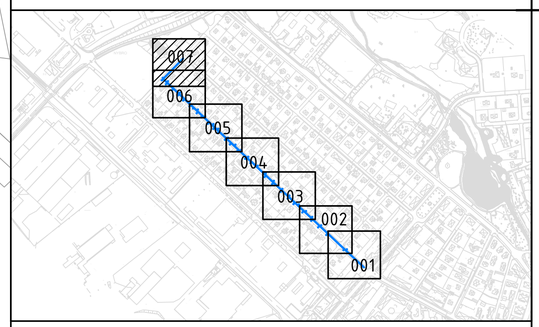

BET	ANT	ÄNDRINGEN AVSER	SIGN	DATUM

FÖRFRÅGNINGSUNDERLAG

HORNSGATAN
NYBRO

NYBRO ENERGI
ditt lokala energibolag

PROJEKT BYGGAREN

UPPDRAG NR	RITAD AV	HANDLÄGGARE
8524006	I. P/H. K TEL:	J. WIJK TEL:
DATUM	ANSVARIG	
2025-02-10	J. WIJK	

SANERING AV VA-LEDNINGAR SAMT EL- OCH BELYSNINGSKABLAR

PLAN

SKALA (A1/A3)	NUMMER	BET
1:200	R-51-1-007	