

TECKENFÖRKLARING

- VÄG/GATA  
NY DAGVLEDNING  
NY SPILLVLEDNING  
NY VATTENLEDNING

- NY BRUNN FÖR DAGVATTEN OCH SPILLVATTEN  
NY AVSTÄNGNINGSVENTIL FÖR VATTEN  
NY BRANDPOST

ANMÄRKNING:


OM INGET ANNAT ANGES SKA SERVISLEDNING  
UTANFÖR FASTIGHETGRÄNS FÖR VATTEN VARA  
DIM32 PE100 RC SDR11,  
SPILLVATTEN DIM110 PVC SN8  
OCH DAGVATTEN DIM160 PVC SN8.

KOORDINATSYSTEM

PLAN: SWEREF 991630  
HÖJD: RH2000

PROFIL: Hornsgatan  
LÄNGDSKALA 1:200  
HÖJDSKALA 1:100

|              |                     |                      |                |
|--------------|---------------------|----------------------|----------------|
| LÄNGDMÄTNING |                     |                      |                |
| MARKSLAG     |                     | ASFALT               |                |
| PLANRITNING  |                     | R-51-1-001           |                |
| TYPSEKTION   |                     | R-51-N-001           |                |
| VATTEN       | MATERIAL & DIM I MM | V110 PE100 RC SDR 17 |                |
|              | VATTENGÅNG NIVÅ     | 83.78                | 84.10<br>84.10 |
| DAGVATTEN    | MATERIAL & DIM I MM | D895/785 PP SN8      |                |
|              | LUTNING I ‰         | 4.7‰                 | 5.1‰           |
|              | VATTENGÅNG NIVÅ     | 84.04                | 84.42<br>84.42 |
|              | MATERIAL & DIM I MM | S250 PP SN8          |                |
| SPILLVATTEN  | LUTNING I ‰         | 5.0‰                 | 5.0‰           |
|              | VATTENGÅNG NIVÅ     | 83.44                | 83.86<br>83.86 |

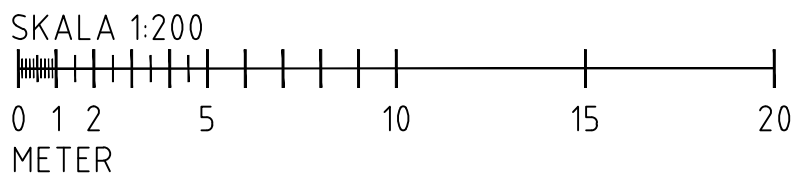

PROJEKT BYGGAREN

|                                                           |                                |                                |
|-----------------------------------------------------------|--------------------------------|--------------------------------|
| UPPDRAG NR<br>8524006                                     | RITAD AV<br>I. PÅLSSON<br>TEL: | HANDLÄGGARE<br>J. WIJK<br>TEL: |
| DATUM<br>2025-02-10                                       | ANSVARIG<br>J. WIJK            |                                |
| SANERING AV VA-LEDNINGAR SAMT EL- OCH<br>BELYSNINGSKABLAR |                                |                                |
| PROFIL                                                    |                                |                                |
| SKALA (A1/A3)                                             | NUMMER                         | BET                            |
| L=1:200, H=1:100                                          | R-51-2Q-001                    |                                |