

TECKENFÖRKLARING

- VÄG/GATA
NY DAGVLEDNING
NY SPILLVLEDNING
NY VATTENLEDNING



NY AVSTÄNGNINGSVENTIL FÖR VATTEN

NY BRANDPOST

ANMÄRKNING:


OM INGET ANNAT ANGES SKA SERVISLEDNING
UTANFÖR FASTIGHETGRÄNS FÖR VATTEN VARA
DIM32 PE100 RC SDR11,
SPILLVATTEN DIM110 PVC SN8
OCH DAGVATTEN DIM160 PVC SN8.

KOORDINATSYSTEM

PLAN: SWEREF 991630
HÖJD: RH2000

PROFIL: Hornsgatan
LÄNGDSKALA 1:200
HÖJDSKALA 1:100

LÄNGDMÄTNING	
MARKSLAG	ASFALT
PLANRITNING	R-51-1-003
TYPSEKTION	R-51-N-001
VATTEN	MATERIAL & DIM I MM VATTENGÅNG NIVÅ
	V110 PE100 RC SDR 17
	85.10 85.10
DAGVATTEN	MATERIAL & DIM I MM LUTNING I ‰
	5.0‰
	85.32 85.32
SPILLVATTEN	MATERIAL & DIM I MM LUTNING I ‰
	5.0‰
	84.76 84.76

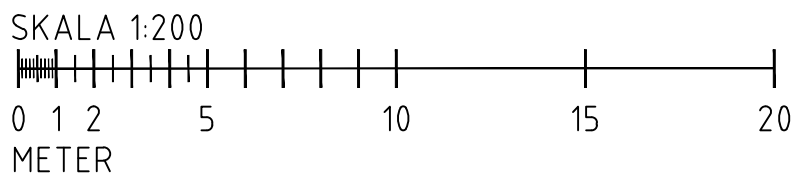

PROJEKTBYGGAREN

UPPDRAG NR 8524-006	RITAD AV I. PÅLSSON TEL:	HANDLÄGGARE J. WIJK TEL:
DATUM 2025-02-10	ANSVARIG J. WIJK	
SANERING AV VA-LEDNINGAR SAMT EL- OCH BELYSNINGSKABLAR		
PROFIL SKALA (A1/A3)	NUMMER	BET
L=1:200, H=1:100	R-51-2Q-003	