

TECKENFÖRKLARING

- VÄG/GATA
NY DAGVÄDNING
NY SPILLVÄDNING
NY VÄTTELEDNING

- NY BRUNN FÖR DAGVÄTTE OCH SPILLVÄTTE
NY AVSTÄNGNINGSVENTIL FÖR VÄTTE
NY BRANDPOST

ANMÄRKNING:

OM INGET ANNAT ANGES SKA SERVISELEDNING
UTANFÖR FASTIGHETGRÄNS FÖR VÄTTE VARA
DIM32 PE100 RC SDR11,
SPILLVÄTTE DIM110 PVC SN8
OCH DAGVÄTTE DIM160 PVC SN8.

KOORDINATSYSTEM

PLAN: SWEREF 991630
HÖJD: RH2000

BET	ANT	ÄNDRINGEN AVSER	SIGN	DATUM
-----	-----	-----------------	------	-------


FÖRFRÅGNINGSUNDERLAG

HORNSGATAN
NYBRÖ



PROJEKTBYGGAREN

UPPDRAG NR 8524-006	RITAD AV I. PÄLSSON TEL:	HANDLÄGGARE J. WIJK TEL:
DATUM 2025-02-10	ANSVARIG J. WIJK	
SANERING AV VÄ-LEDNINGAR SAMT EL- OCH BELYSNINGSKABLAR		
PROFIL		
SKALA (A1/A3) L=1:200, H=1:100	NUMMER	BET
R-51-2Q-005		

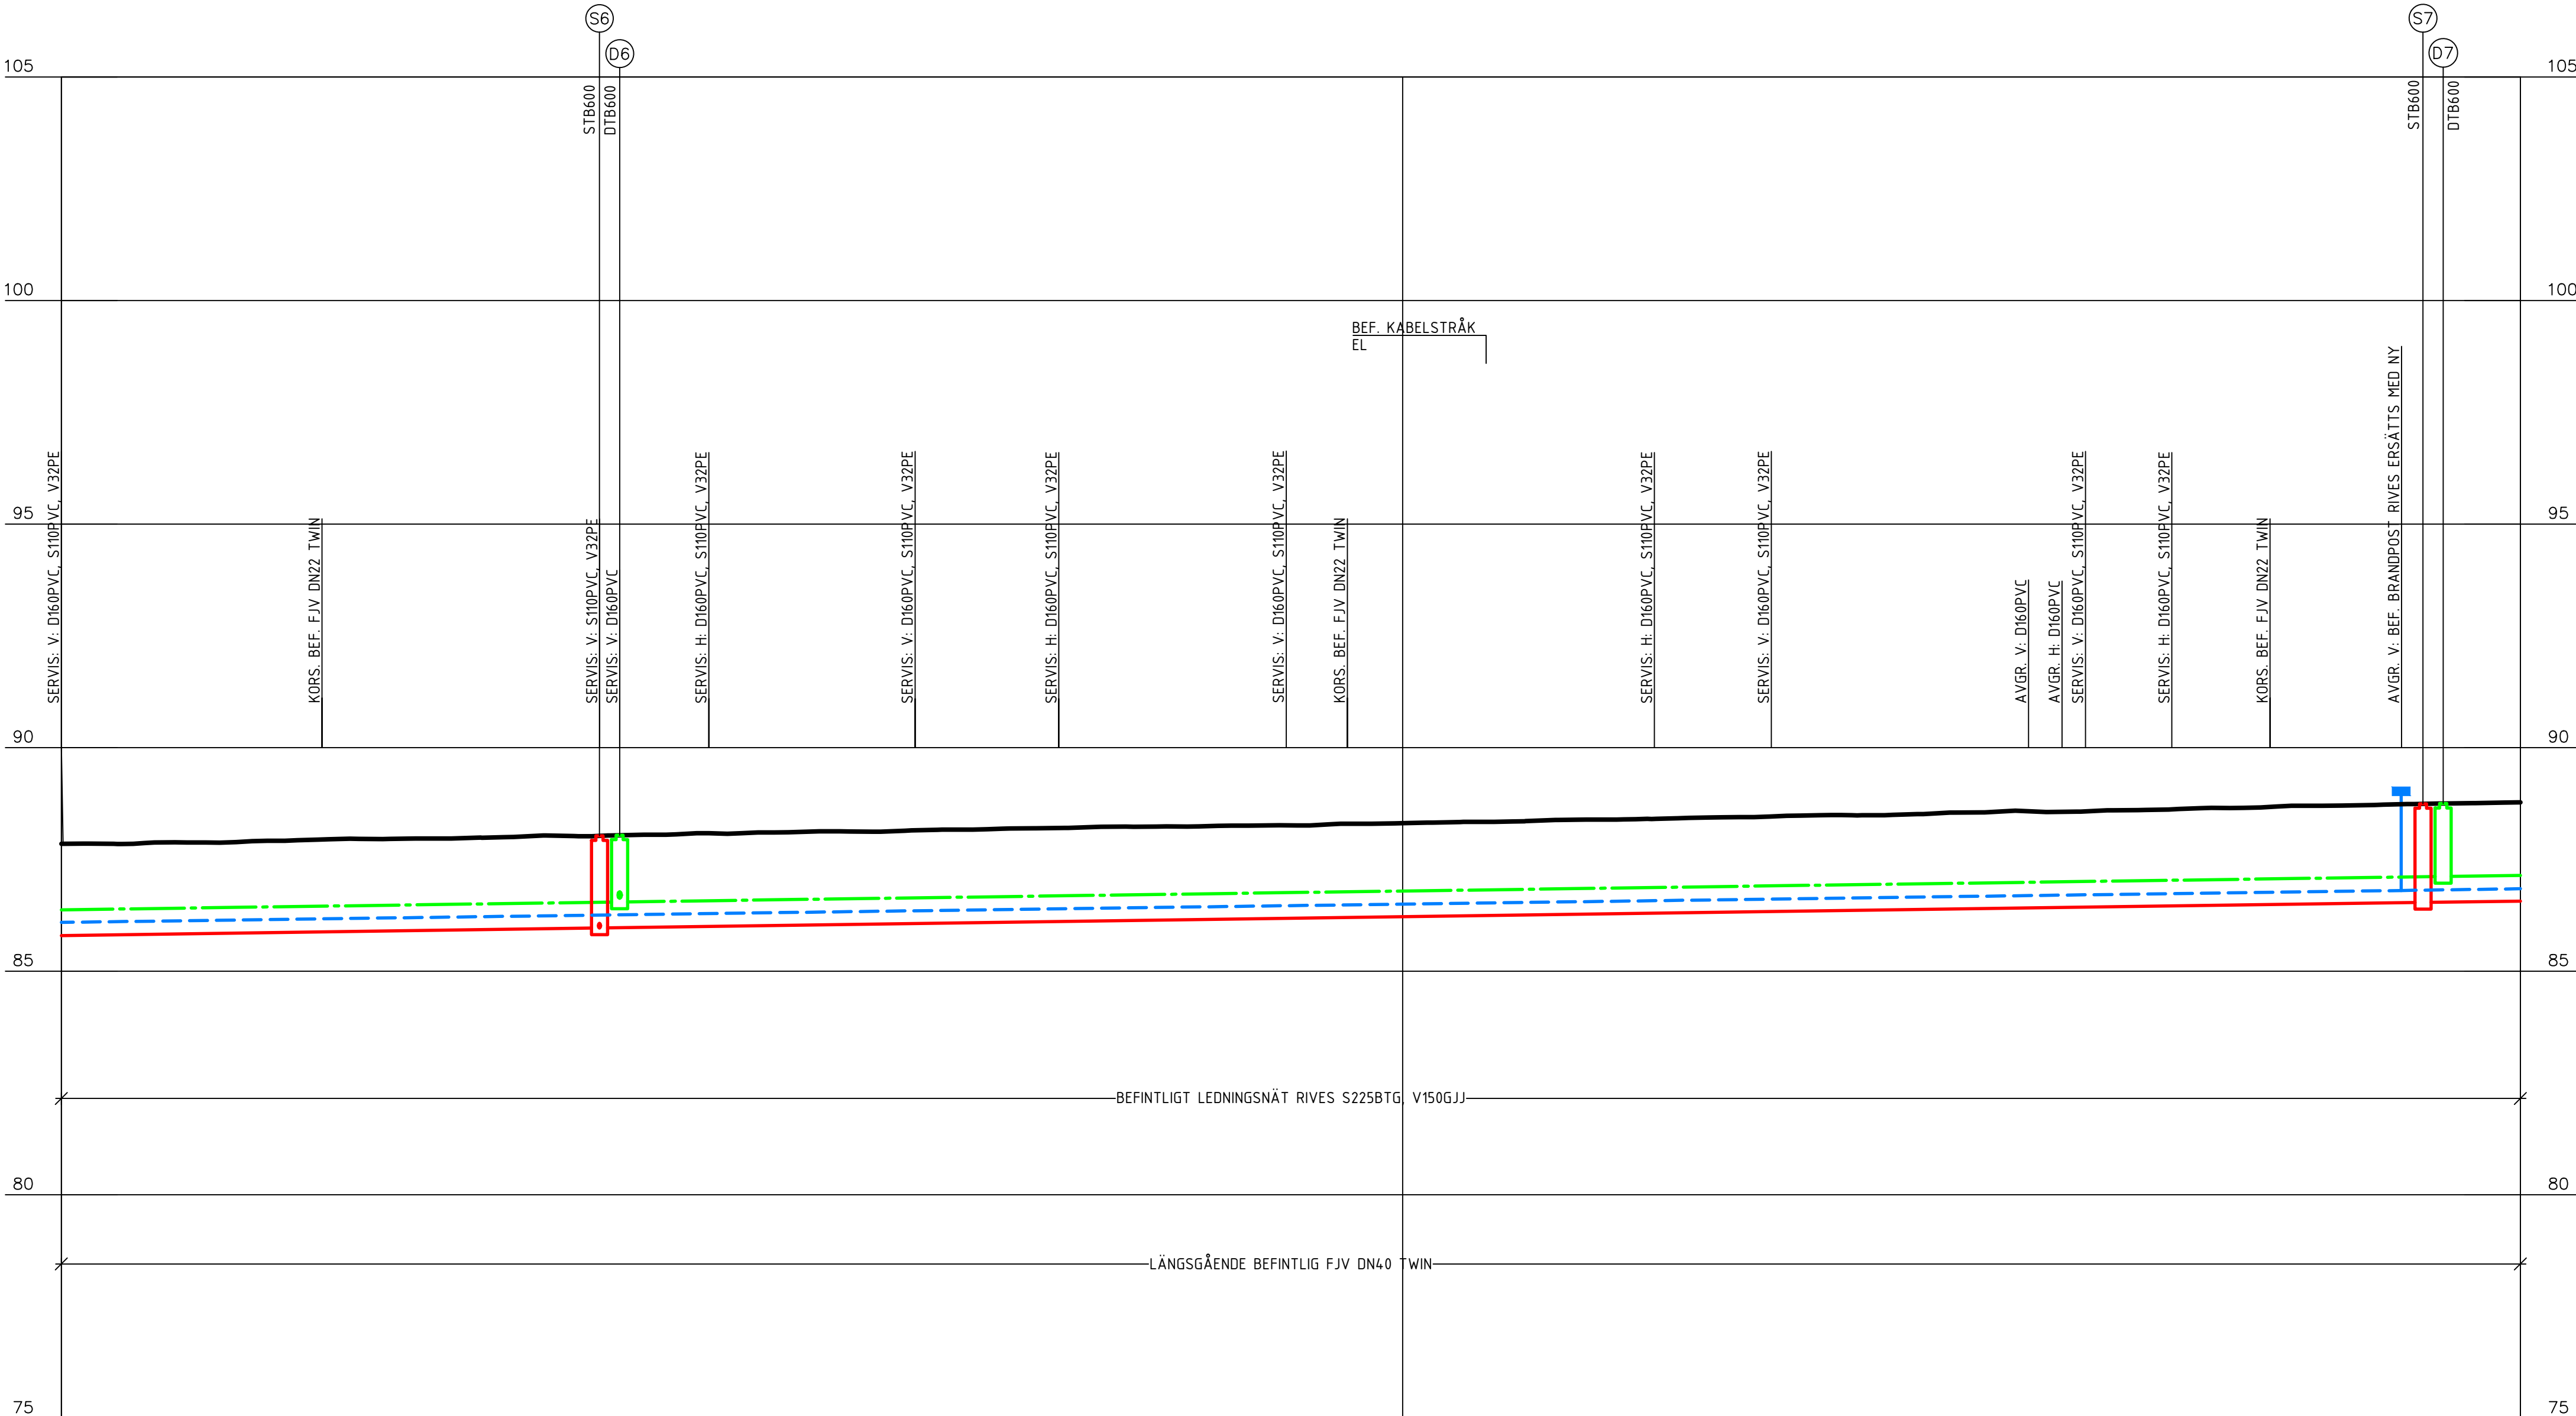

PROFIL: Hornsgatan
LÄNGDSKALA 1:200
HÖJDSKALA 1:100

LÄNGDMÄTNING			
MARKSLAG	ASFALT		
PLANRITNING	R-51-1-005		
TYPSEKTION	R-51-N-001		
VÄTTE	MATERIAL & DIM I MM VÄTTEGÄNG NIVÅ		
	V110 PE100 RC SDR 17		
	86.81		
DAGVÄTTE	MATERIAL & DIM I MM LUTNING I ‰		
	D315 PP SN8		
	7.0‰		
	VÄTTEGÄNG NIVÅ		
	86.55 86.55		
	87.12 87.12		
SPILLVÄTTE	MATERIAL & DIM I MM LUTNING I ‰		
	S200 PP SN8		
	7.0‰		
	VÄTTEGÄNG NIVÅ		
	85.97 85.97		
	86.54 86.54		

