

TECKENFÖRKLARING

— VÄG/GATA
 - - - NY DAGV.LEDNING
 — NY SPILLV.LEDNING
 - - - NY VATTENLEDNING

NY BRUNN FÖR DAGVATTEN
OCH SPILLVATTEN

NY AVSTÄNGNINGSVENTIL FÖR VATTEN



NY BRANDPOST

ANMÄRKNING:

OM INGET ANNAT ANGES SKA SERVISLEDNING
UTANFÖR FASTIGHETGRÄNS FÖR VATTEN VARA
DIM32 PE100 RC SDR11,
SPILLVATTEN DIM110 PVC SN8
OCH DAGVATTEN DIM160 PVC SN8.

COORDINATSYSTEM

PLAN: SWEREF 991630
HÖJD: RH2000

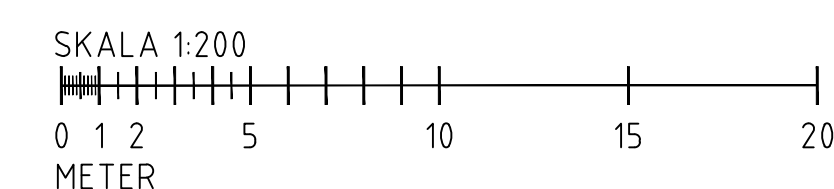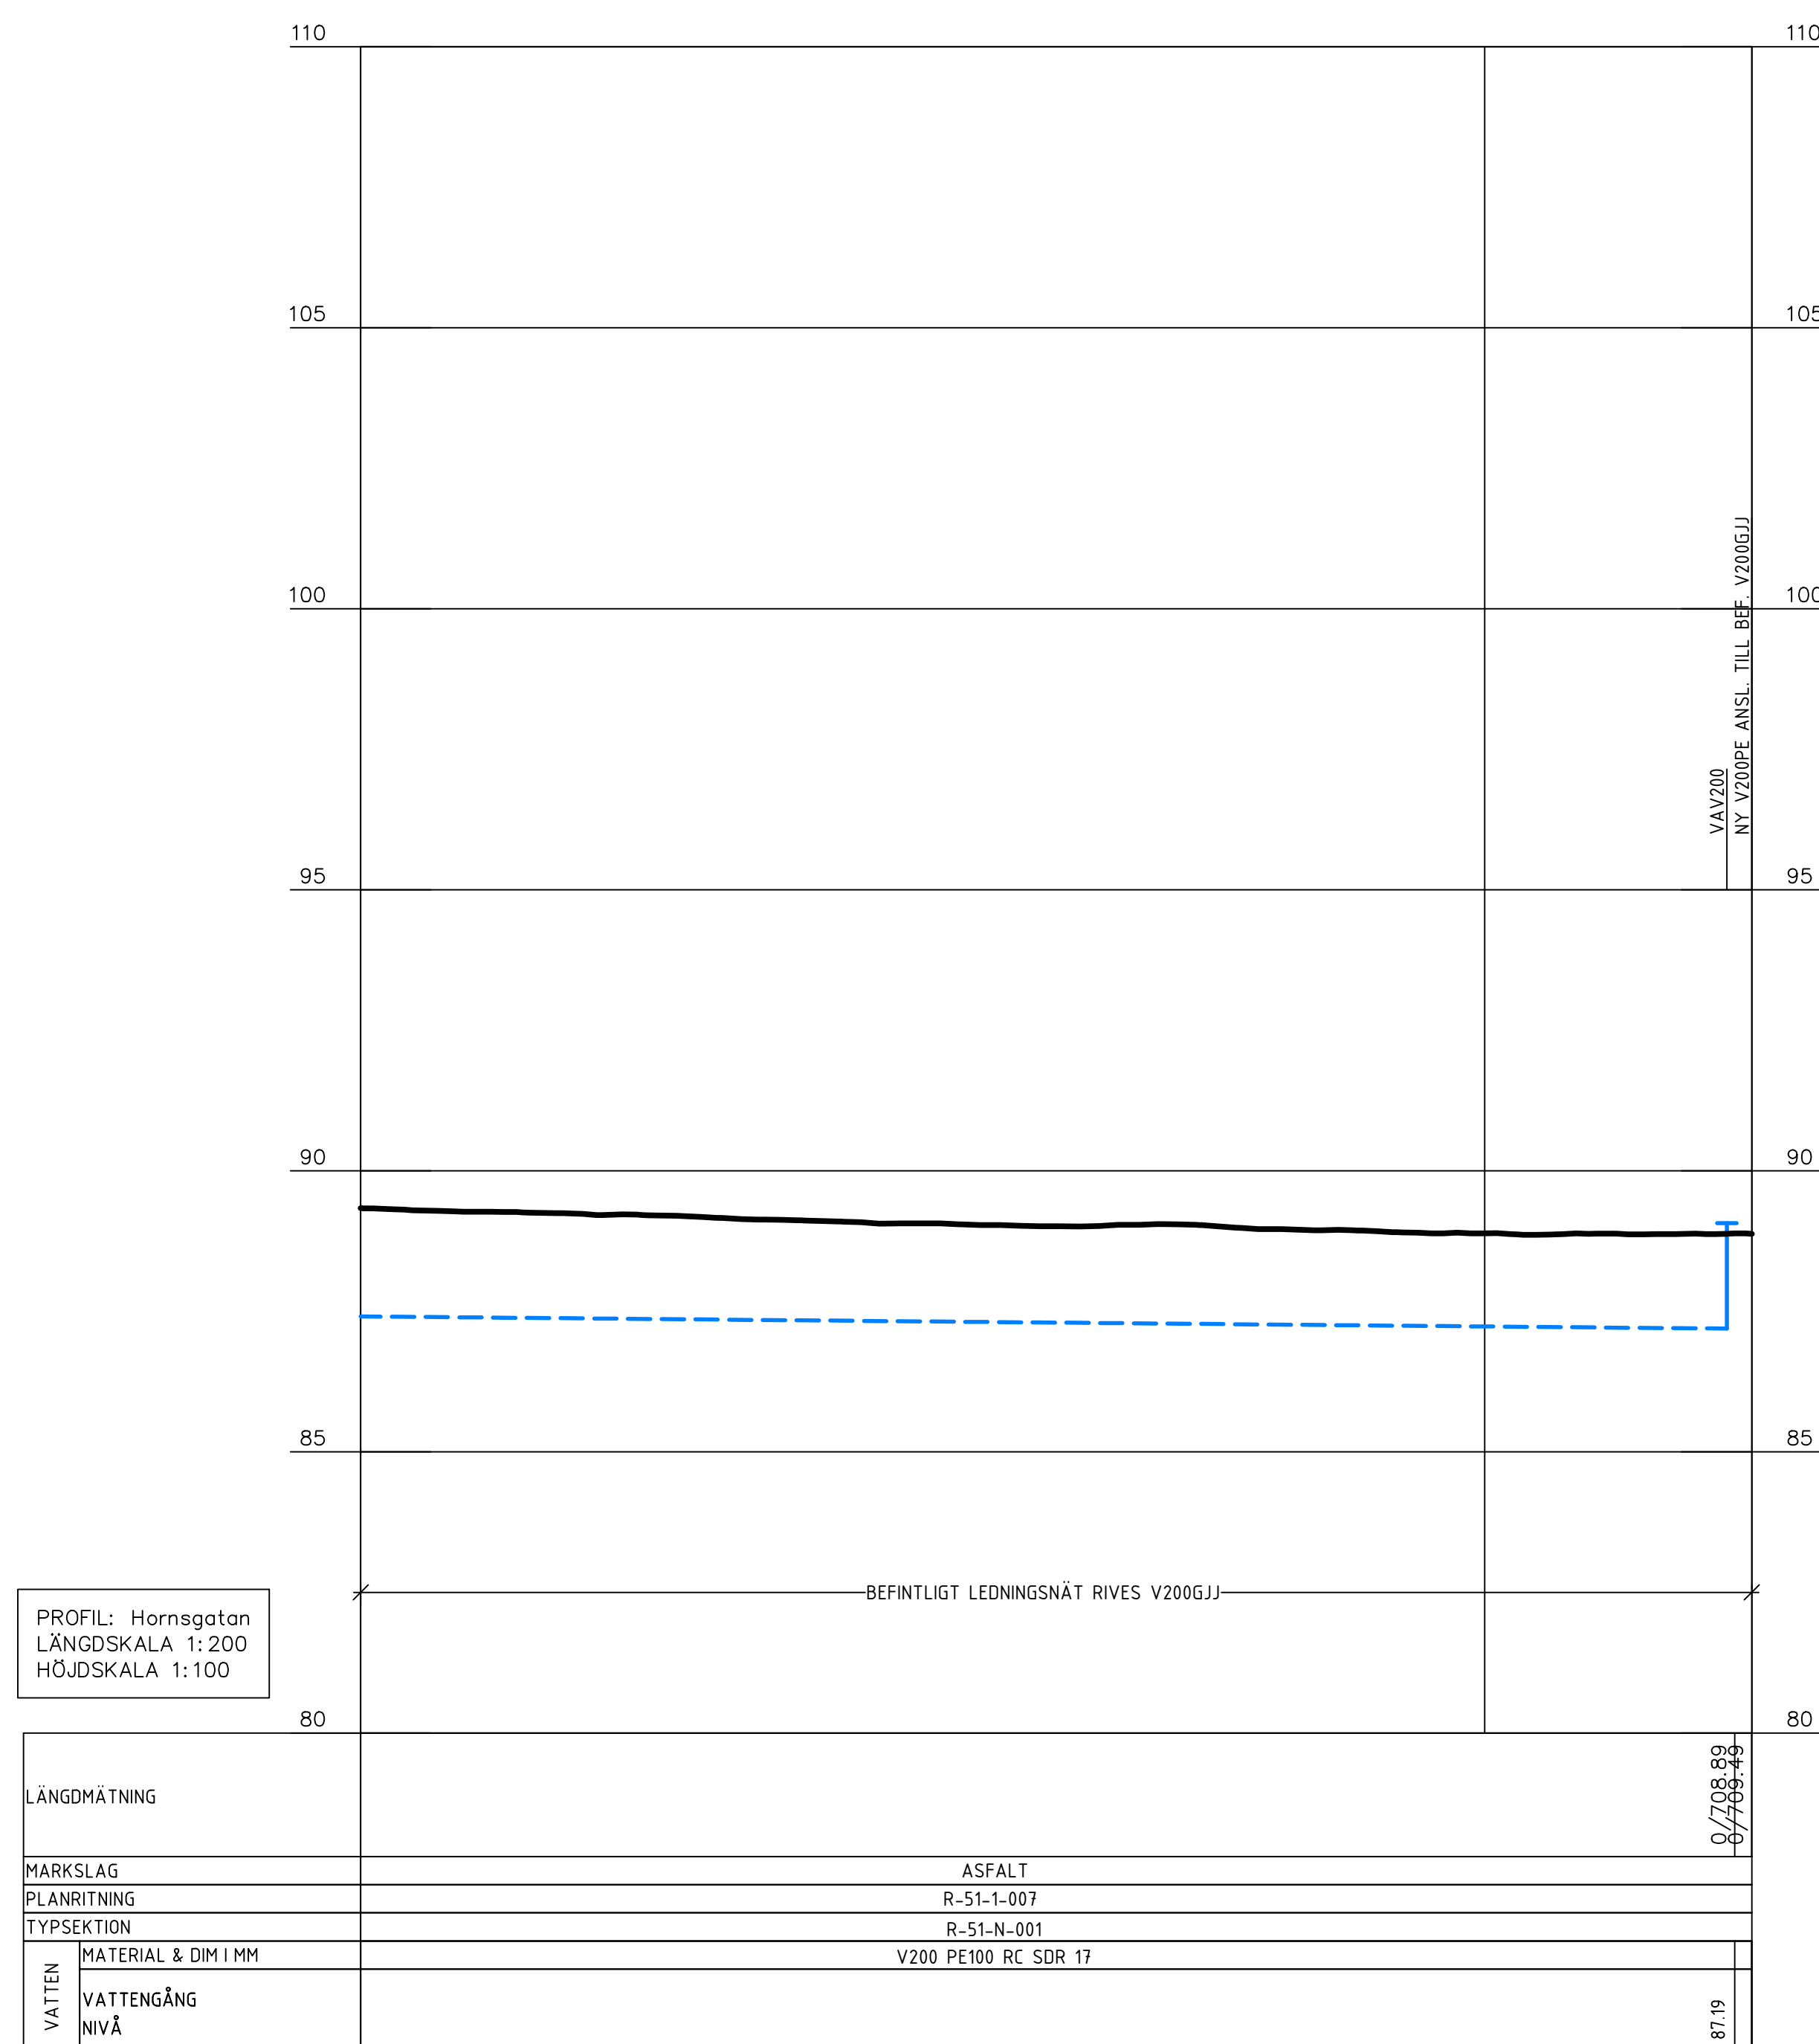

BET	ANT	ÄNDRINGEN AVSR	SIGN	DATUM
FÖRFÖRÅGNINGSUNDERLAG				
HORNSGATAN				
NYBRO				
 NYBRO ENERGI <i>ett lokala energibolag</i>				
PROJEKT BYGGGAREN				
UPPDRAG NR 8524006		RITAD AV I. PÅLSSON TEL		HANDLÄGGARE J. WIJK TEL
DATUM 2025-02-10		ANSVARIG J. WIJK		
SANERING AV VA-LEDNINGAR SAMT EL- OCH BELYSNINGSKABLAR				
PROFIL				
SKALA (A1/A3)		NUMMER		I BET
1:1:200 H=1:100		R-51-2Q-007		