


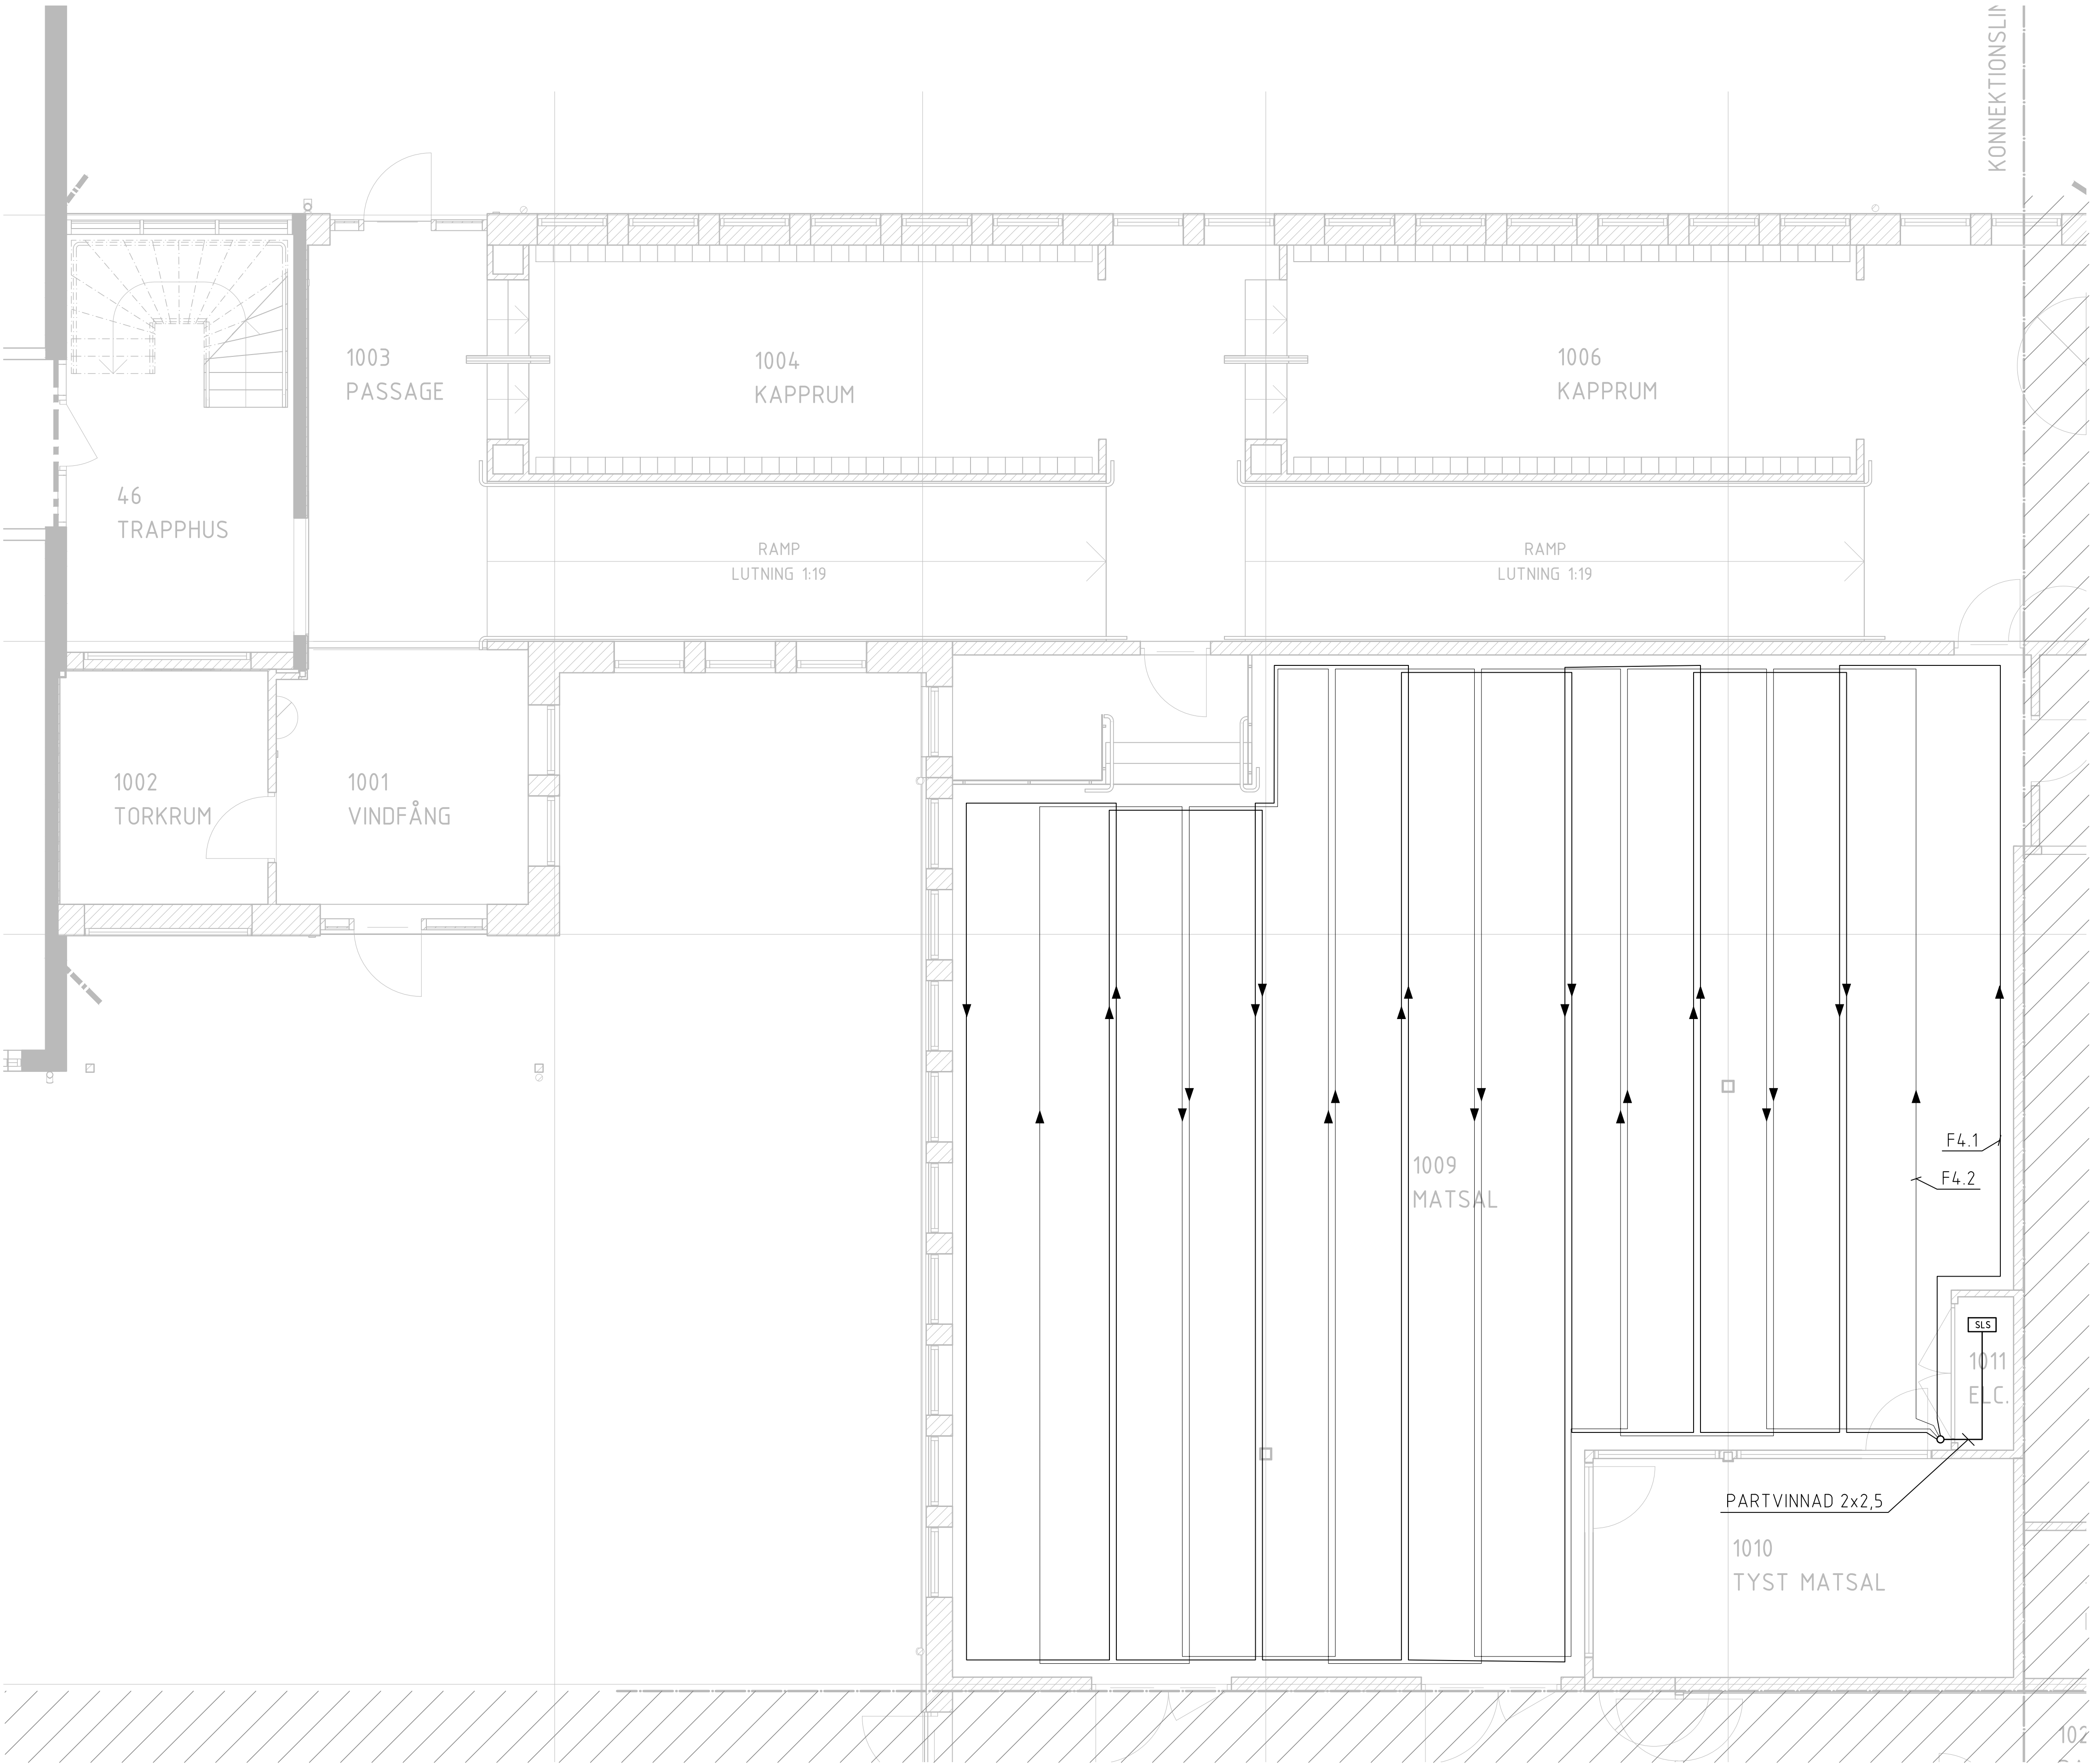

ANVISNINGAR

UNDERLAGET SKA VARA PRIMAT RENT OCH FRITT FRÅN SMUTS OCH ANDRA PARTIKLAR FÖR ATT TEJPEN SKA KUNNA FÄSTA. SLINGAN RESISTANSMÄTS OCH KONTROLLERAS OKULÄRT FÖR ATT SÄKERSTÄLLA ATT SLINGAN FUNGERAR OCH LIGGER ENLIGT RITNING INNAN PWT SKYDDS- OCH VARNINGSTEJP TÄCKER SLINGFOLIEN.

SYMBOLFÖRKLARINGAR

SLS HÖRSLINGEFÖRSTÄRKARE


F4.1 LOOP 1 2x1,25mm² KOPPARFOLIEKABEL

F4.2 LOOP 2 2x1,25mm² KOPPARFOLIEKABEL

HÄNVISNINGAR

SE ÄVEN

- TEKNISK BESKRIVNING EL

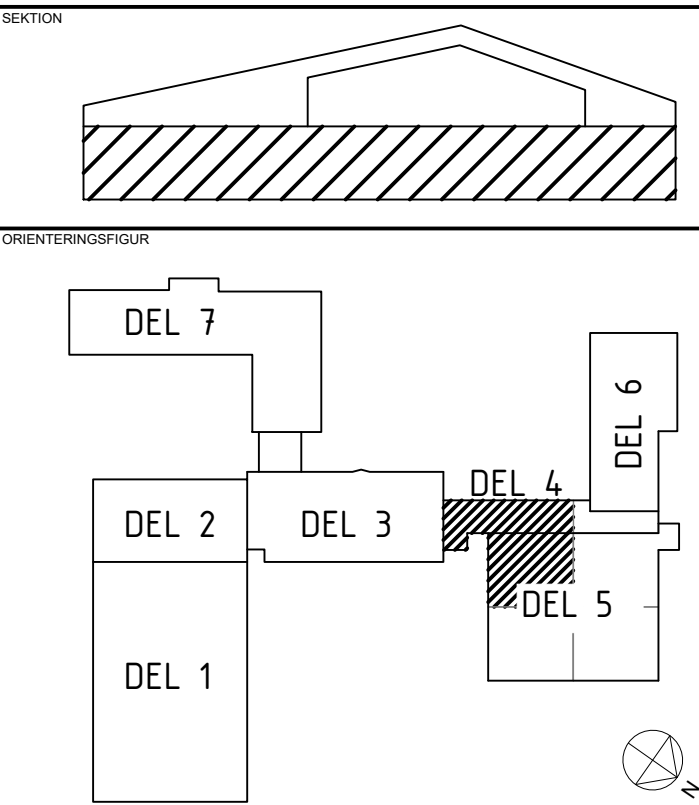

STATUS
FÖRFRÅGNINGSUNDERLAG

HANDLING
BYGGHANDLING

DATUM
2024-12-20

LOPPAD AV
GIN

ÄNDRINGS PM
-



PROJEKTNAMN
CENTRAALKÖK

ORADGE
ROBERTSFORS KOMMUN

PROJEKTNUMMER
YTTRE RINGVÄGEN 4

DIREKTOR
FORDONET 1

DISCIPLIN
E

UPPDAGSNUMMER
1088371

TELEFON
010 141 80 00

BYGGNADSVÄRK
+45,54 (FG)

VÄNINGSPLAN
1

VÄNINGSDEL
DEL 4.1, 5.1

SYSTEM
HÖRSLINGA

SPECIFIKATION
PLAN 1

FORMAT
A1

ANORDNING
BILAGA 3 - HÖRSLINGA

