
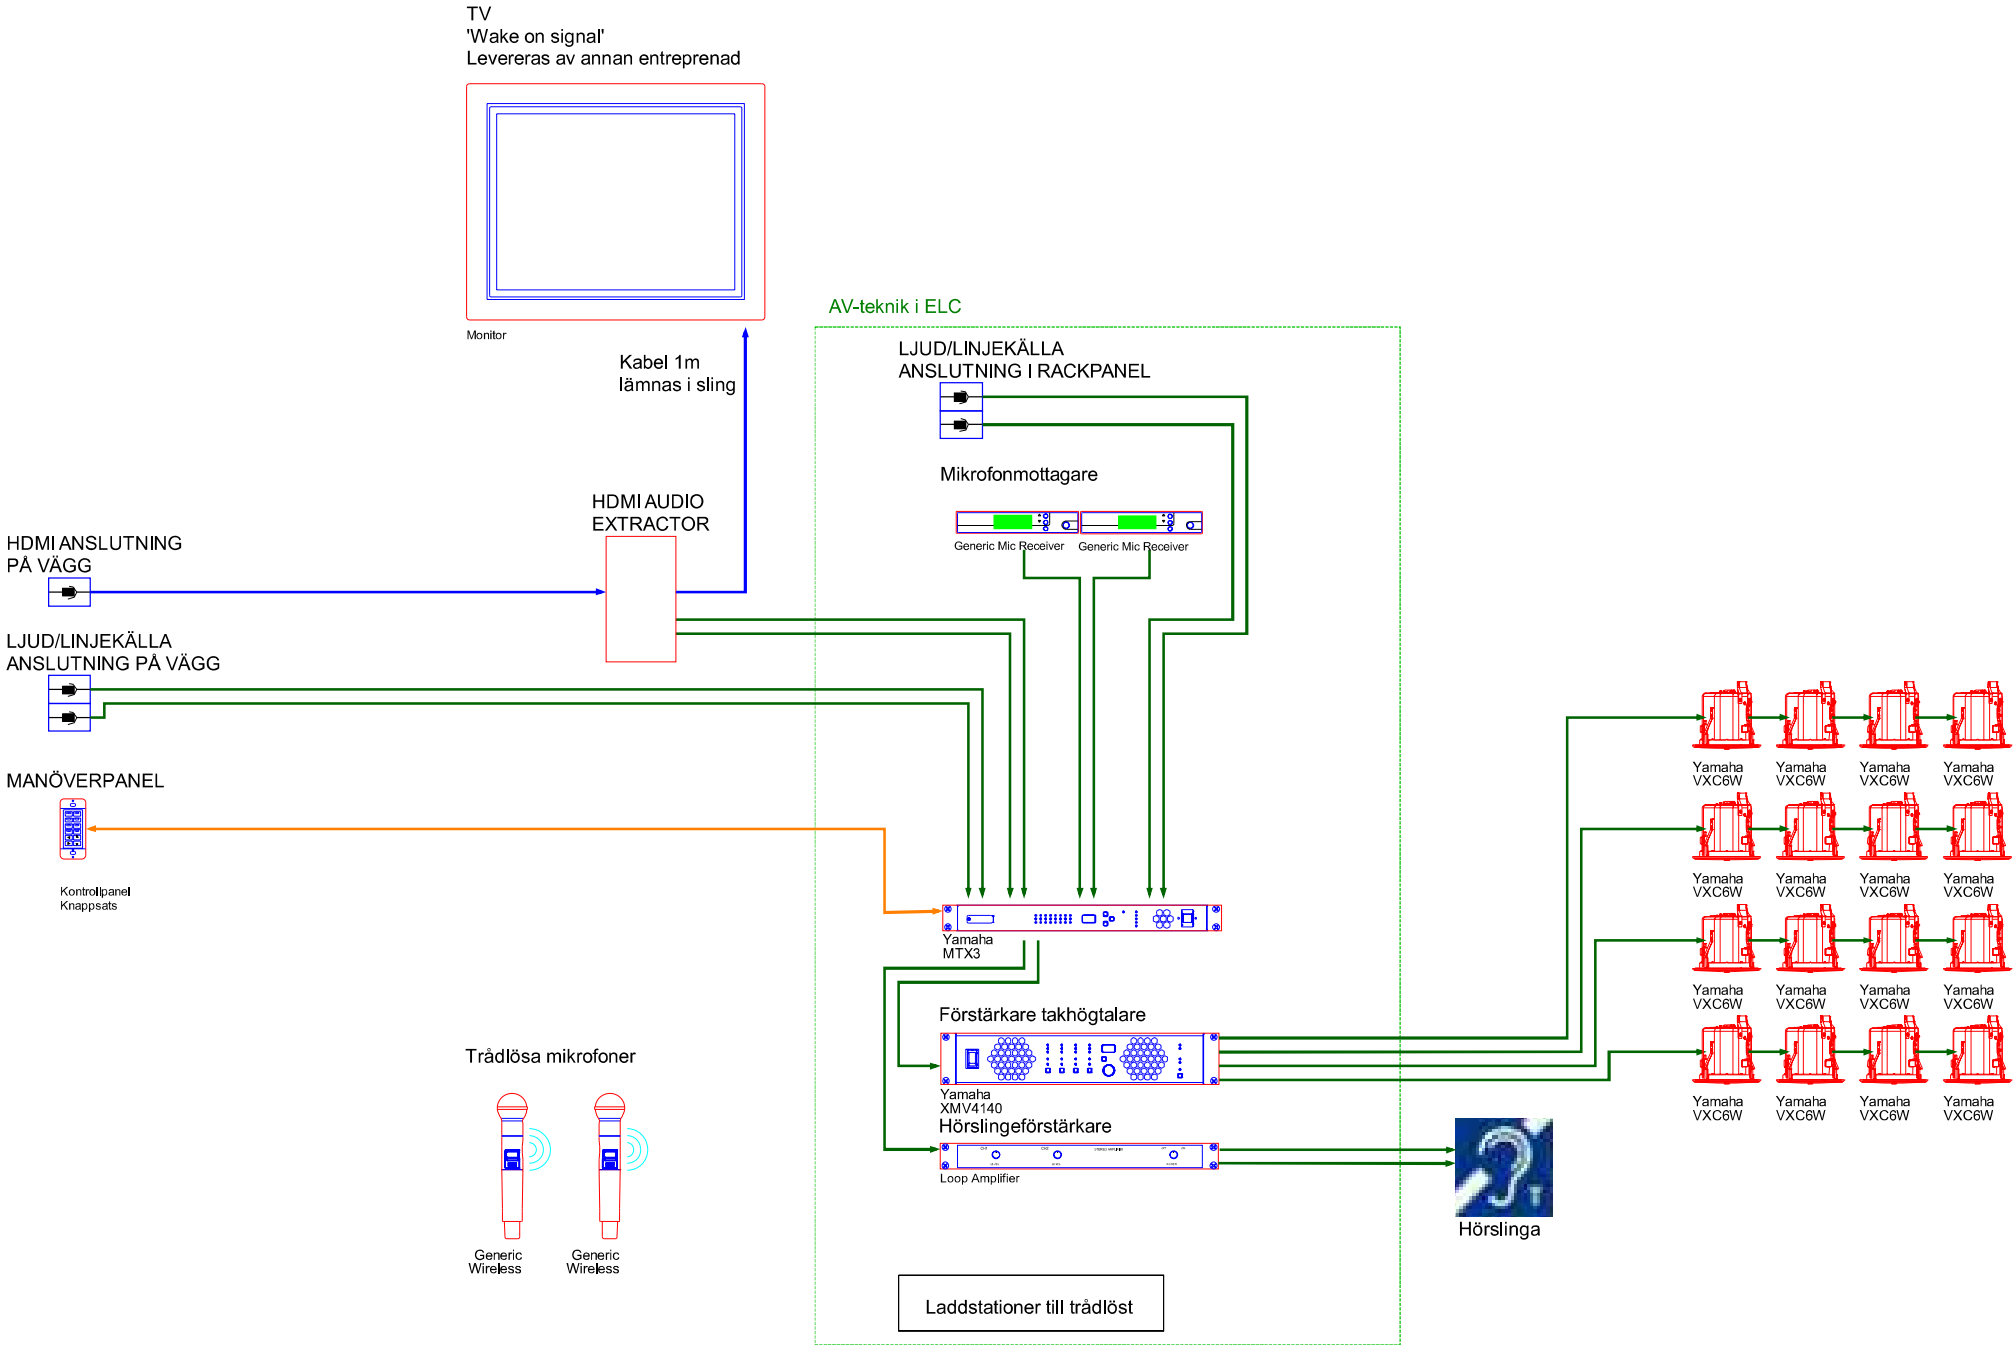


Detta schema är till för att ge en grafisk presentation av funktion och principlösningar.

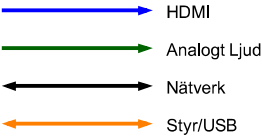

FÖRFRÅGNINGSUNDERLAG
INFORMATIONSRITNING

Bet	Ant	Ändringen avser	Sign	Datum
-----	-----	-----------------	------	-------

Beställare
Robertsfors kommun

Akustikon / Norconsult



Uppdragsnummer 1088371	Ritad/konstruerad JB	Handläggare
Datum 2024-12-04	Ansvarig Jonas Backman	

PRINCIPSCHEMA AV-
UTRUSTNING MATSAL

Skala	BILAGA 5	Bet
-------	----------	-----