



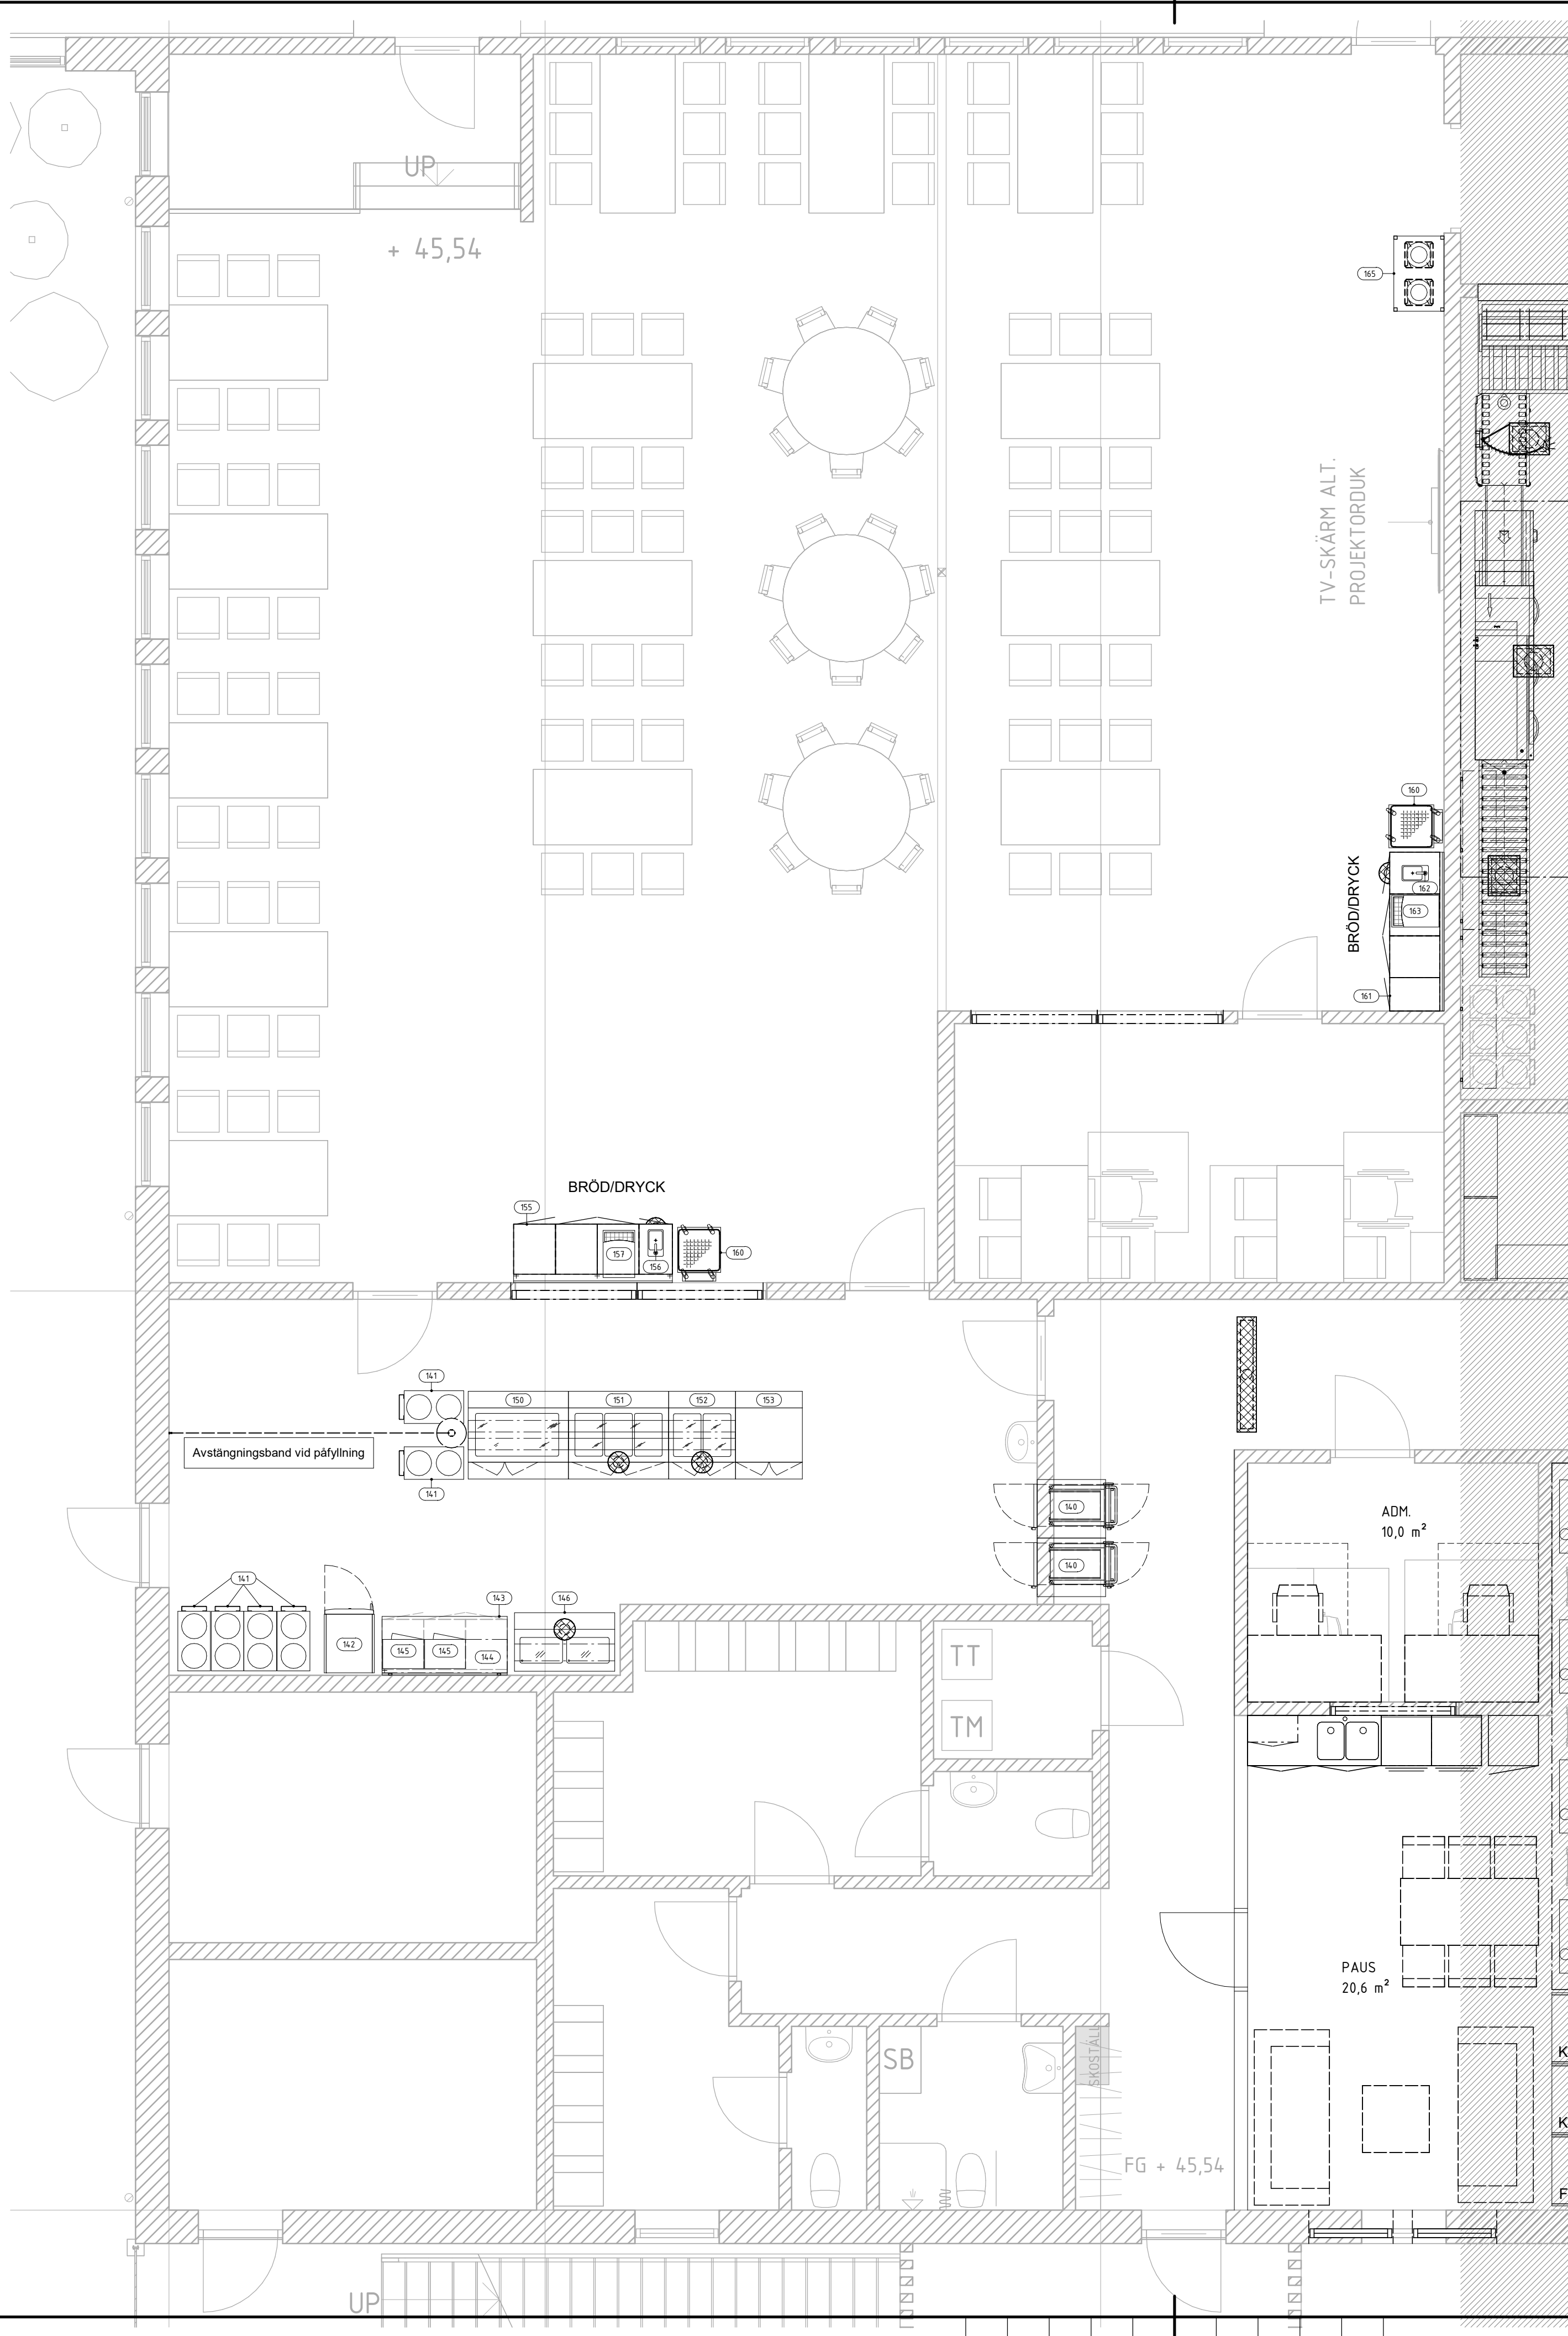

POSITIONSLISTA	
POS	Beteckning
1	Plats för varuskrinda
2	Rostfri arbetsbänk, höj- & sänkbar med el
3	Rostfri vägghylla 2-plan
4	Plats för bordvagn
5	Golvrengöringsanläggning
6	Redskaps-/borsthållare
7	Lyftvagn
8	Balpress/sopkomprimator
9	VAKANT
10	Gallerhyllställning
11	Hyllställning
12-14	VAKANT
15	Mobilt värmeskåp
16	Rostfri vägghylla 2-plan
17	Rostfri vägghylla 2-plan
18	Rostfri vägghylla 2-plan
19	VAKANT
20	Hyllställning
21	Hyllställning
22	Hyllställning
23-24	VAKANT
25	Golvrengöringsanläggning
26	Redskaps-/borsthållare
27	Redskaps-/borsthållare
28-29	VAKANT
30	Visp- och blandningsmaskin 60 L
31	Rostfri diskbänk med stor ho
32	Förspolningsdusch
33	Rostfri vägghylla 2-plan
34-35	VAKANT
36	Grönsaksskårmaskin, golvmmodell
37	Redskapsvagn till grönsaksskärare
38	Kantinvagn till grönsaksskärare
39	VAKANT
40	Rostfri arbetsbänk, höj- & sänkbar med el
41	Rostfri arbetsbänk, höj- & sänkbar med el
42	Rostfri arbetsbänk, höj- & sänkbar med el
43	Rostfri överhylla på ståndare, 2-plan
44	VAKANT
45	Frys-kåp för C-kyla
46	Kylskåp för C-kyla
47	Kombiugn 15 x GN1/1
48	Plats för ugnsvagn
49	VAKANT
50	Uppställningsplats för mobilt värmeskåp
51	Mobilt rostfritt arbetsbord, höj- & sänkbar med vev
52-54	VAKANT
55	Induktionsspis 4 zoner
56	Rostfri diskbänk med utslagsvask
57	Rostfri överhylla på ståndare, 2-plan
58	Stekbord, höj- & sänkbar med ellipp
59	Stekbord, höj- & sänkbar med ellipp
60	Rostfri installationskanal
61-64	VAKANT
65	Kokgryta 200 L med omrörare
66	Kokgryta 200 L med omrörare
67	Kokgryta 100 L med omrörare
68	Redskapsvagn till kokgrytor
69-70	VAKANT
71	Kylskåp för C-kyla
72	Frys-kåp för C-kyla
73	Laminathögs-kåp på rostfria ben
74	Uppställningsplats för mobilt värmeskåp
75	Rostfri arbetsbänk, höj- & sänkbar med el
76	Rostfri vägghylla 2-plan
77	BEF Förslutningsmaskin bänkmodell
78-79	VAKANT
80	Stackad kombiugn 5+5 GN1/1
81	Plats för kantinvagn

POSITIONSLISTA	
POS	Beteckning
82	Induktionsspis 4 zoner
83	Rostfri diskbänk med stor ho
84	Rostfri vägghylla 2-plan
85-89	VAKANT
90	Kantinvagn
91	Hyllställning
92-93	VAKANT
94	Inmatningsrullbana för grovdisk
95	Förspolningsdusch inkl blandare
96	Kombimaskin grov-/fndisk med granuler
97	Utmatningsrullbana för grovdisk
98-99	VAKANT
99	Redskaps-/borsthållare
100	Rostfri tallriksbana
101	Diskinlämningsbänk 5 korgar med överhylla
102	Bassängrullbana med integrerat stänkskydd
103	Förspolningsdusch inkl blandare
104	Förspolningstunnel inkl matning
105	Tunneldiskmaskin
106	Utmatningsrullbana med ändlägesbrytare
107	Rostfri vägghylla 2-plan
108	Plats för tallriksdispenser
109-110	VAKANT
111	Golvrengöringsanläggning
112	Redskaps-/borsthållare
113	Hyllställning
114	Snabbnedkylningsrum för C-kyla
115-117	VAKANT
118	Rostfri arbetsbänk, höj- & sänkbar med el
119	Rostfri överhylla på ståndare, 2-plan
120	BEF Förslutningsmaskin på rullbord
121	Rostfri arbetsbänk, höj- & sänkbar med el
122	Rostfri överhylla på ståndare, 2-plan
123	BEF Förslutningsmaskin på rullbord
124	Hyllställning
125	Hyllställning
126-129	VAKANT
130	Uppställningsplats för mobilt värmeskåp
131	Plats för avdelningsvagn
132	Rostfri arbetsbänk, höj- & sänkbar med el
133	Rostfri vägghylla 2-plan
134	Plats för korgvagn
135	Plats för tallriksdispenser
136-139	VAKANT
140	Värmeskåp för genomräckning
141	Tallriksdispenser
142	Kylskåp med inbyggd kompressor
143	Rostfri toppskiva på laminatskåpsunderrede
144	Rostfri vägghylla 2-plan
145	Mikrovågsugn
146	Värmeri skolmodell, 2 x GN 1/1
147-149	VAKANT
150	Kall buffé, 3 x GN1/1
151	Varm buffé, 3 x GN1/1
152	Varm buffé, 2 x GN1/1
153	Neutral buffé
154	VAKANT
155	Rostfri toppskiva på laminatskåpsunderrede
156	Infälld vattensifon med spillbricka
157	Plats för kyld mjölkdispenser
158-159	VAKANT
160	Korgvagn
161	Rostfri toppskiva på laminatskåpsunderrede
162	Infälld vattensifon med spillbricka
163	Plats för kyld mjölkdispenser
165	Rostfri avfallsstation, 2 stos

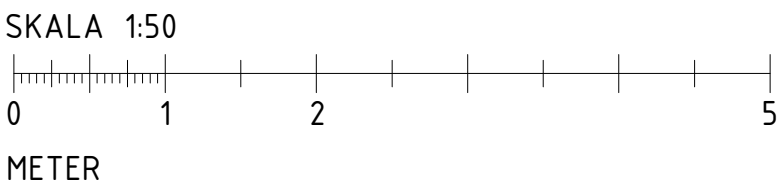

BET	ANDRINGEN AVSER	DATUM	SIGN
PROGRAMHANDLING			
STORKÖK ROBERTSFORS			
 ROBERTSFORS KOMMUN			
Norconsult  www.norconsult.se			
A NORCONSULT AB		tel. 010-141 80 00	
K NORCONSULT AB			
X SK NORCONSULT AB			
M NORCONSULT AB			
VS NORCONSULT AB			
L NORCONSULT AB			
E NORCONSULT AB			
UPPRAG NR 108 83 71	RITADKONSTR AV ALG	HANDLÄGGARE ALG	
DATUM 2024-06-26	ANSVARIG TOMAS BERGSTRÖM		
STORKÖK ROBERTSFORS			
PLAN, DEL 2 STORKÖK			
SKALA A1 1:50 A3 1:100	NUMMER SK-46-1-02		BET