


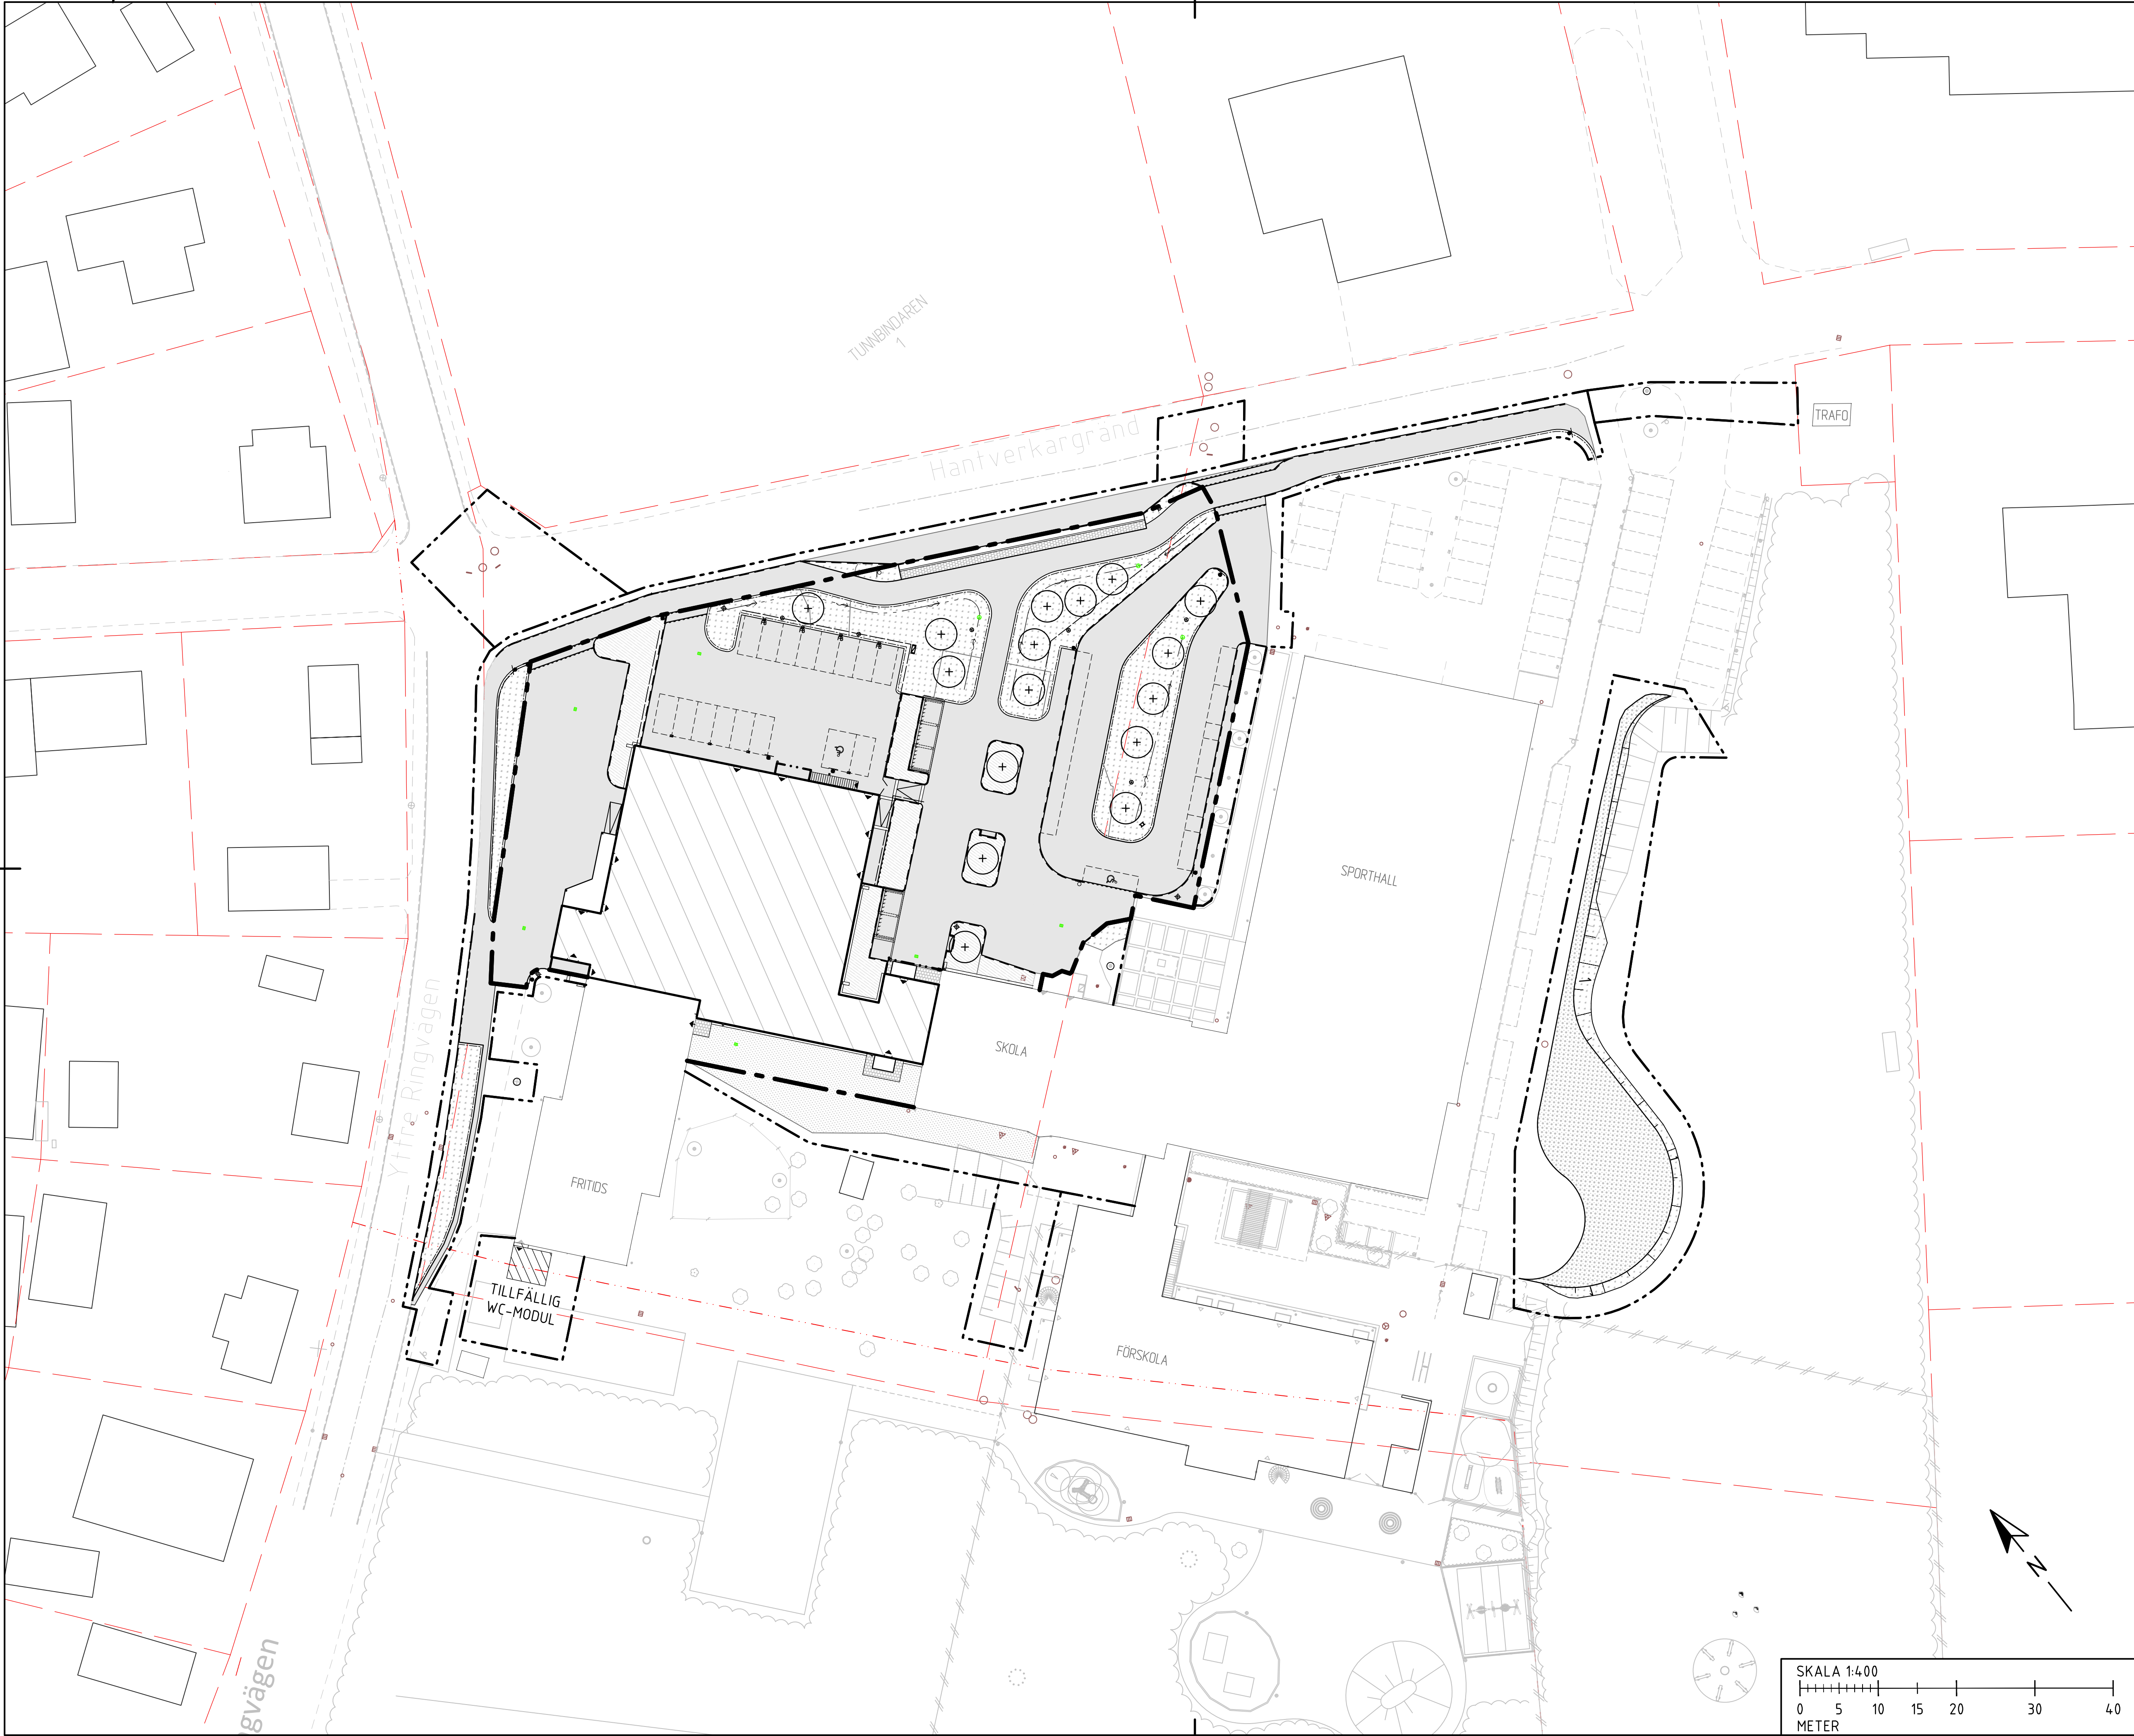

TECKENFÖRKLARING

FASTIGHETSGRÄNS

ARBETSMRÄDESGRÄNS

TILLFÄLLIGT ARBETSMRÅDE

ANMÄRKNING

KOORDINATSYSTEM SWEREF99 2015

HÖJDSYSTEM RH2000

STATUS		
FÖRFRÅGNINGSUNDERLAG		
HANDLING		
BYGGHANDLING		
DATUM	GODKÄND AV	ÄNDRINGS PM
2024-12-20		
BESTÄLLARE		
ROBERTSFORS KOMMUN		
PROJEKTNAMN		
CENTRALKÖK		
OMRÅDE		
ROBERTSFORS KOMMUN		
PROJEKTNUMMER	ADRESS	
	YTTRE RINGVÄGEN 4	
DIARIENUMMER	FASTIGHET	
	FORDONET 1	
DISCIPLIN	FÖRETAG	
M	NORCONSULT SVERIGE AB	
OPPFÖRINGSNUMMER	SKAPACIAV	
108 83 71	AVH	
TELEFON	KOORDINATSYSTEM	
010 141 80 00	TOMAS BERGSTRÖM	
BYGGNADSVÄRDE	HÖJDSYSTEM (RH 2000)	
	+44.60, +45.07, +45.54 (FG)	
VÄNINGSPLAN	VÄNINGSDEL	DELOMRÅDE
SYSTEM		
30 SAMMANSATT REDOVISNING MARK		
RESERVATION		
ÖVERSIKT		
RITNINGSCATEGORI	SKALA	FORMAT
PLAN	1:400	A1
DOKUMENTNUMMER	ÄNDRING	
M-01-1-001		