


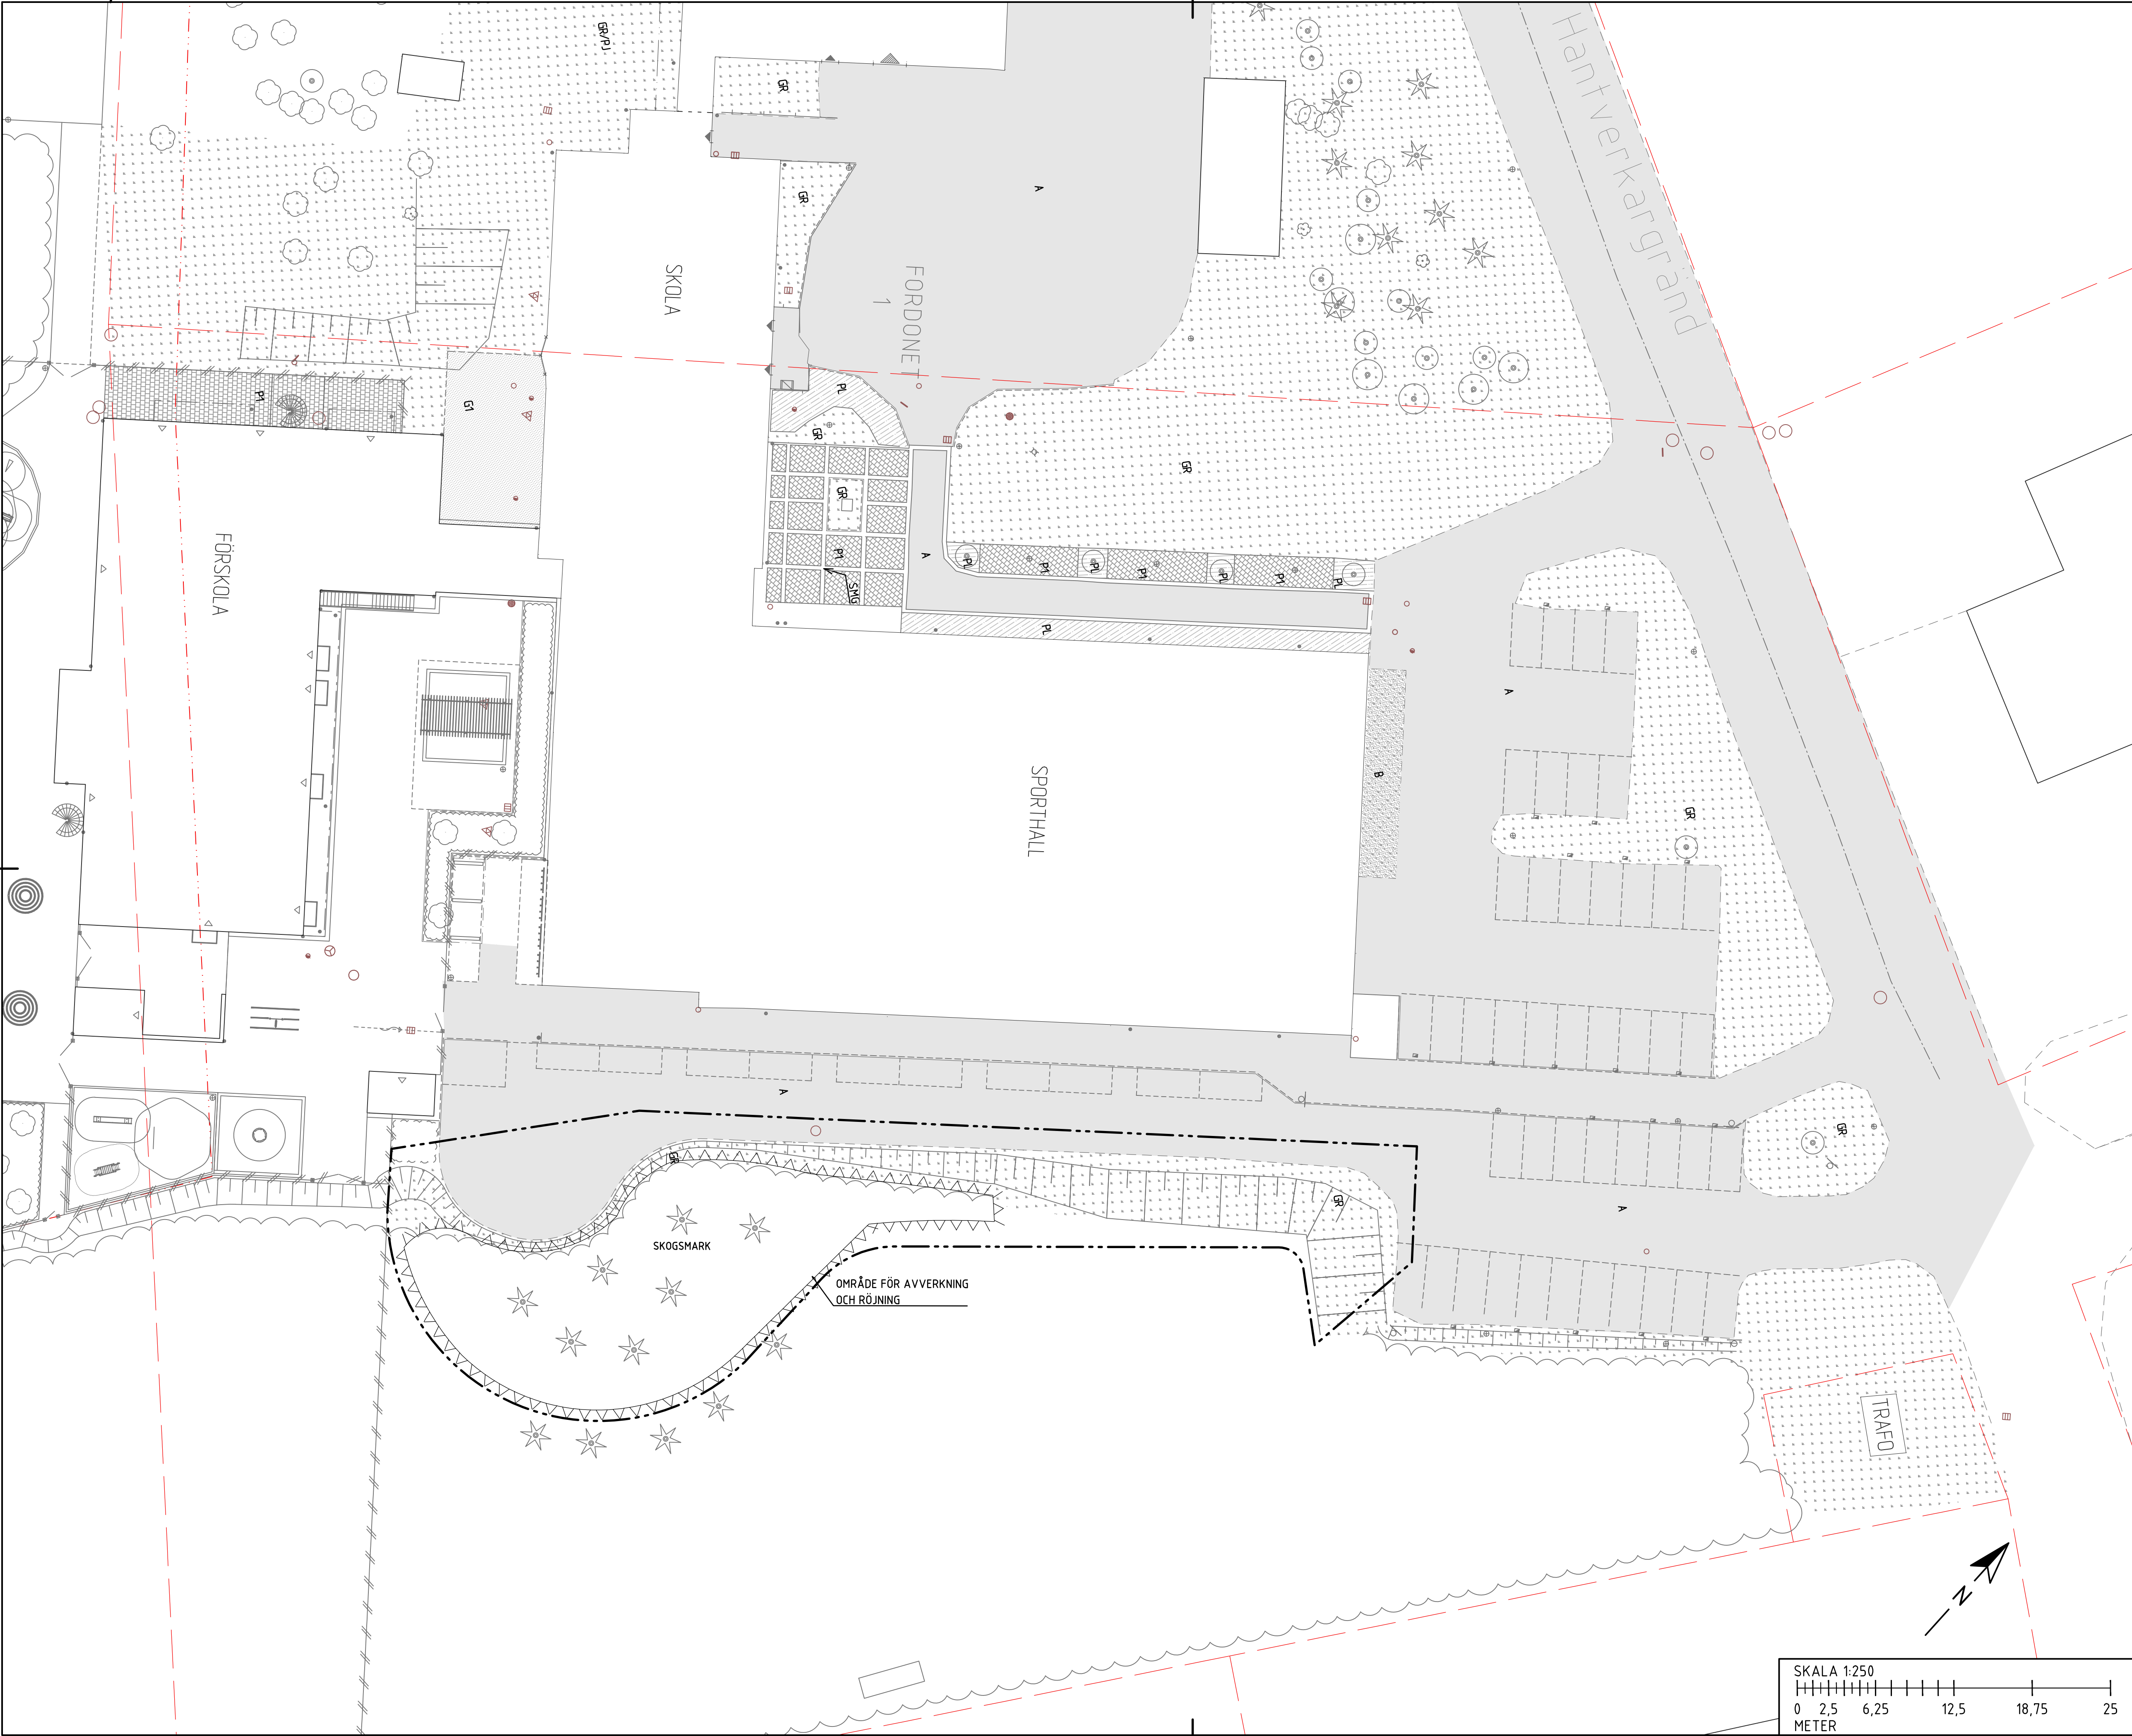

TECKENFÖRKLARING

— FASTIGHETSGRÄNS

- - - TILLFÄLLIGT ARBETSOMRÅDE

/// STAKET

▼ ENTRÉ

A ASFALT

GR GRÄS

P1 STENPLATTOR

P2 BETONGPLATTOR

B BETONG

▲▲▲▲▲ OMRÅDE FÖR AVVERKNING OCH RÖJNING

★ BEFINTLIGA TRÄD EJ INMÄTTA

ANMÄRKNING

KOORDINATSYSTEM SWEREF99 2015

HÖJDSYSTEM RH2000

STATUS		
FÖRFRÅGNINGSUNDERLAG		
HANDLING		
BYGGHANDLING		
DATUM	GODKÄND AV	ÄNDRINGS PM
2024-12-20		
BESTÄLLARE		
 ROBERTSFORS KOMMUN		
PROJEKTNAMN		
CENTRALKÖK		
OMRÅDE		
ROBERTSFORS KOMMUN		
PROJEKTNUMMER	ADRESS	
	YTTRE RINGVÄGEN 4	
DIARIENUMMER	FASTIGHET	
	FORDONET 1	
DISCIPLIN	FÖRETAG	
M	NORCONSULT SVERIGE AB	
UPPDRAGSNUMMER	SKAPAD AV	
108 83 71	AVH	
TELEFON	KOORDINERINGS	
010 141 80 00	TOMAS BERGSTRÖM	
BYGGNADSVÄRK	HÖJDSYSTEM (RH 2000)	
	+44.60, +45.07, +45.54 (FG)	
VÄNINGSPLAN	VÄNINGSDEL	DELOMRÅDE
SYSTEM		
30 SAMMANSATT REDOVISNING MARK		
RITNINGSKATEGORI		
PLAN		
DOKUMENTNUMMER	SKALA	FORMAT
M-11-1-002	1:250	A1
ÄNDRING		