


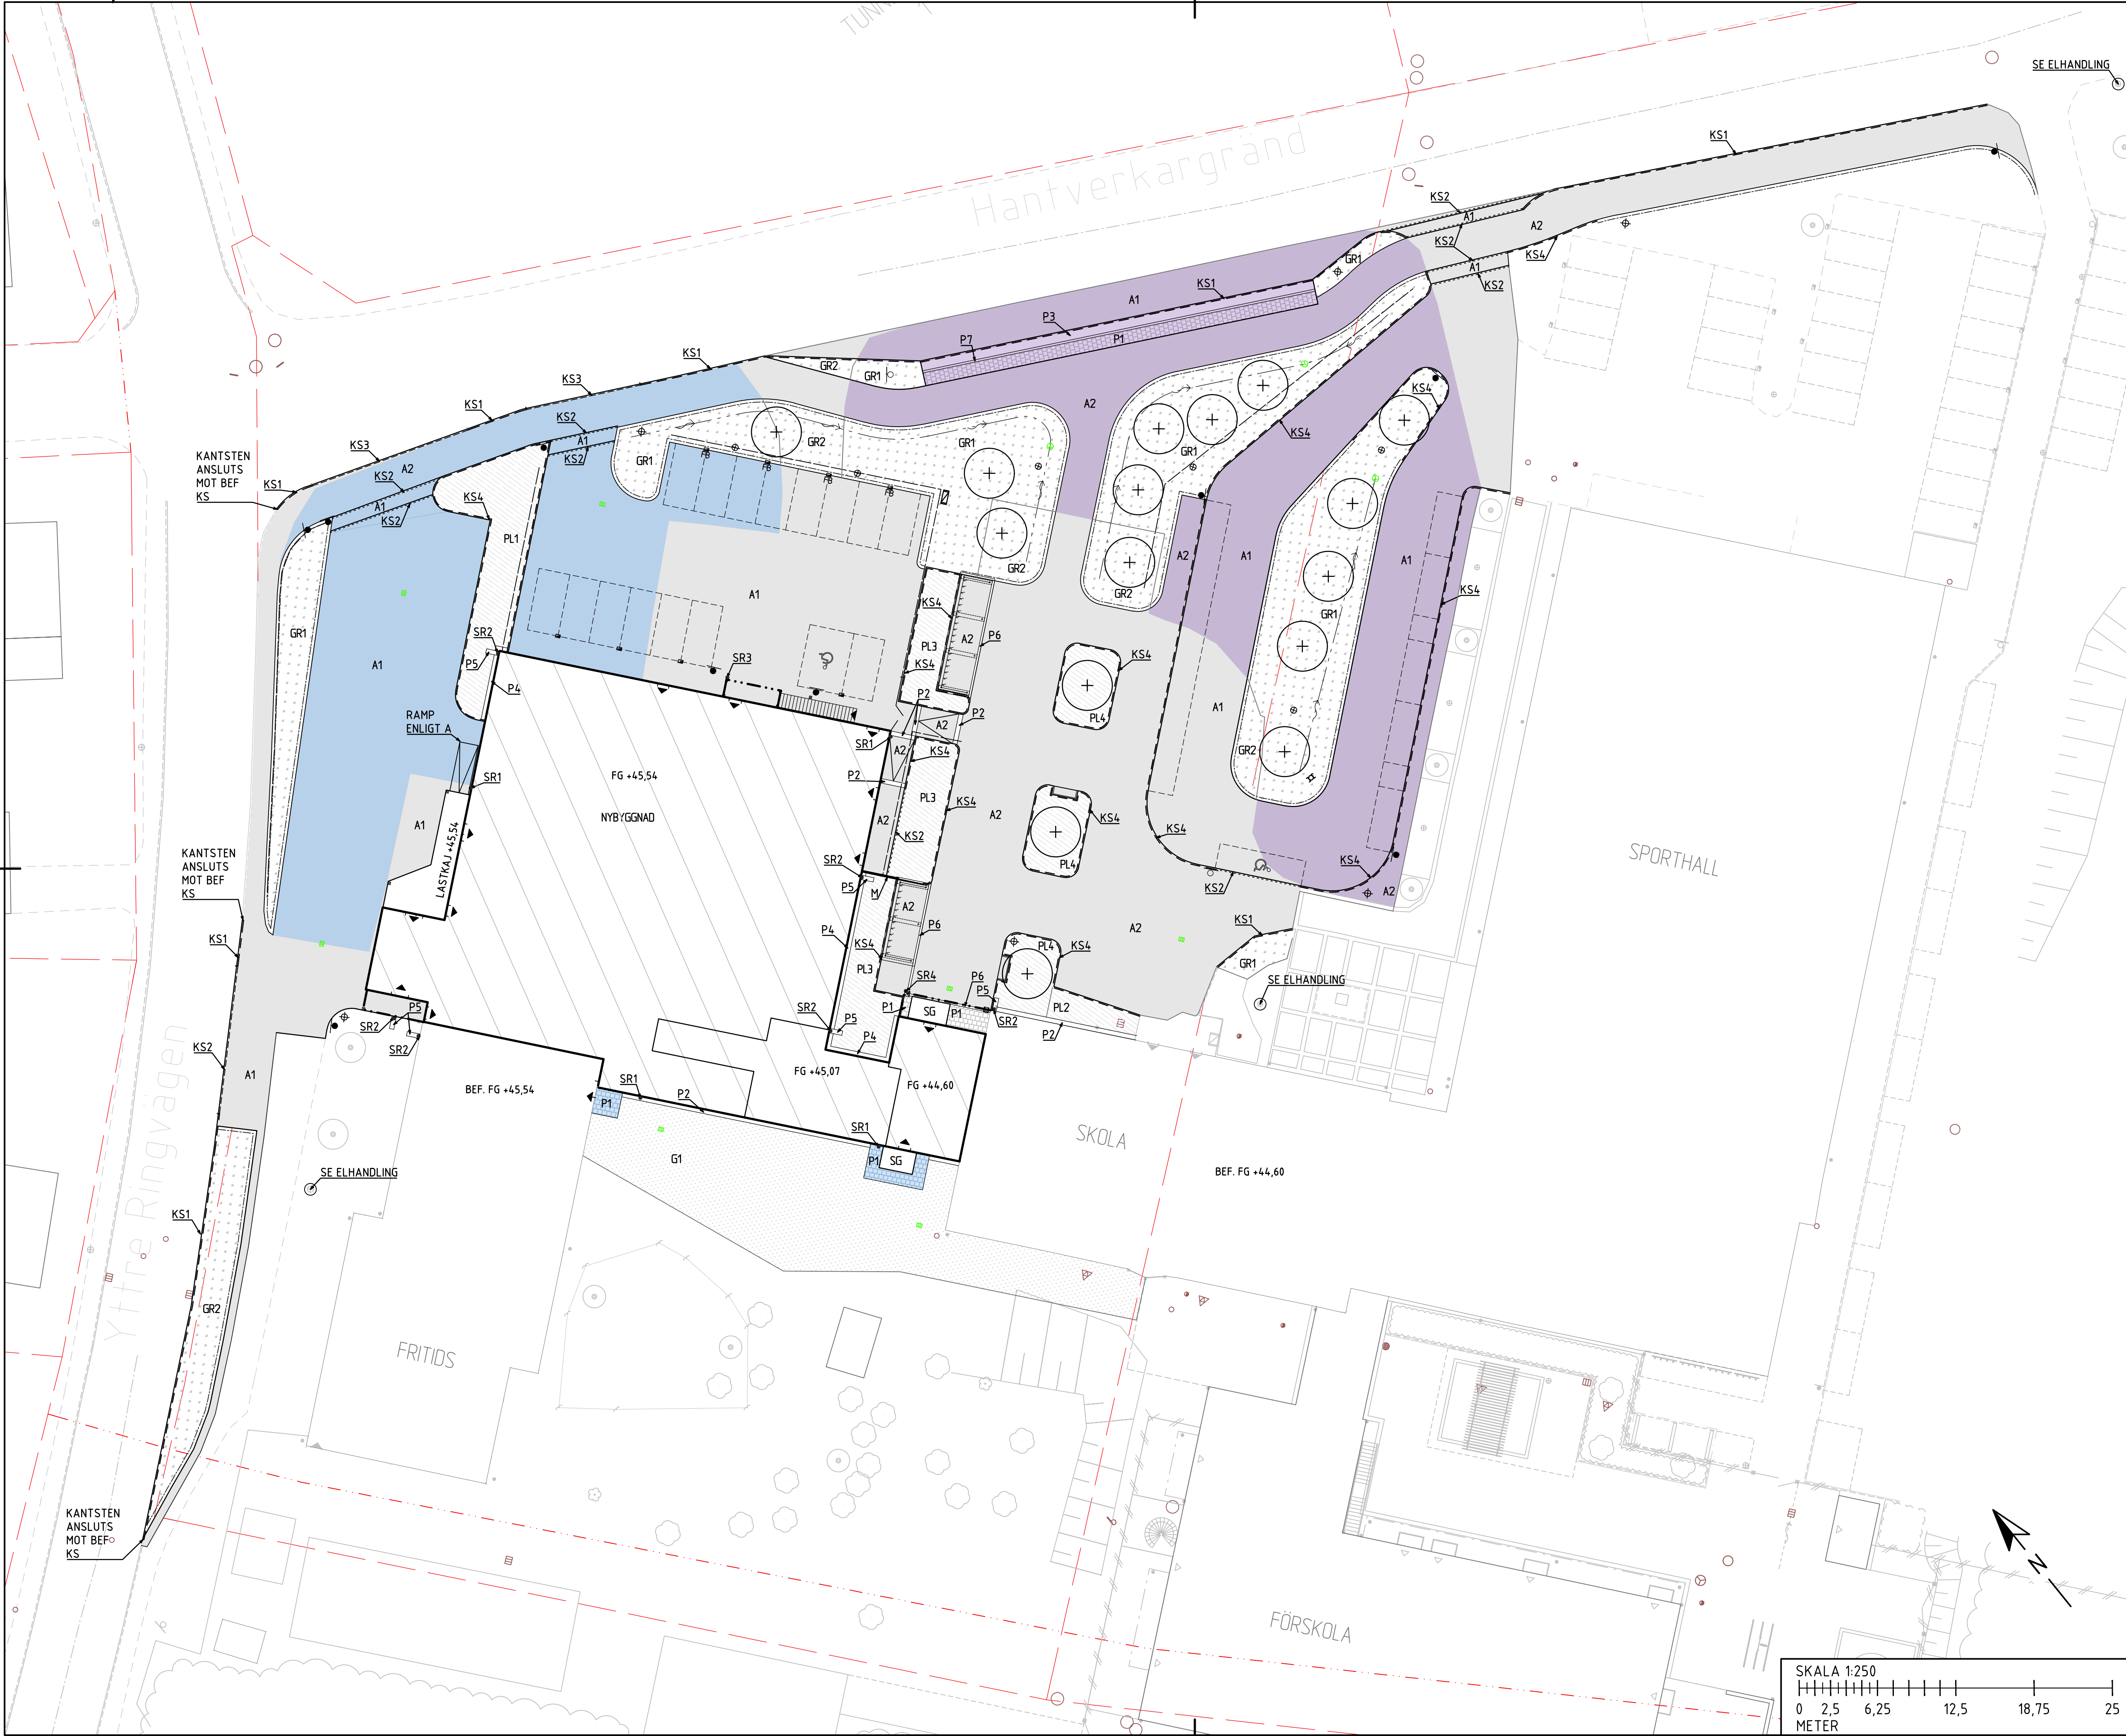

TECKENFÖRKLARING

FASTIGHETSGRÄNS

ASFALTKANT MED STÖDREMSA

KS1, BETONGKANTSTÖD MED VISNING

KS2, GRANITKANTSTEN NEDSÄNK

KS3, BETONGKANTSTÖD FASAD

KS4, GRANITKANTSTEN MED VISNING

SKÄRMTAK

M, STÖDMUR

DIKESANVISNING

HANDELDARE

STAKET, HÖGT

AVGRÄNSNING

ASFALT, ABT16

ASFALT, ABT11

PL1

PL2

PL3

PL4

GR1

GR2

P1

P2, PLATTRAD VID RAMP

P3, 2ST PLATTRADER

P4, PLATTRAD VID FASAD

P5, RÄNDALPLATTOR

P6, P7 HALVPLATTA

G1

YTA SOM UTSKIFTAS

YTA MED NY ÖVERBYGGNAD

TRAPPA

RAMPER

+

TRÄD/BUSKE

MOTORVÄRMARE

FÖRBEREDELSE FÖR MOTORVÄRMARE MED FUNDAMENT

BELYSNING

BEF BELYSNING SOM FLYTTAS

BYTE AV ARMAUTR PÅ BELYSNING

ENTRÉ

NY PLACERING FLAGGSTÅNG

SKYLSTOLPE

BEF. SKYLSTOLPE SOM FLYTTAS

FUNDAMENT

BRUNNAR

SR1, SR3, SR4 STUPRÖR MARKANSLUTET

SR2, STUPRÖR MED UTKASTARE

SG

ELSKÅP ENL. EL-HANDLING

FÖR UTRUSTNING OCH VÄXTER SE RITNING M-32-1-001

ANMÄRKNING

KOORDINATSYSTEM SWEREF99 2015

HÖJDSYSTEM RH2000

STATUS

FÖRFRÅGNINGSUNDERLAG

HANDLING

BYGGHANDLING

DATUM

2024-12-20

GODKÄND AV

ANDRINGS PM

BESTÄLLARE

ROBERTSFORS KOMMUN

PROJEKTNAMN

CENTRAALKÖK

OMRADE

ROBERTSFORS KOMMUN

PROJEKTNUMMER

YTTRE RINGVÄGEN 4

DIARIENUMMER

FORDONET 1

DISCIPLIN

M

FÖRETAG

NORCONSULT SVERIGE AB

UPPDRAGSNUMMER

108 83 71

SKAPAD AV

AVH

TELEFON

010 141 80 00

KONTAKTPERSON

TOMAS BERGSTRÖM

BYGGNADSVÄRK

(FLUSHÖJD (RH 2000))

+44.60, +45.07, +45.54 (FG)

VÄNINGSPLAN

VÄNINGSDEL

DELOMRADE

SYSTEM

30 SAMMANSATT REDOVISNING MARK

SPESIFIKATION

YTSKIKT

RITNINGSKATEGORI

PLAN

SKALA

1:250

FORMAT

A1

DOKUMENTNUMMER

M-31-1-001

ÄNDRING

