


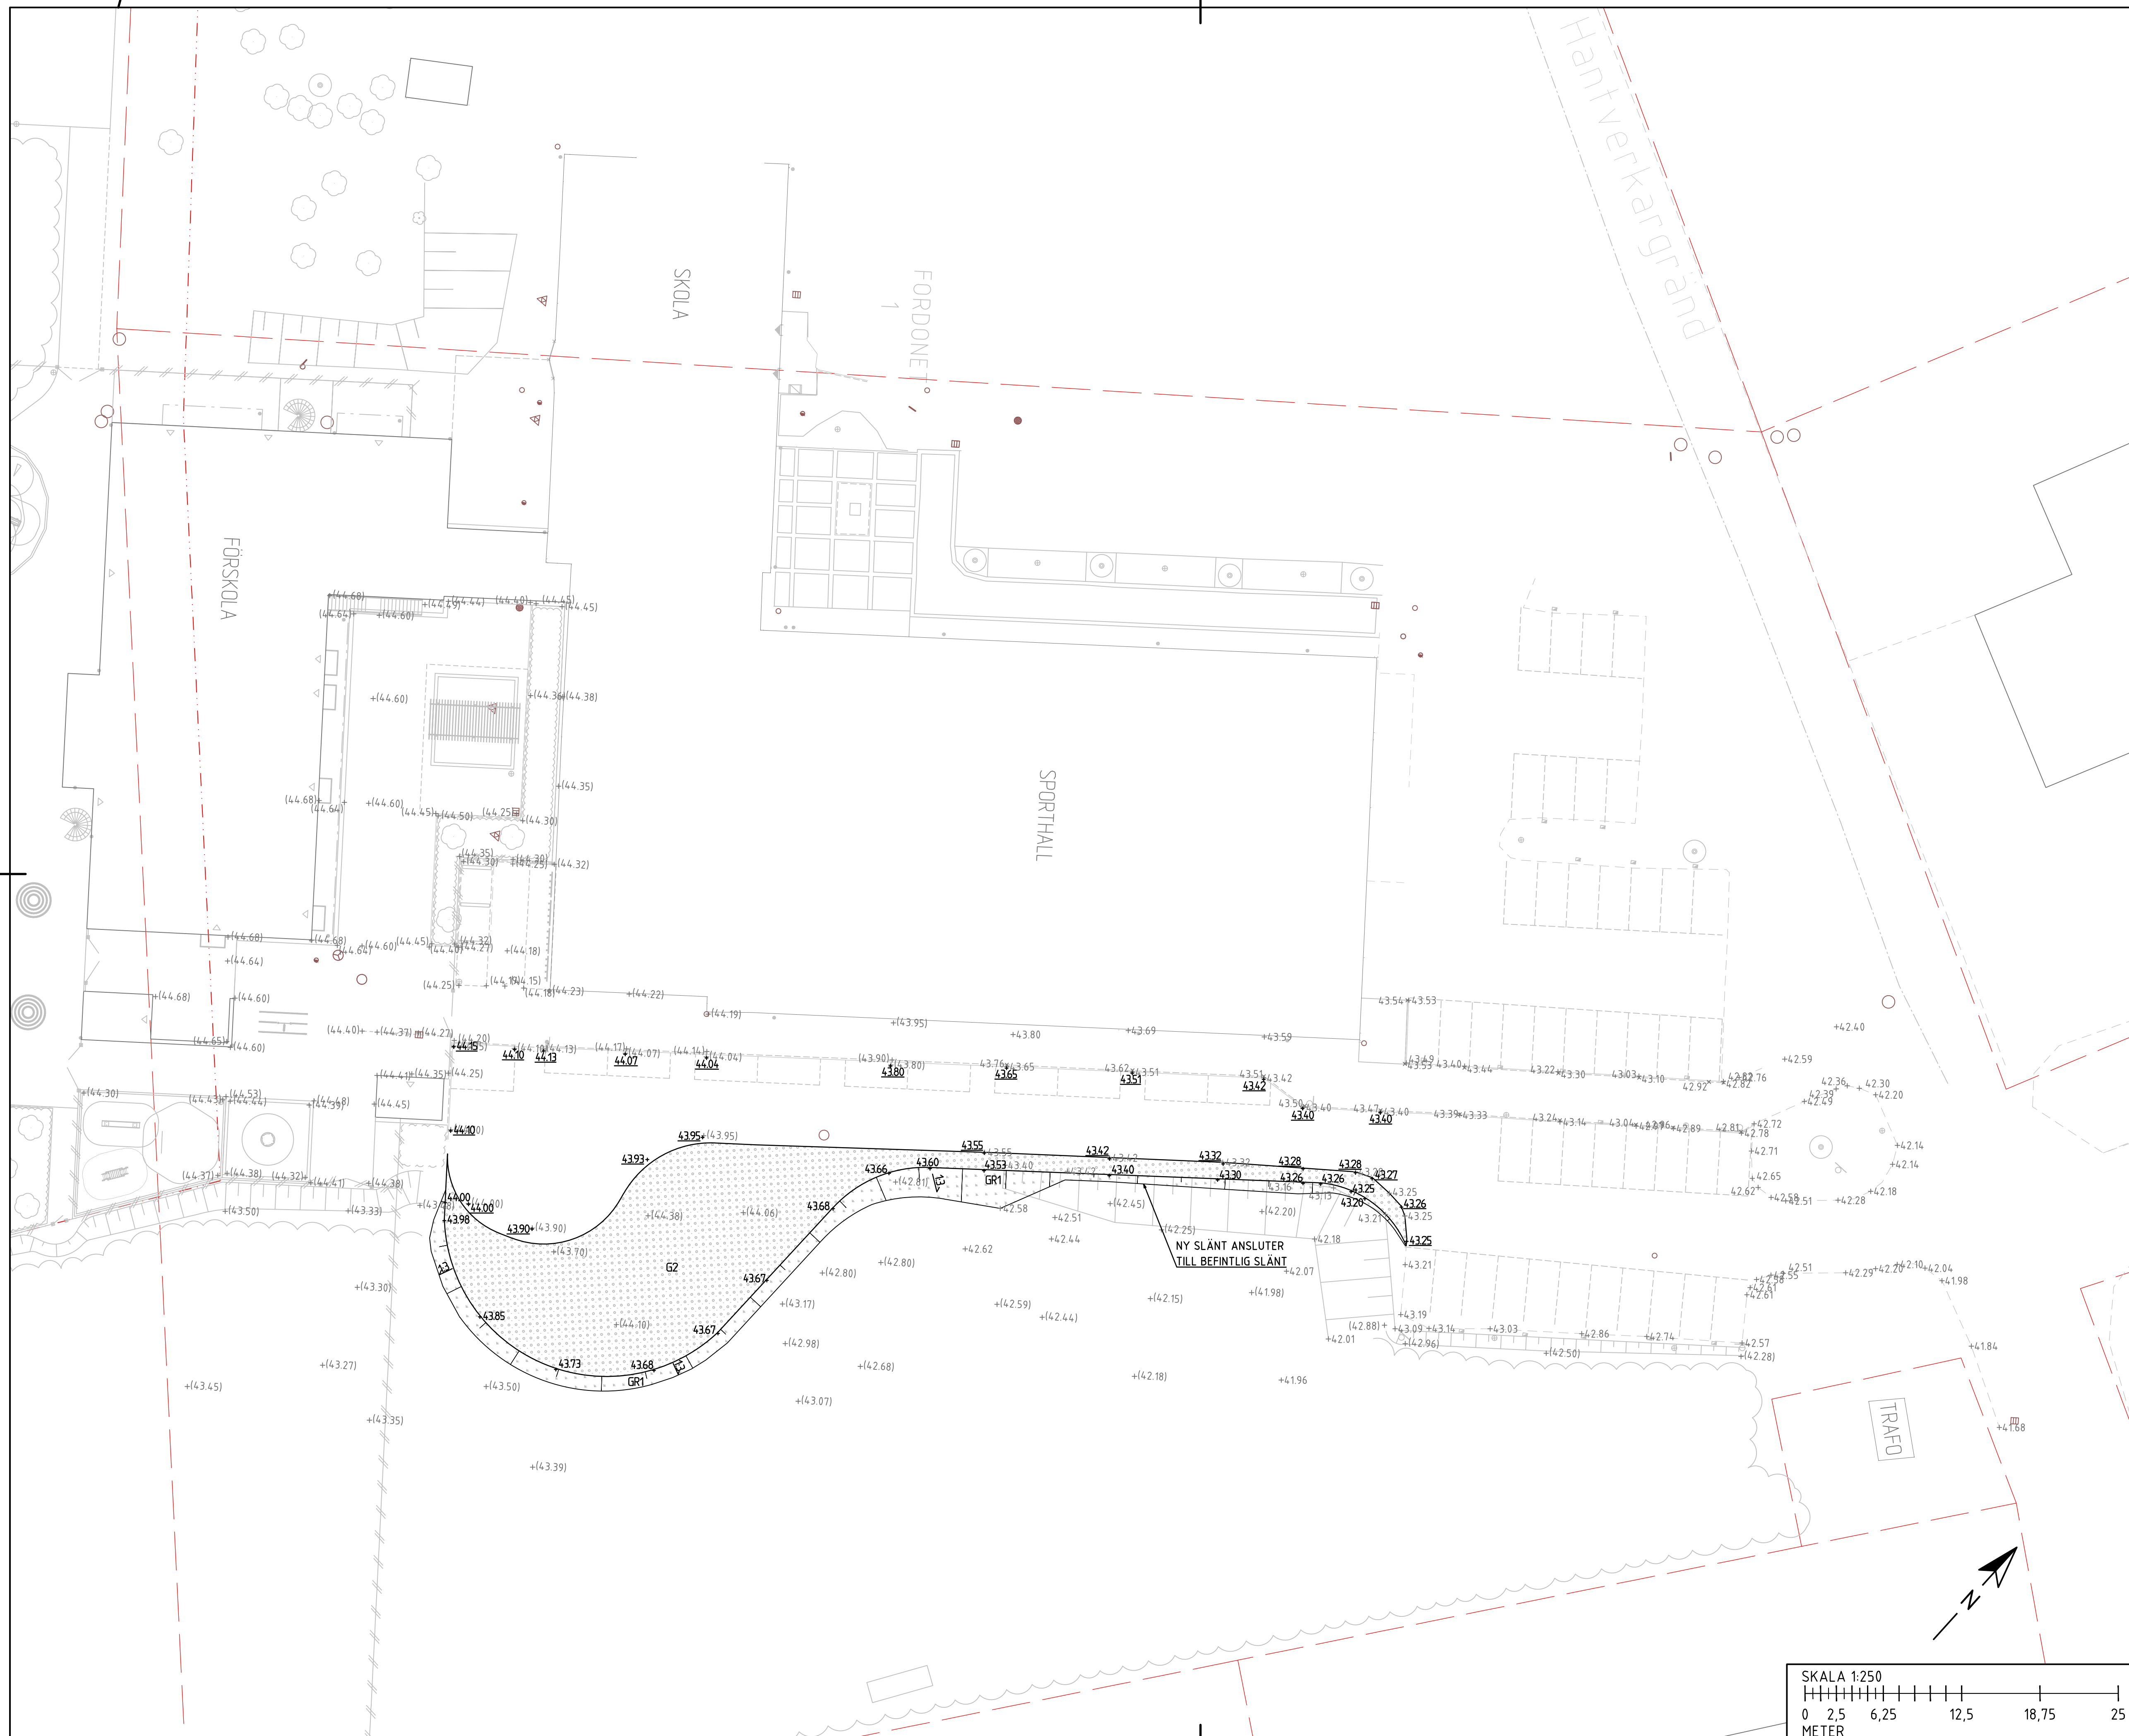

TECKENFÖRKLARING

+0.00
+(0.00)
+0.00
+0.00

FASTIGHETSGRÄNS
INMÄTTA HÖJDER
EJ INMÄTTA HÖJDER
PROJEKTERADE HÖJDER
BEFINTLIGA HÖJDER SOM BEHÅLLS

GR1

GZ

GRÄS

GRUS
40 MM SLITLAGER AV GRUS
80 MM BÄRLAGER
420 MM FÖRSTÄRKNINGSLAGER

ANMÄRKNING

KOORDINATSYSTEM SWEREFP99 2015
HÖJD SYSTEM RH2000

STATUS

FÖRFRÅGNINGSUNDERLAG

HANDLING

BYGGHANDLING

DATUM
2024-12-20

GÖDMANG AV

ÄNDRINGS PM

BESTÄLLARE

ROBERTSFORS

KOMMUN

PROJEKTNUMMER

CENTRALKÖK

OMRADE

ROBERTSFORS KOMMUN

PROJEKTNUMMER

ADRESS

DARIENUMMER

FASTIGHET

OBSERVATION

M

YTTRE RINGVÄGEN 4

FORDONET 1

DISCIPLIN

FORETAG

NORCONSULT SVERIGE AB

SIGNATUR

BYGGNADSNUMMER

VANNINGSPLAN

108 83 71

A/H

TELIFON

KONTAKTPERSON

010 141 80 00

TOMAS BERGSTRÖM

BYGGNADSVIRK

(FLUSHÖLD - (RH 2000))

+44.60, +45.07, +45.54 (FG)

DELKOMRAD

VANNINGSPLAN

VANNINGSDEL

DELKOMRAD

DELKOMRAD

SYSTEM

30 SAMMANSAATT REDOVISNING MARK

INFRASTRUKTUR

YTTSIKT OCH HÖJDER TILLFÄLIG VÄG

RITTINGSKATEGORI

SKALA

FORMAT

PLAN

1:250

A1

DOCUMENTNUMMER

ÄNDRING

M-31-1-002