


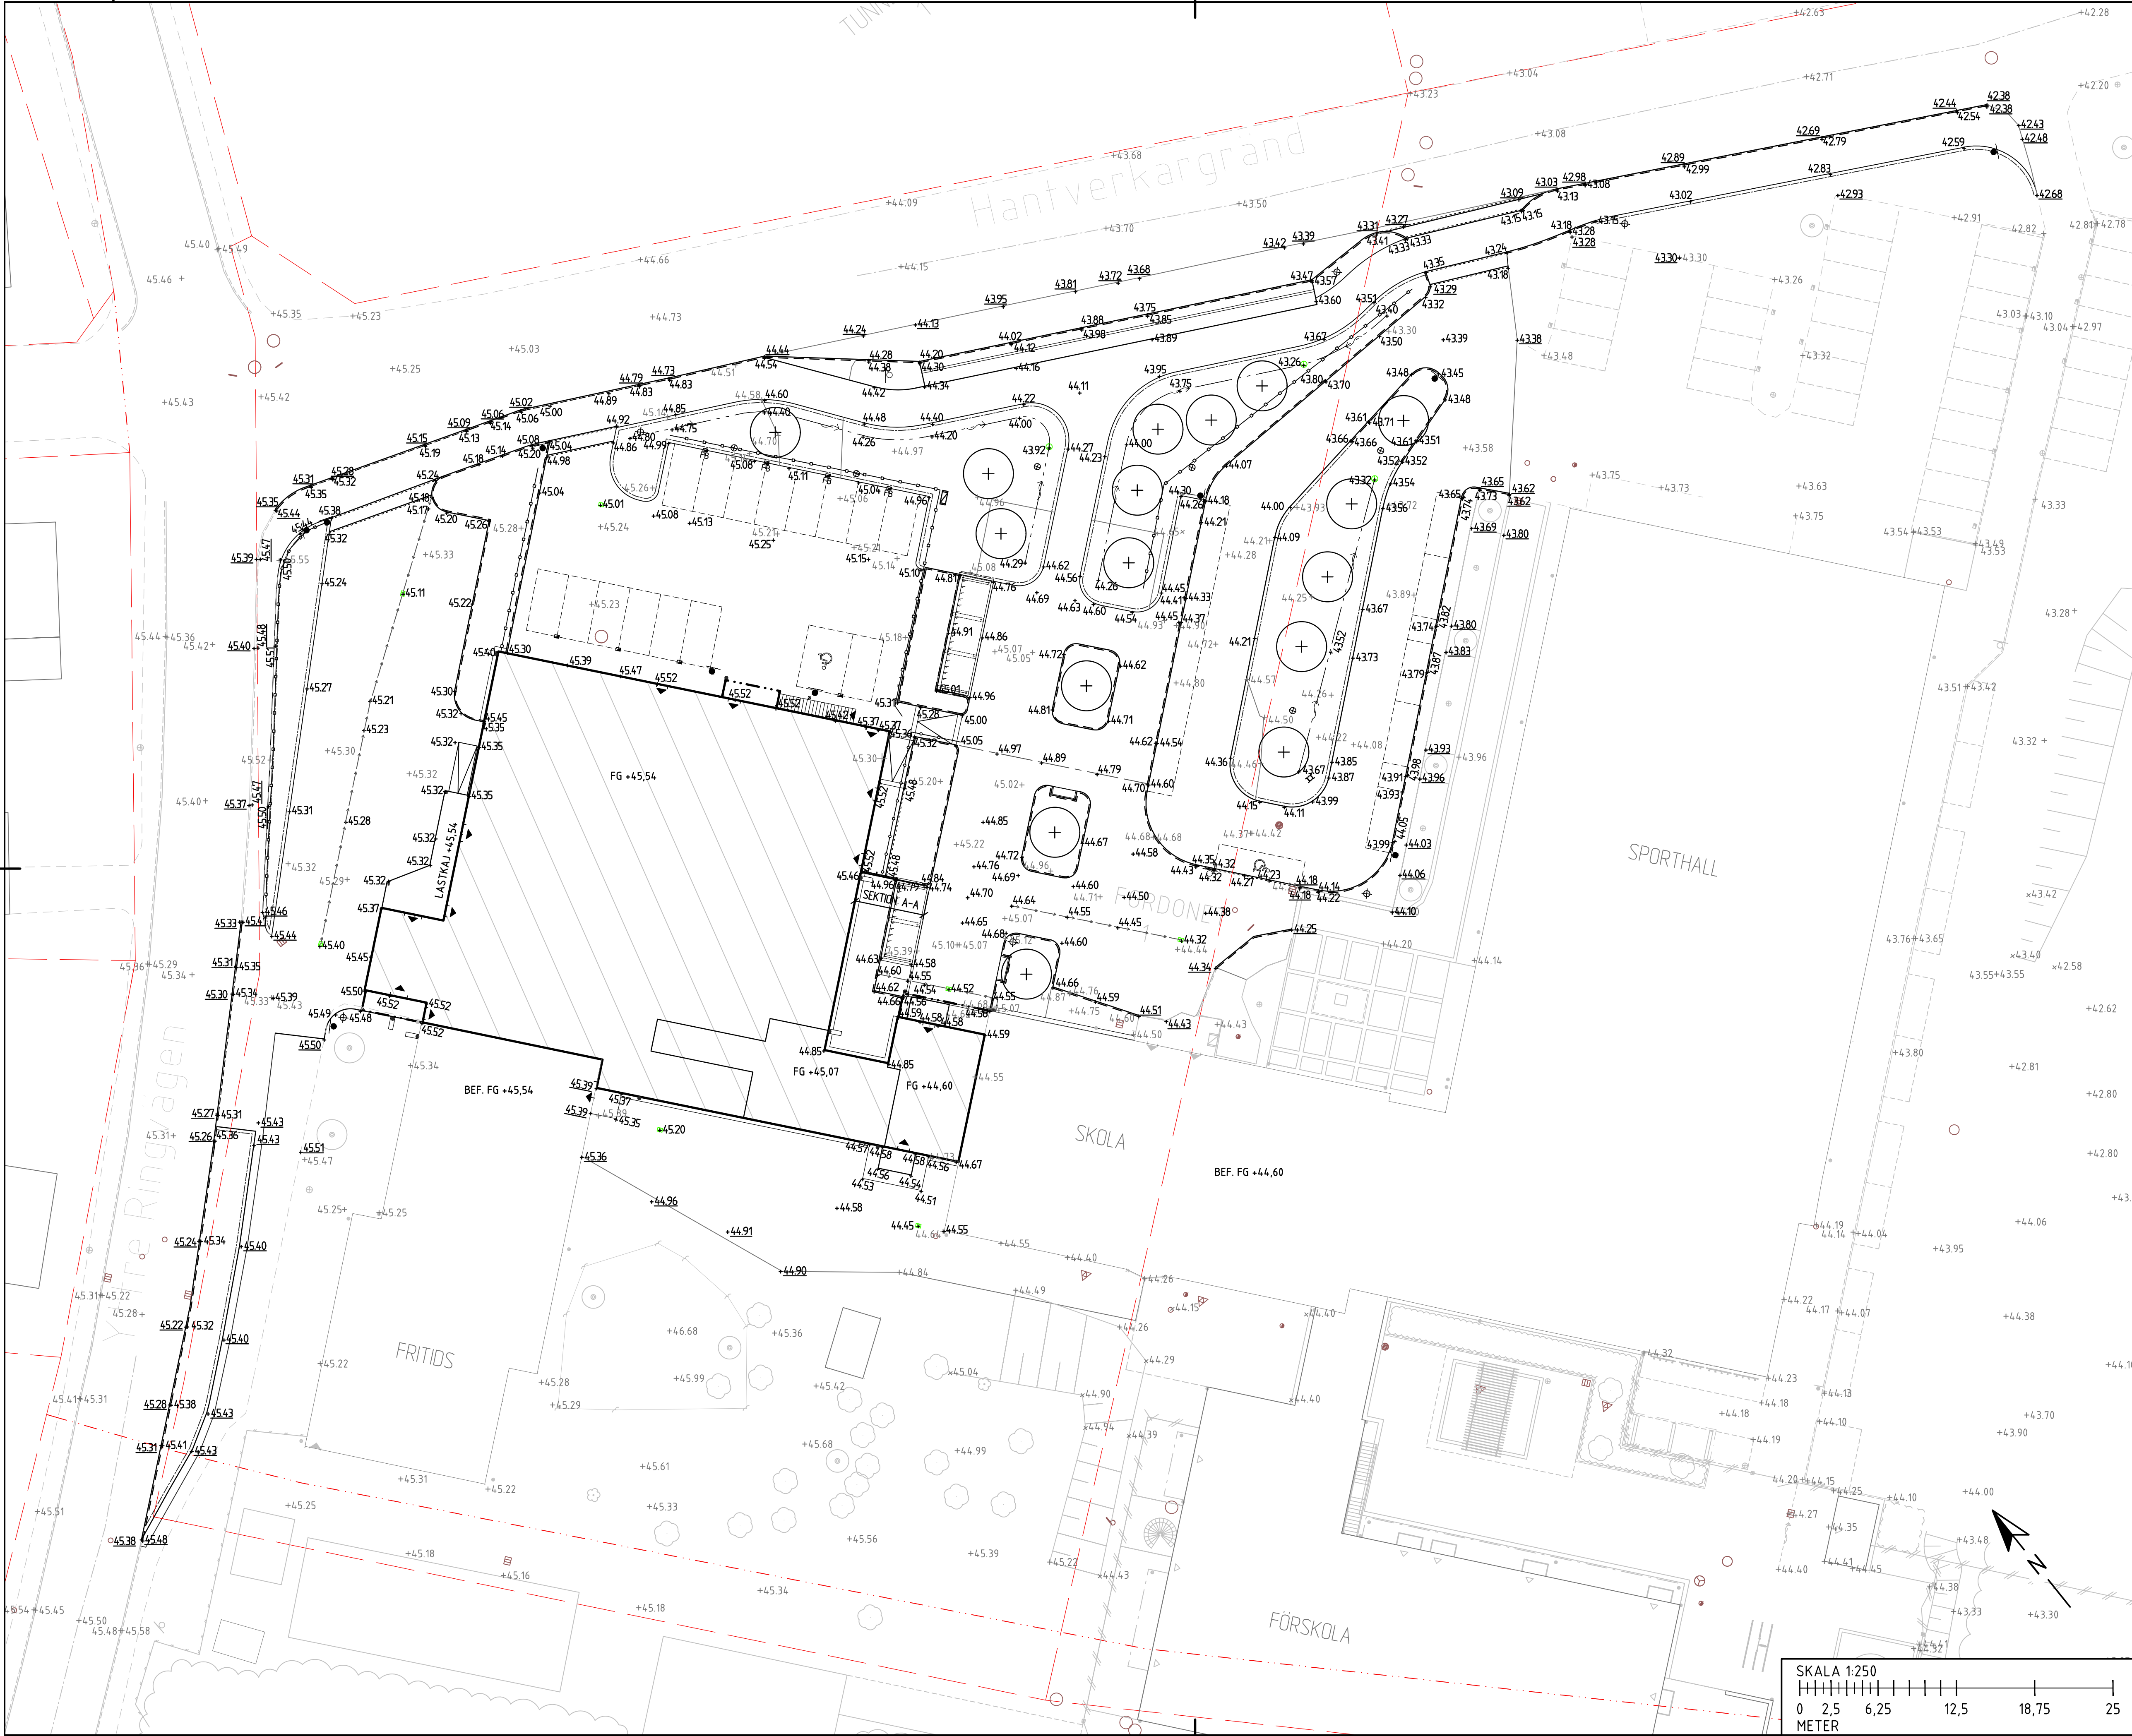

TECKENFÖRKLARING

+ 0.00

+0.00

+0.00

FASTIGHETSGRÄNS

INMÄTTA HÖJDER

PROJEKTERADE HÖJDER

BEFINTLIGA HÖJDER SOM BEHÅLLS

DAGVATTENBRUNN MED SANDFÄNG

KUPOLBRUNN

KS1, KANTSTÖD MED 100 MM

VISNING DÄR ANNAT EJ ANGES

KS2, KANTSTEN MED 0 MM

VISNING

KS3, KANTSTÖD FASAD 40 MM

VISNING

KS4, KANTSTEN MED 100 MM

VISNING DÄR ANNAT EJ ANGES

LÅGPUNKTSLINJE

HÖGPUNKTSLINJE

ANMÄRKNING

KOORDINATSYSTEM SWEREF99 2015

HÖJDSYSTEM RH2000

STATUS

FÖRFRÅGNINGSUNDERLAG

HANDLING

BYGGHANDLING

DATUM

2024-12-20

GODKÄND AV

ANDRINGS PM

BESTÄLLARE

ROBERTSFORS
KOMMUN

PROJEKTNAMN

CENTRALEKÖK

OMRÅDE

ROBERTSFORS KOMMUN

PROJEKTNUMMER

YTTERE RINGVÄGEN 4

DISCIPLIN

FORDONET 1

DISCIPLIN

NORCONSULT SVERIGE AB

UPPGIFTSNUMMER

108 83 71

SKAPAD AV

MAA

TELEFON

010 141 80 00

KONTAKTPERSON

TOMAS BERGSTRÖM

BYGGNADSVÄRME

PLUJHÖJD (RH 2000)

+44.60, +45.07, +45.54 (FG)

VÄNINGSPLAN

VÄNINGSDEL

DELOMRÅDE

SYSTEM

30 SAMMANSATT REDOVISNING MARK

DISPOSITION

HÖJDSÄTTNING

PLAN

SKALA

1:250

FORMAT

A1

DOKUMENTNUMMER

M-31-1-101

ANDRING

SKALA 1:250

0 2,5 6,25 12,5 18,75 25

METER