

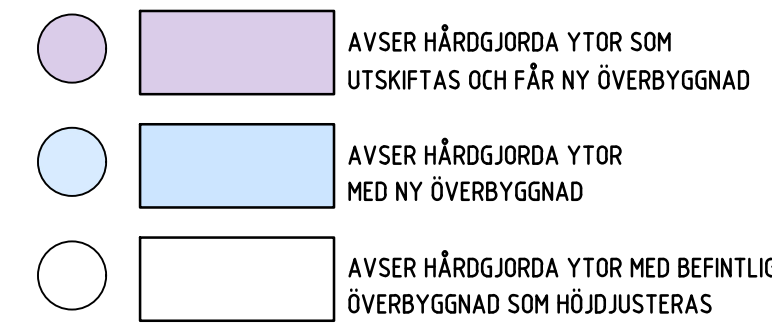
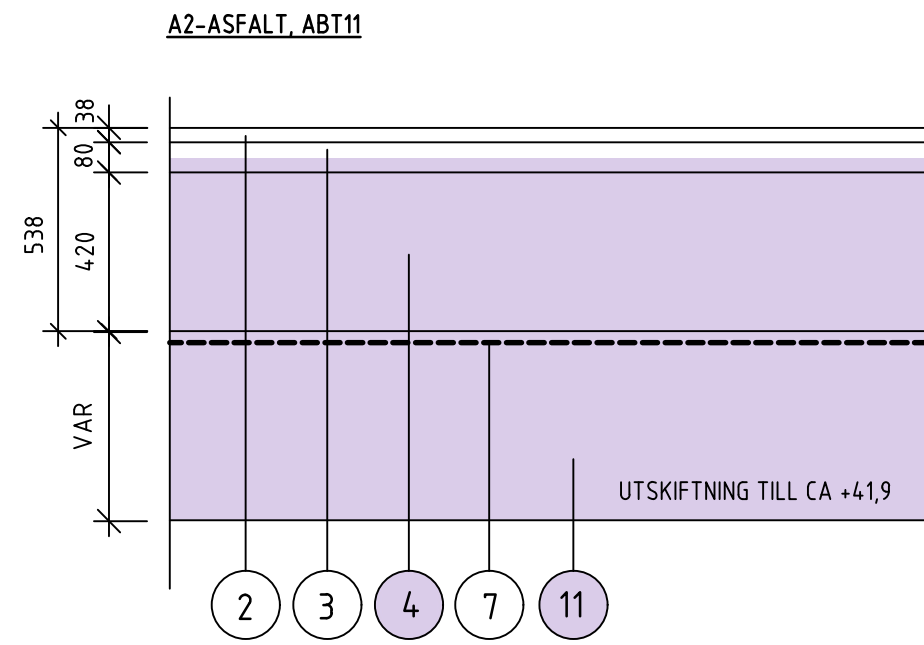
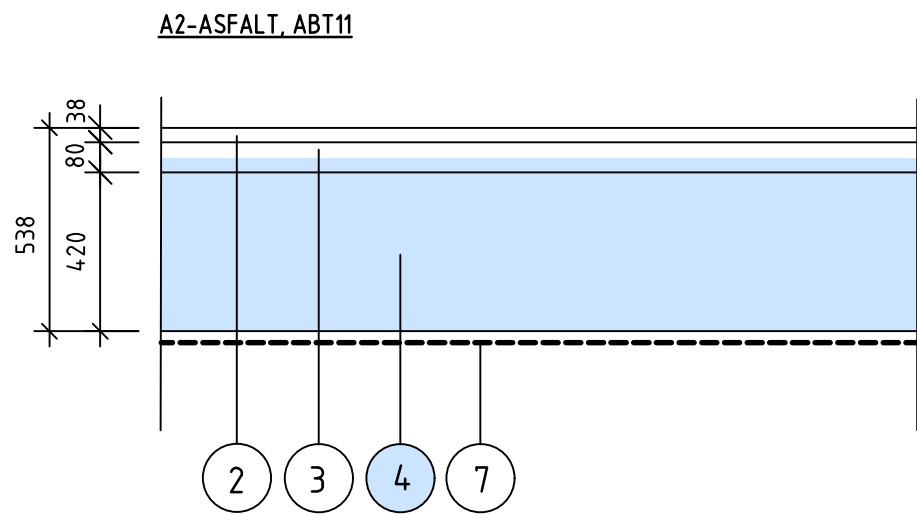
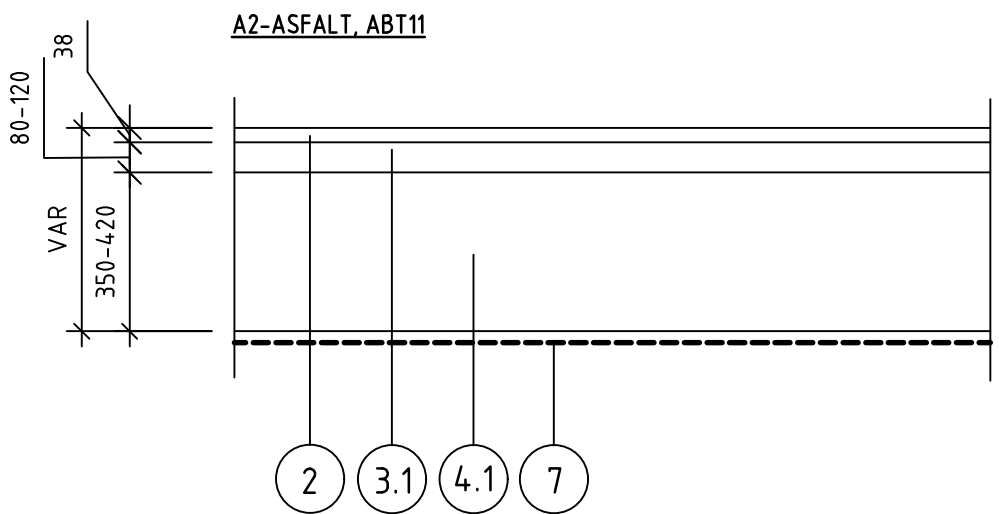
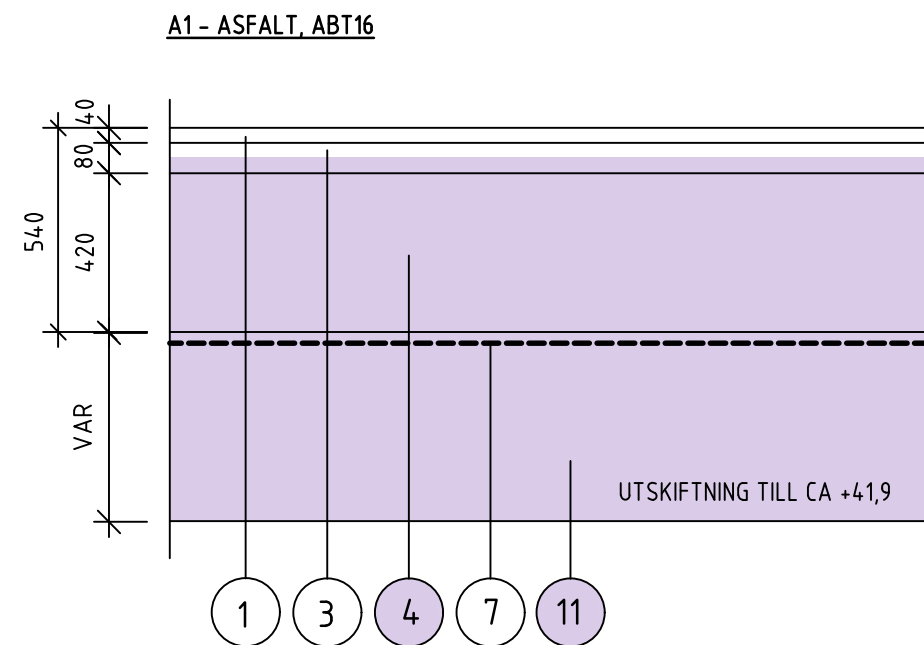
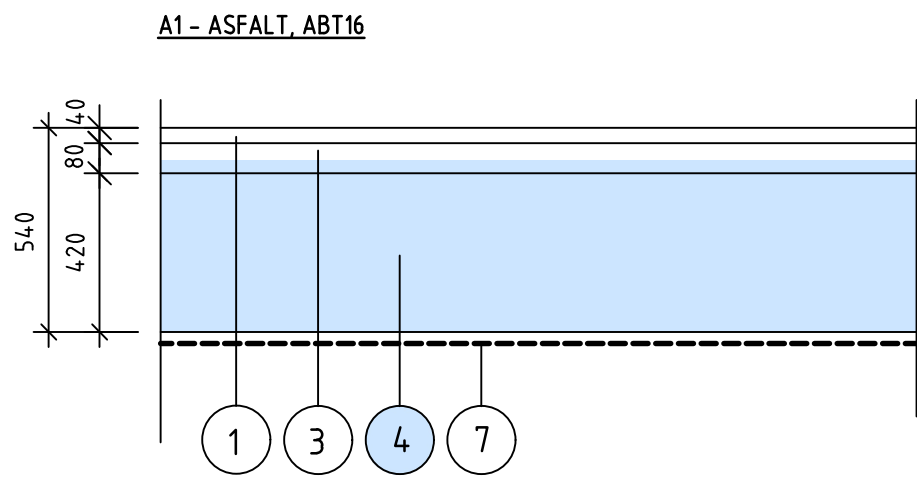
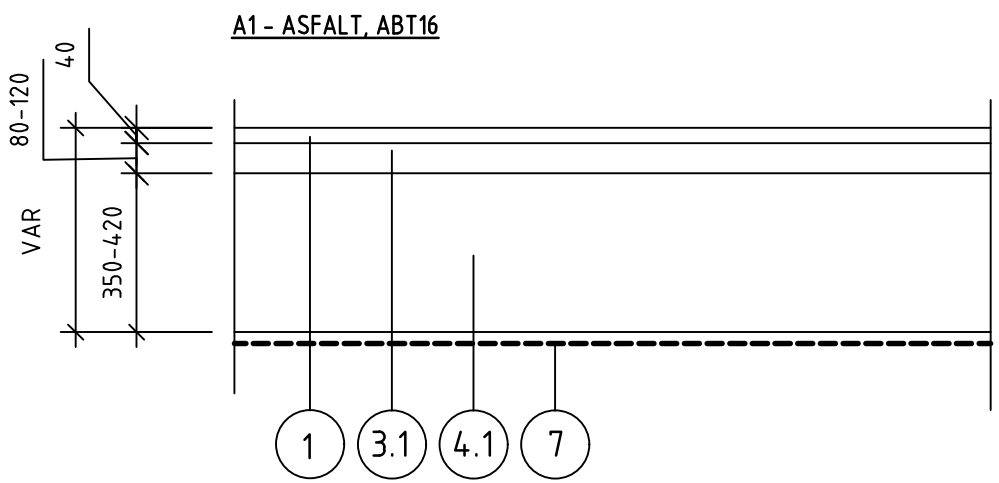
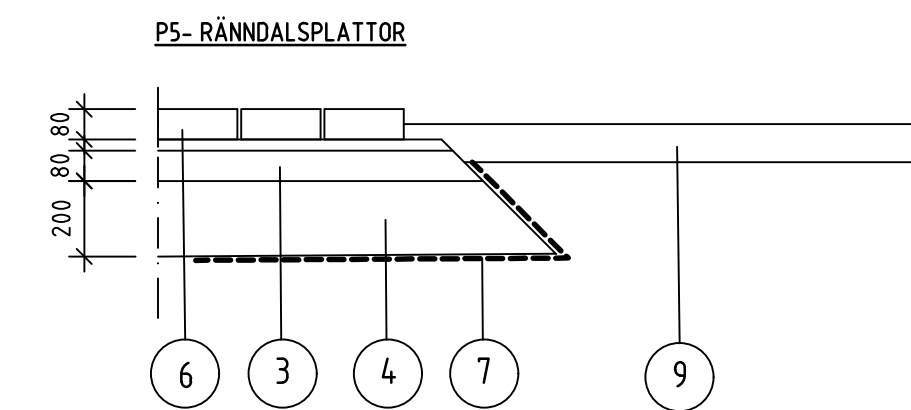
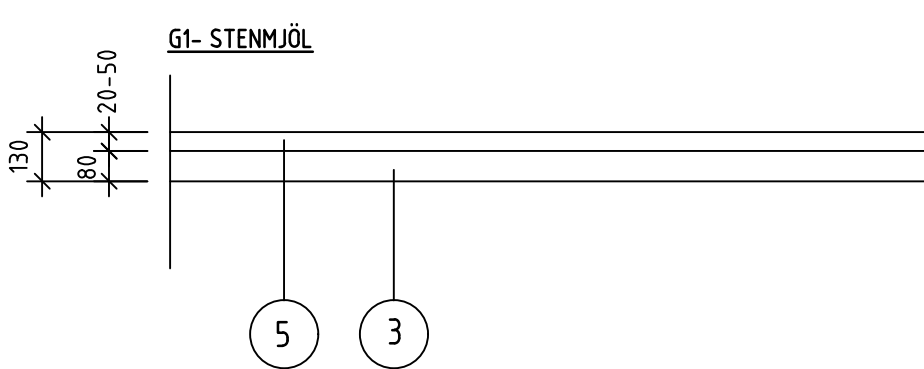
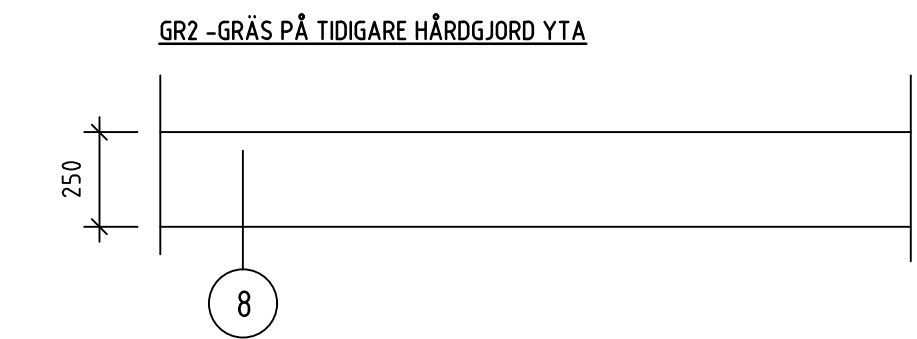
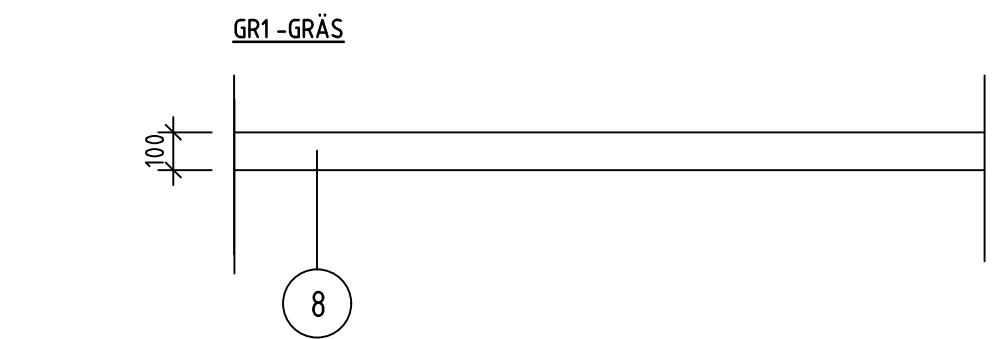
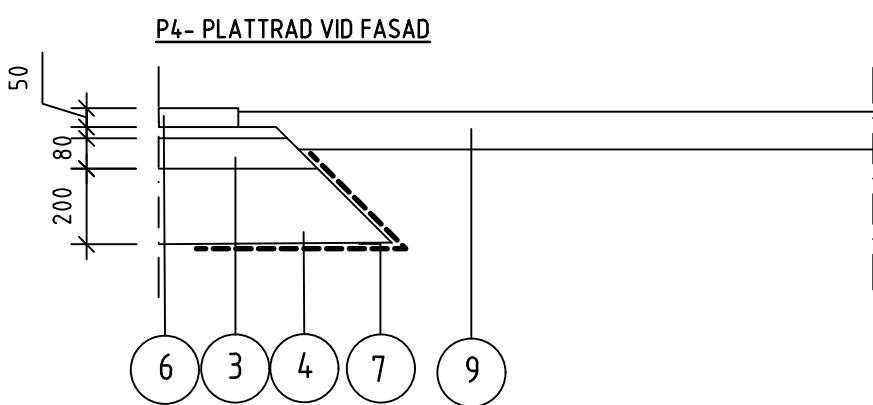
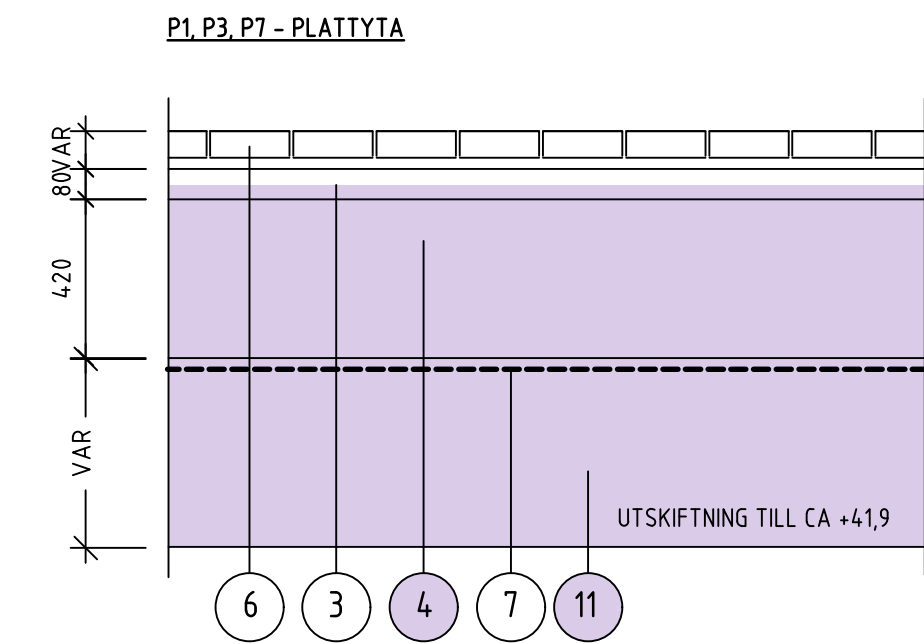
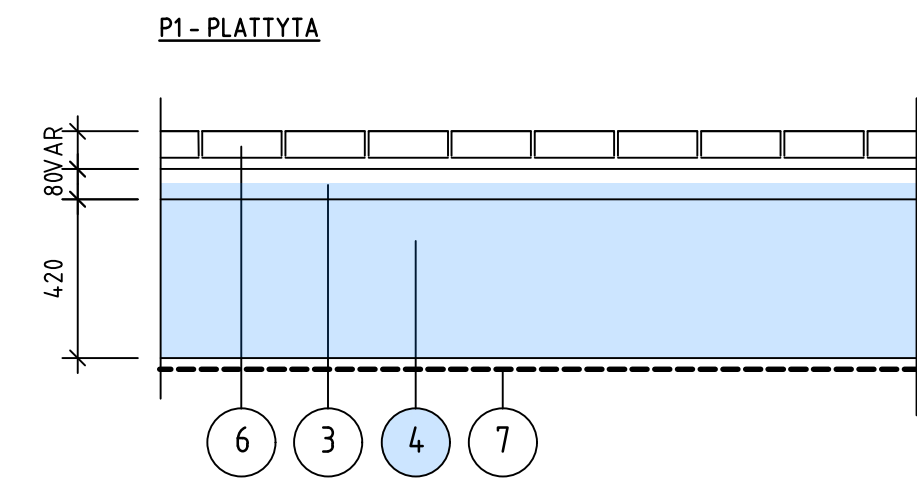
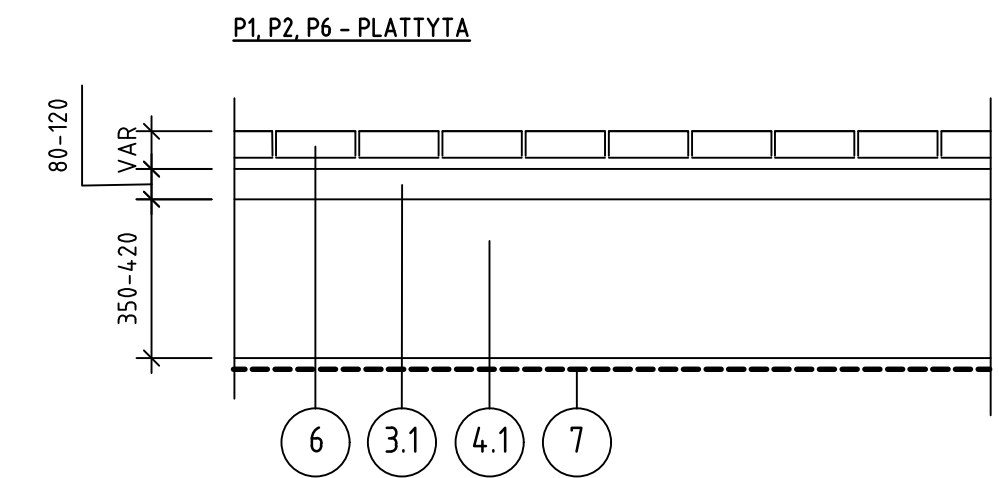
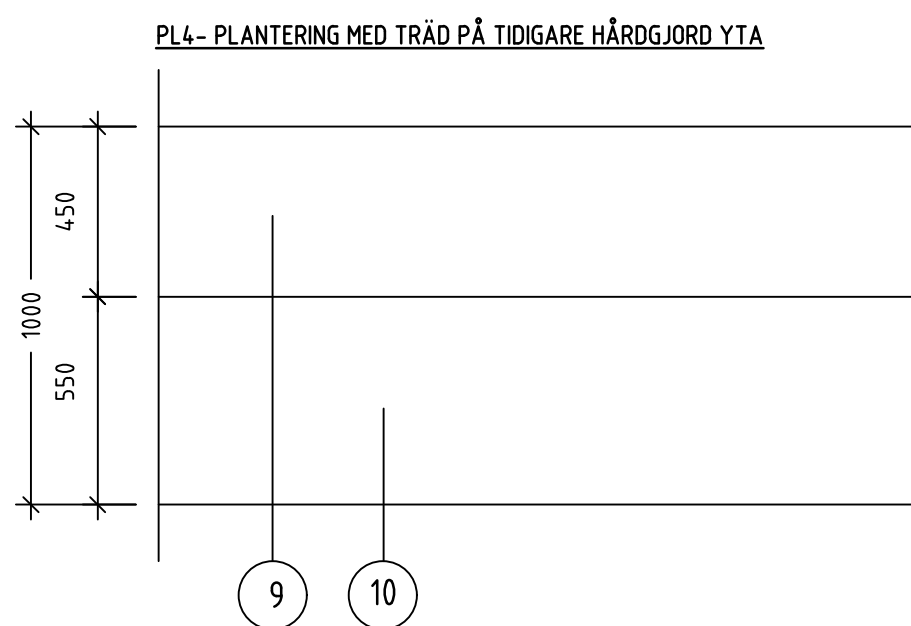
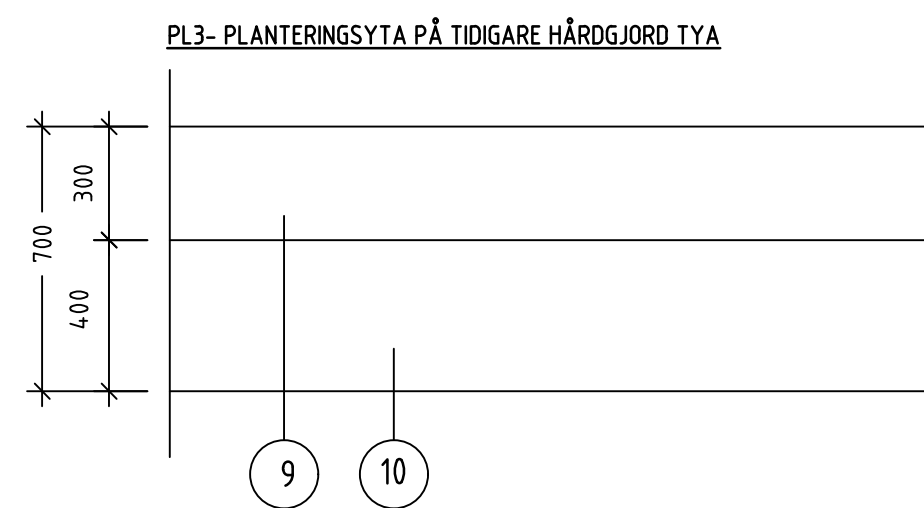


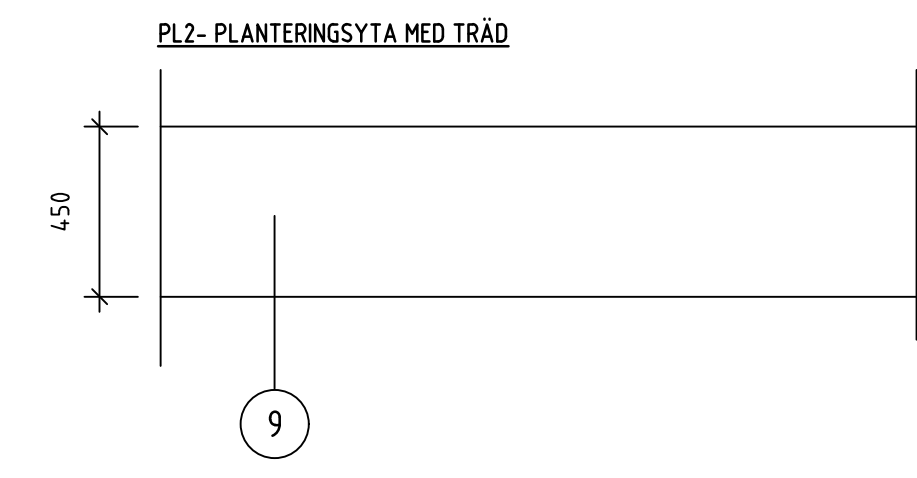


ANMÄRKNING
PLATTOR SOM ANGRÄNSAR MOT GRÄS/PLANTERINGSYTA
UTFÖRS MED INSPÄNNING ENLIGT PRINCIPRITNING DCG.

BETECKNINGAR		
NR	BENÄMNING	AMA-KOD
1	40 MM, ASFALT TYP ABT 16,	DCC.24.11
2	38 MM, ASFALT TYP ABT 11, 160/220	DCC.24.11
3	OBUNDET BÄRLAGER	DCB.312
3.1	JUSTERINGSLAGER AV OBUNDET BÄRLAGER	DCB.552
4	FÖRSTÄRKNINGSLAGER	DCB.212
4.1	JUSTERINGSLAGER AV FÖRSTÄRKNINGSLAGER	DCB.522
5	SLITLAGER AV STENMJÖL	DCB.42
6	BELÄGGNING AV BETONGMARKPLATTOR	DCG.21
7	GEOTEXTIL BRUKSKLASS N3	DOB.3131
8	VÄXTJORD TYP 2	DCL.1122
9	JORD A, ÖVRE VÄXTJORD	DCL.1121
10	JORD A, UNDER VÄXTJORD	DCL.1121
11	FYLLNING EFTER UTGRÄVNING FÖR VÄG KATEGORI A	CEB.7111

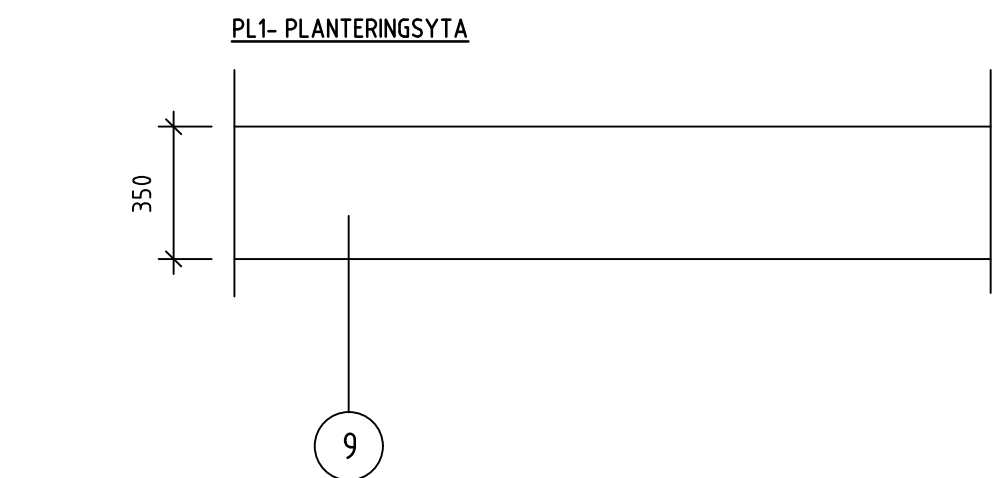

DETALJER ÖVERBYGGNAD
TYPSEKTION
SKALA 1:20 (mm)

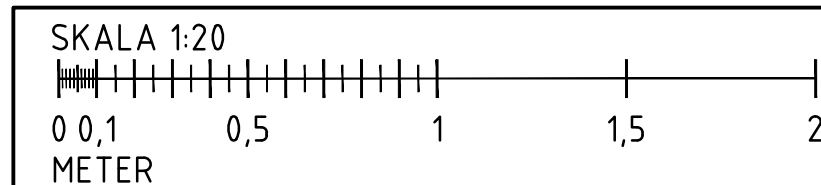

STATUS			
FÖRFRÅGNINGSUNDERLAG			
HANDLING			
BYGGHANDLING			
DATUM	2024-12-20		ODOKAND AV
BESTÄLLARE		ANDRINGS PM	
 ROBERTSFORS KOMMUN			
PROJEKTNAMN			
CENTRALEKÖK			
OMRADE			
ROBERTSFORS KOMMUN			
PROJEKTNUMMER	ADRESS		
YTRE RINGVÄGEN 4			
DIARIENUMMER	FASTIGHET		
FORDONET 1			
DISCIPLIN	FÖRETAG		
NORCONSULT SVERIGE AB			
OPPFÖRINGSNUMMER	SKAPAD AV		
108 83 71 AVH			
TELEFON	KONTAKTPERSON		
010 141 80 00 TOMAS BERGSTRÖM			
BYGGNADSVÄRKE	FLISSTÖCK (RM 2000)		
VÄNINGSPLAN	VÄNINGSDEL	DELOMRADE	
SYSTEM			
30 SAMMANSATT REDOVISNING MARK			
ÖVERBYGGNAD			
RITNINGSKATEGORI		SKALA	FORMAT
DETALJ		1:20	A1
DOKUMENTNUMMER		ANDRING	
M-31-6-001			