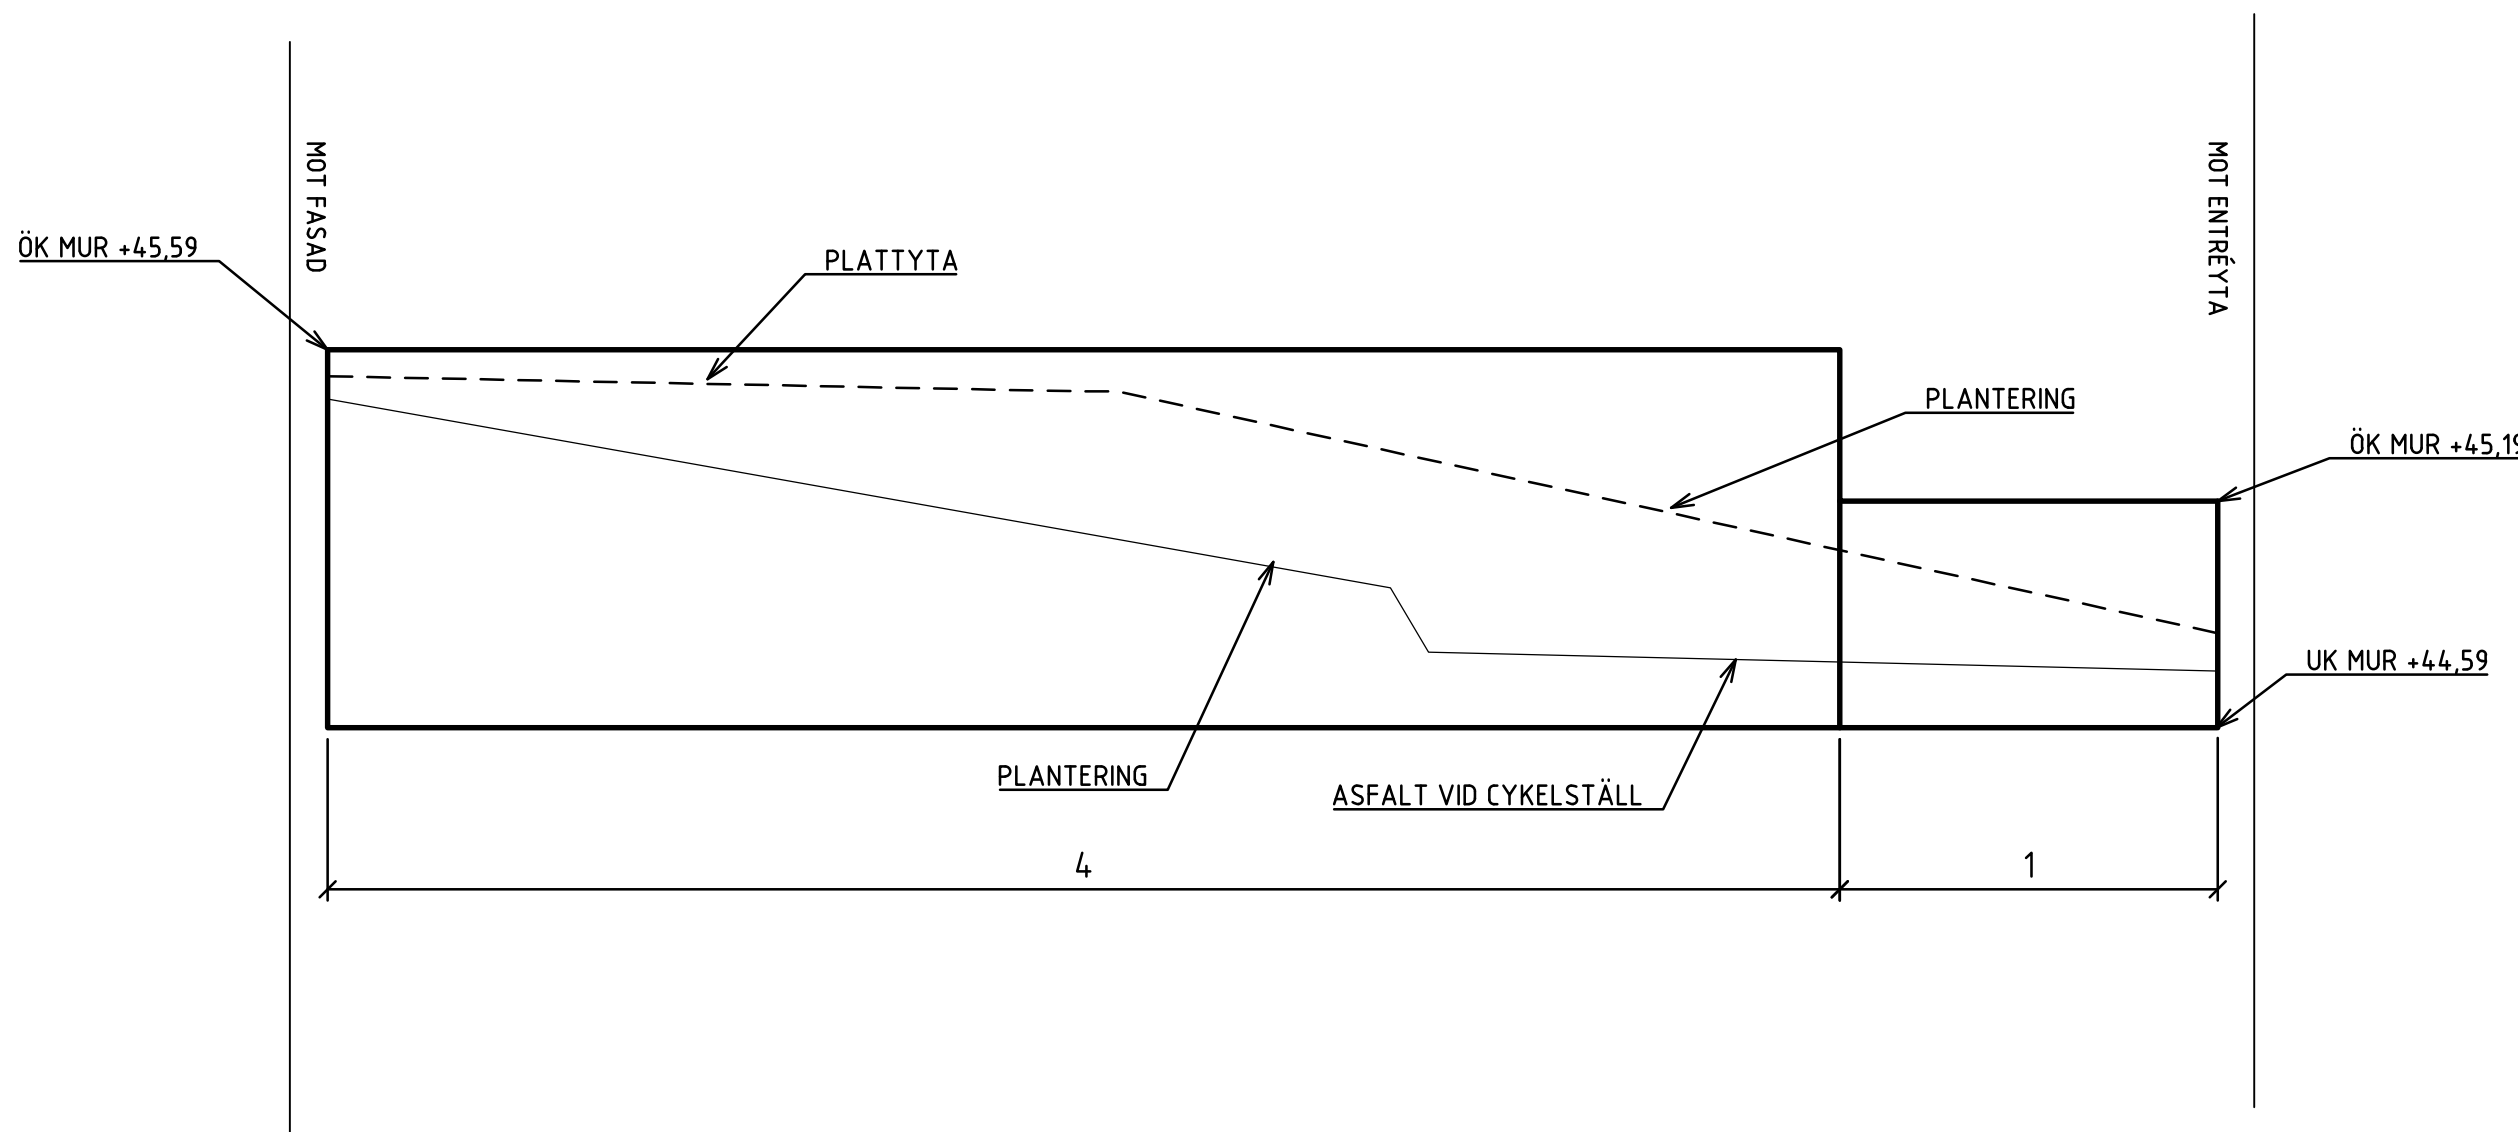


STATUS			
FÖRFRÅGNINGSUNDERLAG			
HANDLING			
BYGGHANDLING			
DATUM		GODKÄND AV	
2024-12-20			
BESTÄLLARE			
 ROBERTSFORS KOMMUN			
PROJEKTNAMN			
CENTRAALKÖK			
OMRADE			
ROBERTSFORS KOMMUN			
PROJEKTNUMMER		ADRESS	
		YTTRE RINGVÄGEN 4	
DIARIENUMMER		FASTIGHET	
		FORDONET 1	
DISCIPLIN		FÖRETAG	
M		NORCONSULT SVERIGE AB	
UPPDRAGSNUMMER		SKAPAD AV	
108 83 71		AVH	
TELEFON		KONTAKTPERSON	
010 141 80 00		TOMAS BERGSTRÖM	
BYGGNADSVÄRKE		FLISKHÖJD (RM 2008)	
VÄNINGSPLAN		VÄNINGSDEL	
		DELOMRADE	
SYSTEM			
30 SAMMANSATT REDOVISNING MARK			
L-STÖD			
RITNINGSKATEGORI		SKALA	FORMAT
DETALJ		1:20	A1
DOKUMENTNUMMER		ÄNDRING	
M-31-6-002			