


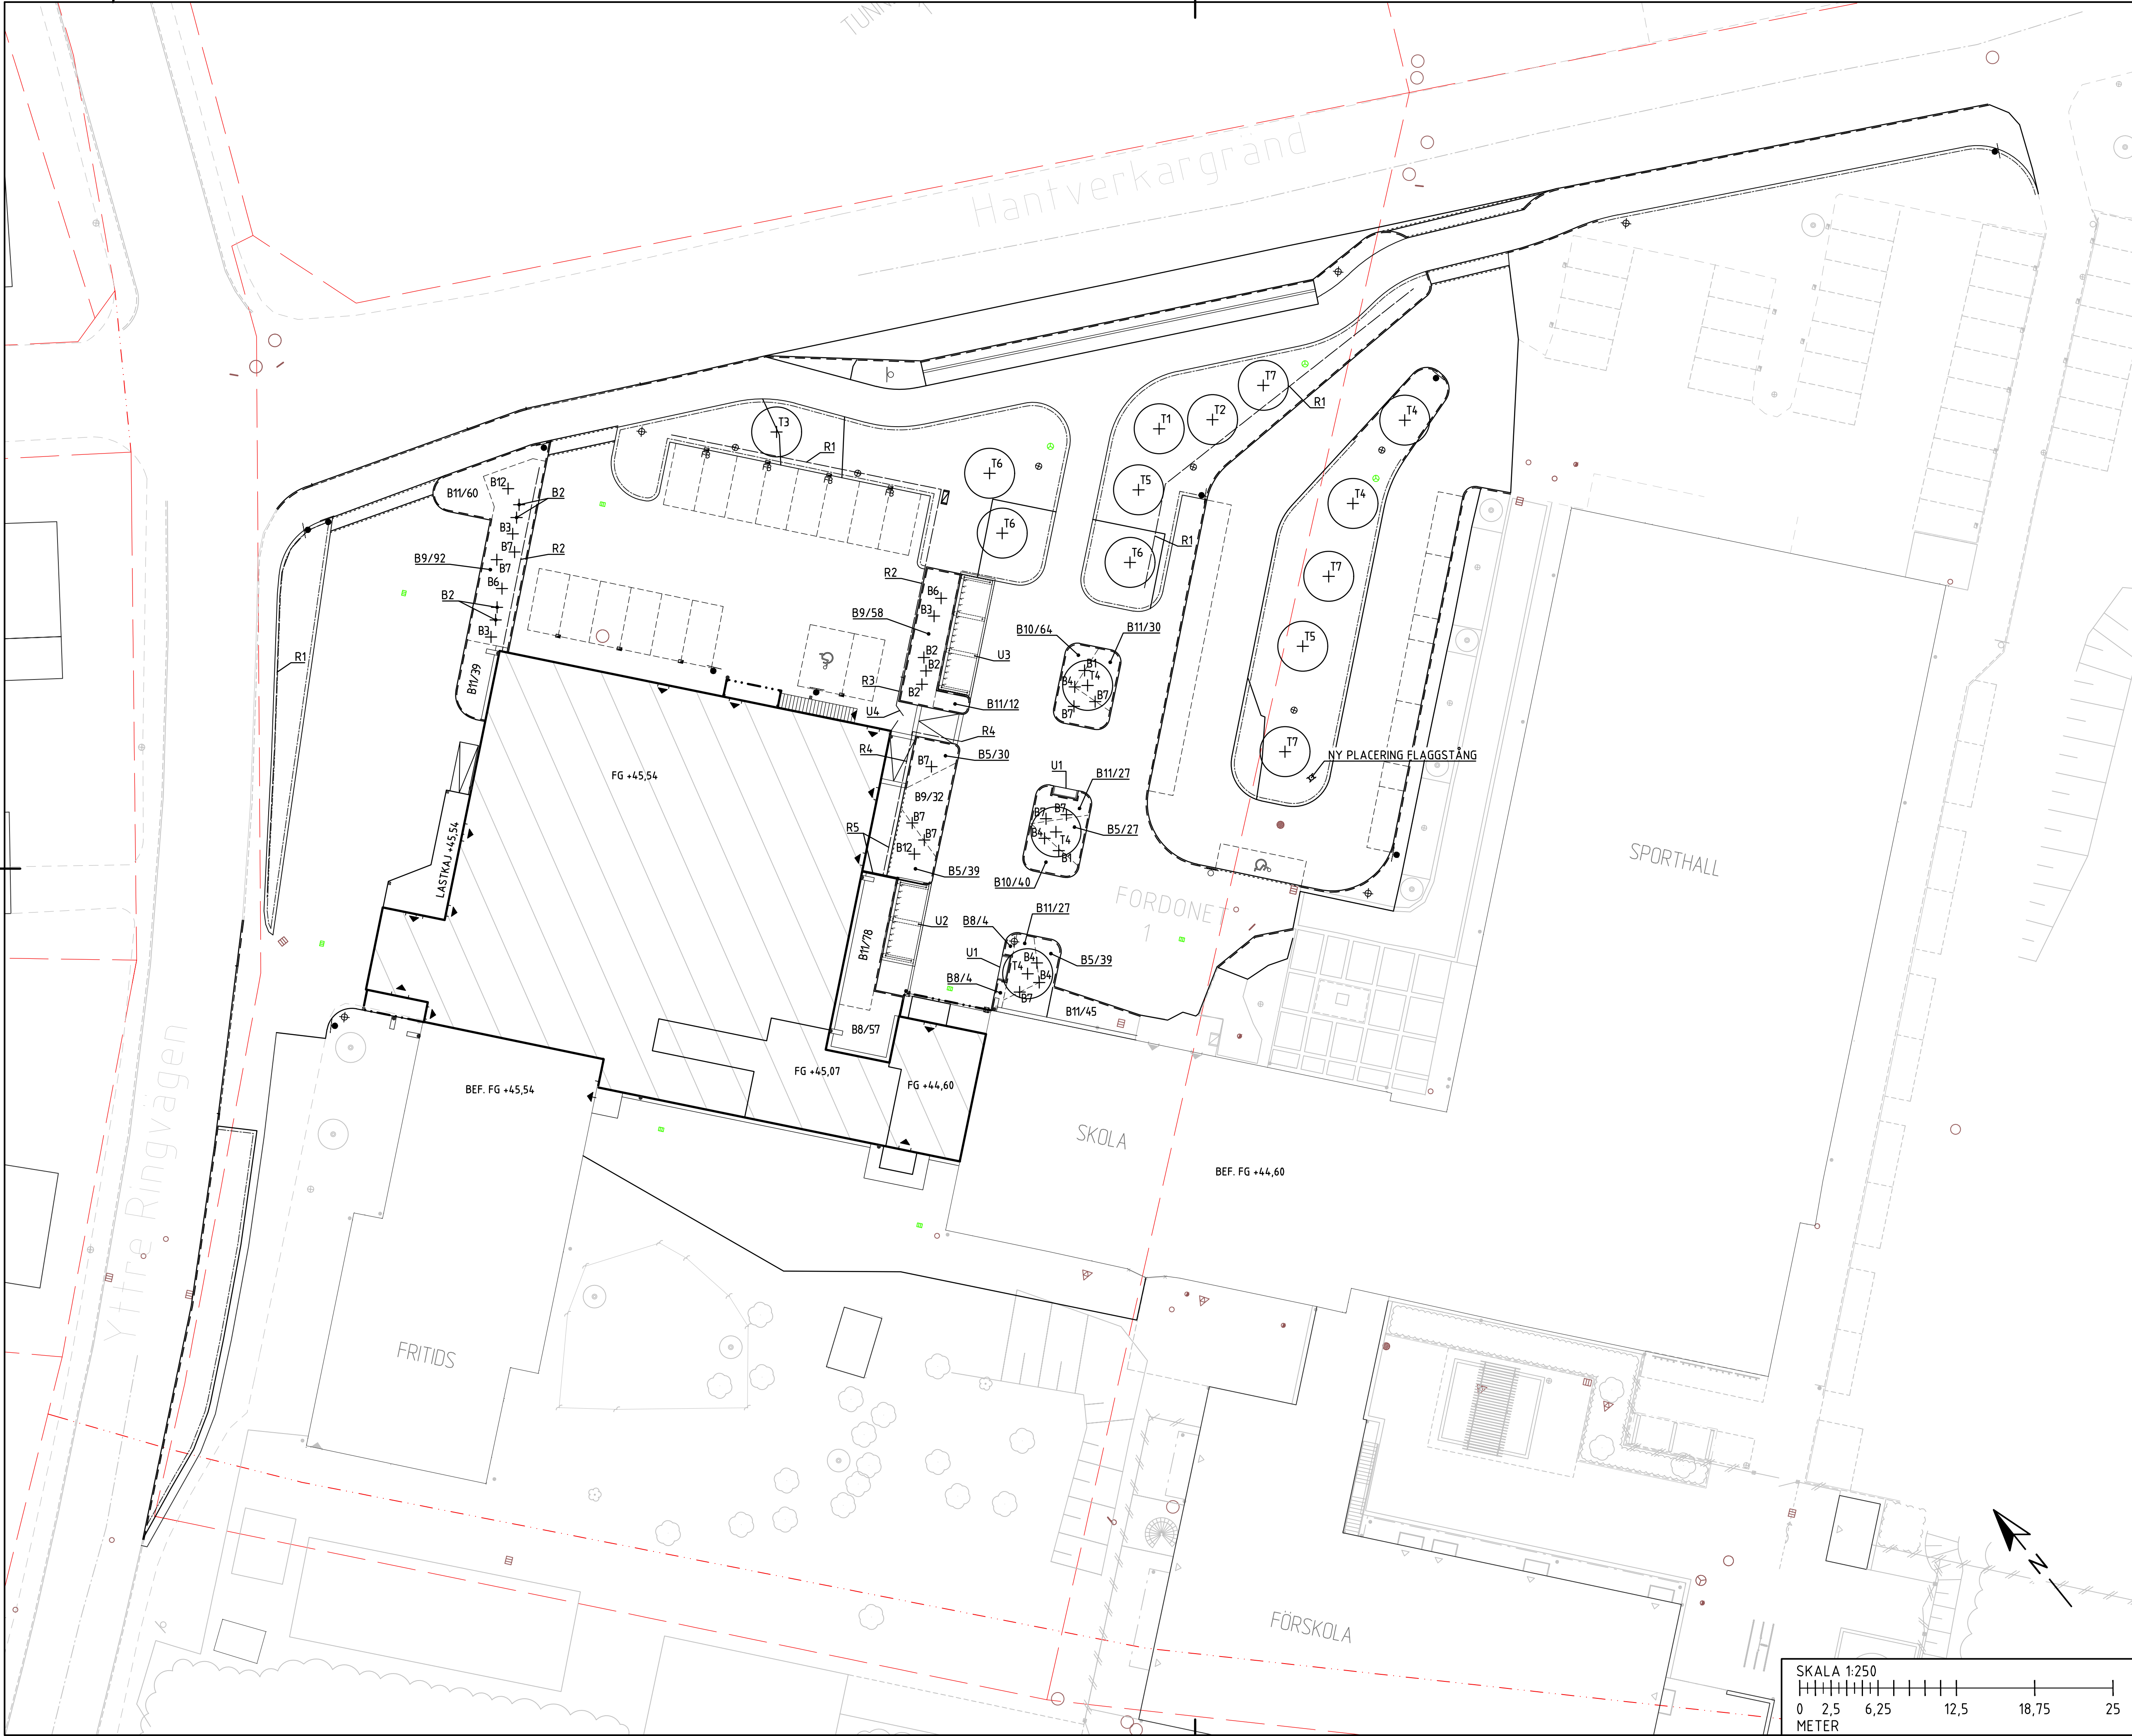

FASTIGHETSGRÄNS

U1, SOFFA

U2, CYKELTAK

U3, CYKELTAK

U4, GRIND

R1, RÄCKE, 3-RÄCKESRÖR

R2, RÄCKE MED SPJÄLOR

R3, INDUSTRISTÄNGSEL

R4, HANDELDARE RAMP

R5, HANDELDARE

BX/XX

BUSKE SOM PLANTERAS
ART/ANTAL

TX

TRÄD SOM PLANTERAS
ART ENLIGT VÄXTFÖRTECKNING

BX

SOLITÄRBUSKE SOM PLANTERAS
ART ENLIGT VÄXTFÖRTECKNING

NY PLACERING AV BEF.
FLAGGSTÄNG

ARTER ENLIGT BILAGA 1 VÄXTFÖRTECKNING

ANMÄRKNING

KOORDINATSYSTEM SWEREF99 2015

HÖJDSYSTEM RH2000

STATUS

FÖRFRÅGNINGSUNDERLAG

HANDLING

BYGGHANDLING

DATUM

2024-12-20

GODKÄND AV

ÄNDRINGS PM

BESTÄLLARE

ROBERTSFORS

KOMMUN

PROJEKTNAMN

CENTRALKÖK

OMRÅDE

ROBERTSFORS KOMMUN

PROJEKTNUMMER

YTTRE RINGVÄGEN 4

DIARIENUMMER

FASTIGHET

FORDONET 1

DISCIPLIN

FÖRETAG

NORCONSULT SVERIGE AB

UPPDRAGSNUMMER

SKAPAD AV

ASE

TELEFON

KONTAKTPERSON

010 141 80 00

TOMAS BERGSTRÖM

BYGGNADSVÄRKE

FÖRHÖJD (RH 2000)

+44.60, +45.07, +45.54 (FG)

VÄNINGSPLAN

VÄNINGSDEL

DELOMRÅDE

SYSTEM

30 SAMMANSATT REDOVISNING MARK

DESIGNATOR

PLANTERING- OCH UTRUSTNING

RITNINGSKATEGORI

PLAN

SKALA

1:250

FORMAT

A1

DOKUMENTNUMMER

M-32-1-001

ÄNDRING

SKALA 1:250

0

2,5

6,25

12,5

18,75

25

METER