


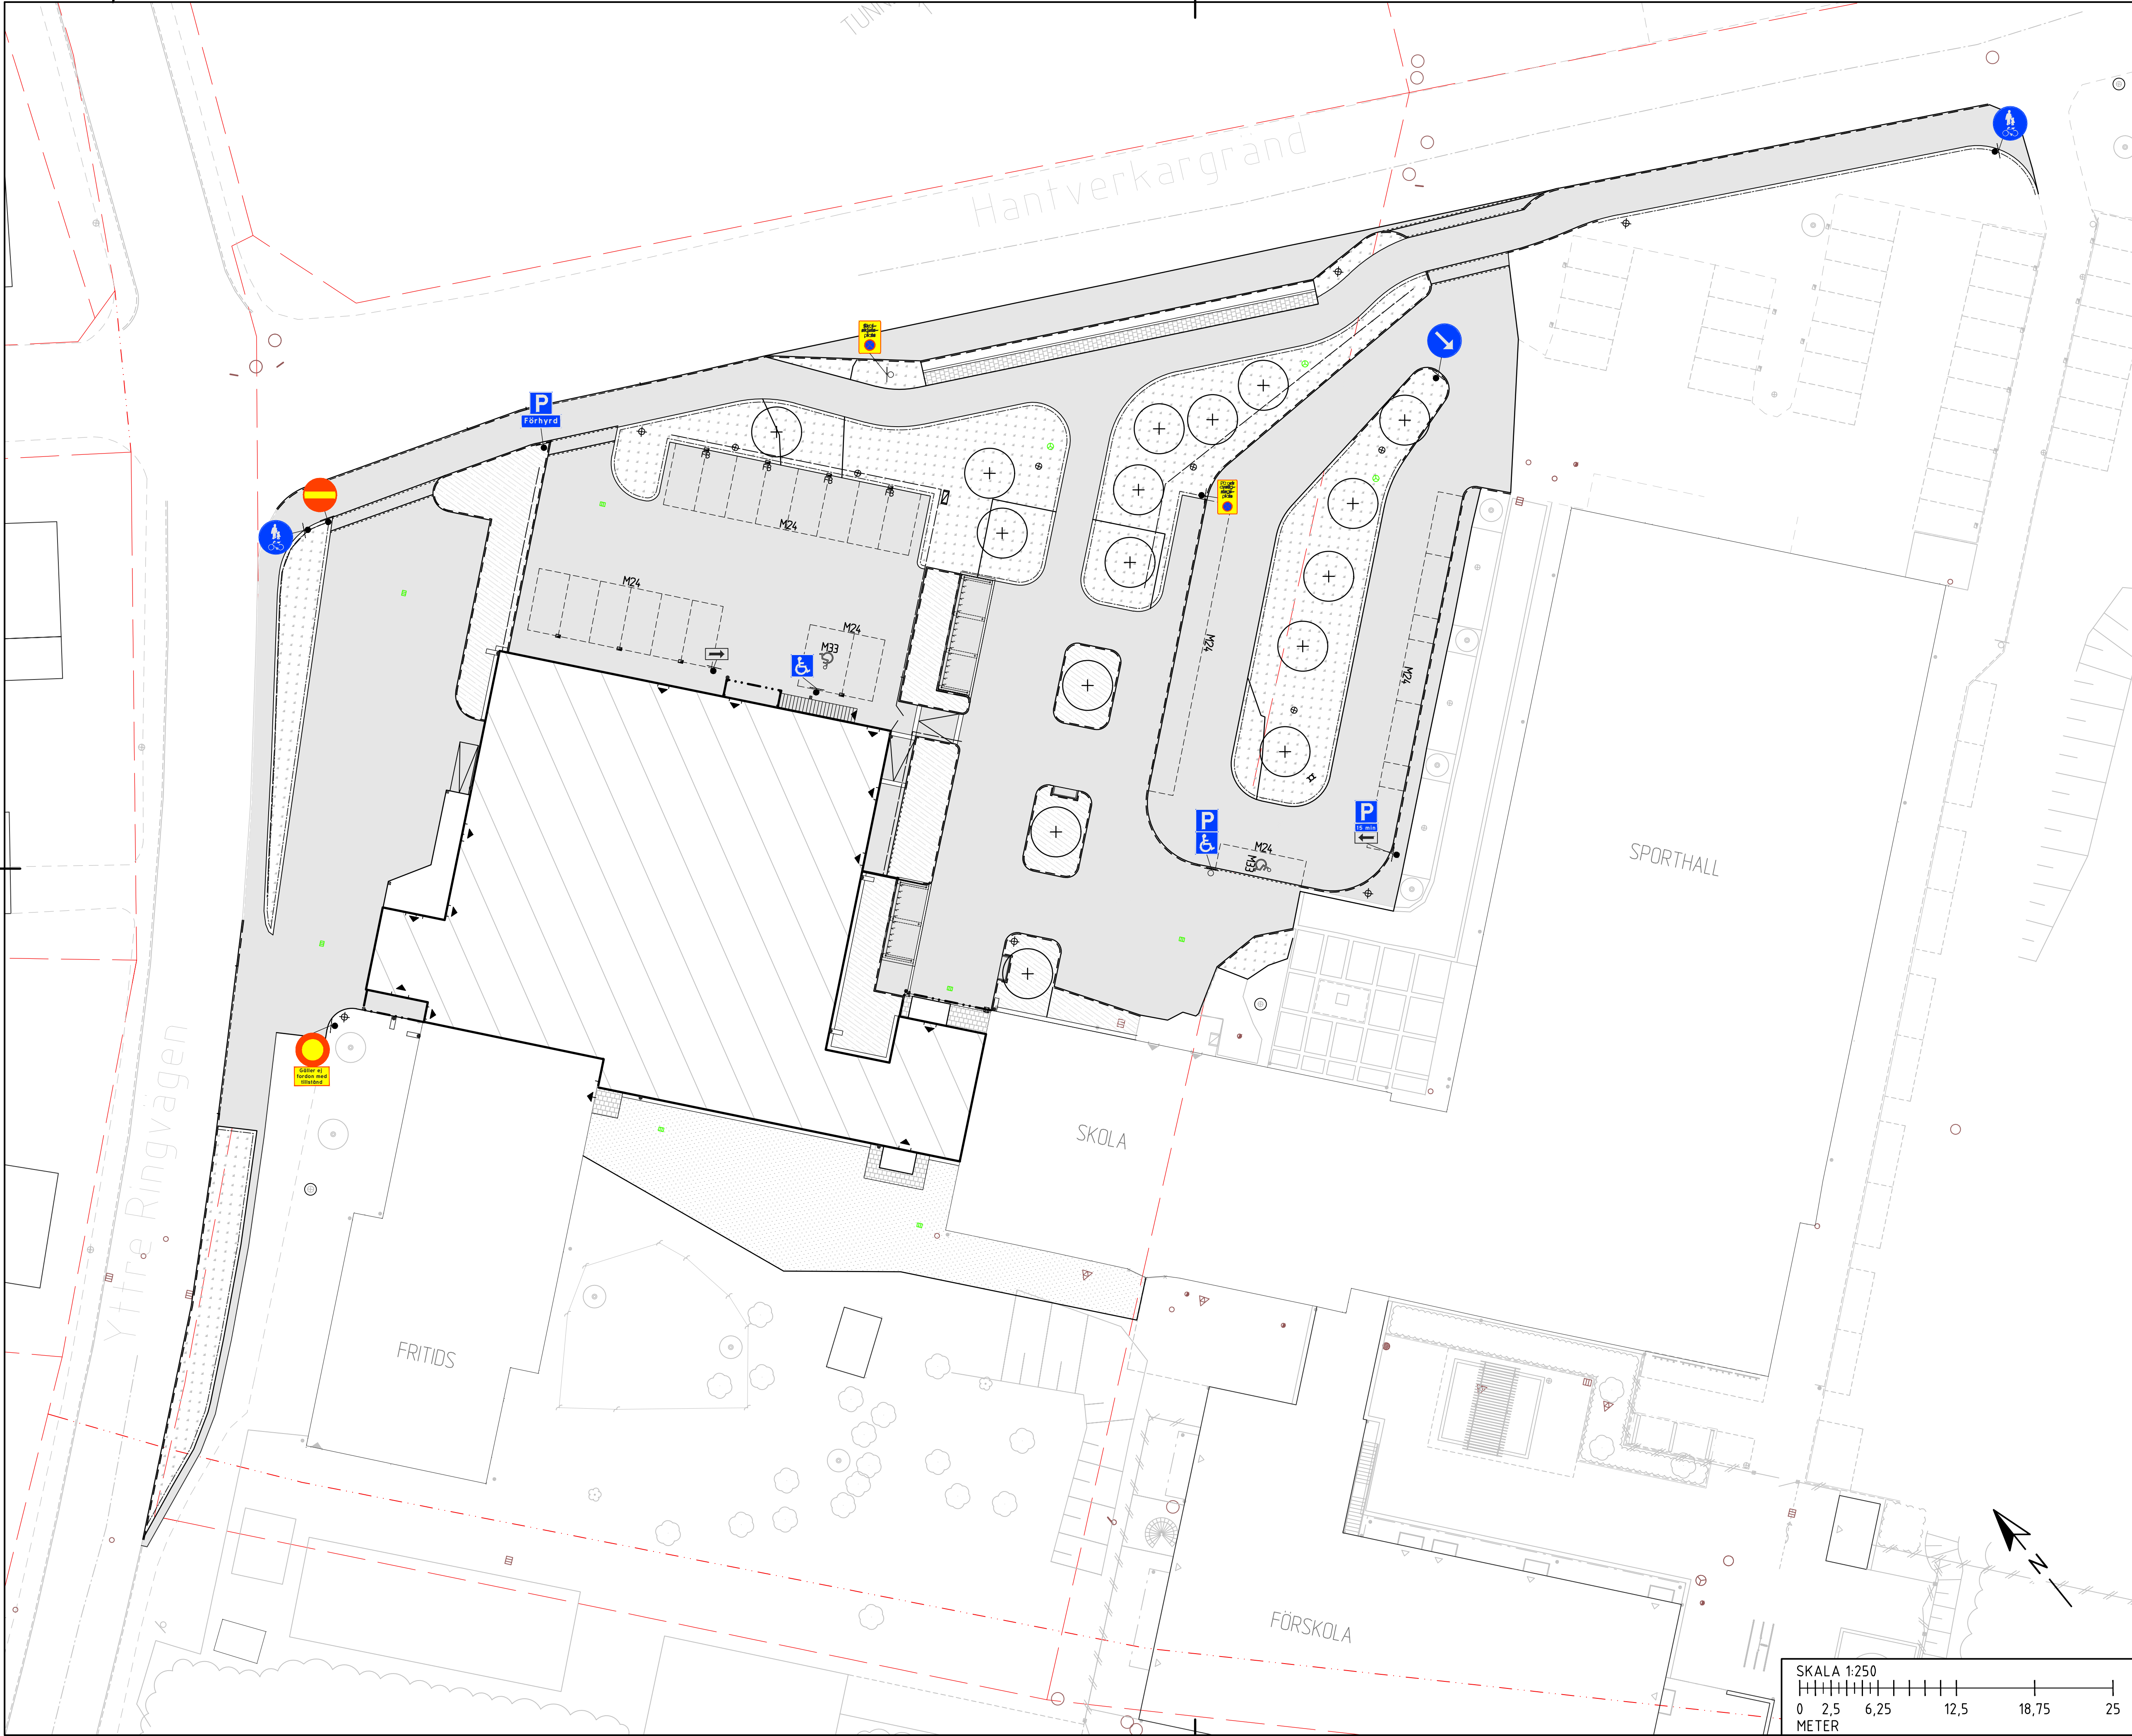

TECKENFÖRKLARING

FASTIGHETSGRÄNS

M24, UPPSTÄLLINGSYTA

SKYLTSTOLPE

BEF. SKYLTSTOLPE SOM FLYTTAS

E19, PARKERING

T7, RÖRELSEHINDRADE

Förhyrd

T22, TEXT "FÖRHYRD"

T11-H, UTSTRÄCKNING

T11-V, UTSTRÄCKNING

C1, FÖRBUD MOT INFART MED FORDON

C2, FÖRBUD MOT TRAFIK MED FORDON

D6, PÅBJUDEN GÅNG- OCH CYKELBANA

C40-6, ÄNDAMÅLSPLATS

15 min

T18, TILLÅTEN TID FÖR PARKERING

T22, TEXT

C40-3, ÄNDAMÅLSPLATS

D2-1, PÅBJUDEN KÖRBANA

M33, MÅLNING RÖRELSEHINDRAD

ANMÄRKNING

KOORDINATSYSTEM SWEREF99 2015

HÖJDSYSTEM RH2000

STATUS

FÖRFRÅGNINGSUNDERLAG

HANDLING

BYGGHANDLING

DATUM

2024-12-20

GODKÄND AV

ANDRINGS PM

BESTÄLLARE

ROBERTSFORS

KOMMUN

PROJEKTNAMN

CENTRALKÖK

OMRADE

ROBERTSFORS KOMMUN

PROJEKTNUMMER

YTTRE RINGVÄGEN 4

DIARIENUMMER

FORDONET 1

DISCIPLIN

FÖRETAG

OPPFÖRINGSNUMMER

NORCONSULT SVERIGE AB

TELEFON

108 83 71

BYGGNADSVÄRK

AVH

VÄNINGSPLAN

KONTAKTPERSON

VÄNINGSDEL

010 141 80 00

DELOMRADE

TOMAS BERGSTRÖM

SYSTEM

(HÖJDSHÖJD RH 2000)

REGISTRATÖR

+44.60, +45.07, +45.54 (FG)

SKYLTNING

SKALA

PLAN

1:250

DOKUMENTNUMMER

FORMAT

M-32-1-002

A1

SKALA 1:250

0 2,5 6,25 12,5 18,75 25

METER