


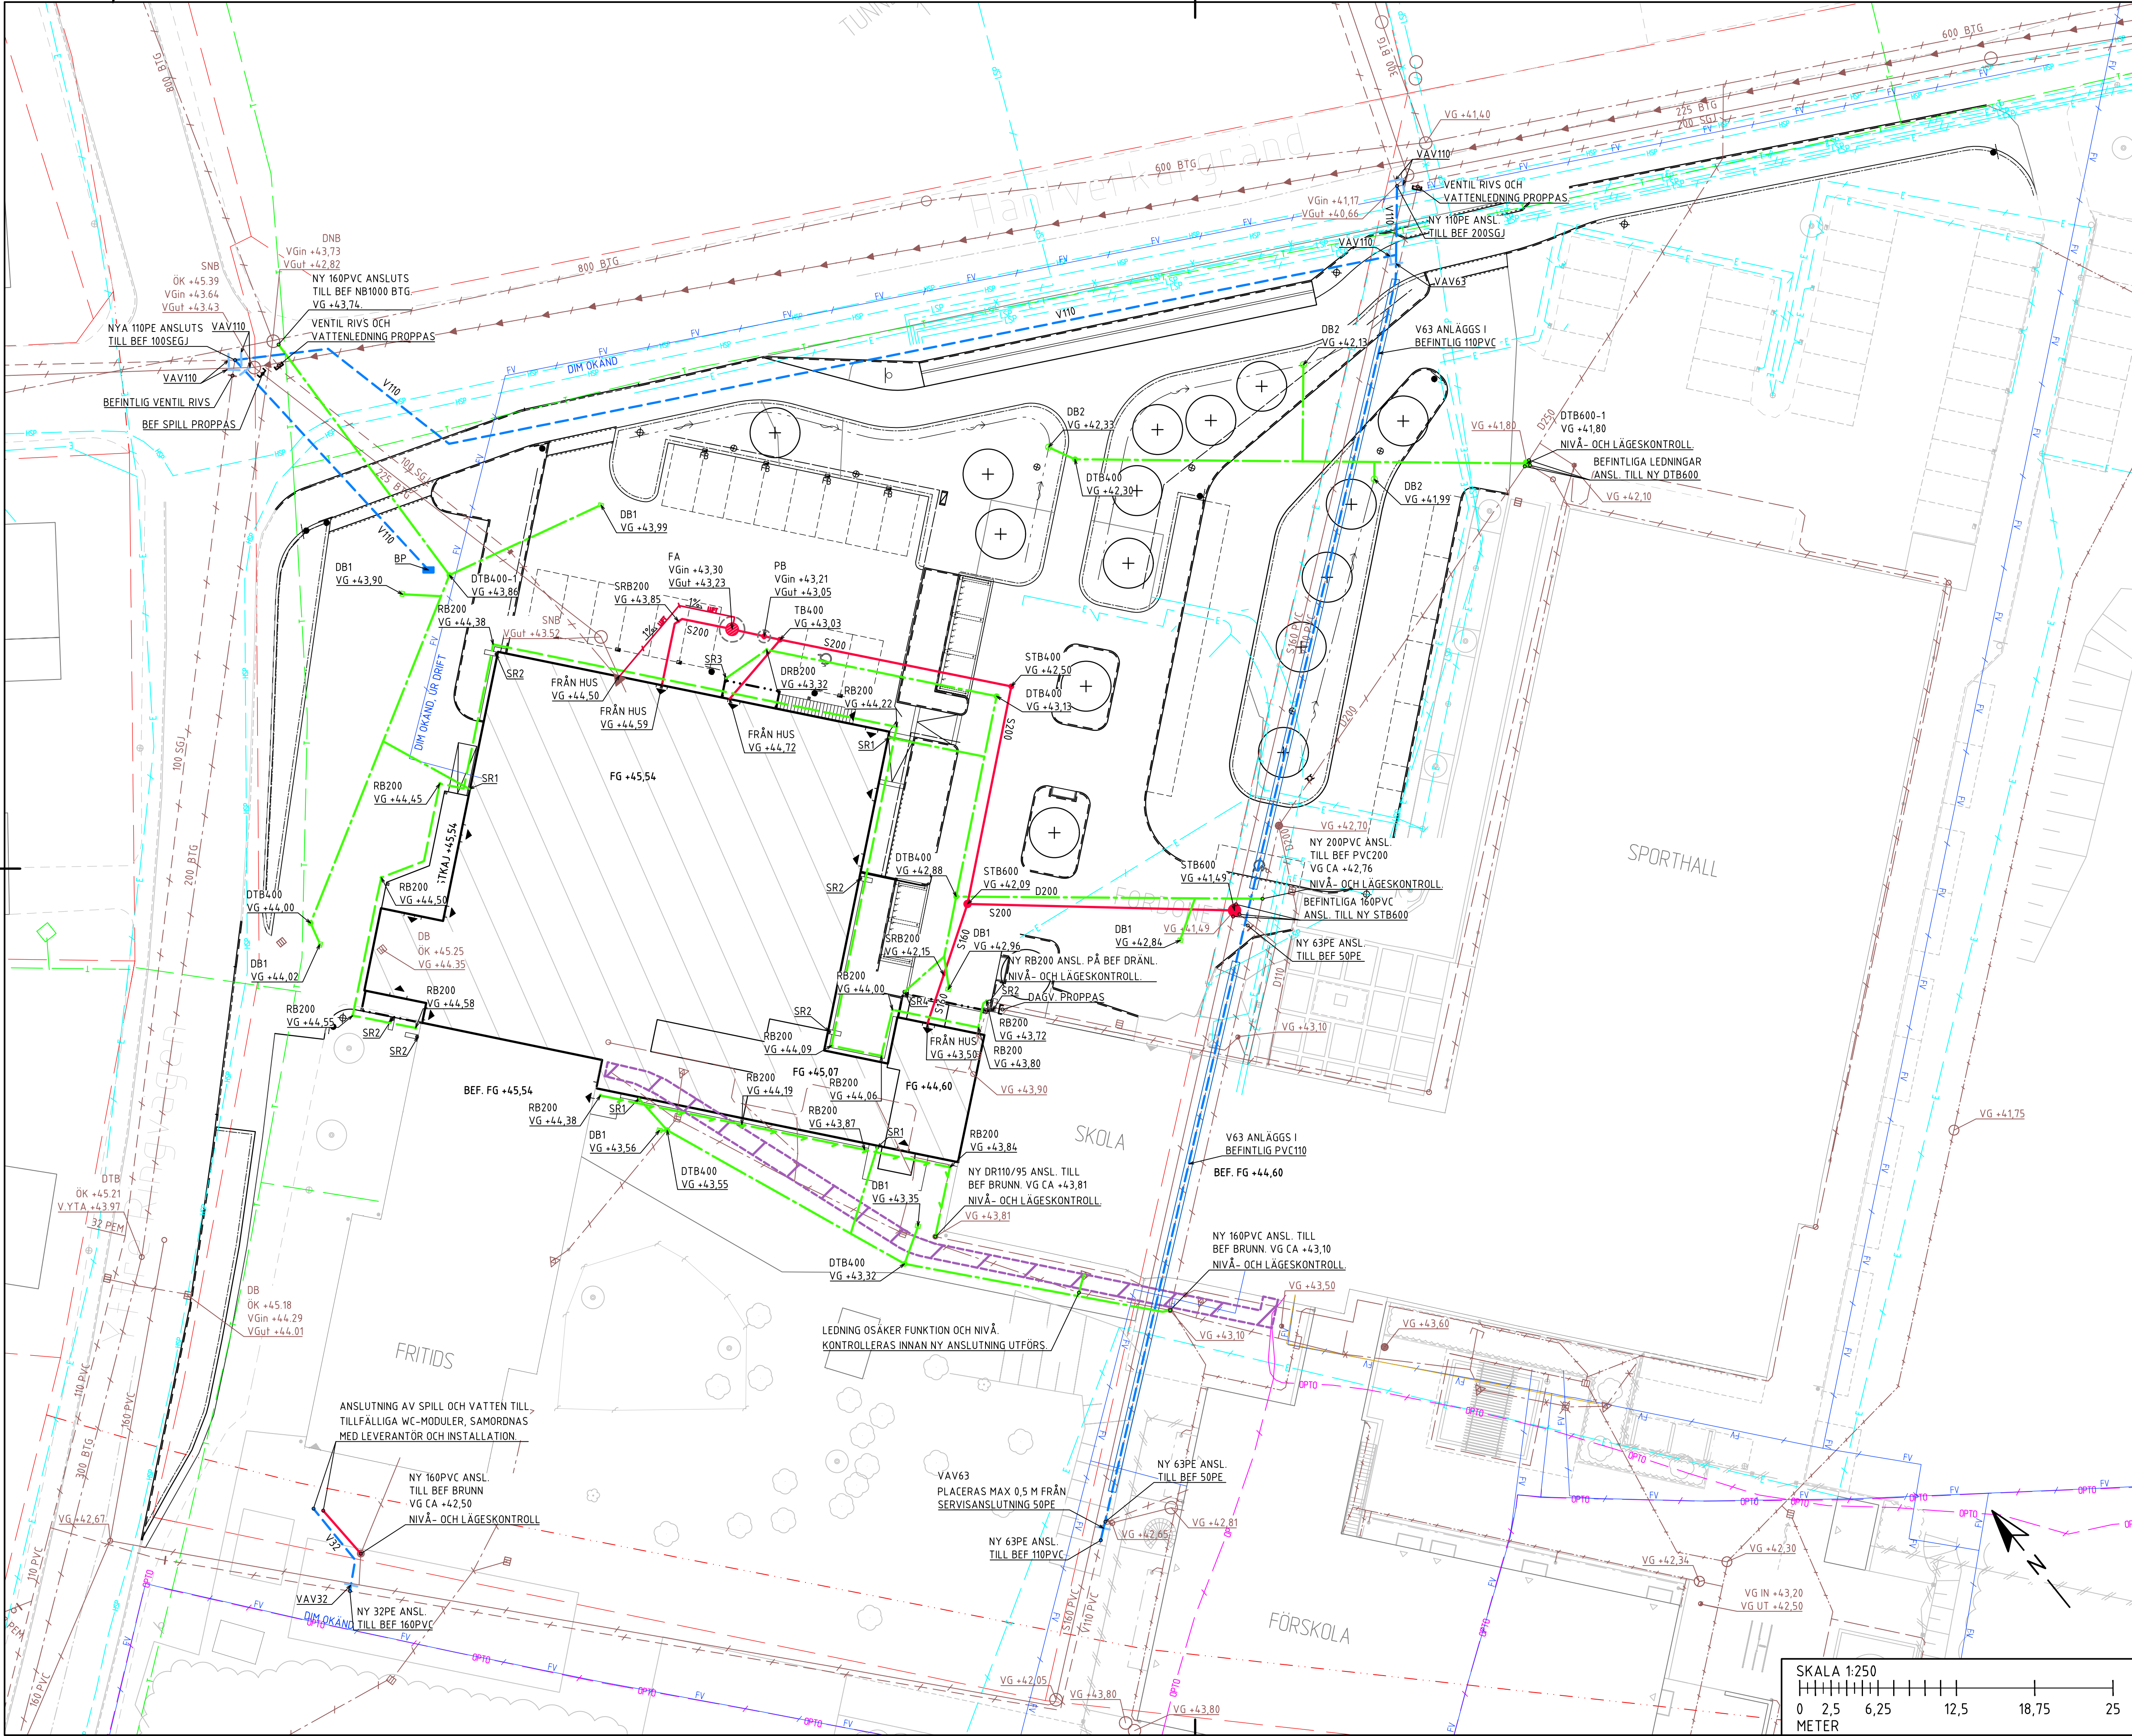

TECKENFÖRKLARING

FASTIGHETSGRÄNS

BEFINTLIG OPTOLEDNING

BEFINTLIG TELEDNING

BEFINTLIG ELLEDNING

LÄGSPÄNNINGSLEDNING

HÖGSPÄNNINGSLEDNING

ELLEDNING UR BRUK

FV

BEFINTLIG FJÄRRVÄRMELEDNING

BEFINTLIG VATTENLEDNING MED VENTIL

BEFINTLIG DAGVATTENLEDNING OCH BRUNN

BEFINTLIG SPILLVATTENLEDNING OCH BRUNN

BEFINTLIG SPILLVATTENLEDNING TRYCKSAT

BEFINTLIG DRÄNERING OCH BRUNN

BEFINTLIG DAGVATTENLEDNING UR BRUK

BEF. KUPOL-/GALLERBRUNN

BEF. OKÄND ANSLUTNING/BRUNN

AVLUFTNINGSLEDNING DIM 160

SPILLVATTENLEDNING, DIM 200

DÄR EJ ANNAT ANGES

VATTENLEDNING

VATTENLEDNING, V63 I BEF 110PVC

DAGVATTENLEDNING, DIM 160 DÄR EJ ANNAT ANGES

DRÄNLEDNING 110/95

ISOLERING

KULVERT. LEDNINGAR SOM KULVERTERAS ENL. RITNING V-50-6-002

BP, BRANDPOST

VAV, VENTIL

PROPPNING

SRB200, RENSBRUNN

STB400, TILLSYNSBRUNN

STB600, TILLSYNSBRUNN

FA, FETTAVSKILJARE

PB, PROVTAAGNSBRUNN

RB200, RENSBRUNN PÅ DRÄNERING

DRB200, RENSBRUNN PÅ DAGV.

DTB400, TILLSYNSBRUNN

DTB400-1, TILLSYNSBRUNN MED SANDFÄNG

DTB600, TILLSYNSBRUNN

DTB600-1, TILLSYNSBRUNN MED SANDFÄNG

DB1, DAGVATTENBRUNN

DB2, KUPOLBRUNN

SR1, SR3, SR4 STUPRÖR MARKANSLUTET

SR2, STUPRÖR MED UTKASTARE

DÄR NYA LEDNINGAR OCH BRUNNAR ANSLUTS TILL BEF. LEDNINGSSYSTEM SKA SAMTLIGA ANSLUTNINGSPUNKTER KONTROLLERAS I NIVÅ OCH PLAN.
KULVERT SKA ANLÄGGAS ENL. RÖR-LEVERANTÖRENS ANVISNING. KULVERT UNDER KANTBALK ANLÄGGES MED TÄCKNINGEN CA 1,4 M. FÖR ÖVRIG DRAGNING SKA KULVERT ANLÄGGAS MED MINST 0,8 M TÄCKNING.

ANMÄRKNING
KOORDINATSYSTEM SWEREF99
2015 HÖJDSYSTEM RH2000

STATUS

FÖRFRÅGNINGSUNDERLAG

HANDLING

BYGGHANDLING

DATUM

2024-12-20

ODOKAND AV

ANDRINGS PM

BESTÄLLARE

ROBERTSFORS
KOMMUN

PROJEKTNAMN

CENTRALEKÖK

OMRÅDE

ROBERTSFORS KOMMUN

PROJEKTNUMMER

YTTRE RINGVÄGEN 4

DIARIENUMMER

FORDONET 1

DISCIPLIN

M

DISCIPLIN

NORCONSULT SVERIGE AB

OPPRORGSNUMMER

108 83 71

SKAPAD AV

MAA

TILLFÖR

010 141 80 00

BYGGNADSVÄRDE

FLUKHÖJD (RH 2000)

ANVÄNDRING

30 SAMMANSATT REDOVISNING MARK

ANVÄNDRING

PLAN

ANVÄNDRING

R-51-1-101

ANVÄNDRING

SKALA 1:250

0

2,5

6,25

12,5

18,75

25

METER