




DETALJ ANSLUTNING, SR1,
MARKANSLUTNA STUPRÖR MOT DIM 100

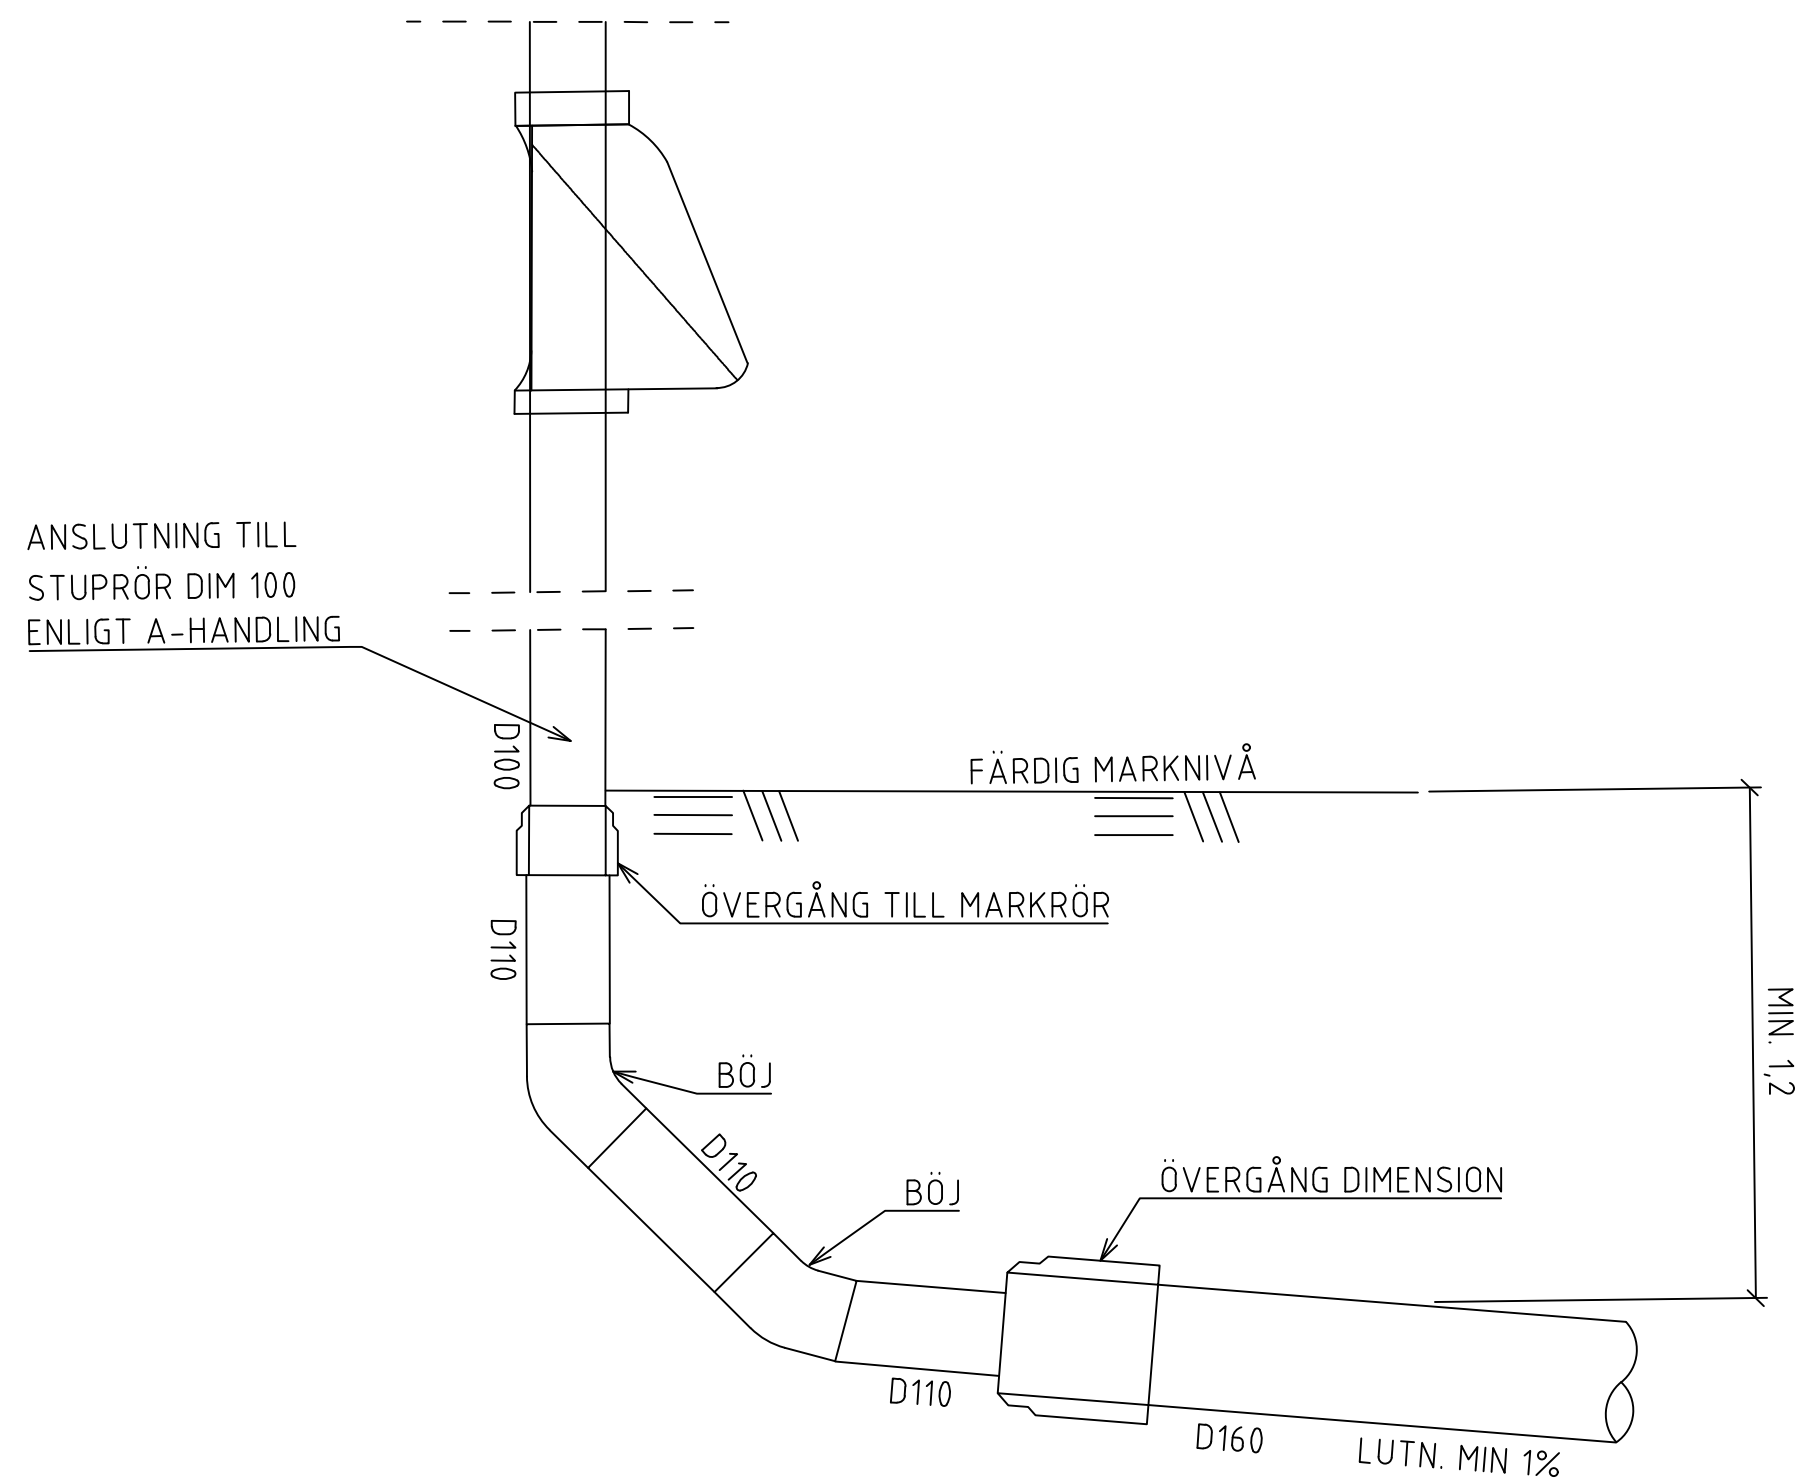

DETALJ ANSLUTNING, SR3,
MARKANSLUTNA STUPRÖR MOT DIM 100

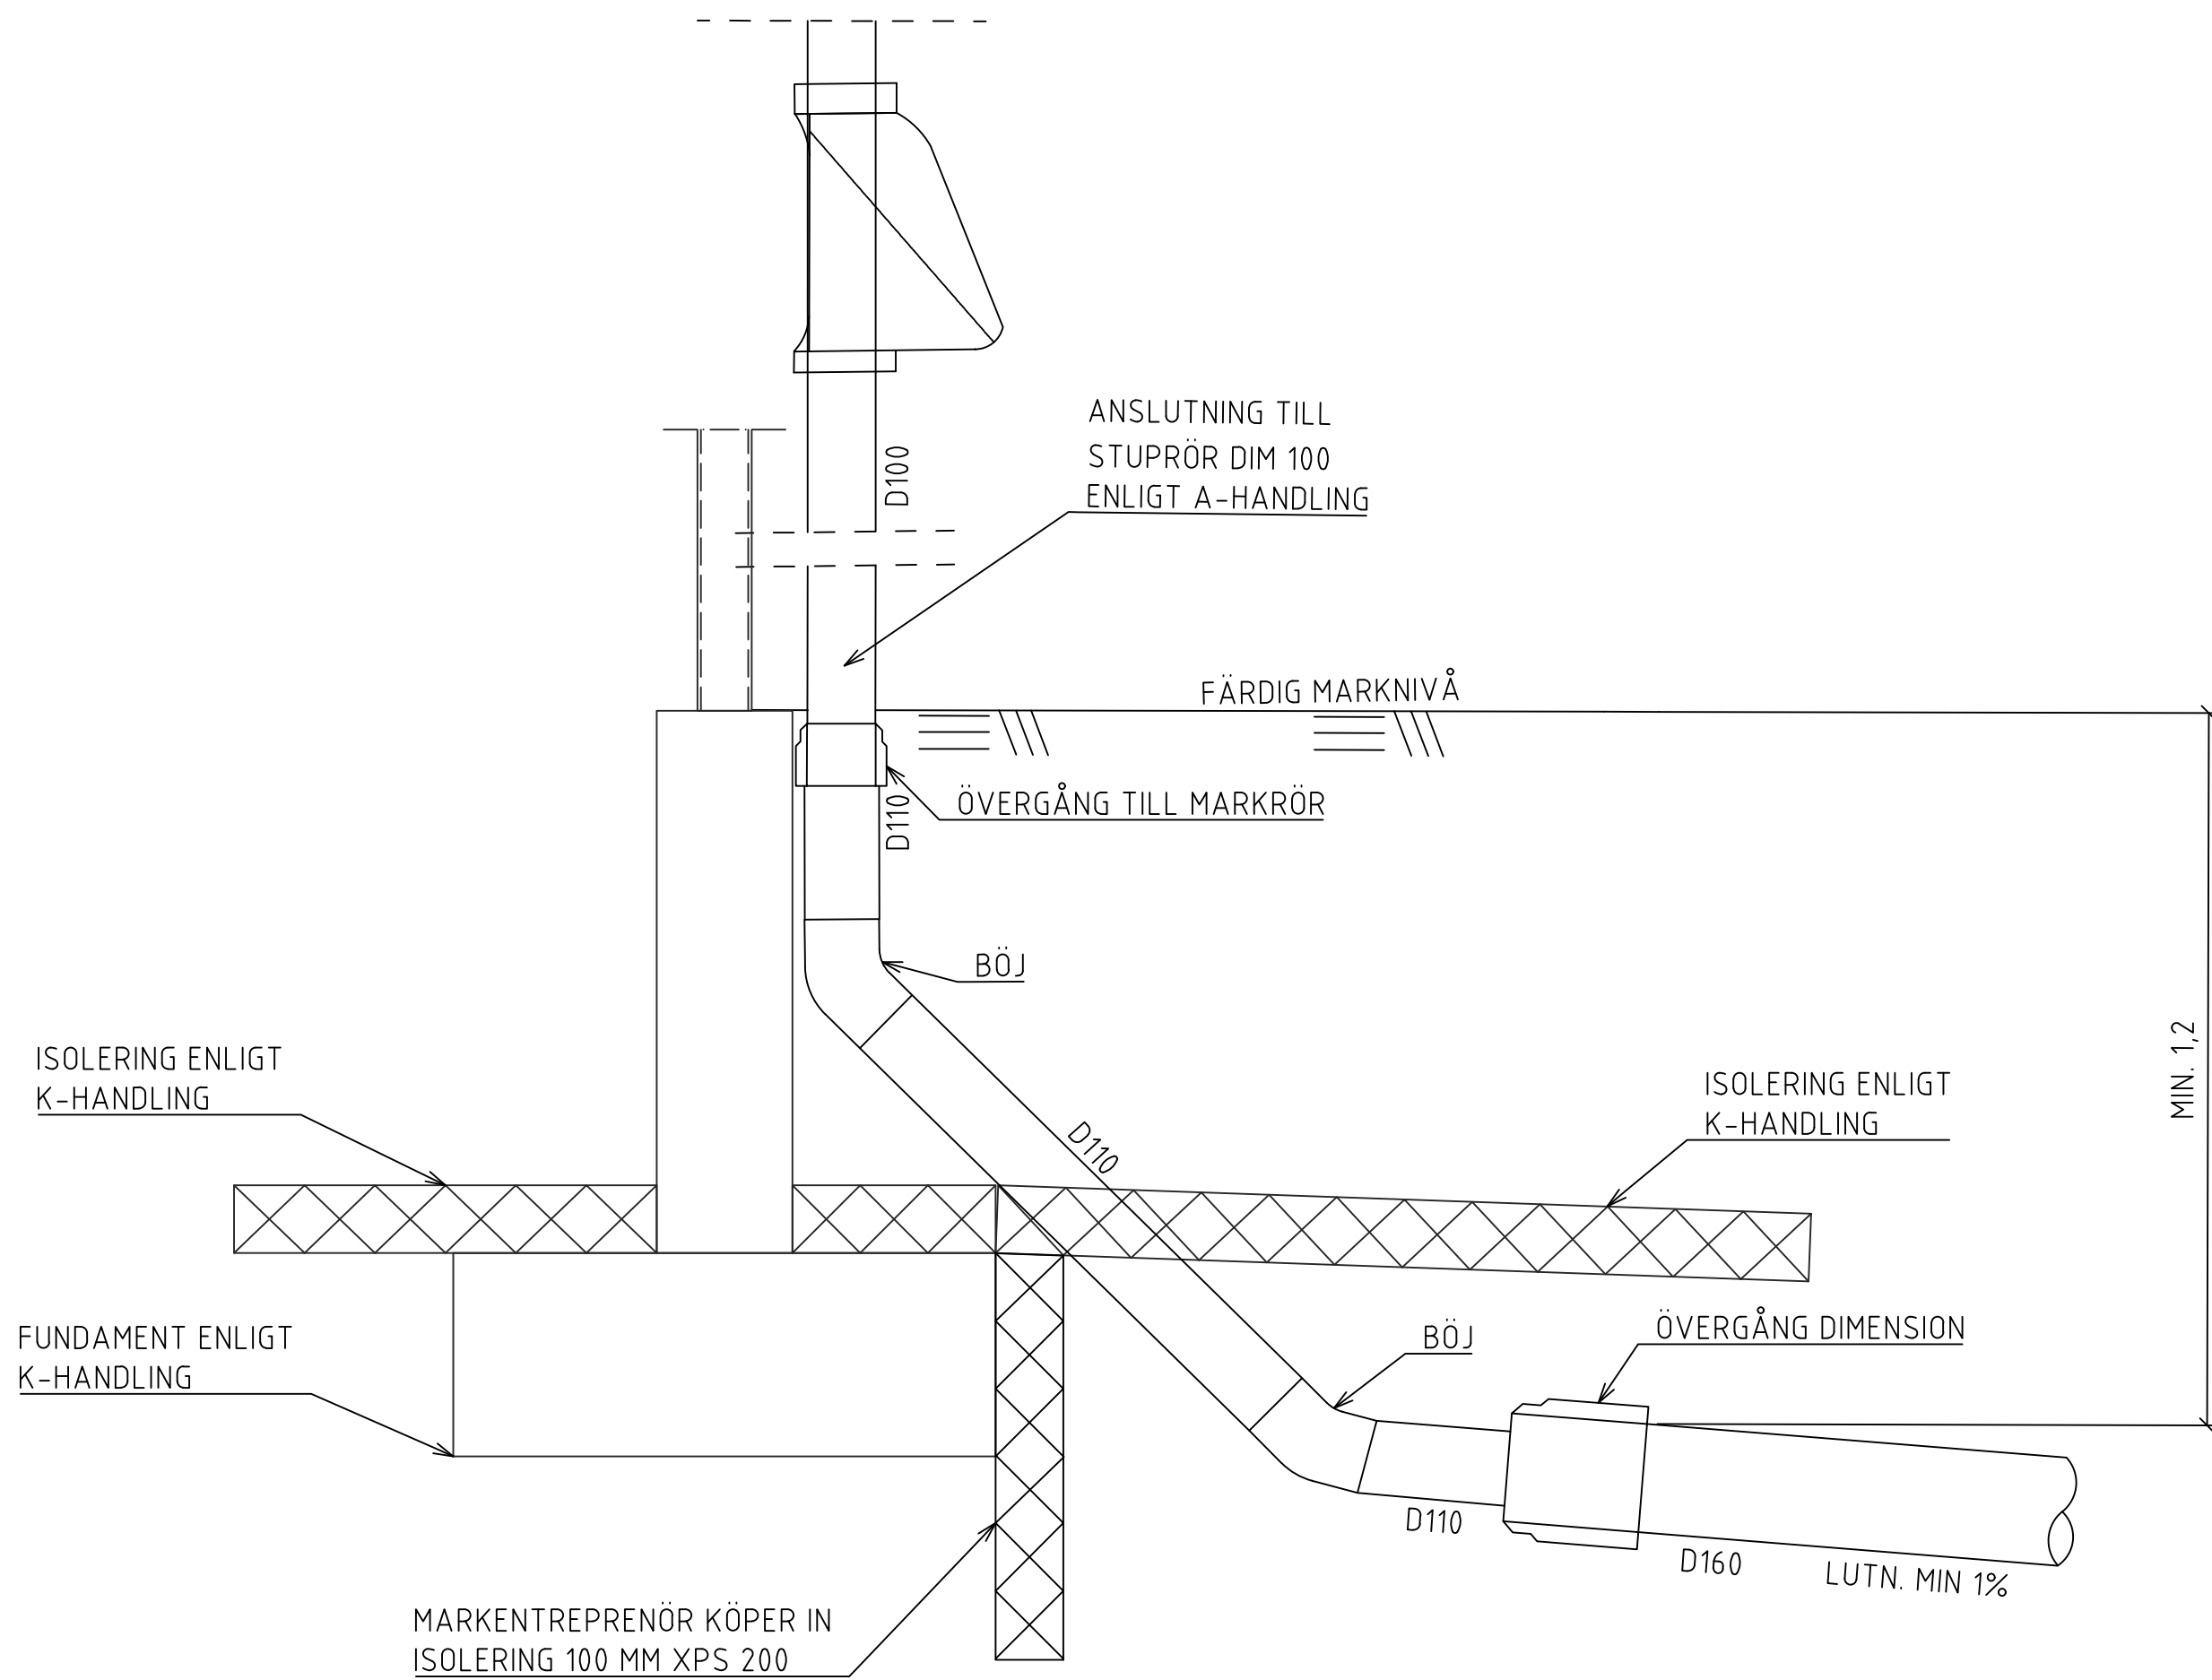

DETALJ ANSLUTNING, SR4,
MARKANSLUTNA STUPRÖR MOT DIM 100

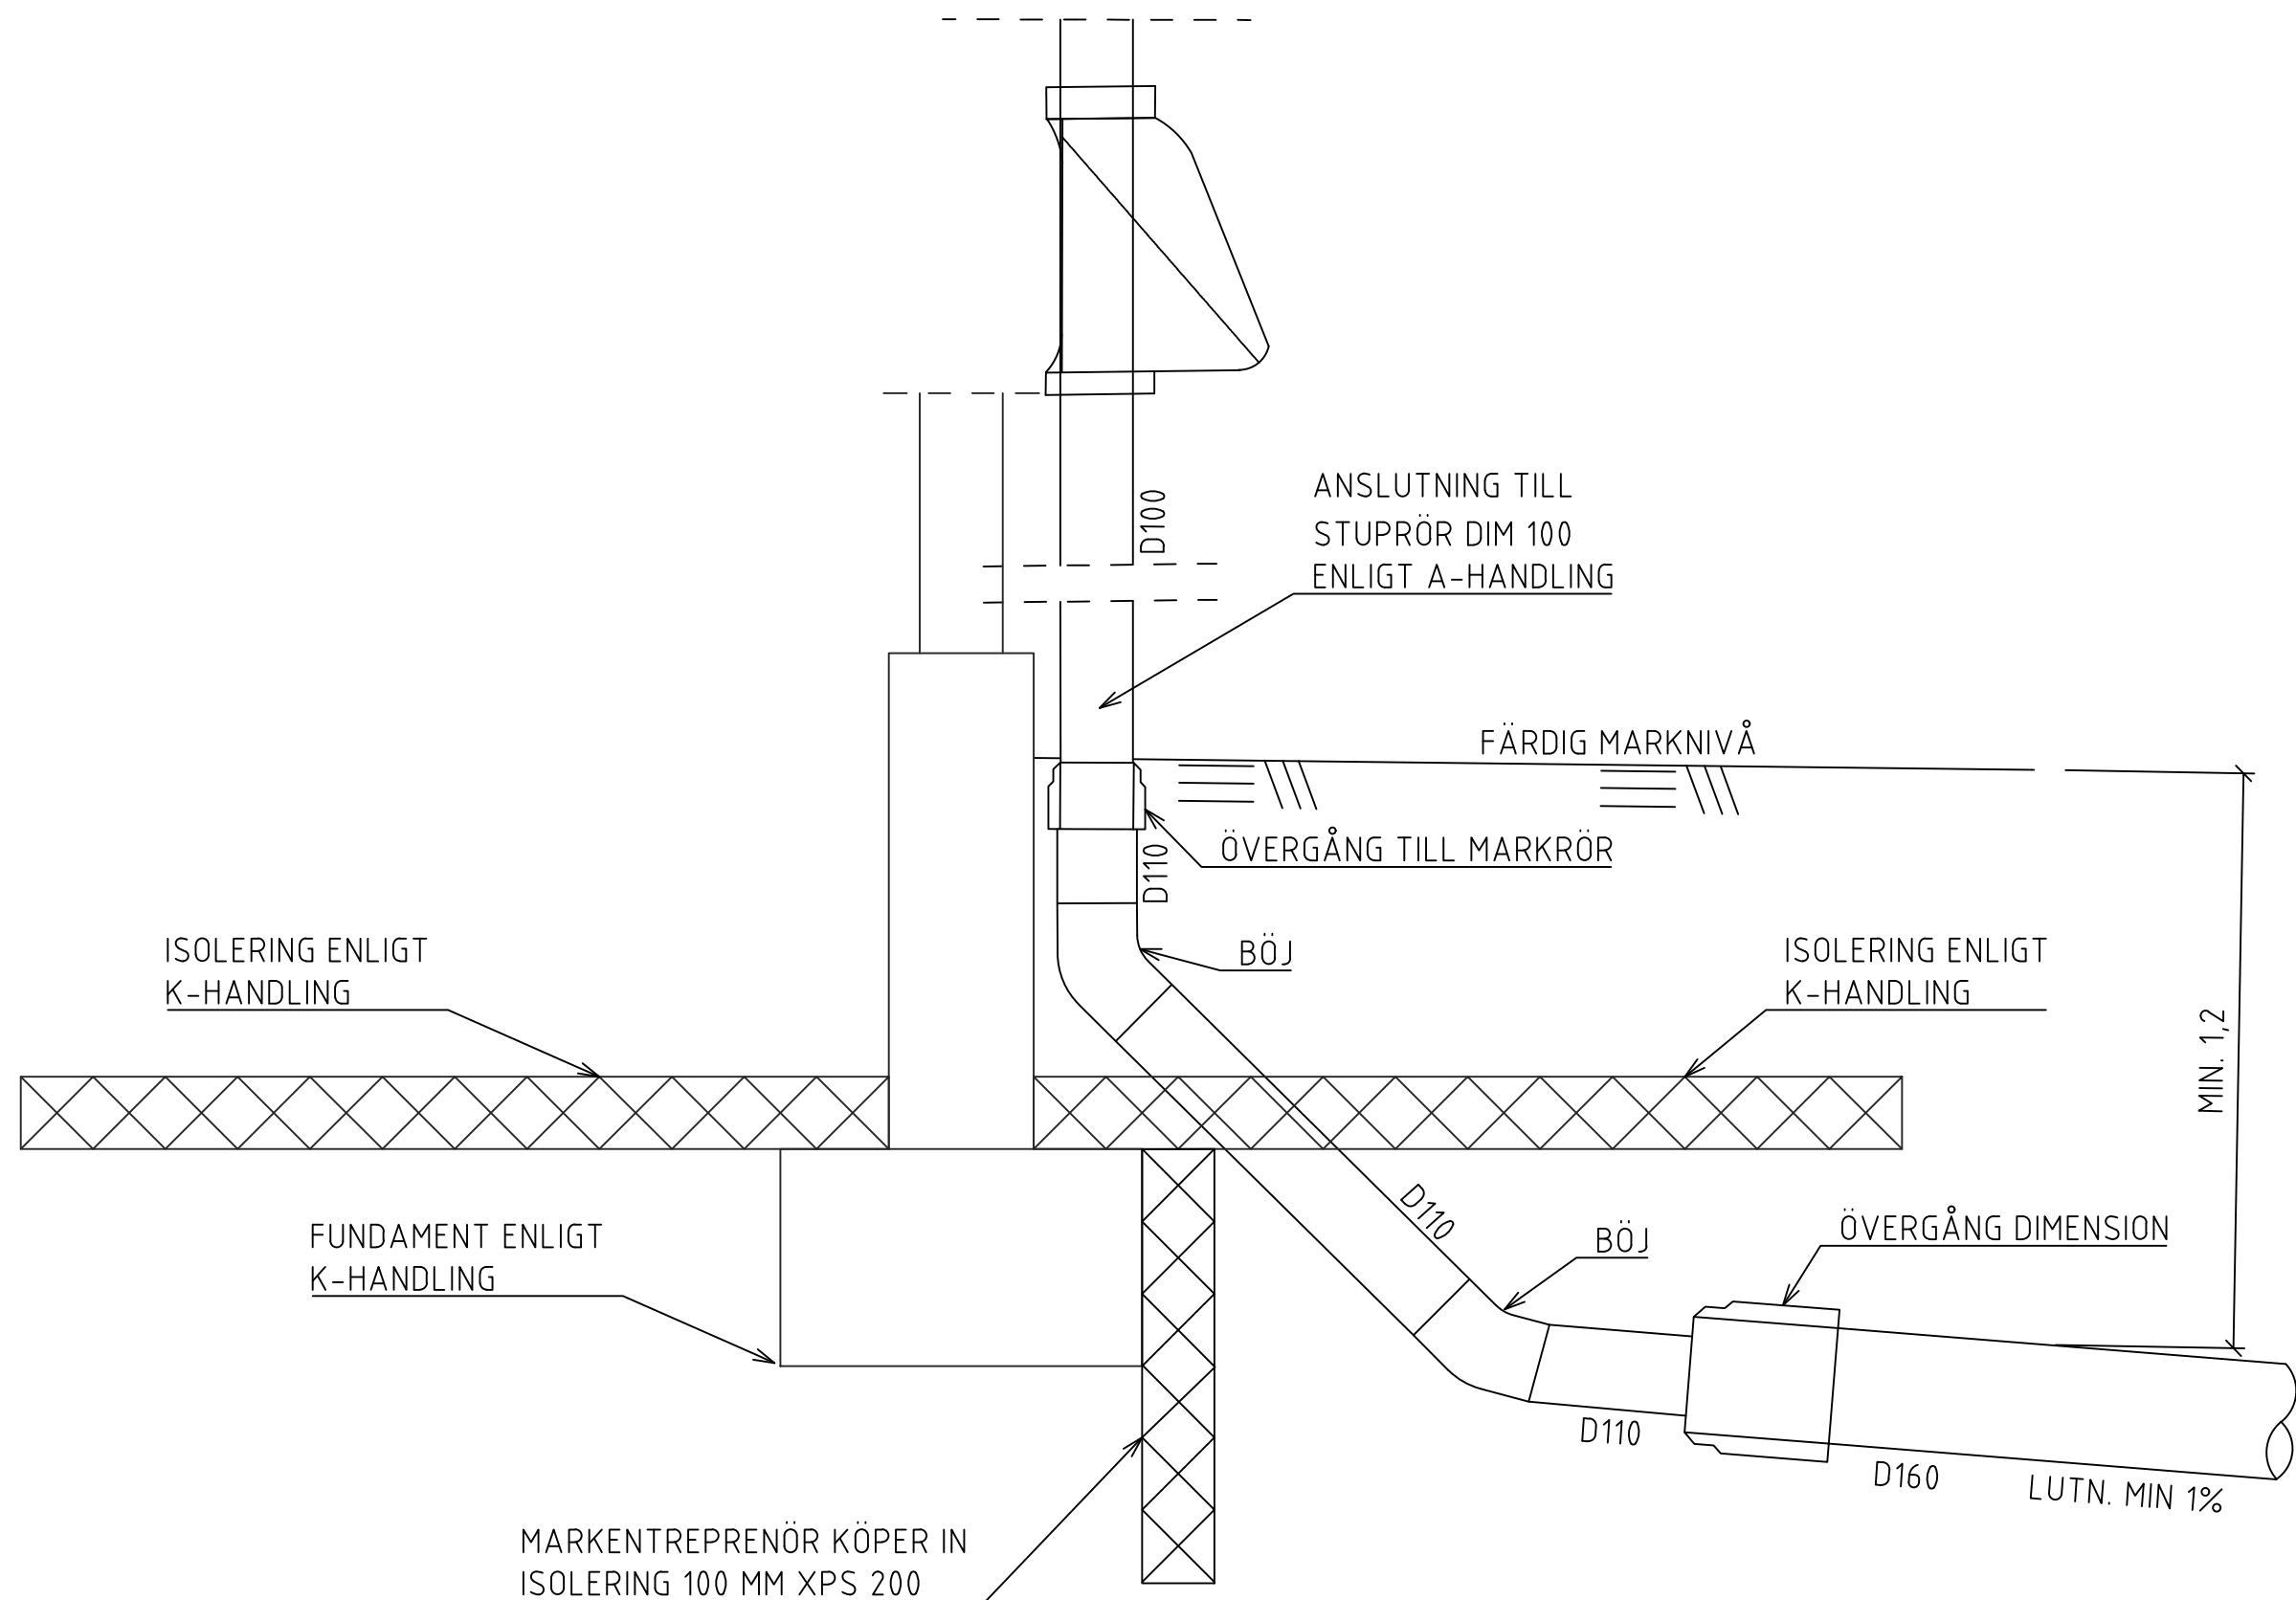

STATUS				
FÖRFRÅGNINGSUNDERLAG				
HANDLING				
BYGGHANDLING				
DATUM	2024-12-20		ODKÄND AV	ANDRINGS PM
BESTÄLLARE				
		ROBERTSFORS KOMMUN		
PROJEKTNAMN				
CENTRALKÖK				
OMRÅDE				
ROBERTSFORS KOMMUN				
PROJEKTNUMMER	ADRESS			
	YTTRE RINGVÄGEN 4			
DIARIENUMMER	FASTIGHET			
	FORDONET 1			
DISCIPLIN	FÖRETAG			
M	NORCONSULT SVERIGE AB			
UPPDRAGSNUMMER	SKAPAD AV			
108 83 71	AVH			
TELEFON	KONTAKTPERSON			
010 141 80 00	TOMAS BERGSTRÖM			
BYGGNADSVÄRKE	(FLISBJÖRD (RM 2008))			
VÄNINGSPLAN	VÄNINGSDEL	DELOMRADE		
SYSTEM				
30 SAMMANSATT REDOVISNING MARK				
ANSLUTNING STUPRÖR				
RITNINGSKATEGORI	SKALA	FORMAT		
DETALJ	1:10	A1		
DOKUMENTNUMMER				ANDRING
R-51-6-001				

