


2024-12-18 16:07:39

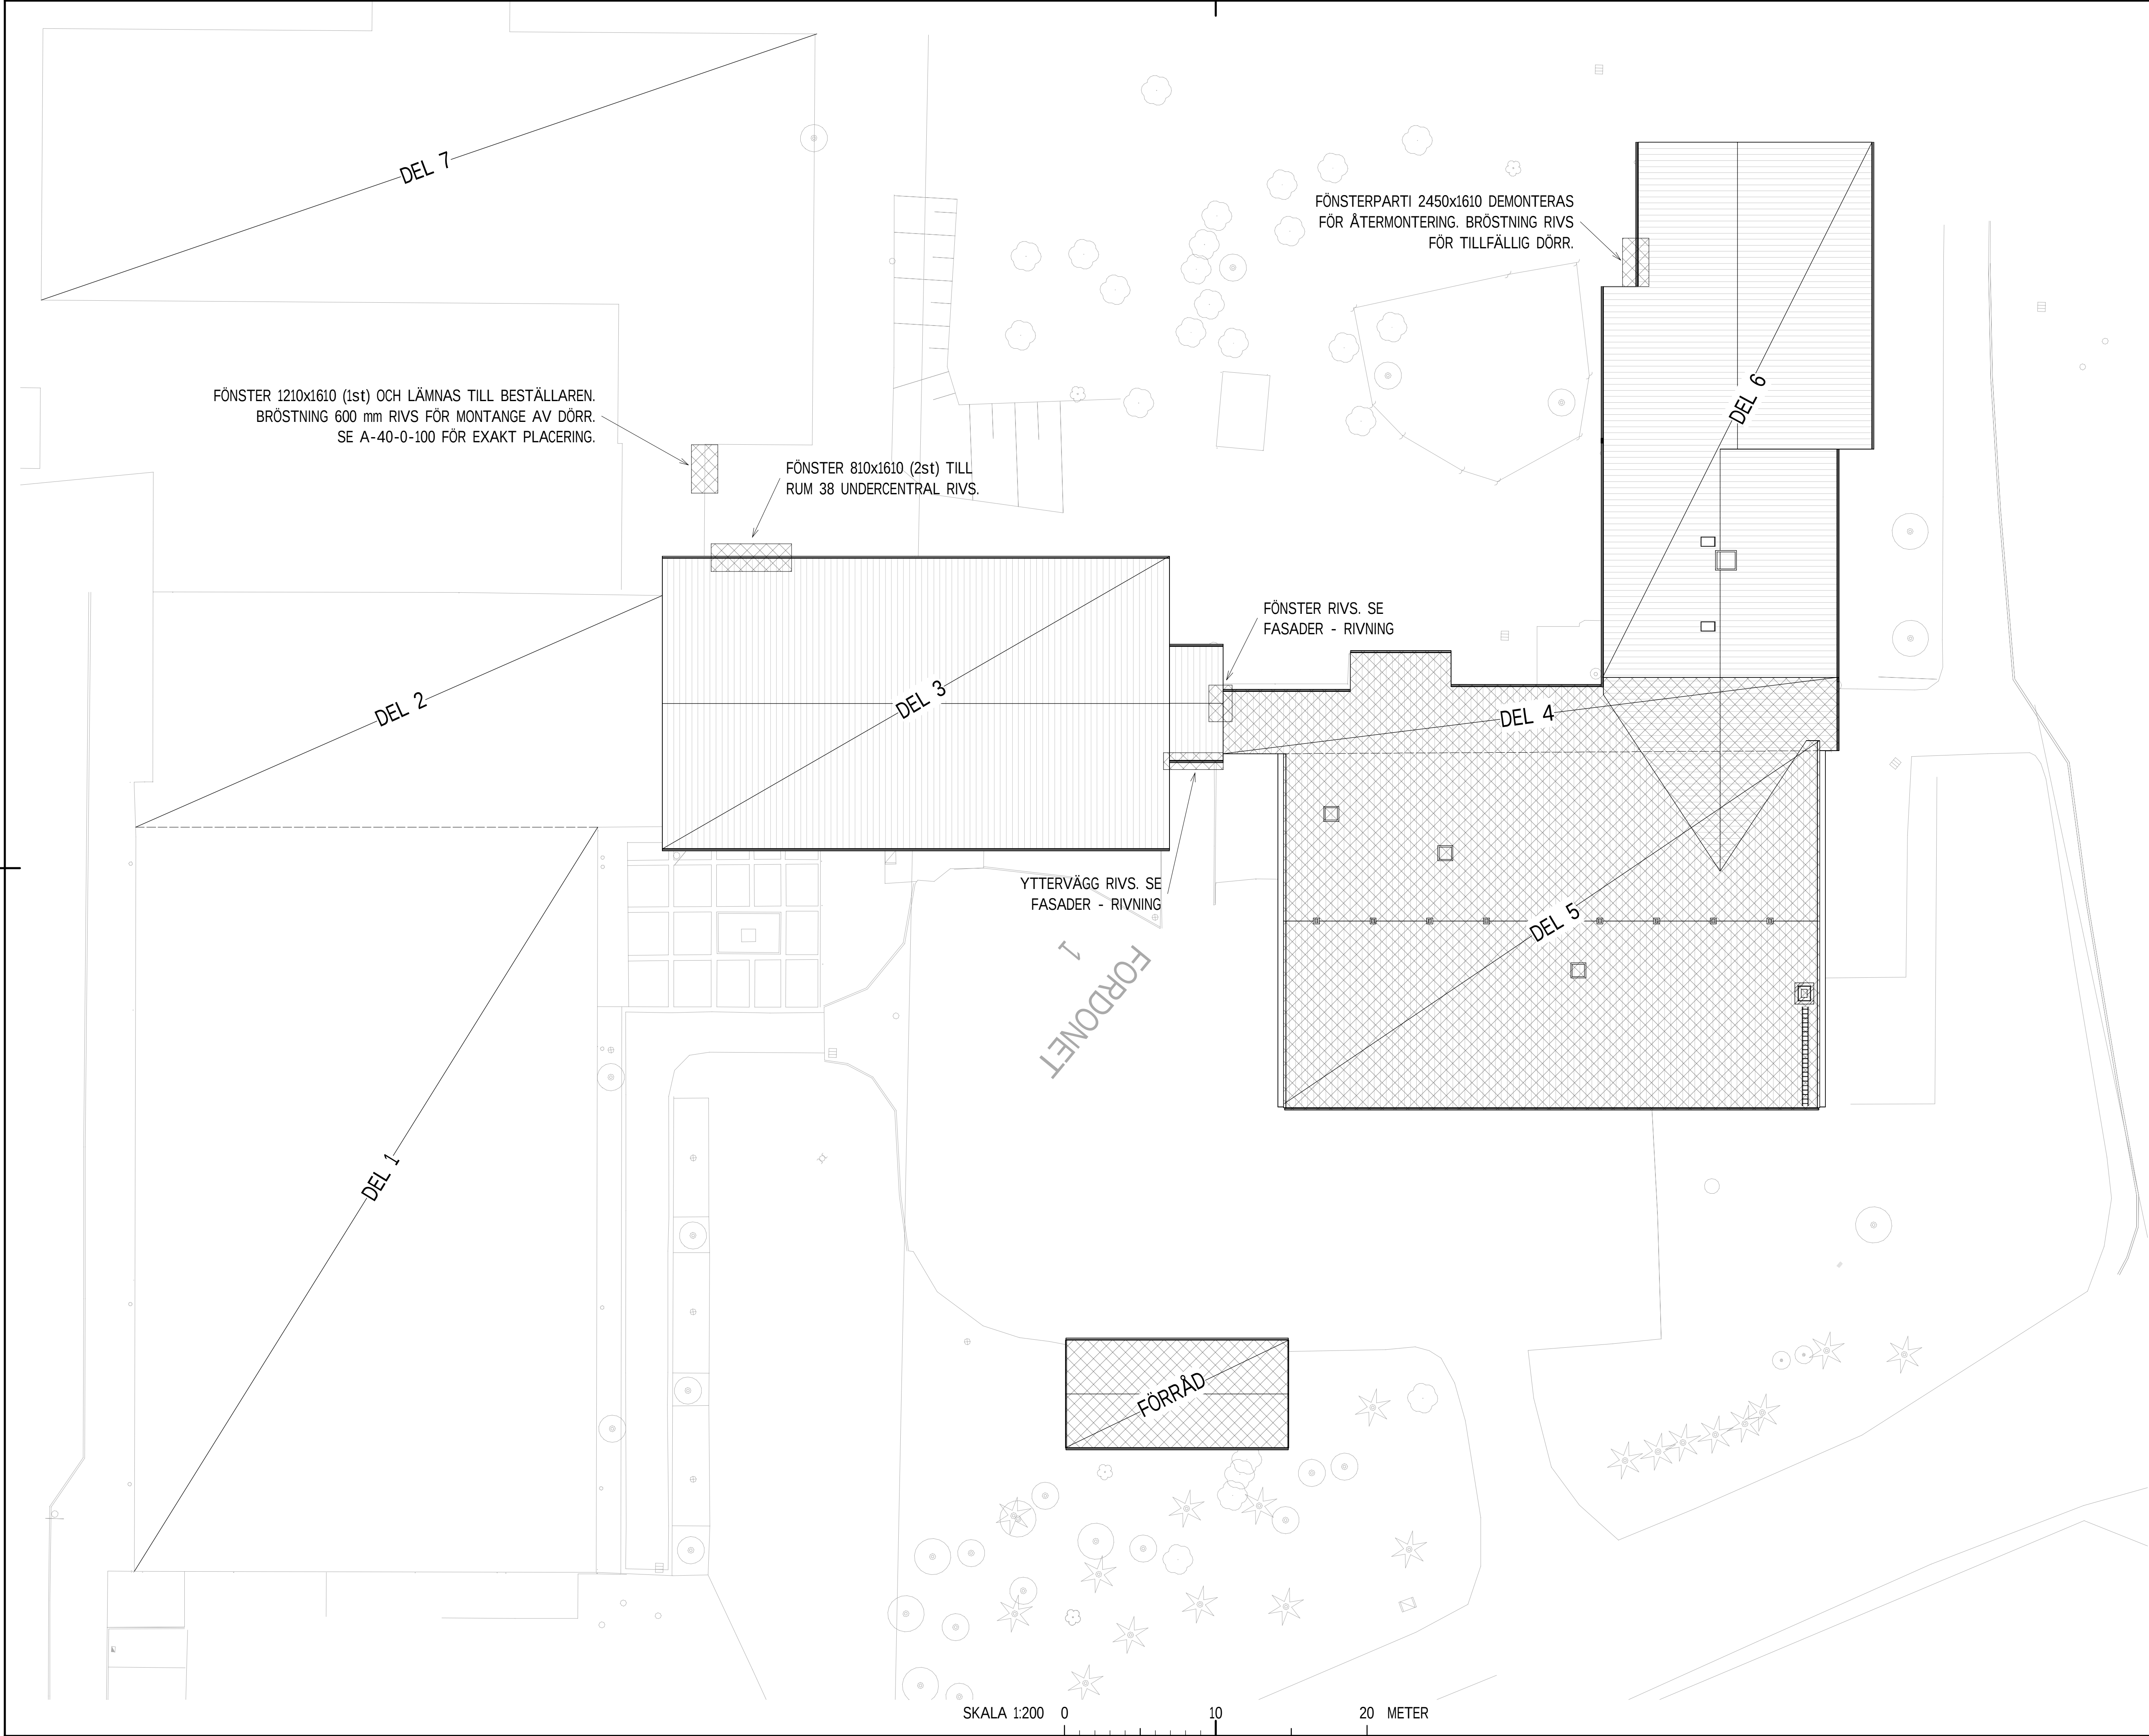

FÖRKLARINGAR

[Cross-hatched box] = BYGGNAD SOM RIVS

HÄNVISNINGAR

PLAN - RIVNING A-40-1-100-R
FASADER - RIVNING A-40-3-001-R
TAKPLAN - RIVNING A-41-1-001-R
FÖRRÅD - RIVNING A-45-4-100-R

STATUS		
FÖRFRÅGNINGSUNDERLAG		
HANDLING		
BYGGHANDLING		
DATUM	2024-12-20	ANSÖKAN AV
BESTÄLLARE	T. BERGSTRÖM	ADRESS PM
 ROBERTSFORS KOMMUN		
PROJEKTNAMN		
CENTRALEKÖ		
OMRÅDE		
ROBERTSFORS KOMMUN		
PROJEKTNUMMER	1088371	ADRESS
DIARIENUMMER	1088371	FASTIGHET
DISCIPLIN	A	FÖRETAG
UPPDRAGSNUMMER	1088371	NORCONSULT SVERIGE AB
TELEFON	010 141 80 00	MSR
BYGGNADSTYP	FÖRFRÅGNINGSUNDERLAG	KONTAKTPERSON
VÄRNINGSPÅN	VÄRNINGSDOM	FLUGHOLM (1972-2008)
SYSTEM		
01 SAMMANSATT REDOVISNING		
SITUATIONSPLAN		
RIVNING	1:200	FORMAT
A-01-1-100-R		A1

FILENAMN: N:\1088371\01 Arbetsmaterial\02 BIM\A3D_Model\Revningmodell-2024.rvt