
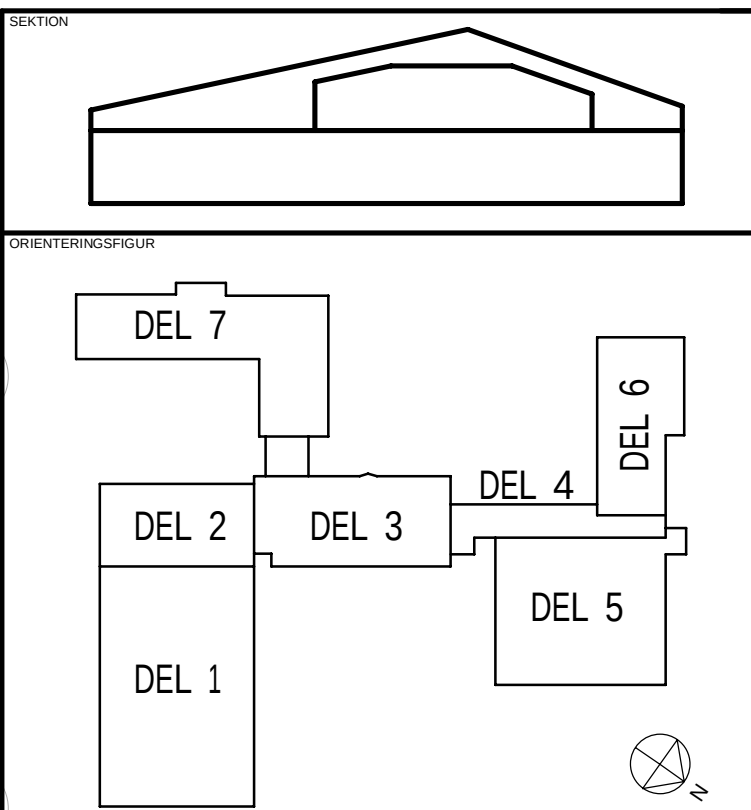


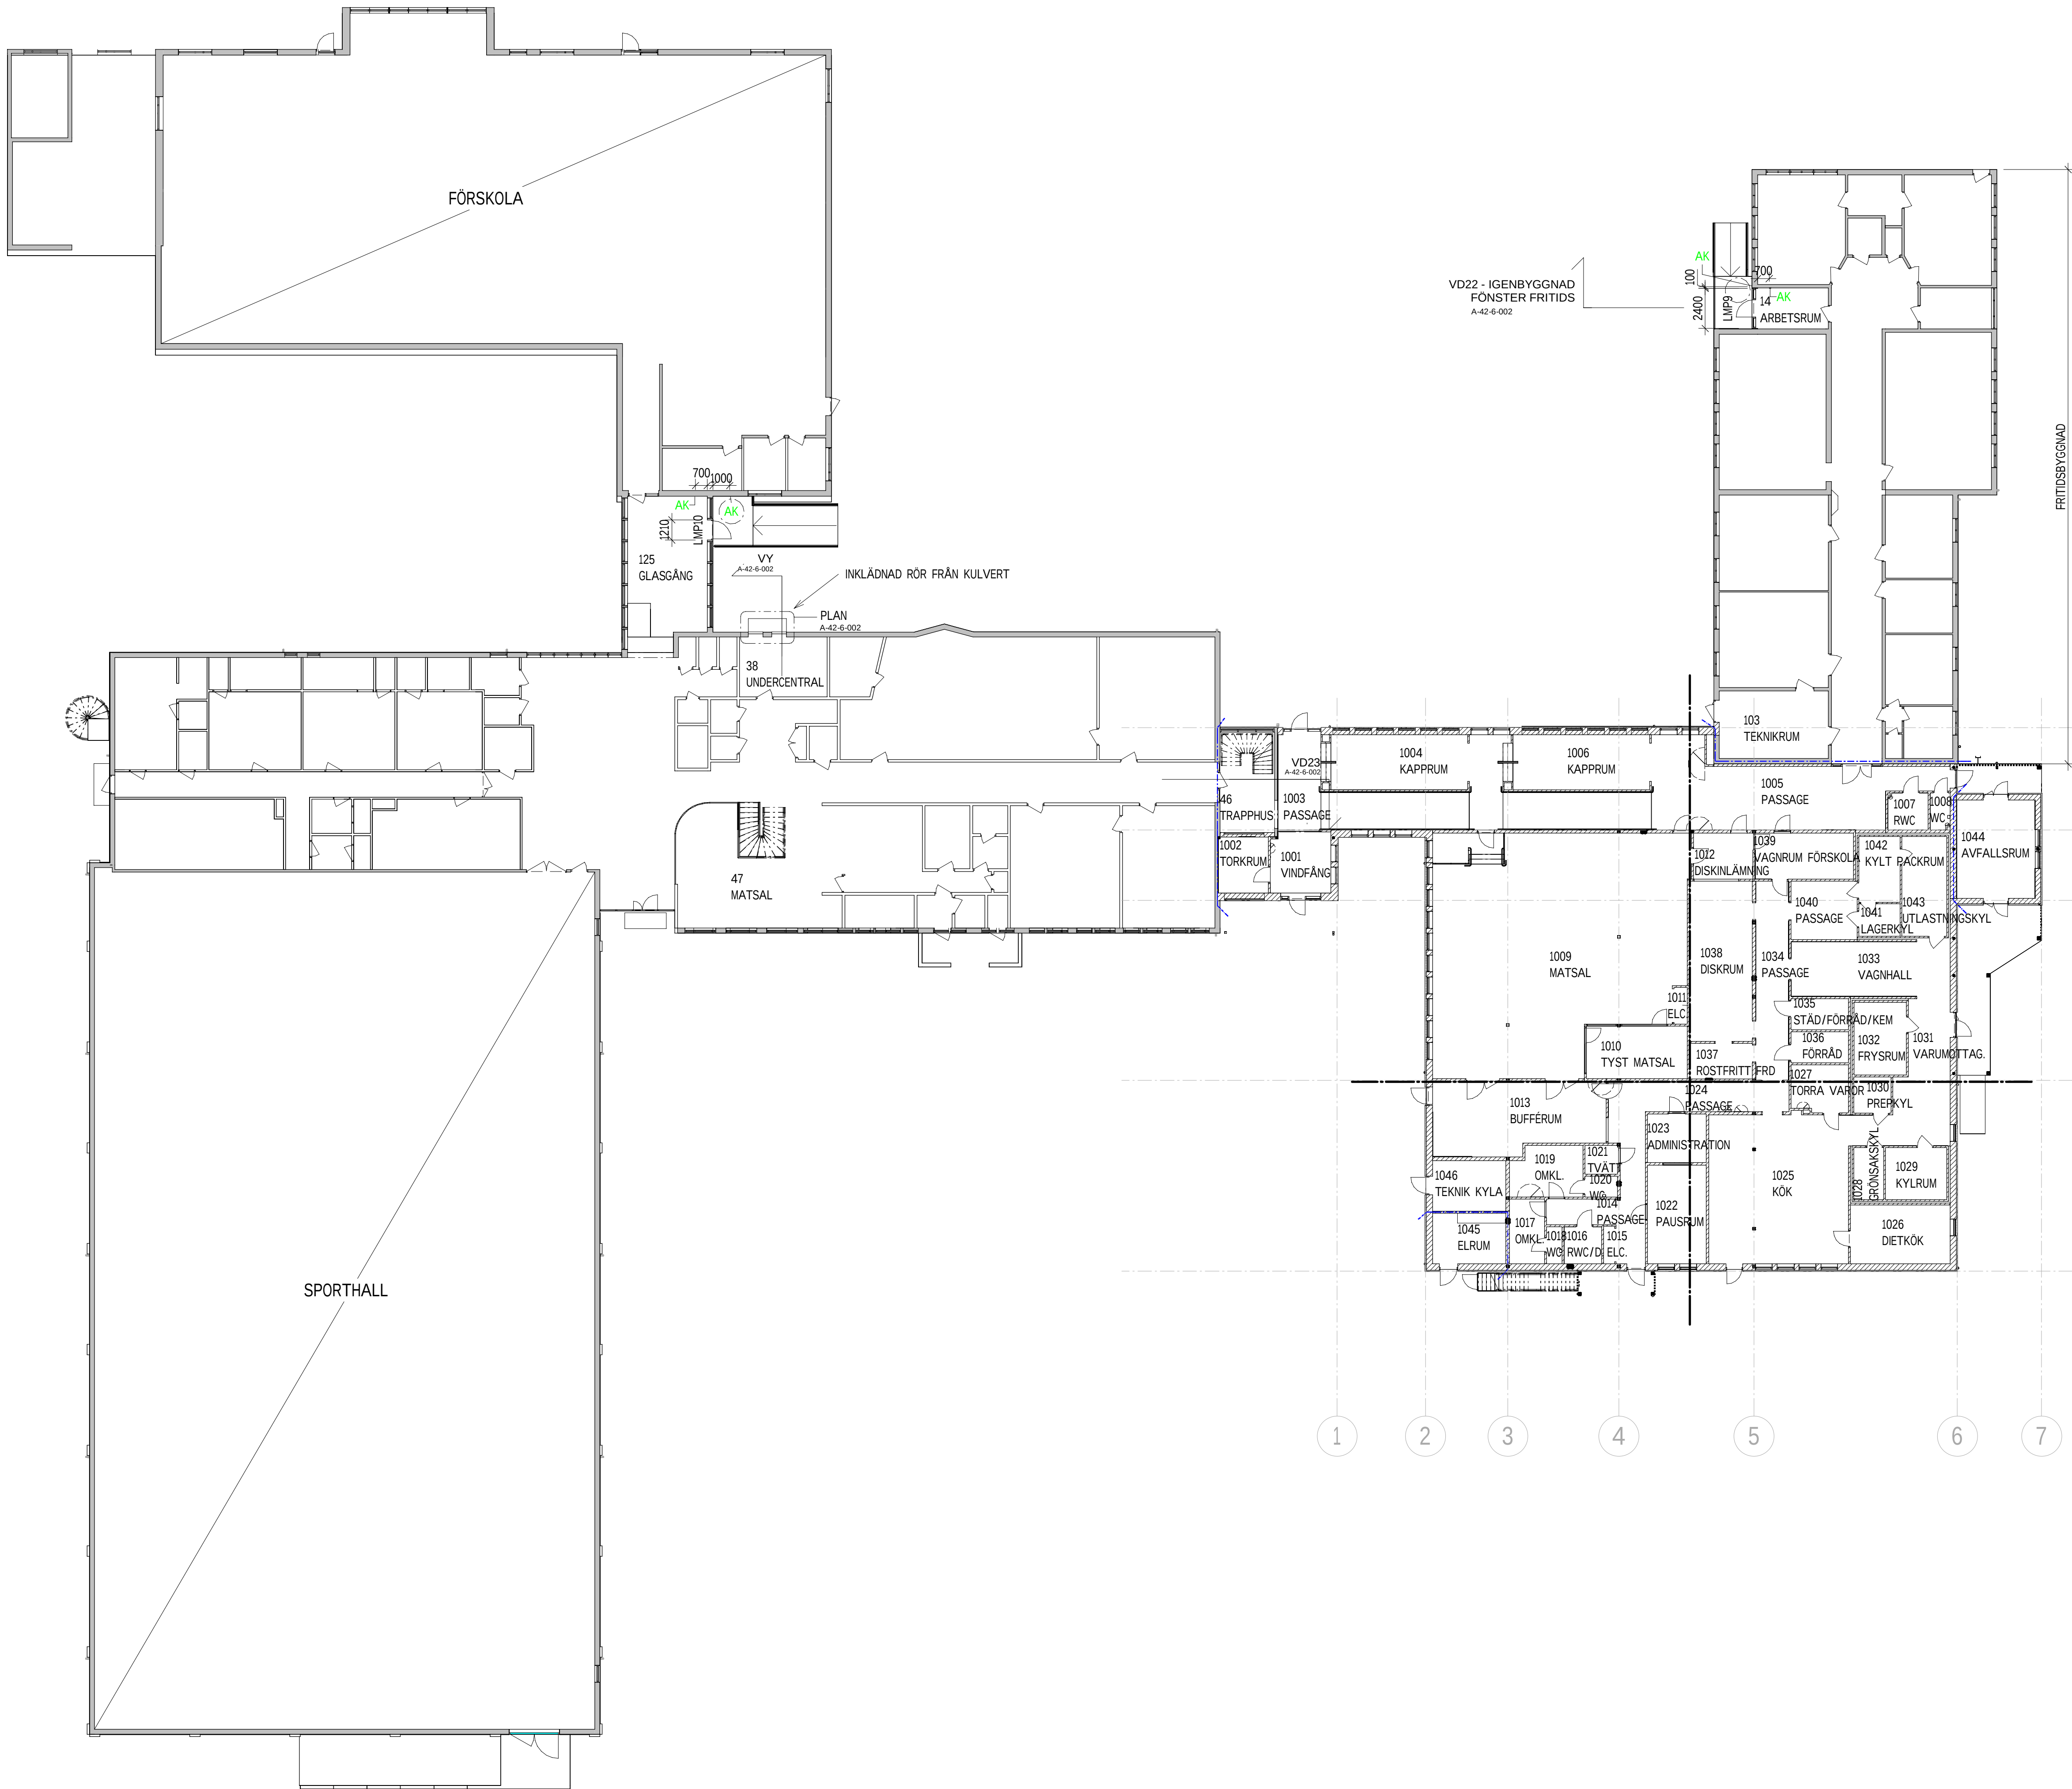

STATUS			
FÖRFRÅGNINGSUNDERLAG			
HANDLING			
BYGGHANDLING			
DATUM	GÖCKAND AV		ANSÖKNINGS PM
2024-12-20	T. BERGSTRÖM		
BESTÄLLARE			
 ROBERTSFORS KOMMUN			
PROJEKTNAMN			
CENTRALKÖK			
OMRÅDE			
ROBERTSFORS KOMMUN			
PROJEKTNUMMER	ADRESS		
	YTTRE RINGVÄGEN 4		
DIARIENUMMER	FASTIGHET		
	FORDONET 1		
DISCIPLIN	FÖRETAG		
A	NORCONSULT SVERIGE AB		
UPPDRAGSRUMMER	SKAPAD AV		
108 83 71	MSR		
TELEFON	KONTAKTPERSON		
010 141 80 00	TOMAS BERGSTRÖM		
BYGGNADSTYP	FLUSKOD (SH 2008)		
1			
VÄRNINGSPÅN	VÄRNINGSDR	DELOMRÅDE	
1			
SYSTEM			
40 SAMMANSATT REDOVISNING			
SPECIFIKATION			
ORIENTERINGSPLAN			
BYGGNADSKATEGORI	SKALA	FORMAT	
PLAN	1:200	A1	
DOKUMENTNUMMER	ÅRSBERG		
A-40-0-100			