



2024-12-20 13:10:44

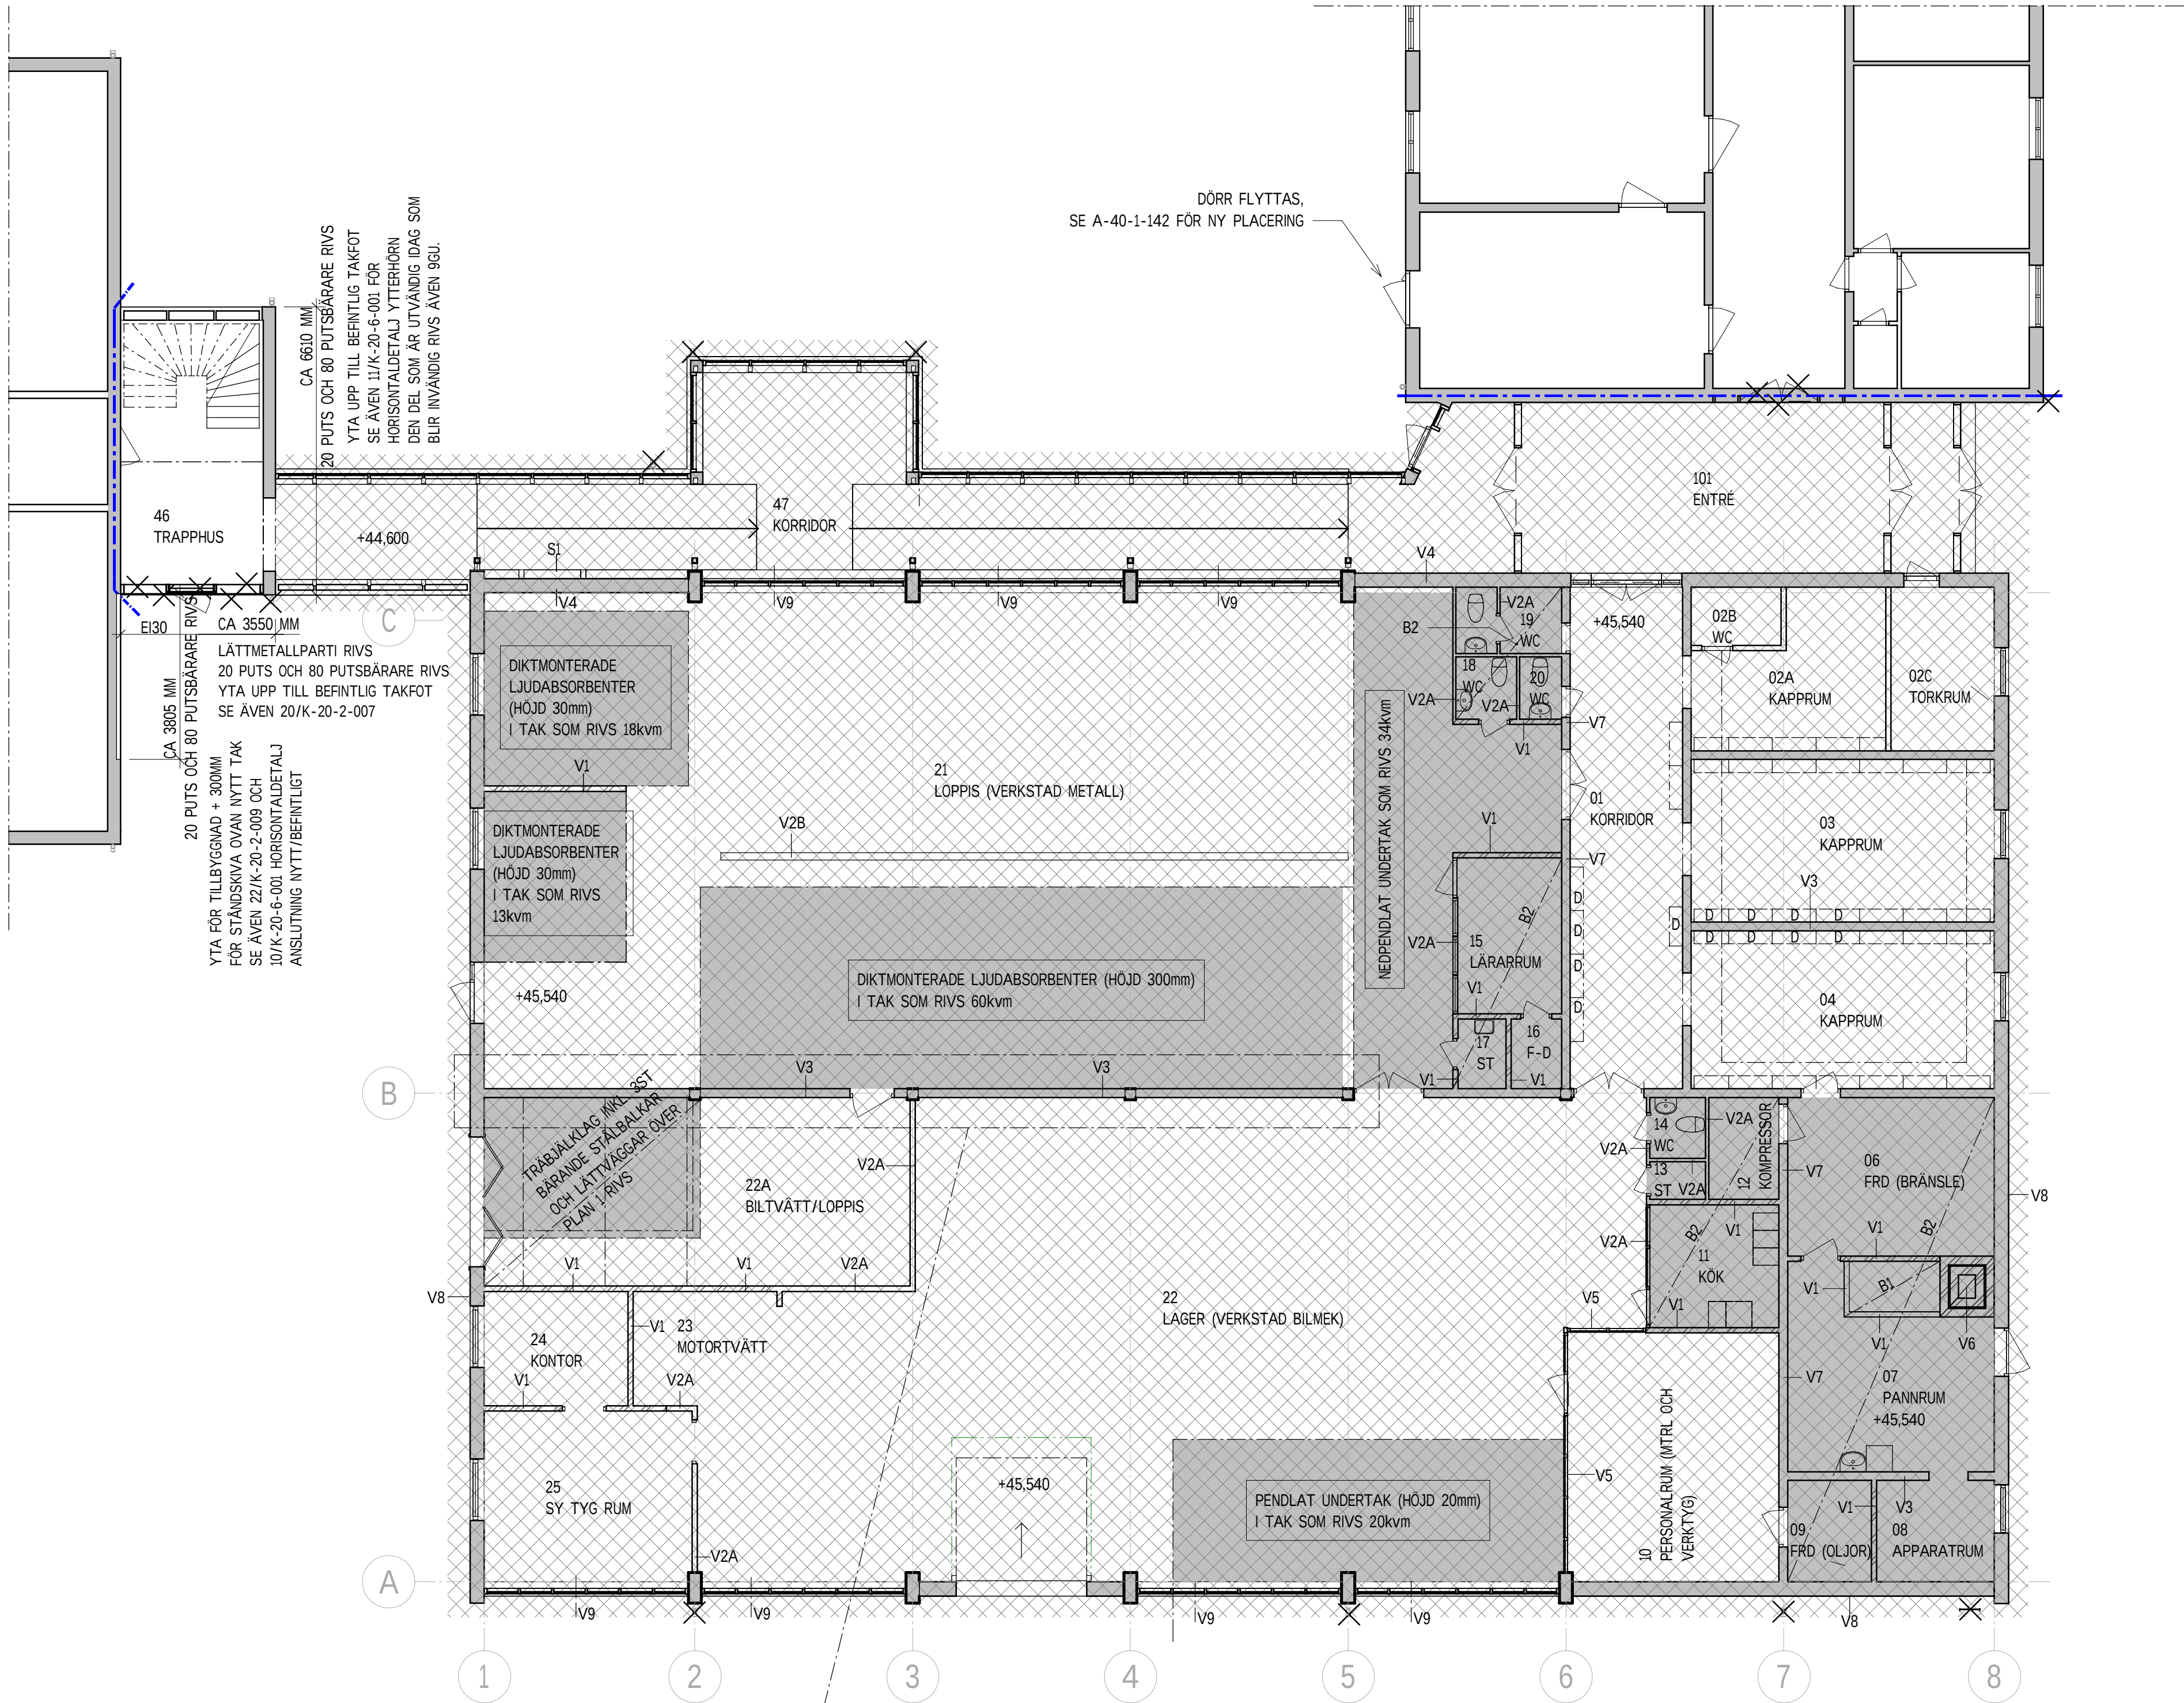

PLAN - BEFINTLIGA FÖRHÅLLANDEN, RIVNING
1 : 100

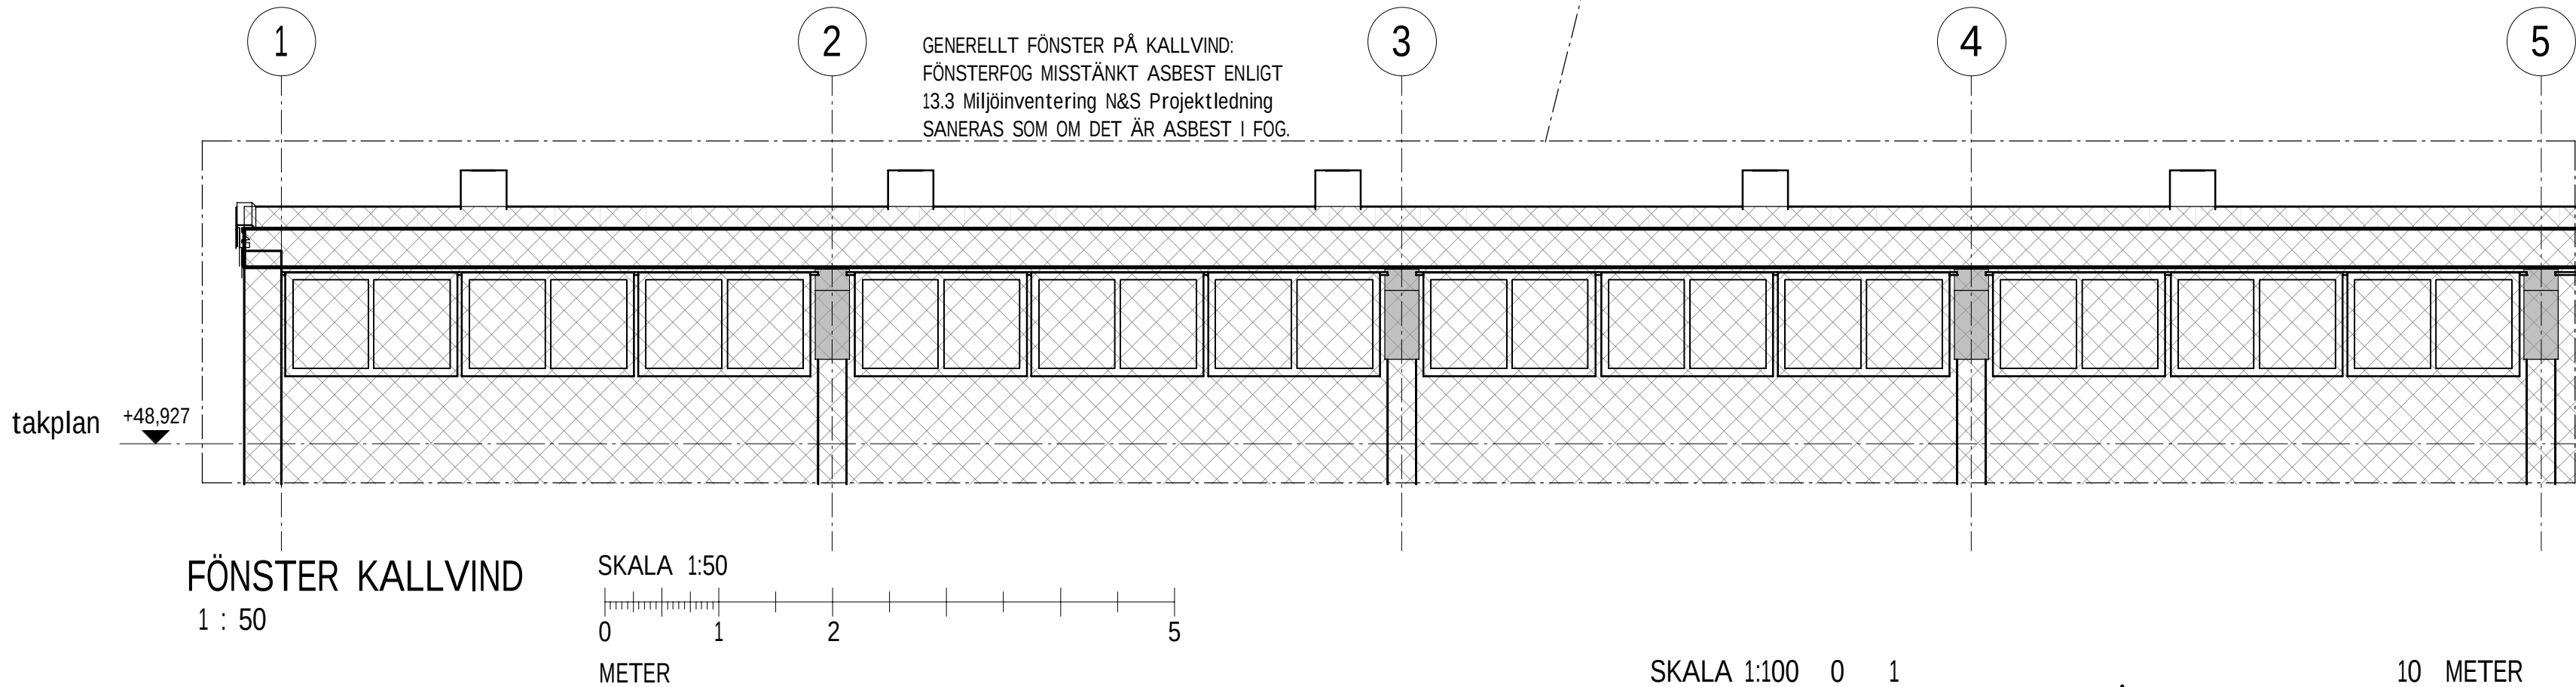

FÖRKLARINGAR

	BYGGNAD SOM RIVS SE RITNINGAR GYMNASIESKOLA DATERADE 1994 OCH MILJÖINVENTERING DATERAD 2022
	BEF. DÖRR
	BRANDCELLSGRÄNS EI30
	BEFINTLIG VÄGG
	BEFINTLIG BÄRANDE VÄGG
S1	BETONGSOCKEL
V1	PUTS + 120 TEGEL + PUTS
V2A	SKIVOR + TRÄREGLAR + SKIVOR
V2B	TRÄREGLAR + SKIVA
V3	200 BETONGSTEN
V4	325 LÄTTBETONG
V5	GLASPARTI VÄGG
V6	SKORSTEN: 200 TEGEL + 30ISOL + 200TEGEL
V7	200 BÄRANDE BETONGSTEN
V8	325 BÄRANDE LÄTTBETONG
V9	YTTERVÄGG, TJOCKLEK 325mm INNEHÅLLER ASBEST-SKIVOR
B1	150 BETONGBJÄLKLAG
B2	200 BETONGBJÄLKLAG + ISOLERING

HÄNVISNINGAR

FASADER - RIVNING	A-40-3-001-R
TAKPLAN - RIVNING	A-41-1-001-R
PLAN 1 - ÖVERSIKT, BRAND	A-40-1-100
FASADER	A-40-3-001

STATUS		
FÖRFRÅGNINGSUNDERLAG		
HANDLING		
BYGGHANDLING		
DATUM	2024-12-20	ANSÖKAN AV
T. BERGSTRÖM		ADRESSER PM
BESTÄLLARE		
ROBERTSFORS KOMMUN		
PROJEKTNAMN		
CENTRALKÖK		
KONTRAKT		
ROBERTSFORS KOMMUN		
PROJEKTNUMMER	1088371	ADRESS
YTTRE RINGVÄGEN 4		FASTIGHET
FORDONET 1		DISCIPLIN
A		FÖRETAG
NORCONSULT SVERIGE AB		UPPDRAGSNUMMER
1088371		SKAPAD AV
MSR		TELEFON
010 141 80 00		KONTAKTPERSON
TOMAS BERGSTRÖM		BYGGNADSTYP
FLUSKÖK (VIT 2008)		VÄNINGSPLAN
1		VÄNINGSDEL
DELOMRÅDE		SYSTEM
40 SAMMANSATT REDOVISNING		
SPECIFIKATION		
PLAN		
RIVNING	SKALA	FORMAT
1:100	A1	ANSÖKAN
FILNAMN: N:\1088371\1088371\Arbetsmaterial\02 BIM\A3D_Model\Rivningsmodell-2024.rvt		