

MÅTT ANGES I MILLIMETER DÄR EJ ANNAT ANGES.  
PLUSHÖJDER ANGES I METER, PLUSHÖJDER ENLIGT RH2000  
OCH AVSER FÄRDIG YTA, DÄR EJ ANNAT ANGES.

— . — . — = BRANDCELLSGRÄNS EI30

DÖRRAR/FÖNSTER

|                   |                                              |
|-------------------|----------------------------------------------|
| E15/E30/Ei30/Ei60 | = BRANDKLASSAD DÖRR/FÖNSTER                  |
| -C                | = DÖRRSTÄNGARE                               |
| M                 | = MAGNETHÅLLARE                              |
| -Sm/-Sa/S200      | = BRANDTÄTHET DÖRRAR ENL<br>DÖRRUPPSTÄLLNING |

 = UTRYMNINGSRIKTNING

  = VÄGLEDANDE MARKERING FÖR  
TILLGÅNGLIG UTRYMNING  
NÖDBELYST

 = HANDBRANDSLÄCKARE

 = UTRYMNINGSPLAN

+XX,XXX = HÖJD ÖVER FÄRDIGT GOLV, METER

☐ = BEFINTLIG VÄGG

 = BÄRANDE INNERVÄGG ENL. K

 = KYL-/FRYSRUMSVÄGG

 = NY VÄGG


 = BEF. DÖRR

 = NY DÖRR



|                    |              |
|--------------------|--------------|
| PLAN - RIVNING     | A-40-1-001-F |
| FASADER - RIVNING  | A-40-3-001-F |
| FASADER - ÖVERSIKT | A-40-3-001   |

RITNING KRÄVER FÄRGUTSKRIFT FÖR KORREKT UTSEENSE

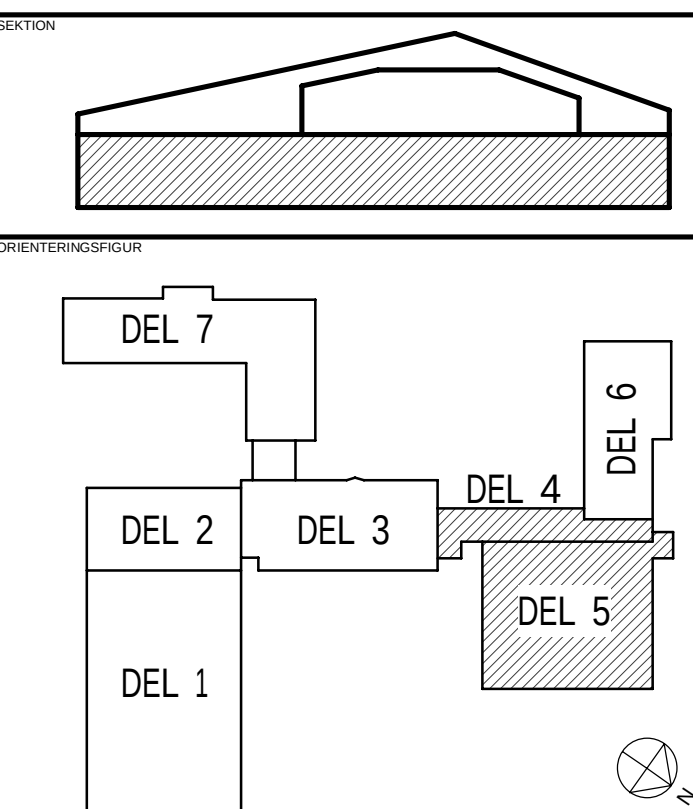

STATUS

# BYGGHANDLING

|            |              |          |
|------------|--------------|----------|
| DATUM      | GÖDKÄND AV   | ÄNDRINGS |
| 2024-12-20 | T. BERGSTRÖM |          |



PROJEKTNAMN

CENTRAALKÖK

OMRÅDE  
ROBERTSFORS KOMMUN

|               |                             |
|---------------|-----------------------------|
| PROJEKTNUMMER | ADRESS<br>YTTRE RINGVÄGEN 4 |
|---------------|-----------------------------|

|               |            |
|---------------|------------|
| ARTIKELNUMMER | FÄSTIGHET  |
|               | FORDONET 1 |
| DISCIPLIN     | FÖRETAG    |

|                            |                    |
|----------------------------|--------------------|
| A                          | NORCONSULT SVERIGE |
| JPPDRAGSNUMMER<br>100-8874 | SKAPAD AV<br>859   |

|               |                 |
|---------------|-----------------|
| 108 83 71     | SBS             |
| TELEFON       | KONTAKTPERSON   |
| 010 141 80 00 | TOMAS BERGSTRÖM |

|                |                            |
|----------------|----------------------------|
| 1010 141 00 00 | TOMAS BERGSTRÖM            |
| 8YGGNÄSVERK    | PLUSHÖJD (RH 2000)         |
|                | +44.60, +45.07, +45.54 (F) |

|   |            |                       |
|---|------------|-----------------------|
| 1 | VÄNINGSDEL | DELOMRÅDE<br>DEL 4, 5 |
|---|------------|-----------------------|

## 40 SAMMANSATT REDOVISNING

|                          |       |        |
|--------------------------|-------|--------|
| PLAN 1 - ÖVERSIKT, BRAND |       |        |
| RITNINGSKATEGORI         | SKALA | FORMAT |

|                |       |          |
|----------------|-------|----------|
| PLAN           | 1:100 | A1       |
| DOKUMENTNUMMER |       | ÄNDERUNG |
| A 10 1 100     |       |          |

|            |  |
|------------|--|
| A-40-1-100 |  |
|------------|--|



PLAN 1  
1 : 100

SKALA 1:100    0    1

10 METER