

MÅTT ANGES I MILLIMETER DÄR EJ ANNAT ANGES.

===== BRANDCELLSGRÄNS EI30

A = VITMÅLAD SLÄTPLÅT.
LÄNGD ANP. SÅ 50mm INFÄSTNINGENSYTA PÅ
VARDERA SIDA ERHÅLLS, HÖJD LIKA KYL-/FRYSRUM

FS1 = FÖRDELARSKÅP GOLVVÄRME ENL. VS

FS2 = FÖRDELARSKÅP FÖR TAPPVATTEN ENL. VS

AK = ARMBÅGSKONTAKT

KL = KORTLÄSARE

ÖK = ÖPPNAKNAPP

HL1 = HÖRNLIST ROSTFRI ENLIGT BESKRIVNING
HL2 = HÖRNLIST PLAST ENLIGT BESKRIVNING

H1,H2=HANDLEDARE &
R1,R2=RÄCKE SE A-45-4-001

ILX = LÅSBAR INSPEKTIONSLUCKA TYP GYPROC INEO,
INFÄSTNING ENL. LEVERANTÖRENS ANVISNINGAR.
STORLEK ENL. RESP. LITTRA
IL1: 150x150mm, 500mm ÖFG
IL2: 400x400mm, 500mm ÖFG

☐ = BEFINTLIG VÄGG

 = BÄRANDE INNERVÄGG ENL. K


 = KYL-/FRYSRUMSVÄGG

 = NY INNERVÄGG ENL. LITTERA

VX

ONSTER	A-42-4-001
ÄTTMETALLPARTIER	A-42-4-002
TÄLDDÖRRAR	A-42-4-021
INERDÖRRAR AV TRÄ	A-43-4-011
IVÄNDIGA GLASPARTIER	A-43-4-012
IVÄNDIGA GLASFIBERDÖRRAR	A-43-4-031
CENTRALFRONTER	A-43-4-041
INNERRÄVGSGTYPER	A-43-4-051 --002
IVÄNDIGA DETALJER	A-43-6-001 --003
RAPPA, HANDELDARE, RÄCKE	A-45-4-001
ONSTRUKTIONSRITNINGAR	

RITNING KRÄVER FÄRGUTSKRIFT FÖR KORREKT UTSEENDE

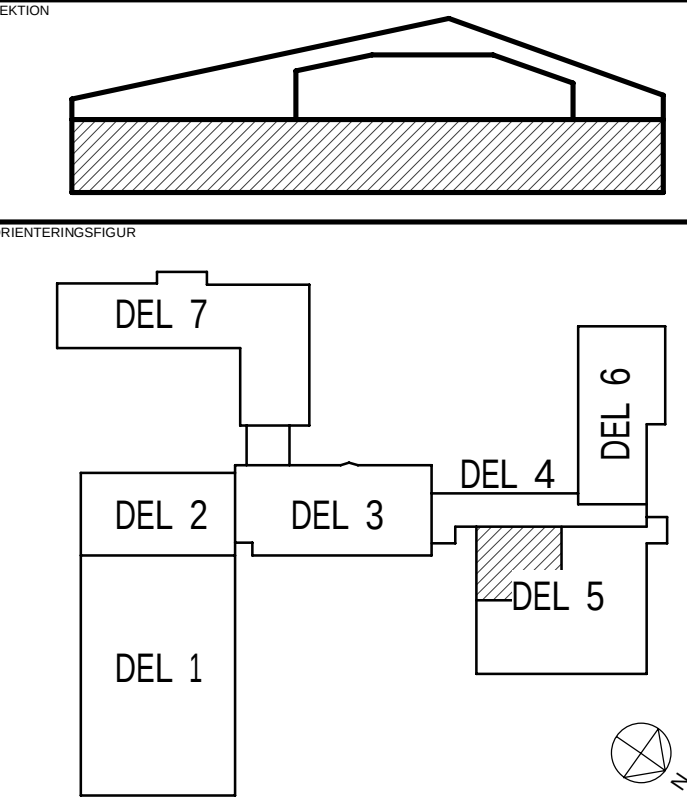

FÖDDER 8 JANUOGUNDEBIL A

DISCUSSION

ATUM	GODKÄND AV	ÄNDRINGS
2004-10-08	E. BERGSTRÖM	

INSTALLARE



PROJEKTNAMN

MRÅDE

PROJEKTNUMMER	ADRESS
---------------	--------

ARIENUMMER	FASTIGHET
	FORDONET 1

DISCIPLIN	FÖRETAG
A	NORCONSULT SVERIGE

108 83 71 SBS

010 141 80 00	TOMAS BERGSTROM
---------------	-----------------


		+45.07, +45.54 (FG)
VÄNINGSPLAN	VÄNINGSDEL	DELOMRÅDE

SYSTEM

PLAN 1 DEL 5.1

PI AN	SKALA	FORMAT
	1:50	A1

A-40-1-151

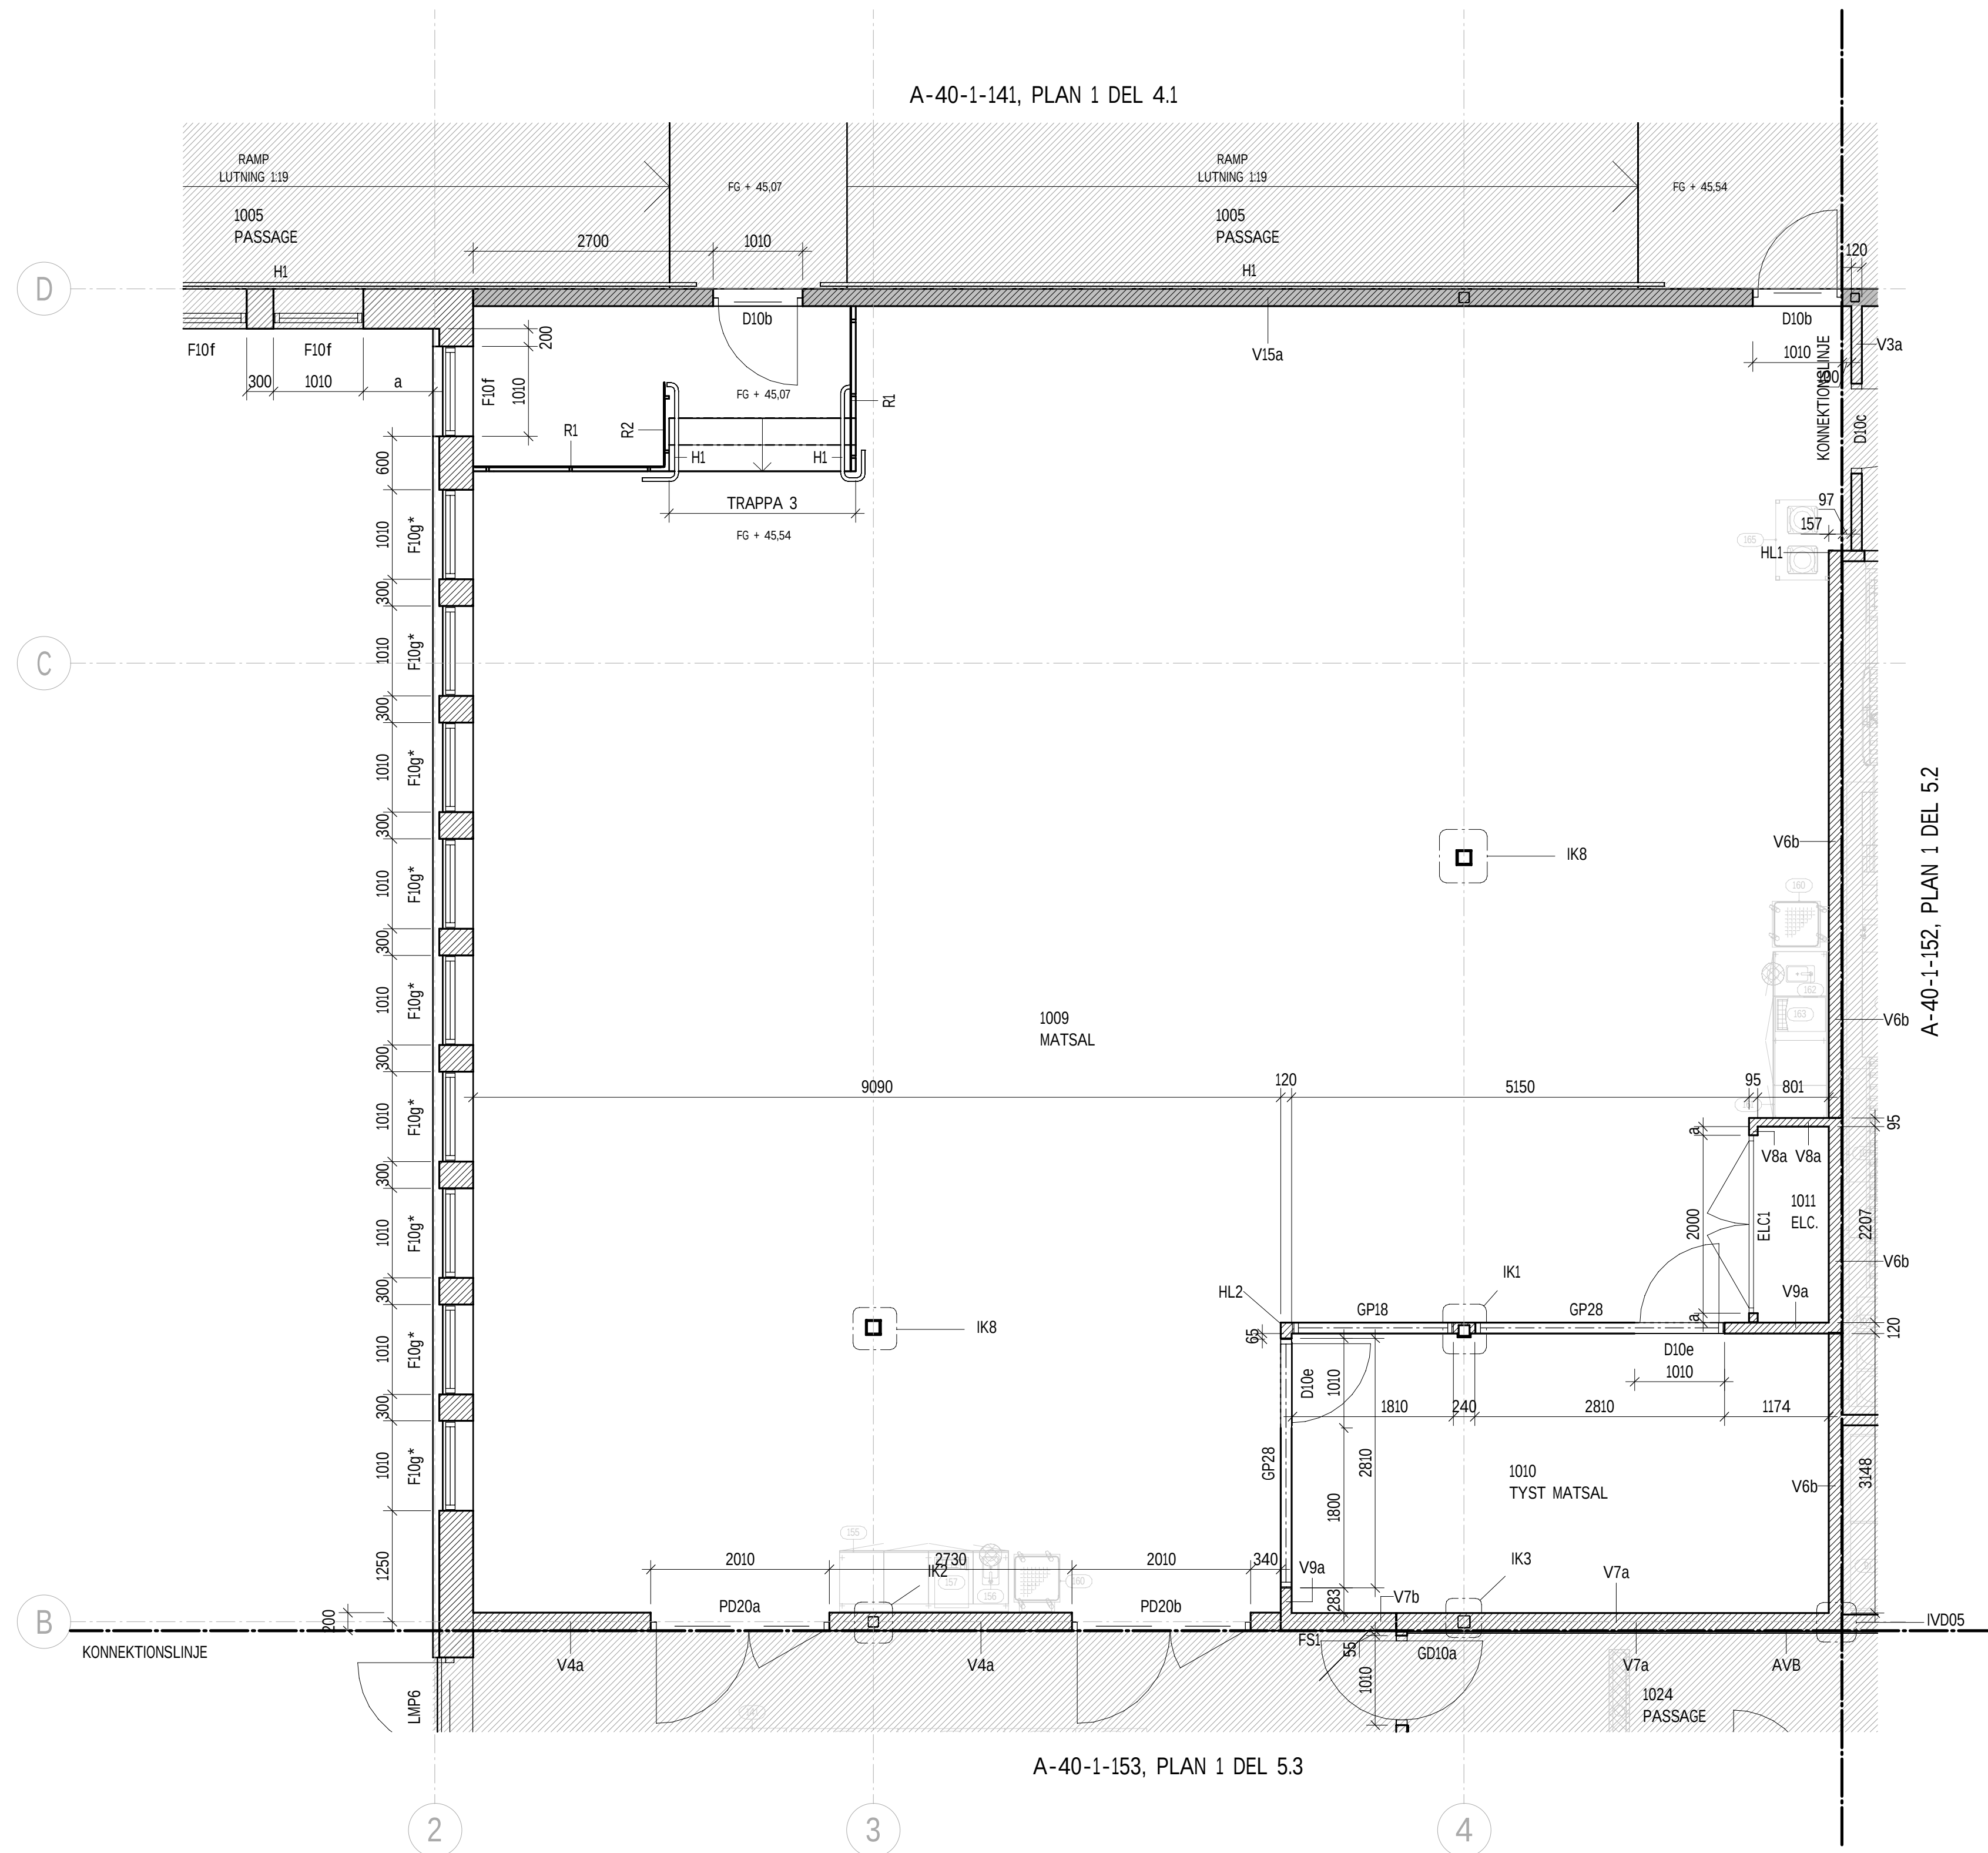

SKALA 1:50 0 1 5 METER