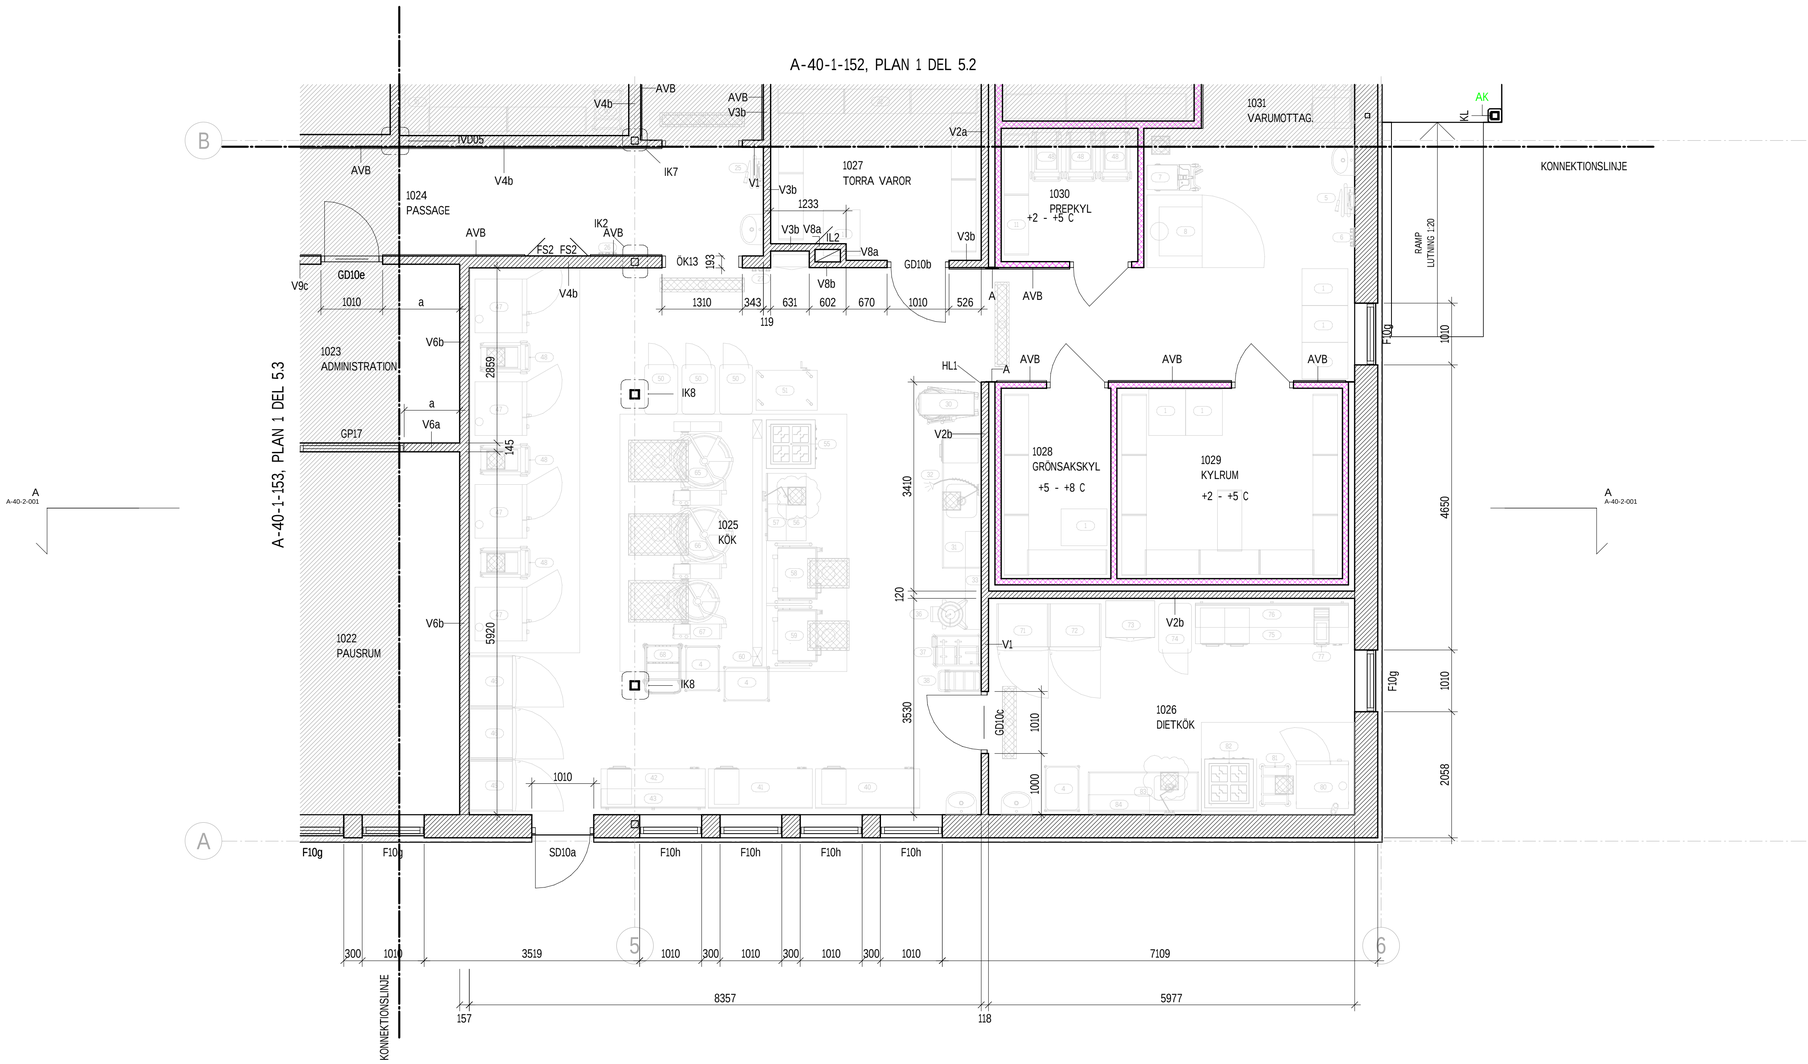

FÖRKLARINGAR

MÅTT ANGES I MILLIMETER DÄR EJ ANNAT ANGES.

= BRANDCELLSGRÄNS EI30

A = VITMÅLAD SLÄTPLÅT.
LÄNGD ANP. SÅ 50mm INFÄSTNINGNSYTA PÅ VARDERA SIDA ERHÅLLS, HÖJD LIKA KYL-/FRYSRUM

FS1 = FÖRDELARSKÅP GOLVVÄRME ENL. VS

FS2 = FÖRDELARSKÅP FÖR TAPPVATTEN ENL. VS

AK = ARMBÅGSKONTAKT

KL = KORTLÄSARE

ÖK = ÖPPNAKNAPP

HL1 = HÖRNLIST ROSTFRI ENLIGT BESKRIVNING
HL2 = HÖRNLIST PLAST ENLIGT BESKRIVNING

H1,H2=HANDLEDARE &
R1,R2=RÄCKE SE A-45-4-001

ILx = LÅSBAR INSPEKTIONSLUCKA TYP GYPROC INEO, INFÄSTNING ENL. LEVERANTÖRENS ANVISNINGAR. STORLEK ENL. RESP. LITTRA
IL1: 150x150mm, 500mm ÖFG
IL2: 400x400mm, 500mm ÖFG

= BEFINTLIG VÄGG

= BÄRANDE INNERVÄGG ENL. K

= KYL-/FRYSRUMSVÄGG

= NY INNERVÄGG ENL. LITTERA
VX

HÄNVISNINGAR

FÖNSTER	A-42-4-001
LÄTTMETALLPARTIER	A-42-4-002
STÄLDÖRRAR	A-42-4-021
INNERDÖRRAR AV TRÄ	A-43-4-011
INVÄNDIGA GLASPARTIER	A-43-4-012
INVÄNDIGA GLASFIBERDÖRRAR	A-43-4-031
ELCENTRALFRONTER	A-43-4-041
INNNERVÄGGSTYPER	A-43-5-001 --002
INVÄNDIGA DETALJER	A-43-6-001 --003
TRAPPA, HANDLEDARE, RÄCKE	A-45-4-001
KONSTRUKTIONSRITNINGAR	

RITNING KRÄVER FÄRGUTSKRIFT FÖR KORREKT UTSEENDE

SEKTION

ORIENTERINGSFIGUR

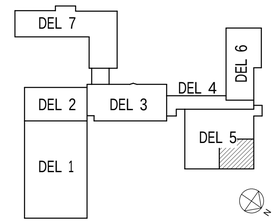

STATUS
FÖRFRÅGNINGSUNDERLAG

HANDLING
BYGGHANDLING

DATUM	GODKÄND AV	ÄNDRINGS PM
2024-12-20	T. BERGSTRÖM	

BESTÄLLARE
ROBERTSFORS KOMMUN

PROJEKTNAMN
CENTRALKÖK

OMRÅDE
ROBERTSFORS KOMMUN

PROJEKTNUMMER	ADRESS: YTTRE RINGVÄGEN 4
DIARIENUMMER	FASTIGHET: FORDONET 1
DISCIPLIN: A	FÖRETAG: NORCONSULT SVERIGE AB
UPPDRAGSNUMMER: 108 83 71	SKAPAD AV: SBS
TELEFON: 010 141 80 00	KONTAKTPERSON: TOMAS BERGSTRÖM
BYGGNADSVERK	PLUSNIVÅ RH 2000: +45,54 (FG)
VÅNINGSPLAN: 1 / VÅNINGSDEL	DELOMRÅDE: DEL 5.4

SYSTEM
40 SAMMANSATT REDOVISNING

SPECIFIKATION
PLAN 1, DEL 5.4

RITNINGSKATEGORI	SKALA	FORMAT
PLAN	1:50	A1

DOKUMENTNUMMER: A-40-1-154 | ÄNDRING:

2024-12-20 11:11:35

FILNAMN: C:\Norconsult\Autodesk\Revit\1088371-Centralkok Robertsfors_centralfil-2024_malsta.rvt