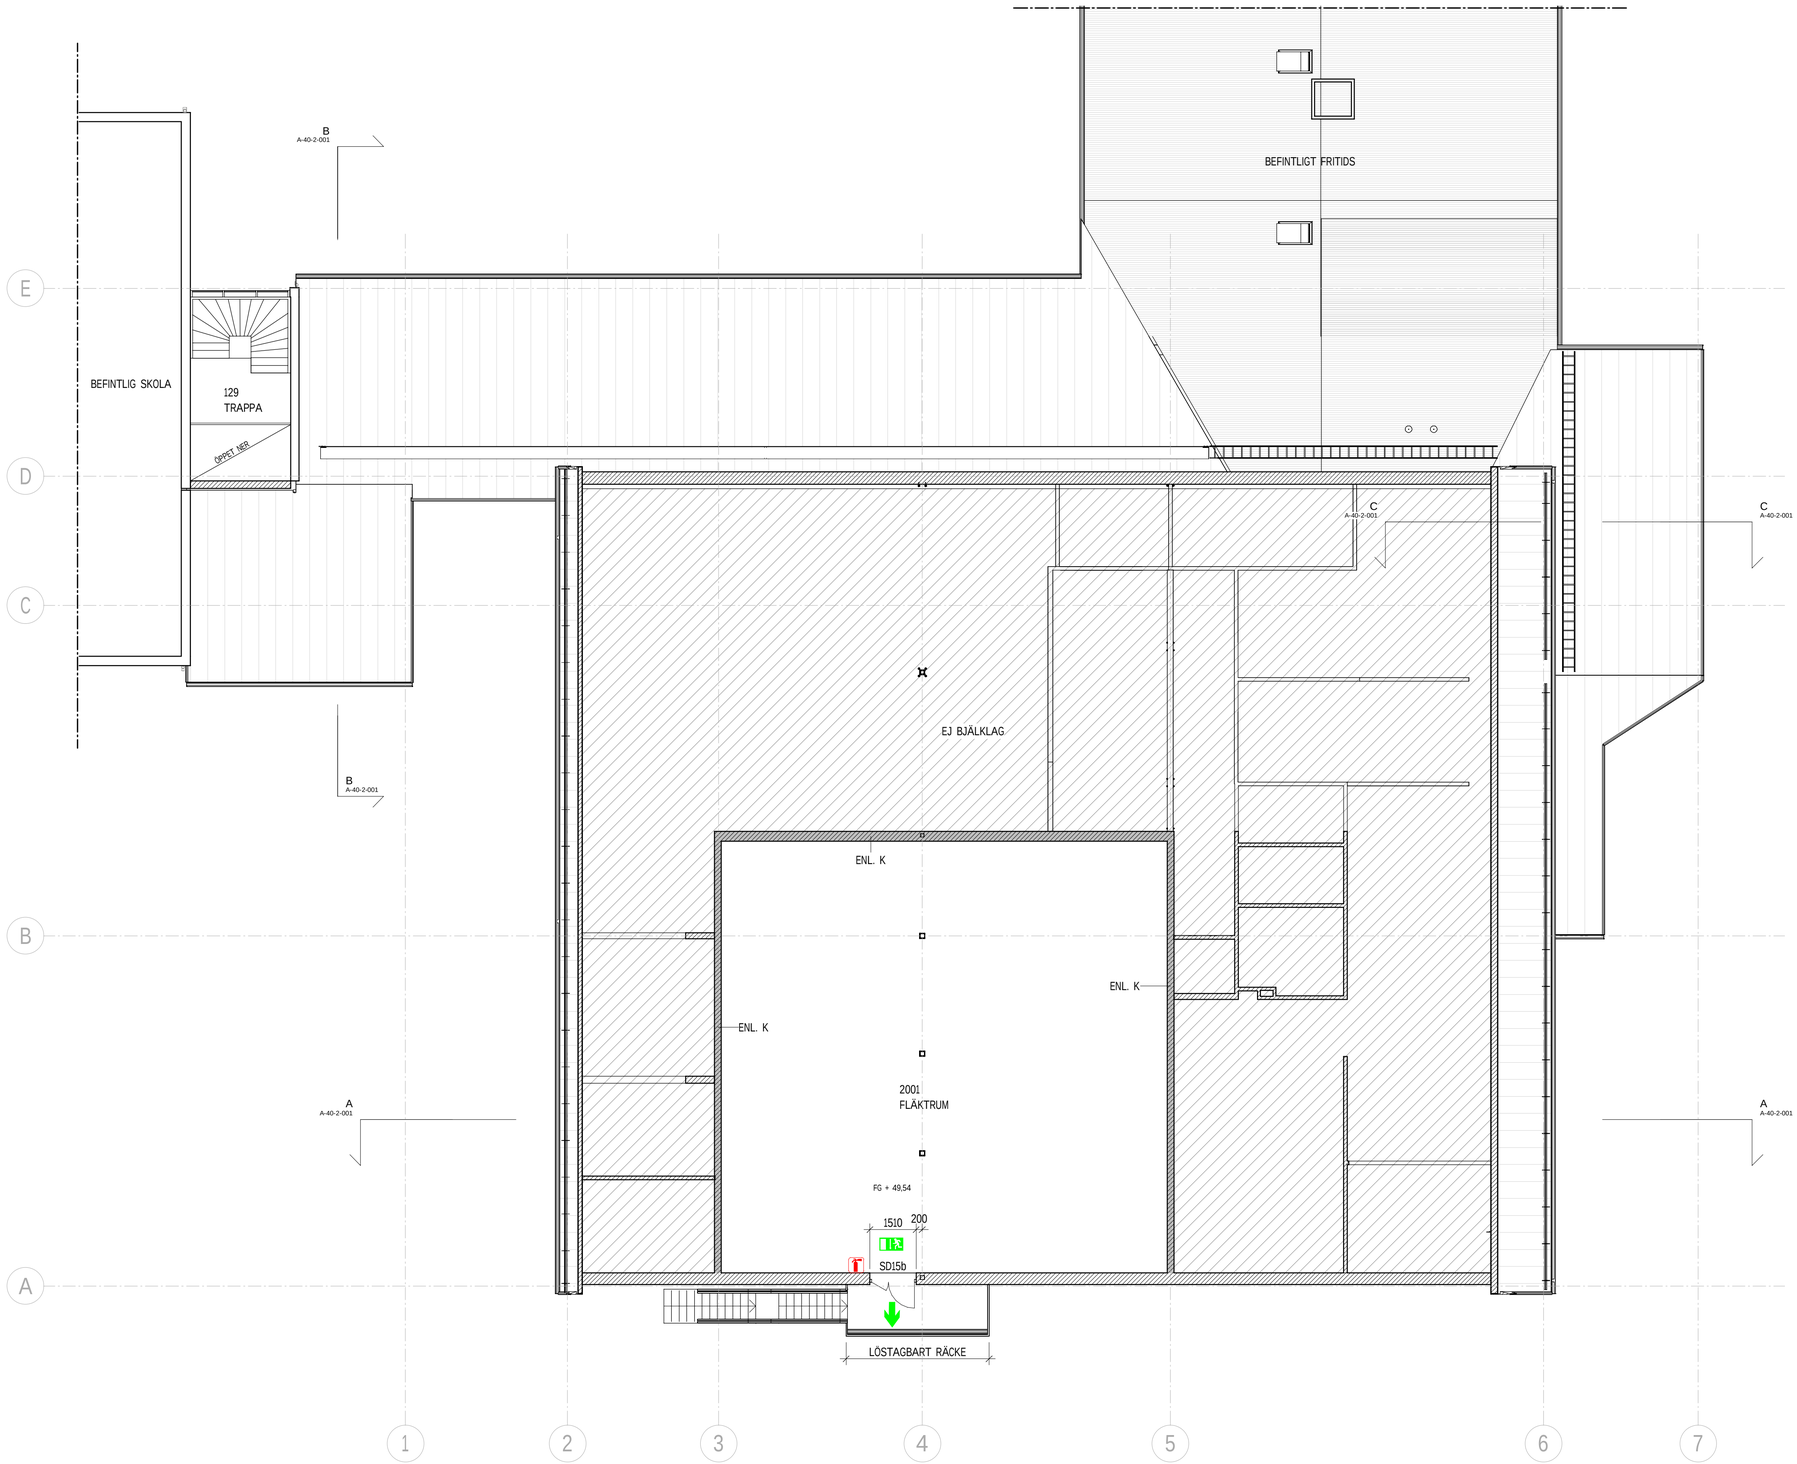

PLAN 2
1 : 100

SKALA 1:100 0 1 10 METER

FÖRKLARINGAR

MÅTT ANGES I MILLIMETER DÄR EJ ANNAT ANGES.
PLUSHÖJDER ANGES I METER, PLUSHÖJDER ENLIGT RH2000 OCH AVSER FÄRDIG YTA, DÄR EJ ANNAT ANGES.

= BRANDCELLSGRÄNS EI30

DÖRRAR/FÖNSTER

EI15/E30/EI30/EI60	= BRANDKLASSAD DÖRR/FÖNSTER
-C	= DÖRRSTÄNGARE
M	= MAGNETHÅLLARE
-Sm/-Sa/S200	= BRANDTÄTHET DÖRRAR ENL DÖRRUPPSTÄLLNING

= UTRYMNINGSRIKTNING

= VÄGLEDANDE MARKERING FÖR TILLGÄNGLIG UTRYMNING NÖDBELYST

= HANDBRANDSLÄCKARE

UP = UTRYMNINGSPLAN

+XX,XXX = HÖJD ÖVER FÄRDIGT Ggolv, METER

= BEFINTLIG VÄGG

= BÄRANDE INNERVÄGG ENL. K

= KYL-/FRYSRUMSVÄGG

= NY VÄGG

30° = BEF. DÖRR

90° = NY DÖRR

45° = KYLRUMSDÖRR

HÄNVISNINGAR

PLAN - RIVNING	A-40-1-001-R
FASADER - RIVNING	A-40-3-001-R
FASADER - ÖVERSIKT	A-40-3-001

RITNING KRÄVER FÄRGUTSKRIFT FÖR KORREKT UTSEENDE

SEKTION

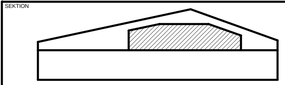

ORIENTERINGSFIGUR

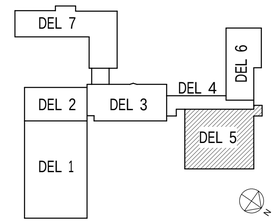

STATUS: FÖRFRÅGNINGSUNDERLAG
HANDLING: BYGGHANDLING

DATUM	GODKÄND AV	ÄNDRINGS PM
2024-12-20	T. BERGSTRÖM	

BESTÄLLARE: ROBERTSFORS KOMMUN

PROJEKTNAMN: CENTRALKÖK
OMRÅDE: ROBERTSFORS KOMMUN

PROJEKTNUMMER	ADRESS: YTTRE RINGVÄGEN 4
DIARIENUMMER	FASTIGHET: FORDONET 1
DISCIPLIN: A	FÖRETAG: NORCONSULT SVERIGE AB
UPPDRAGSNUMMER: 108 83 71	GRANSKAD AV: SBS
TELEFON: 010 141 80 00	KONTAKTPERSON: TOMAS BERGSTRÖM
BYGGNADSVERK	PLUSHÖJD (RH 2000): +49,54 (FG)
VÅNINGSPLAN: 2 / VÅNINGSDEL	DELOMRÅDE: DEL 5
SYSTEM: 40-SAMMANSATT REDOVISNING	
SPECIFIKATION: PLAN 2 - ÖVERSIKT, BRAND	
RITNINGSKATEGORI: PLAN	SKALA: 1:100 / FORMAT: A1
DOKUMENTNUMMER: A-40-1-200	ÄNDRING

2024-12-20 10:54:27

FILNAMN: C:\Norconsult\Autodesk\Revit\1088371-Centralkök Robertsfors_centralfil-2024_matsta.rvt