


FÖRKLARINGAR

MÄTT ANGES I MILLIMETER DÄR EJ ANNAT ANGES.  
PLUSHÖJDER ANGES I METER, PLUSHÖJDER ENLIGT RH2000  
OCH AVSER FÄRDIG YTA, DÄR EJ ANNAT ANGES.

HÄNVISNINGAR

PLAN - RIVNING A-40-1-001-R  
FASADER - RIVNING A-40-3-001-R  
FASADER - ÖVERSIKT A-40-3-001

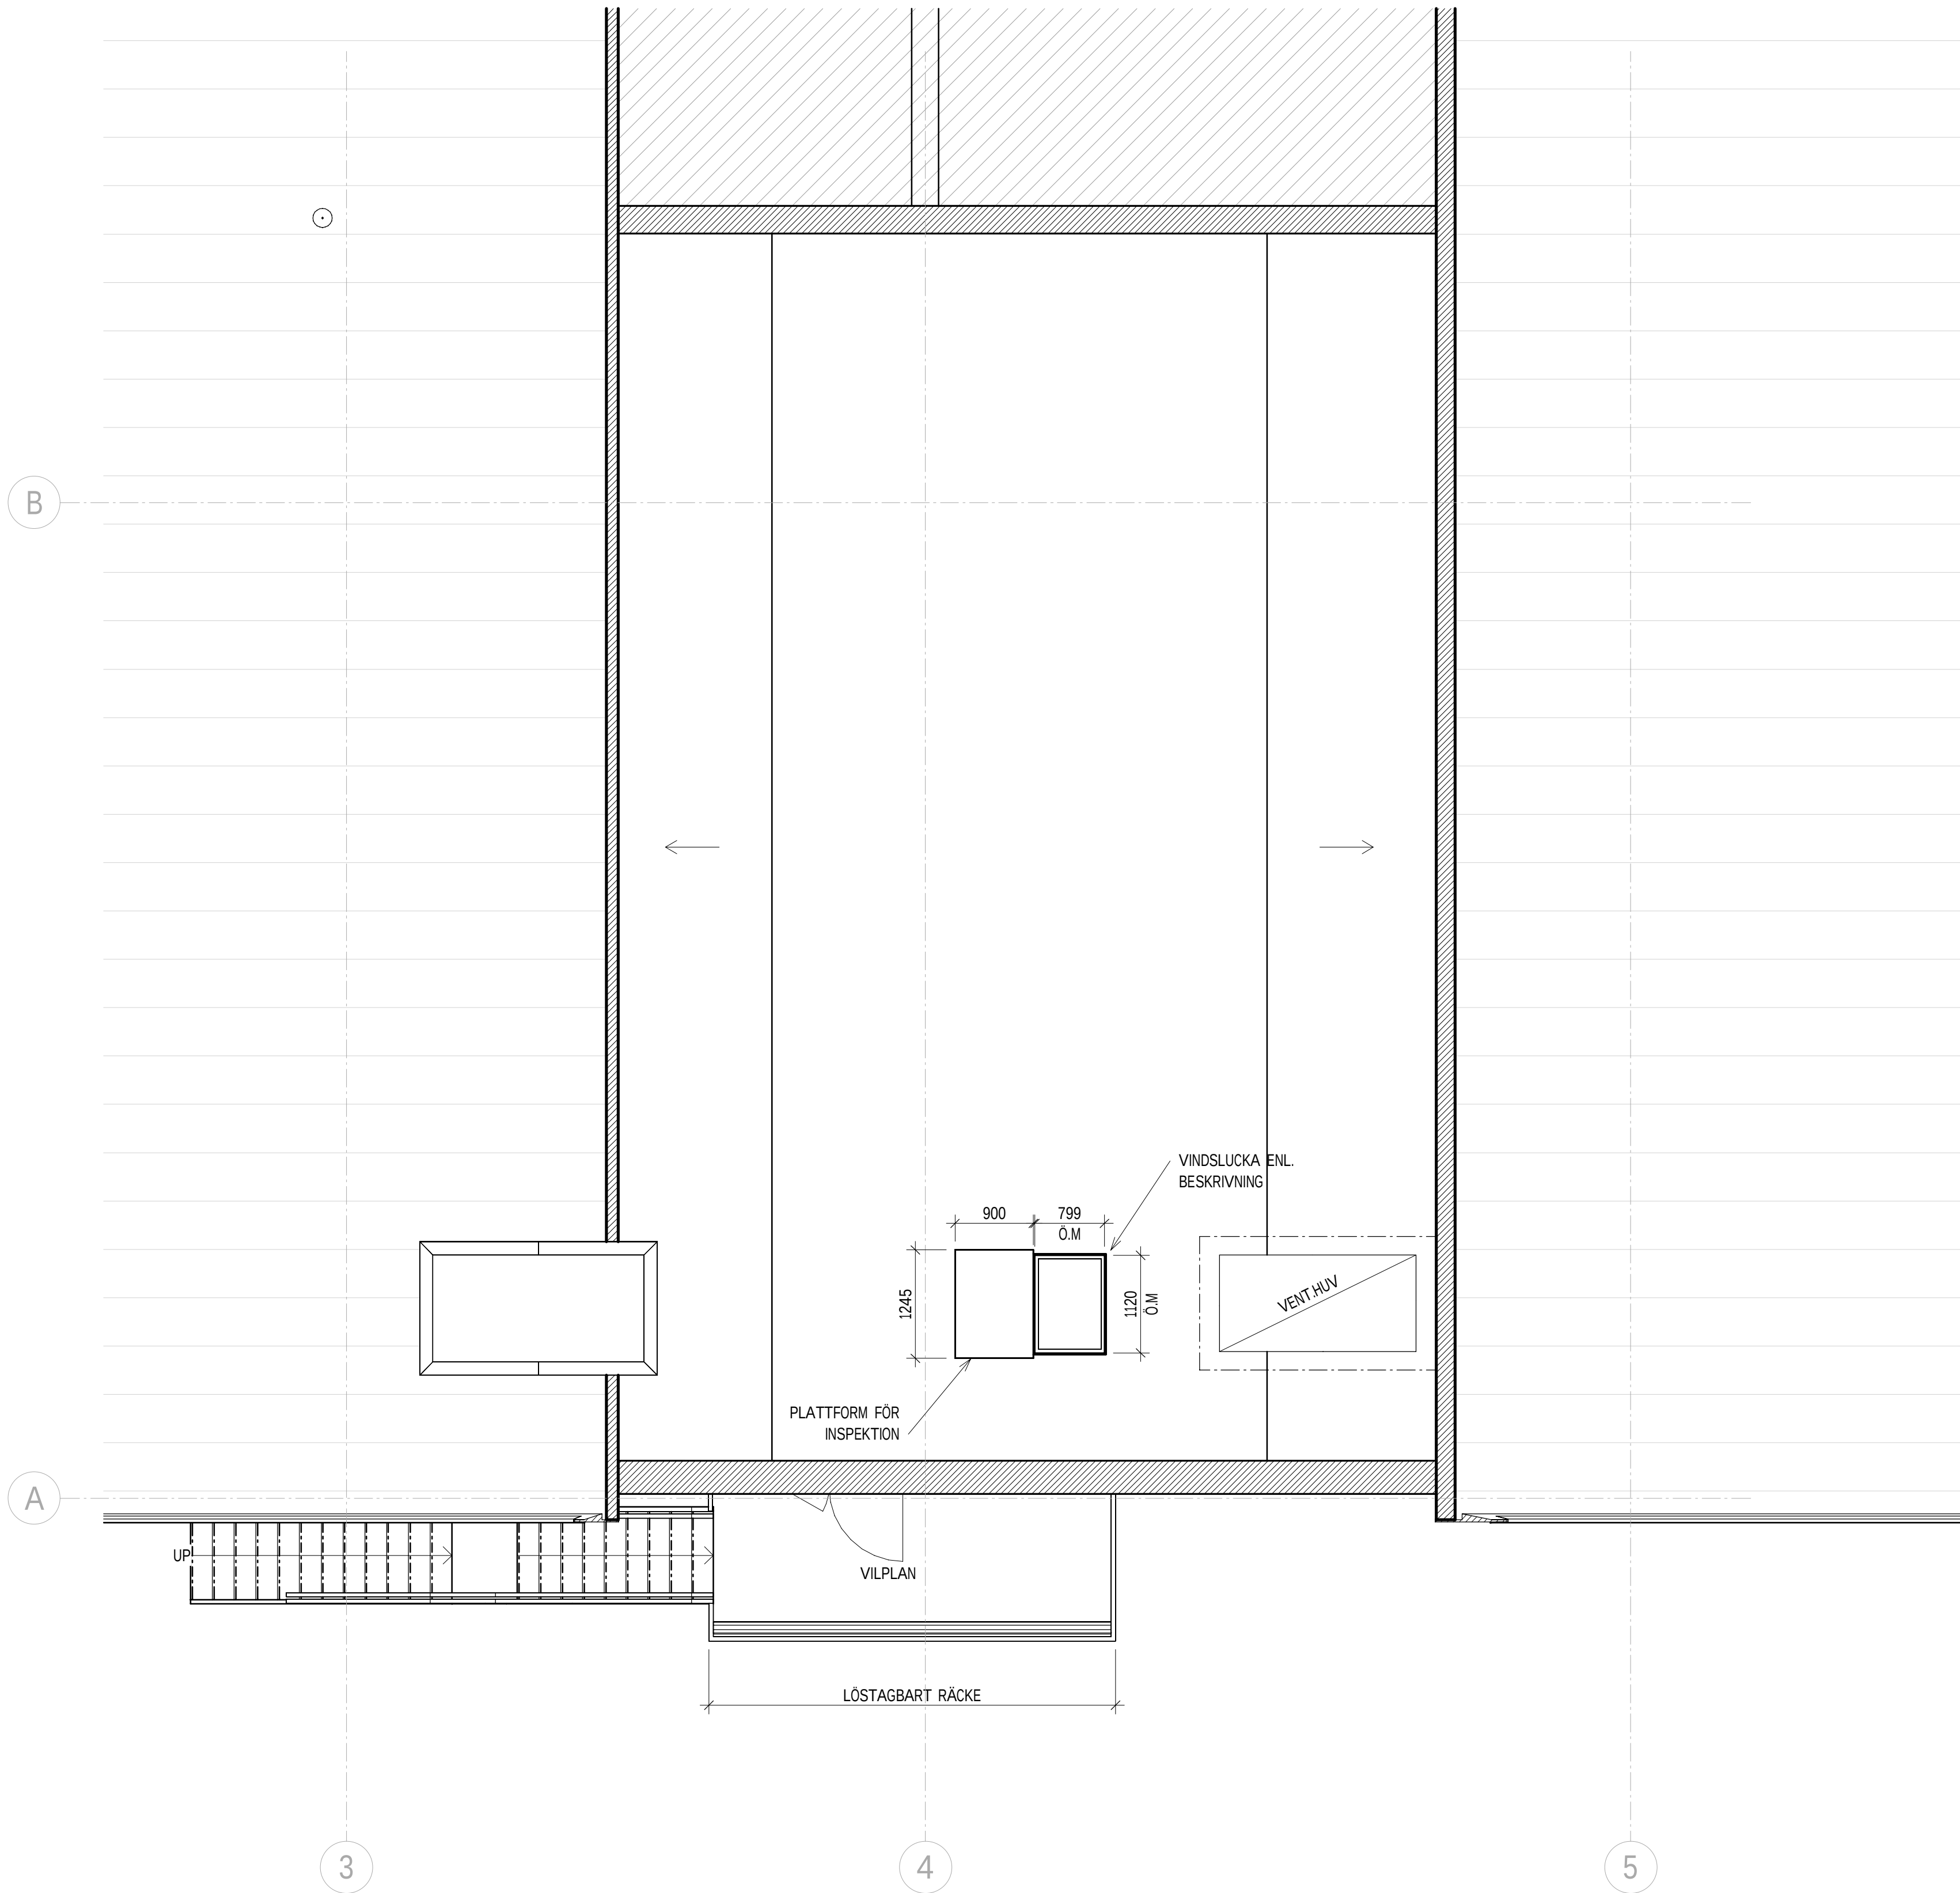

VINDSPLAN  
1 : 50

SKALA 1:50 0 1 5 METER

SEKTION

ORIENTERINGSSKISS

STATUS

HANDLING

DATUM

LOSRÄDD AV

ANSVARIGS PM

BESTÄLLARE

PROJEKTNAMN

OMFÄTTE

PROJEKTNUMMER

ADRESS

DARIENUMMER

FASTIGHET

DISCIPLIN

FÖRETAG

UPPDRAGSRUMMER

SKAPAD AV

TELEFON

KONTAKTPERSON

BYGGNADSTYP

PLUSHÖJDER (RH 2000)

VÄNINGSPLAN

VÄNINGSDEL

DELOMRÅDE

SYSTEM

SPECIFICATION

BYGGNADSTYP

PLAN

SKALA

FORMAT

DOKUMENTNUMMER

ÄNDRING

FÖRFRÅGNINGSUNDERLAG

BYGGHANDLING

2024-12-20

T. BERGSTRÖM

ROBERTSFORS  
KOMMUN

CENTRAKKÖK

ROBERTSFORS KOMMUN

YTTRE RINGVÄGEN 4

FORDONET 1

A

NORCONSULT SVERIGE AB

108 83 71

MSR

010 141 80 00

TOMAS BERGSTRÖM

3

DEL 5

40 SAMMANSATT REDOVISNING

VINDSPLAN

PLAN

1:50

A1

A-40-1-300