

HÄNVISNINGAR
PLAN - RIVNING
TAKPLAN - RIVNING
PLAN - ÖVERSIKT, BRAND
FASADER

A-40-1-100-R
A-41-1-001-R
A-40-1-100
A-40-3-001


FÖRKLARINGAR

- 1 BEFINTLIG GRÅ PUTS RIVS
- 2 BEFINTLIG MÅLAD SPONTAD TRÄPANEL RIVS
- 3 BEFINTLIGA LÄTTMETALLPARTI RIVS
- 4 BEFINTLIGA PORTAR RIVS
- 5 BEFINTLIG LUCKA TILL KALLVIND RIVS
- 6 BEFINTLIG VENTKANAL RIVS AV VENT
- 7 BEFINTLIG VENT. GALLER RIVS AV VENT
- 8 BEFINTLIGA STUPRÖR RIVS
- 9 BEFINTLIG HÄNGRÄNNA RIVS
- 10 BEFINTLIGT PLÅTTAK RIVS
- 11 BEFINTLIG FASADSTEGE, TAKSTEGE RIVS
- 12 BEFINTLIG TEGELSKORSSTEN RIVS
- 13 BEFINTLIGA TAKLUFTNING RIVS
- 14 BEFINTLIGT SNÖRASSKYDD RIVS
- 15 SKYLTT DEMONTERAS OCH ÅTERMONTERAS
- 16 BEFINTLIG BRANDPOST, KYLA RIVS AV RÖR
- 17 BEFINTLIG VENTGENOMFÖRING INKL. FLÄKT/HUV RIVS AV VENT


GENERELLT:
HÄNGRÄNNOR OCH STUPRÖR
FÖNSTER OCH DÖRRAR I FASAD INKL. PLÅTAR,
VENTILATIONSGALLER, BEFINTLIGA VINDSKIVOR, PLÅTAR
PÅ TAK ETC. RIVS

BYGGNAD SOM RIVS
SE RITNINGAR GYMNASIESKOLA DATERADE
1994 OCH MILJÖINVENTERING DATERAD 2022


BYGGNADSDDEL SOM RIVS

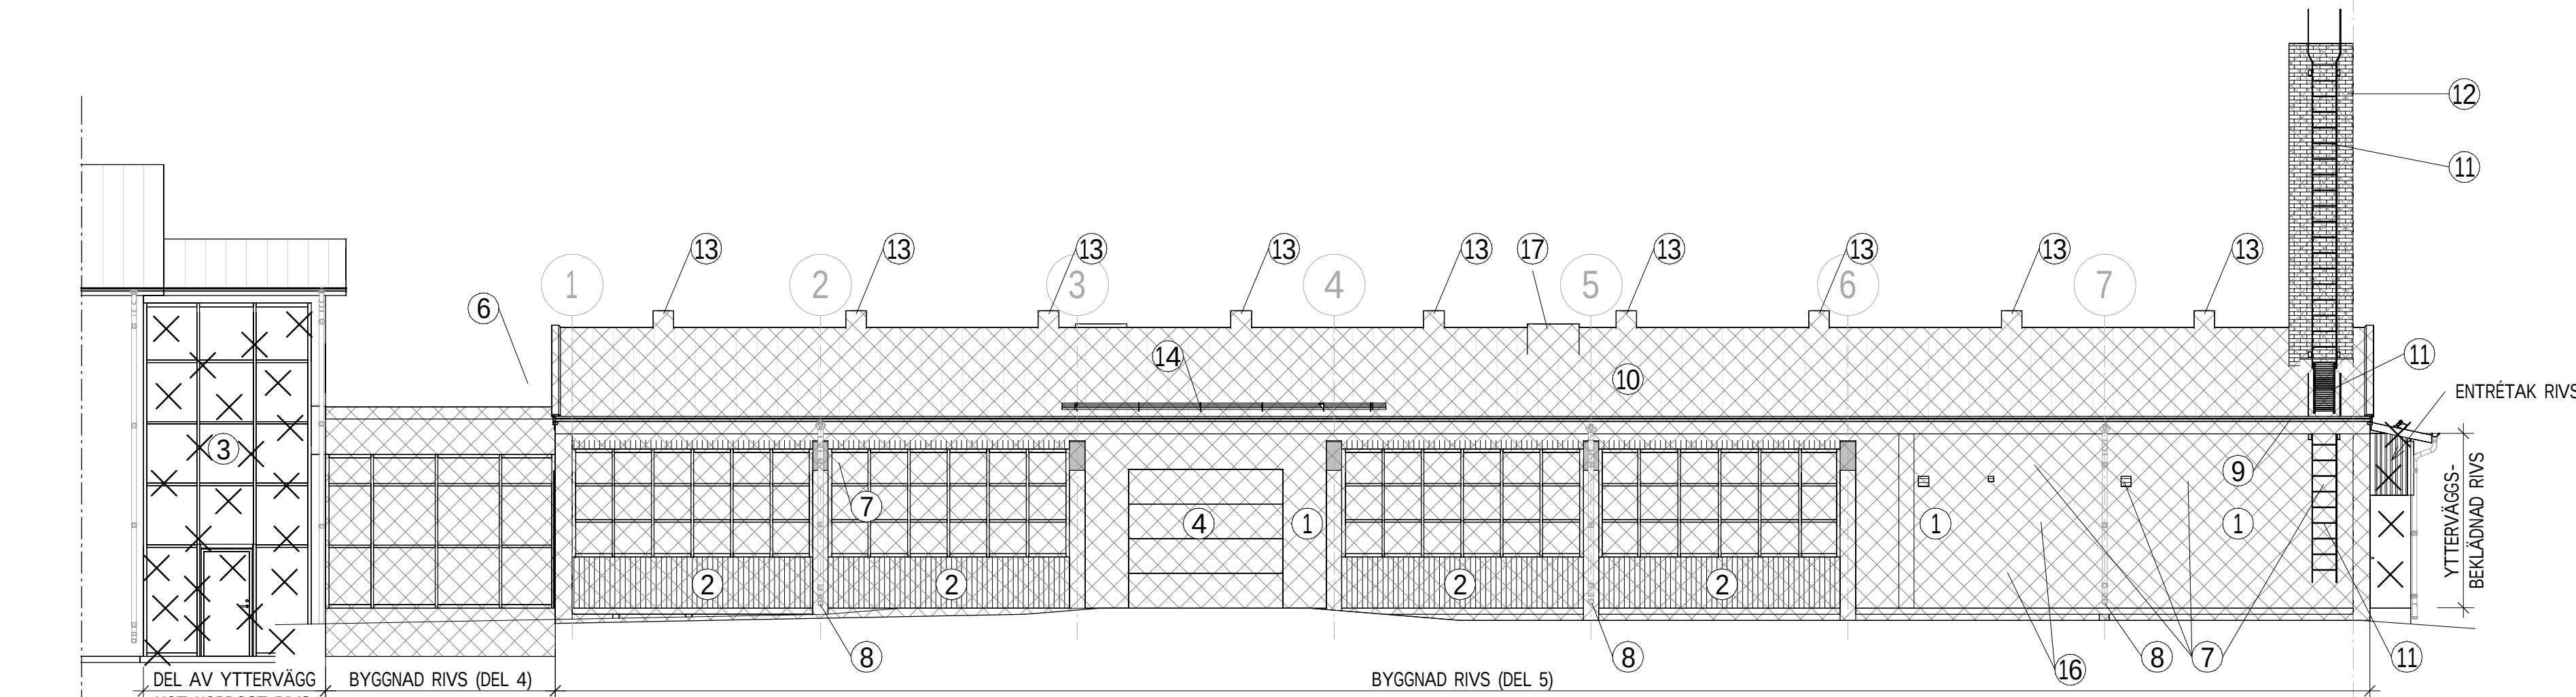


FASAD MOT NORDÖST - RIVNING

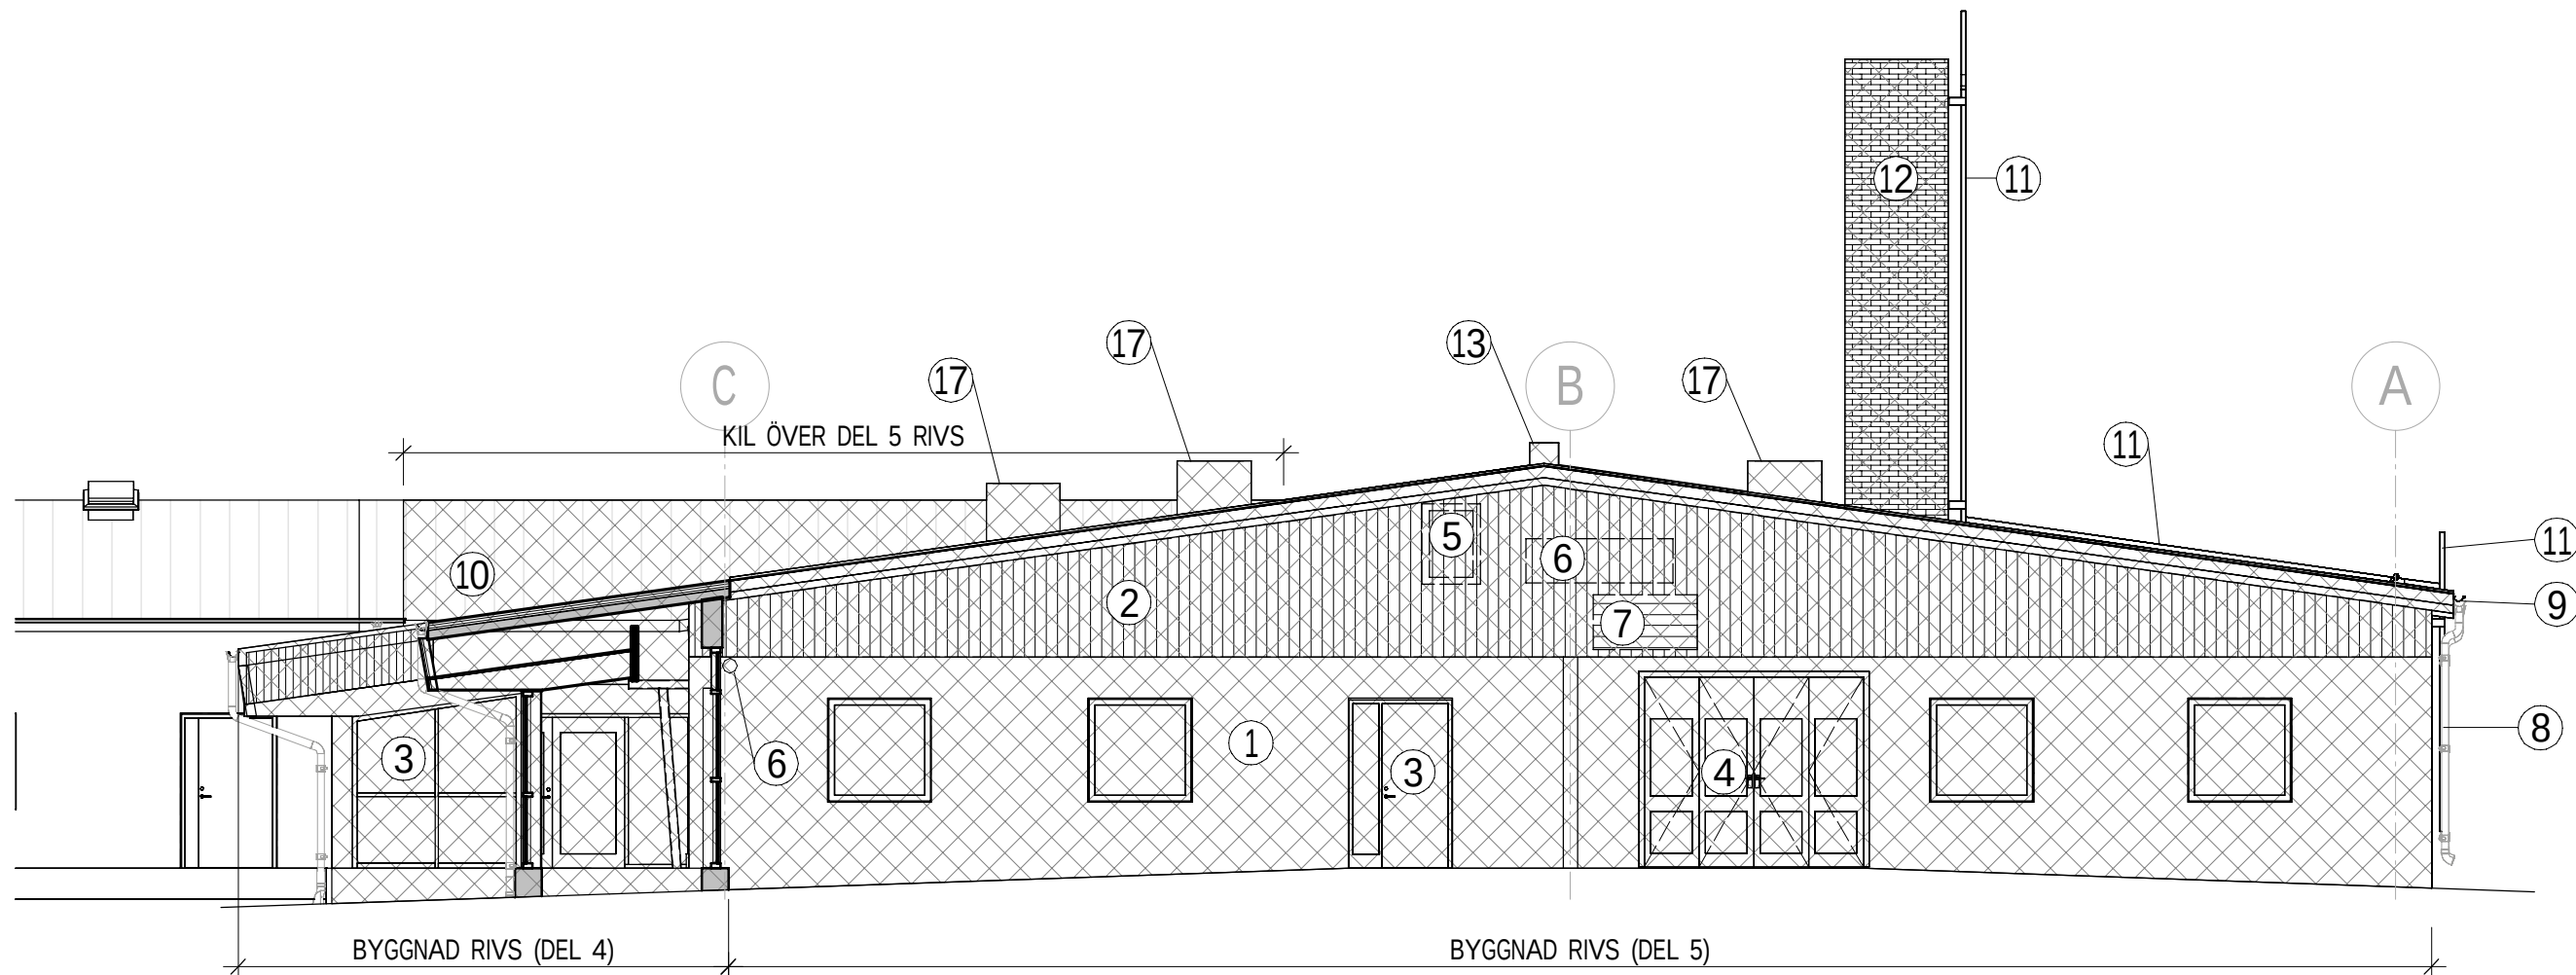

FASAD MOT SYDÖST - RIVNING

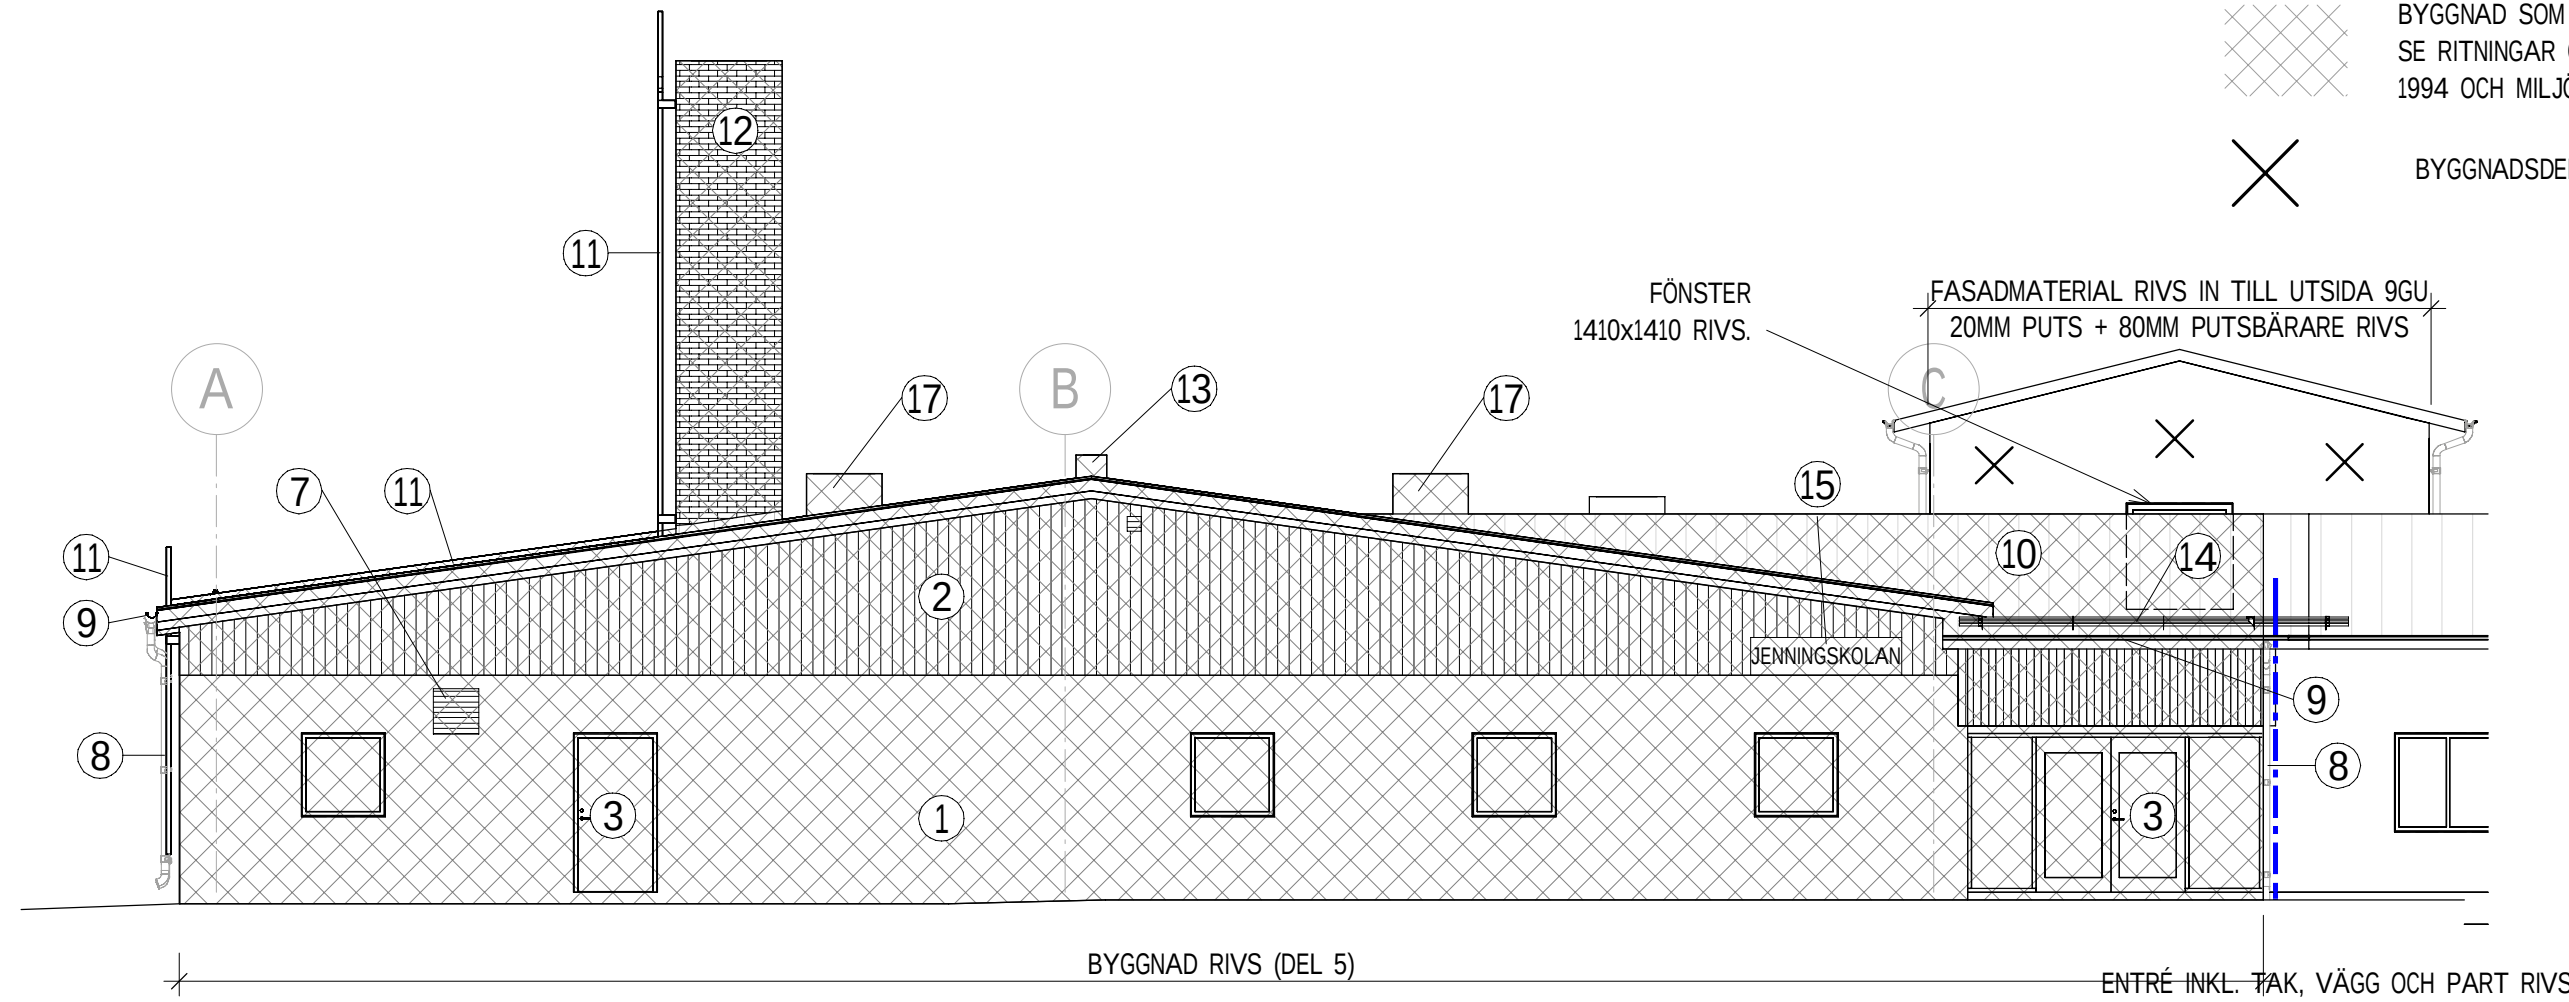


FASAD MOT NORDVÄST - RIVNING

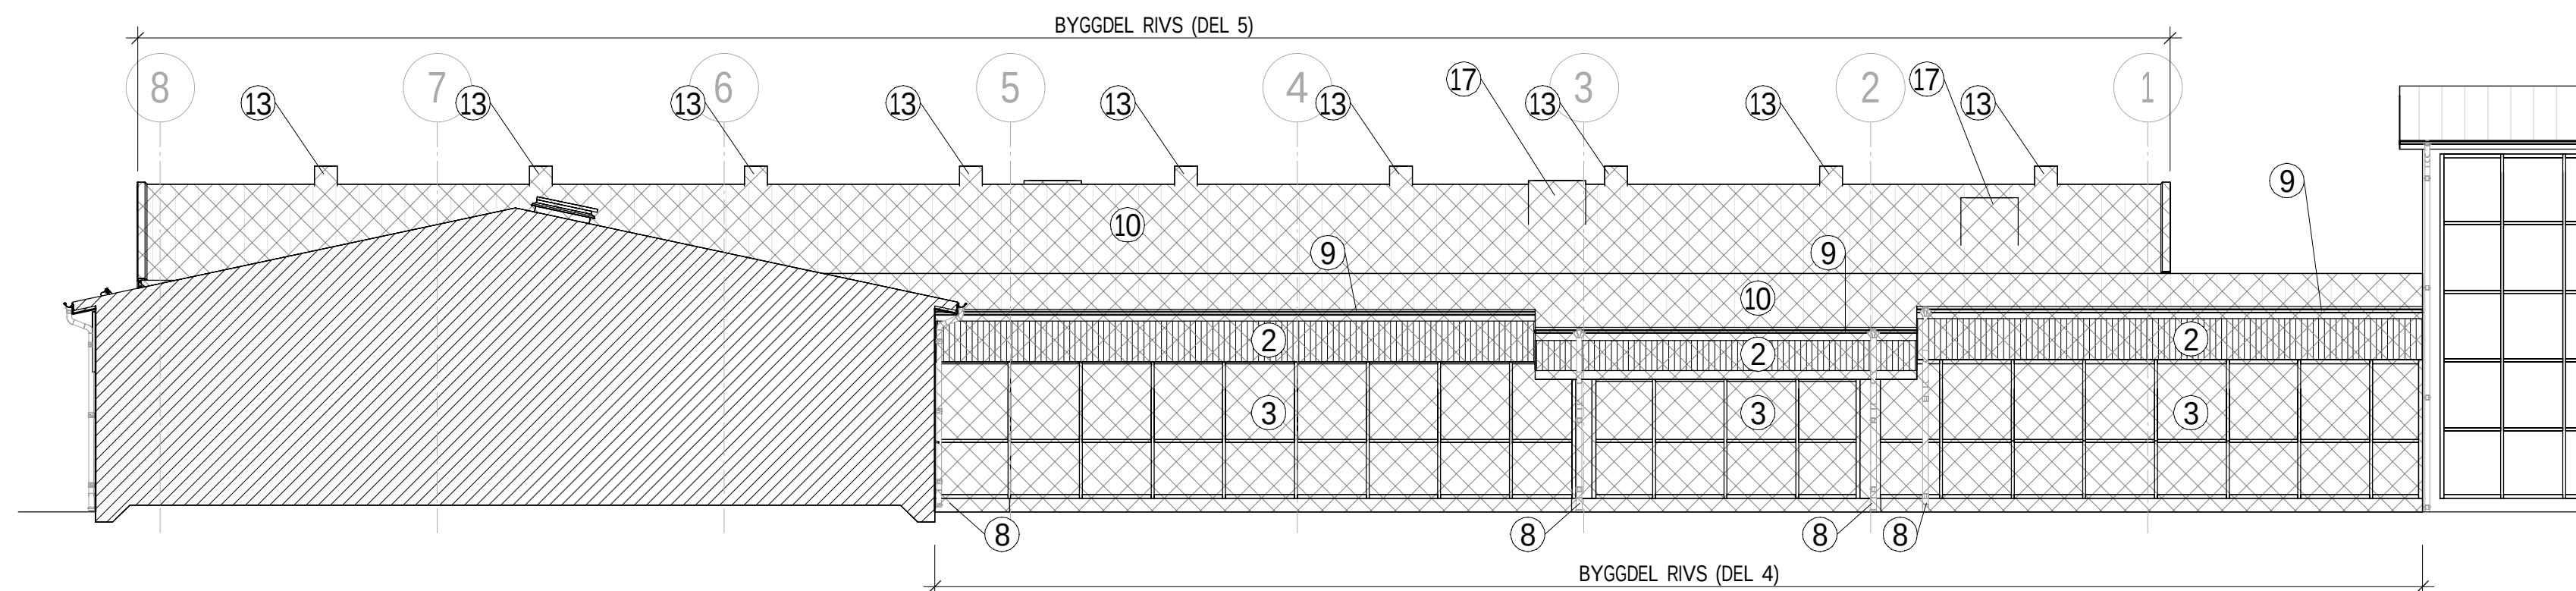

FASAD MOT SYDVÄST - RIVNING

SKALA 1:100 0 1 10 METER

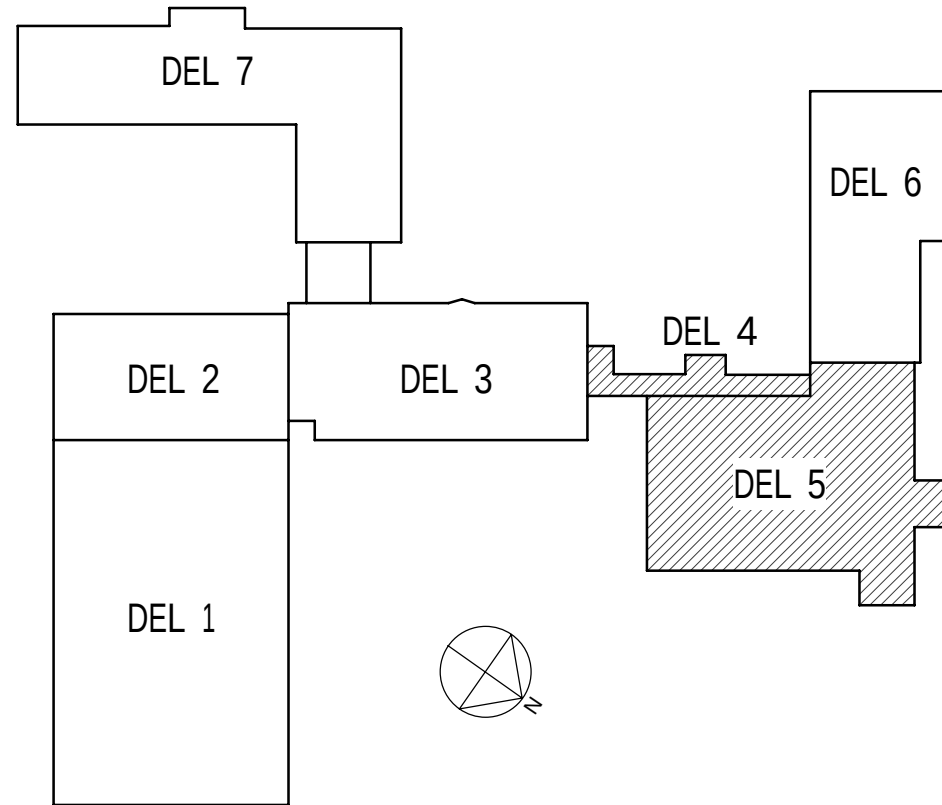

STATUS		
FÖRFRÅGNINGSUNDERLAG		
HANDLING		
BYGGHANDLING		
DATUM	2024-12-20	ANSÖKAN AV
		T. BERGSTRÖM
ANSÖKAN AV		ADRESS PM
BESTÄLLARE		
 ROBERTSFORS KOMMUN		
PROJEKTNAMN		
CENTRALEKÖK		
OMFÄTTE		
ROBERTSFORS KOMMUN		
PROJEKTNUMMER	1088371	FASTIGHET
		FORDONET 1
DISCIPLIN	A	FÖRETAG
		NORCONSULT SVERIGE AB
UPPDRAGSNUMMER	1088371	SKAPAD AV
		MSR
TELEFON	010 141 80 00	KONTAKTPERSON
		TOMAS BERGSTRÖM
BYGGNADSTYP		FÖRSTÄD (BYG 2008)
VÄRNINGSPÅN	1	VÄRNINGSDEL
		DELOMRÅDE
SYSTEM		
40 SAMMANSATT REDOVISNING		
SPECIFIKATION		
FASADER		
RIVNING	1:100	FORMAT
		A1
DOKUMENTNUMMER	A-40-3-001-R	
	ÄNDRING	