




2024-12-20 11:46:32

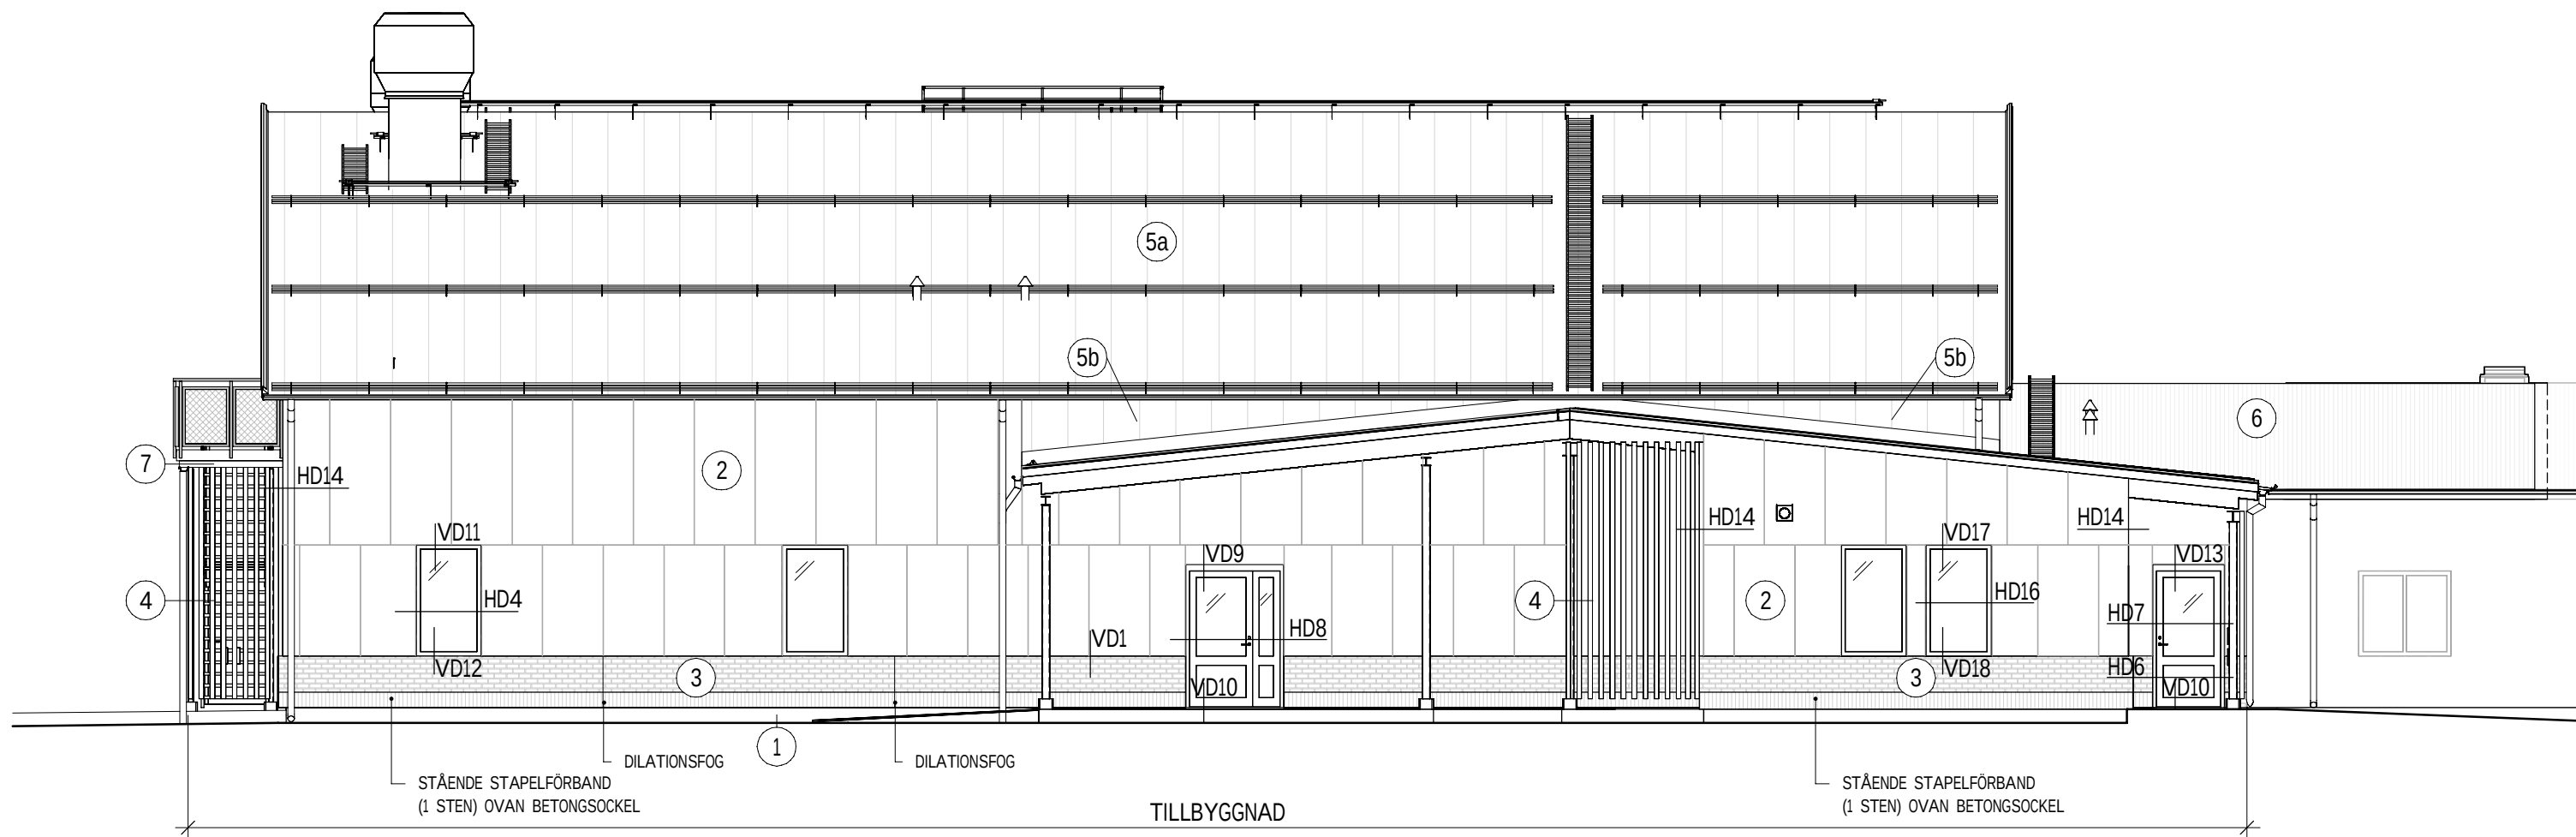


FASAD MOT NORDVÄST
1 : 100

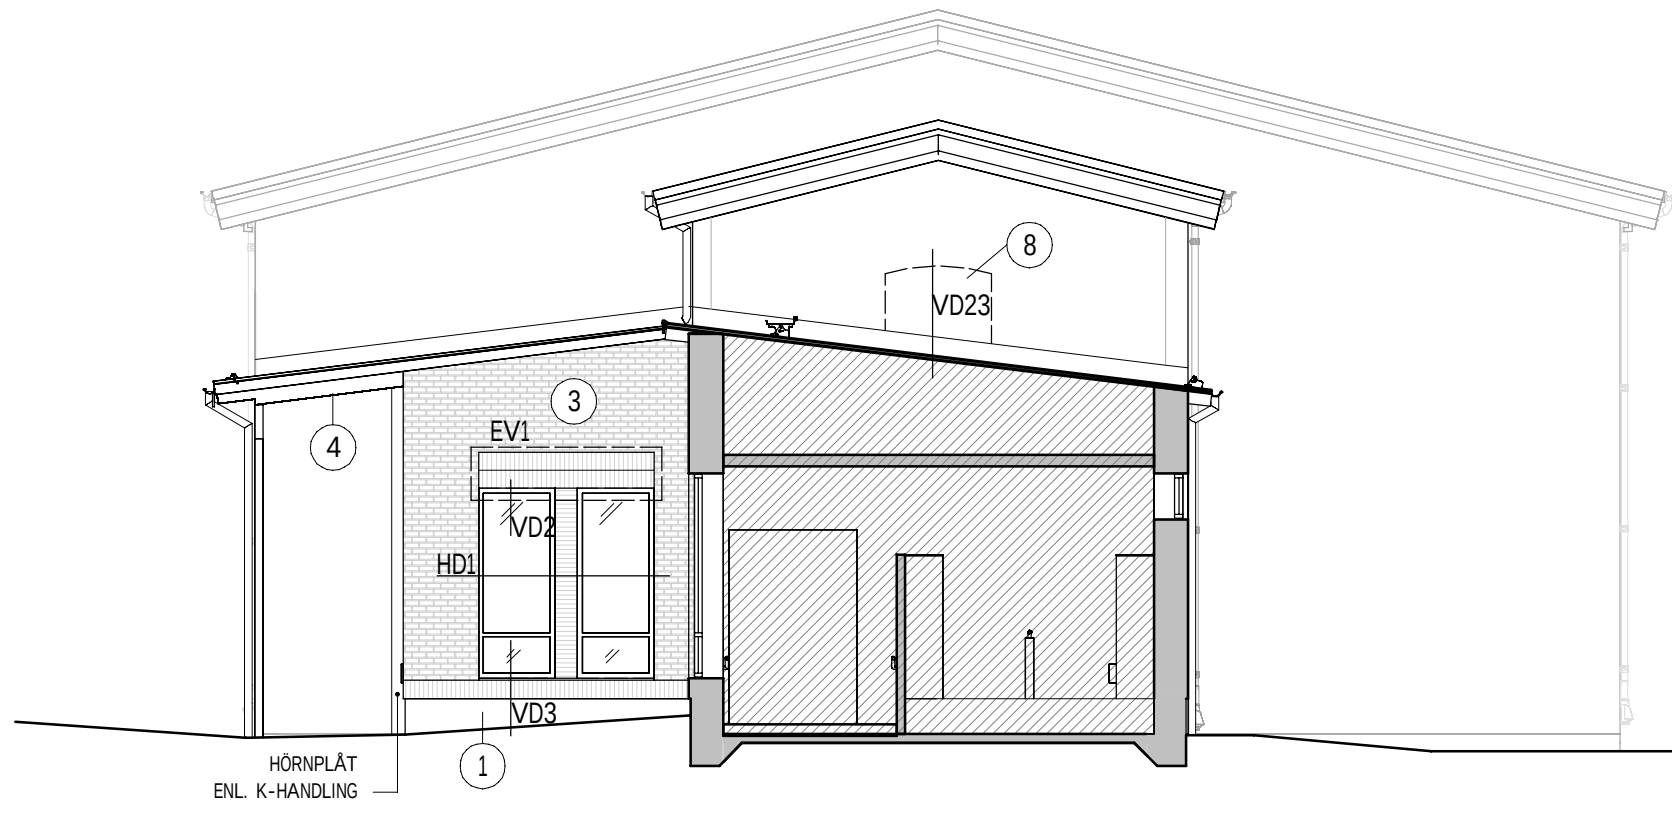


FASAD MOT NORDVÄST - ENTRÉ
1 : 100

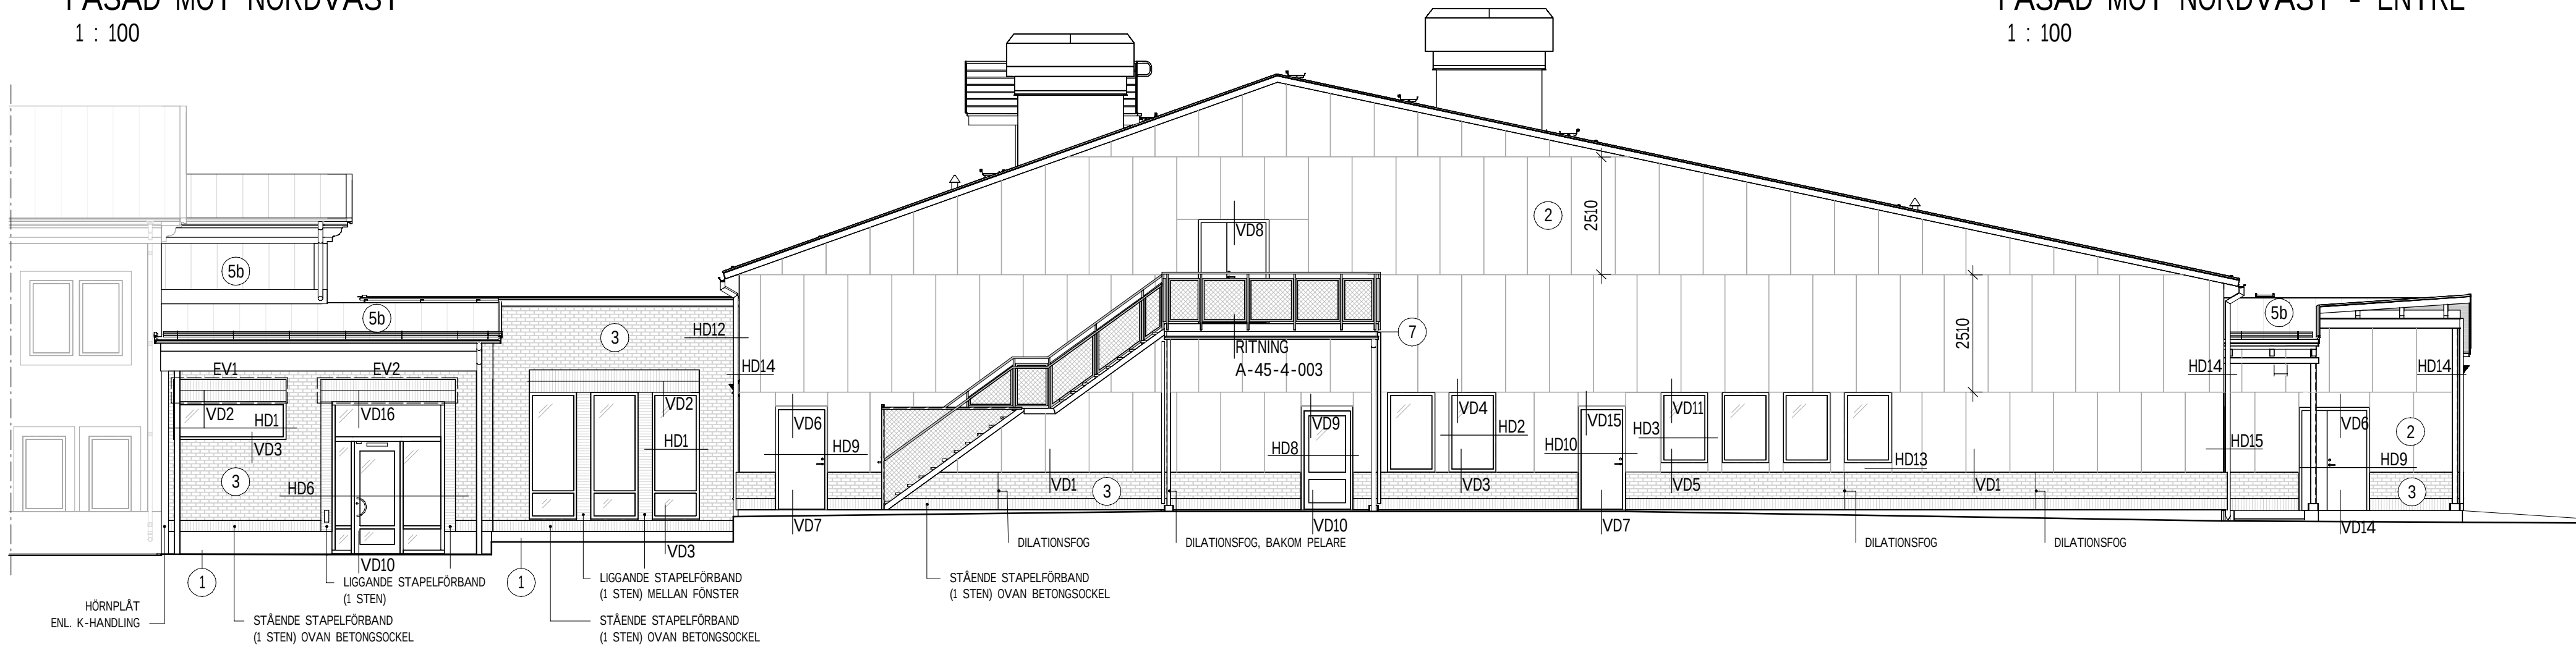

FASAD MOT NORDÖST
1 : 100

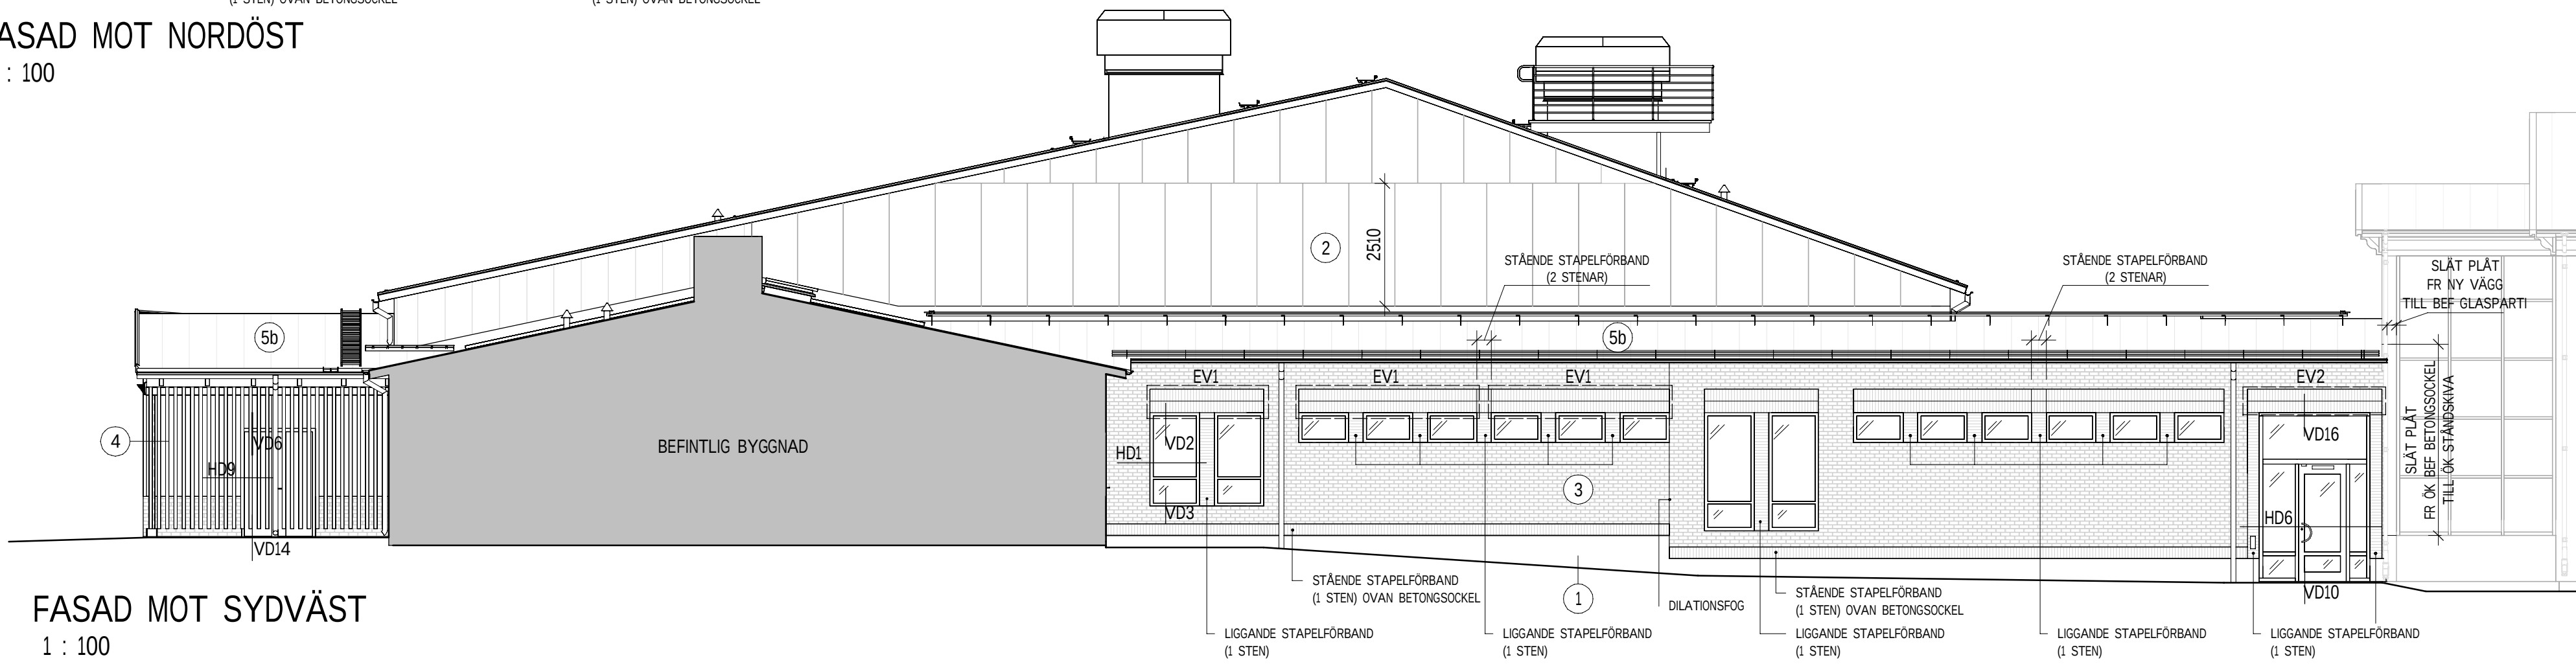

FASAD MOT SYDVÄST
1 : 100

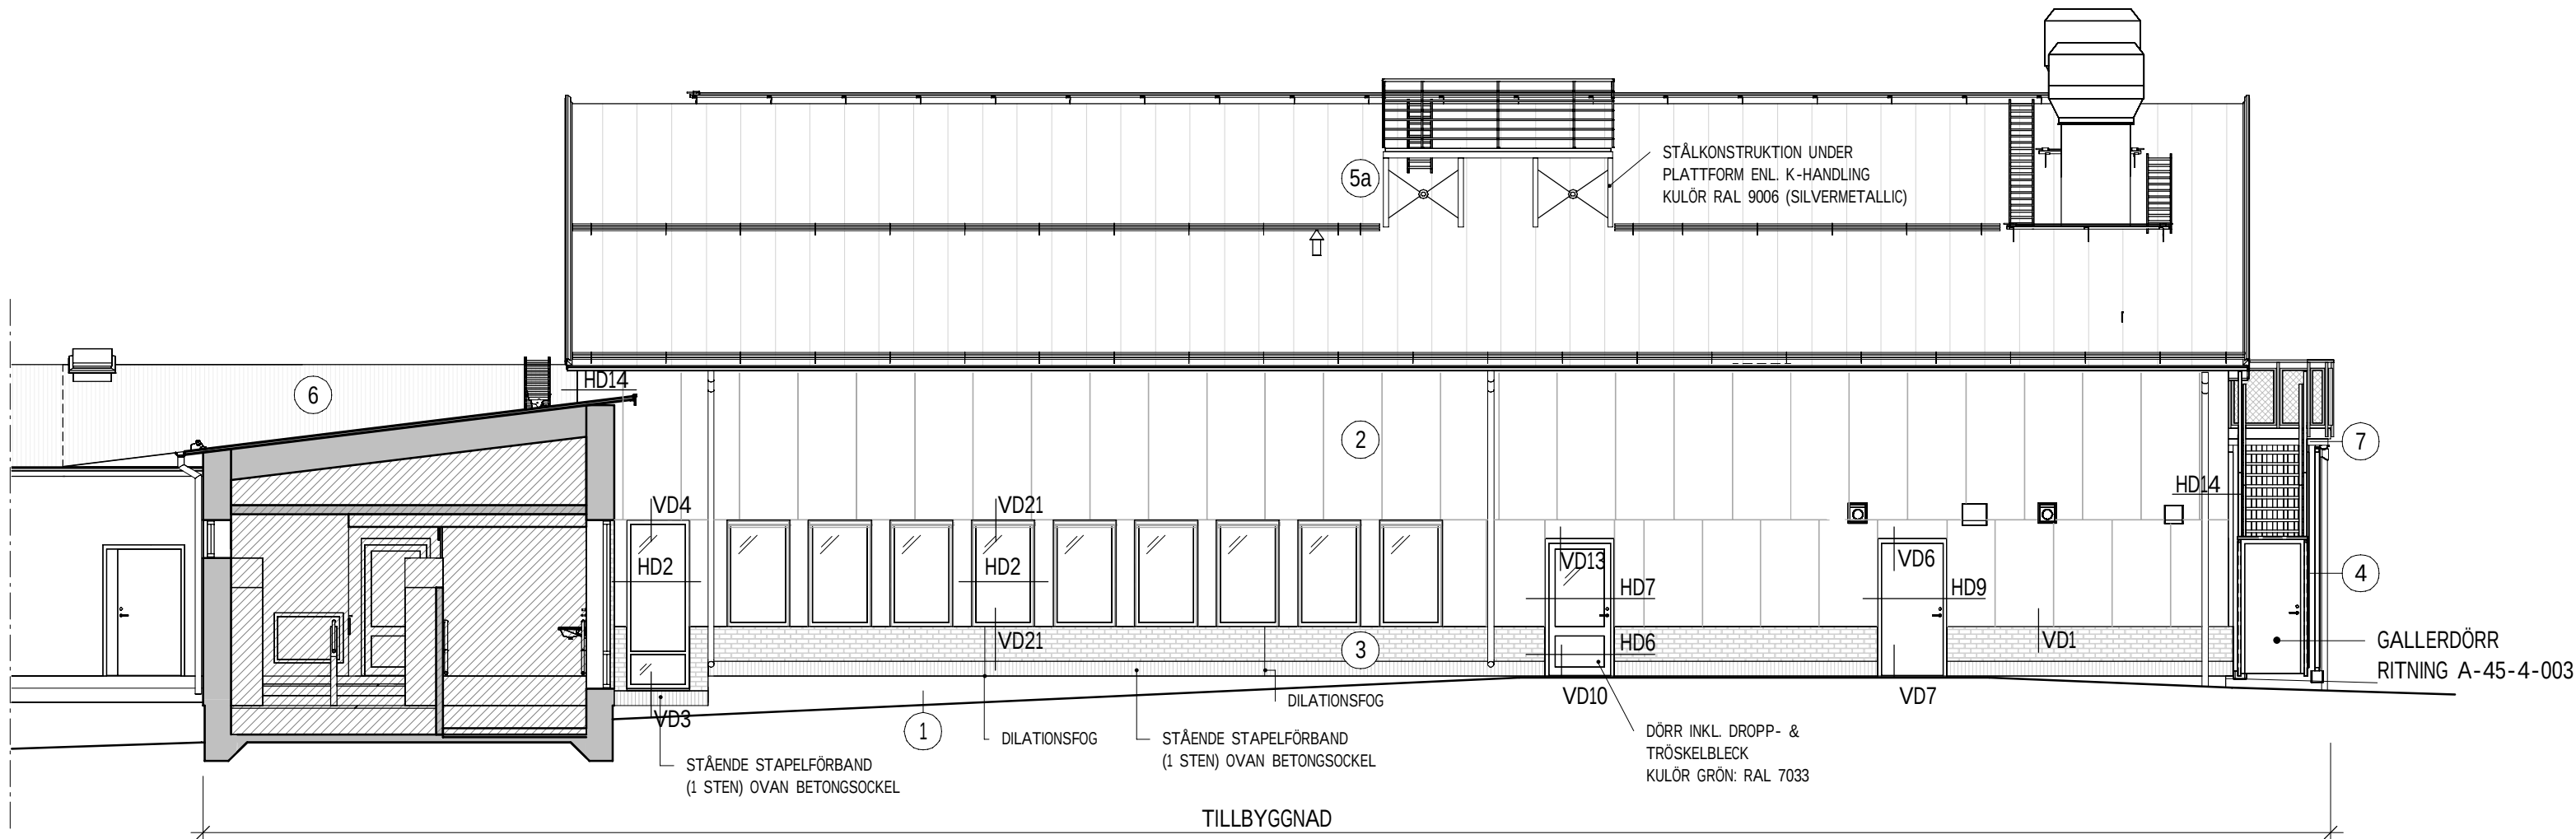

FASAD MOT SYDÖST
1 : 100

SKALA 1:100 0 1 10 METER

ÖVRIGT
DROPPBLECK, FÖNSTERBLECK, TRÖSKELBLECK, SOCKELBESLAG
KULÖR RAL 7044 (SILKESGRÅ) DÄR EJ ANNAT ANGES

HÄNGRÄNNA, STUPRÖR, VINDSKIVA, VINDSKIVELIST, FOTPLÅT,
TAKFOT, GAVELSPRÄNG I PLÅT, SAMT ÖVRIGA PLÅTINKLÄDNADER
KULÖR RAL 9006 (SILVERMETALLIC)

TAKSÄKERHET, STÄNDPLÅT, PLÅTVINKEL OCH
VENTILATIONSHUVAR
KULÖR RAL 9006 (SILVERMETALLIC)

HÖRNPLÅT ENL. K-HANDLING
KULÖR RAL 7044 (SILKESGRÅ)

SLÅT PLÅT PÅ PUTSFASAD
KULÖR VIT LIKA BEFINTLIG TAKFOT

FÖRKLARINGAR

MÅTT I MILLIMETER OCH PLUSHÖJDER I METER OM
INGET ANNAT ANGES.

FASAD & TAK

- 1 SOCKEL AV BETONG
- 2 FASADSKIVA, SWISSPEARL NOBILIS
KULÖR JADE 522 (NÄRMSTA NCS S 5005-G20Y)
FORMAT: 2510x930 mm, ANPASSAS MOT MÖNSTER
SKIVHÖJD 1a RADEN NERIFRÅN: ÖK TEGELSOCKEL TILL
ÖK FÖNSTER, ANPASSAS PÅ PLÅTS
- 3 TEGEL, RANDERS TEGEL RT 479 CORTINA
FÖGFÄRG: GRÅ/VIT
GENERELLT MURFÖRBAND: VILT FÖRBAND, DÄR EJ
ANNAT ANGES
- 4 SPALJÉ SAMT SYNIG TRÄKONSTRUKTION INKL.
SYNIG RÄSPONT MÅLAS
KULÖR NCS S 5005-G20Y (GRÖN)
- 5a PLÅTSKIVTÄCKNING, KULÖR RAL 9006 (SILVERMETALLIC)
- 5b PLÅTBANDTÄCKNING, KULÖR RAL 9006 (SILVERMETALLIC)
- 6 PLÅTTAK, KULÖR SVART LIKA BEF. NÄRLIGGANDE TAK
- 7 PLÅTINKLÄDNAD, KULÖR RAL 9006 (SILVERMETALLIC)
- 8 BEF. FÖNSTER 1410x1410 mm DEMONTERAS OCH SÄTTES
IGEN. HÅL ILAGAS ENL. DETALJ.

SYNLIGA STÅLPELARE & STÅLBALKAR
KULÖR RAL 7033 (DOVGRÖN), DÄR EJ ANNAT ANGES
GLANS 30

FÖNSTER
KULÖR RAL 7044 (SILKESGRÅ)


DÖRRAR MED GLAS
KULÖR RAL 7044 (SILKESGRÅ) DÄR EJ ANNAT ANGES

DÖRRAR TÄTA
KULÖR RAL 7033 (DOVGRÖN)

HÄNVISNINGAR

YTTERVÄGSGDETALJER A-42-6-001 -- 004

UTVÄNDIG TRAPPA A-45-4-003
RAMP, LEJDARE A-45-4-005

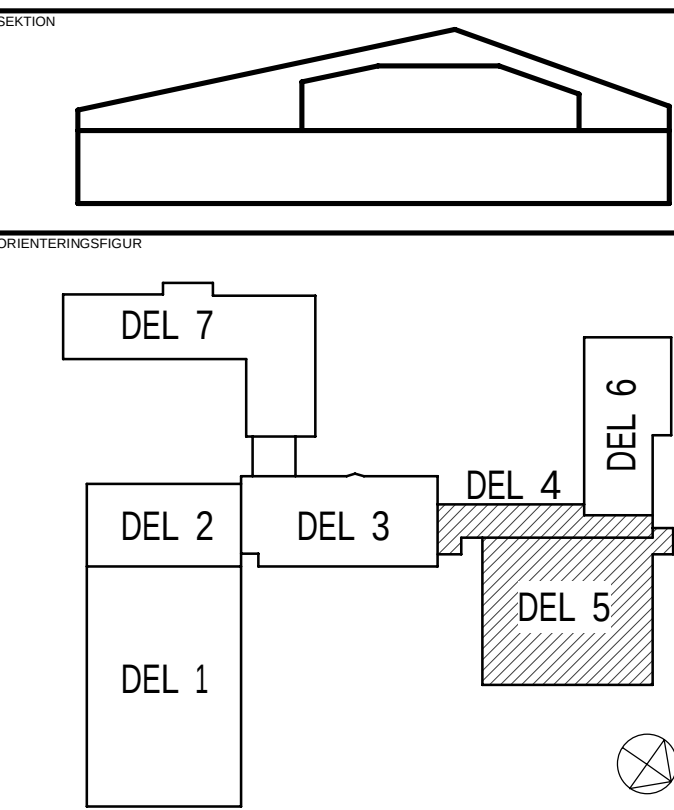

STATUS
FÖRFRÅGNINGSUNDERLAG

HANDLING
BYGGHANDLING

DATUM 2024-12-20 FÖRBERED AV T. BERGSTRÖM



PROJEKTNAMN
CENTRAKKÖK

OMRÅDE
ROBERTSFORS KOMMUN

PROJEKTNUMMER
YTTRE RINGVÄGEN 4

DIARIENUMMER
FORDONET 1

DISCIPLIN
NORCONSULT SVERIGE AB

UPPRAGSGRUPP
108 83 71

TELEFON
010 141 80 00

BYGGNADSTYP
KONTAKTPERSON
TOMAS BERGSTRÖM

VÄRNINGSPÅN
VÄRNINGSDIREKTÖR
DELOMRÅDE

SYSTEM
40 SAMMANSATT REDOVISNING

SPECIFIKATION
FASADER - ÖVERSIKT

SKALA 1:100

FORMAT A1

DOCUMENTNUMMER
A-40-3-001

FILENAMN: C:\Norconsult\Autodesk\Revit\1088371-Centralkök Robertsfors_Centralfil-2024_maista.rvt