


2024-12-18 16:07:36

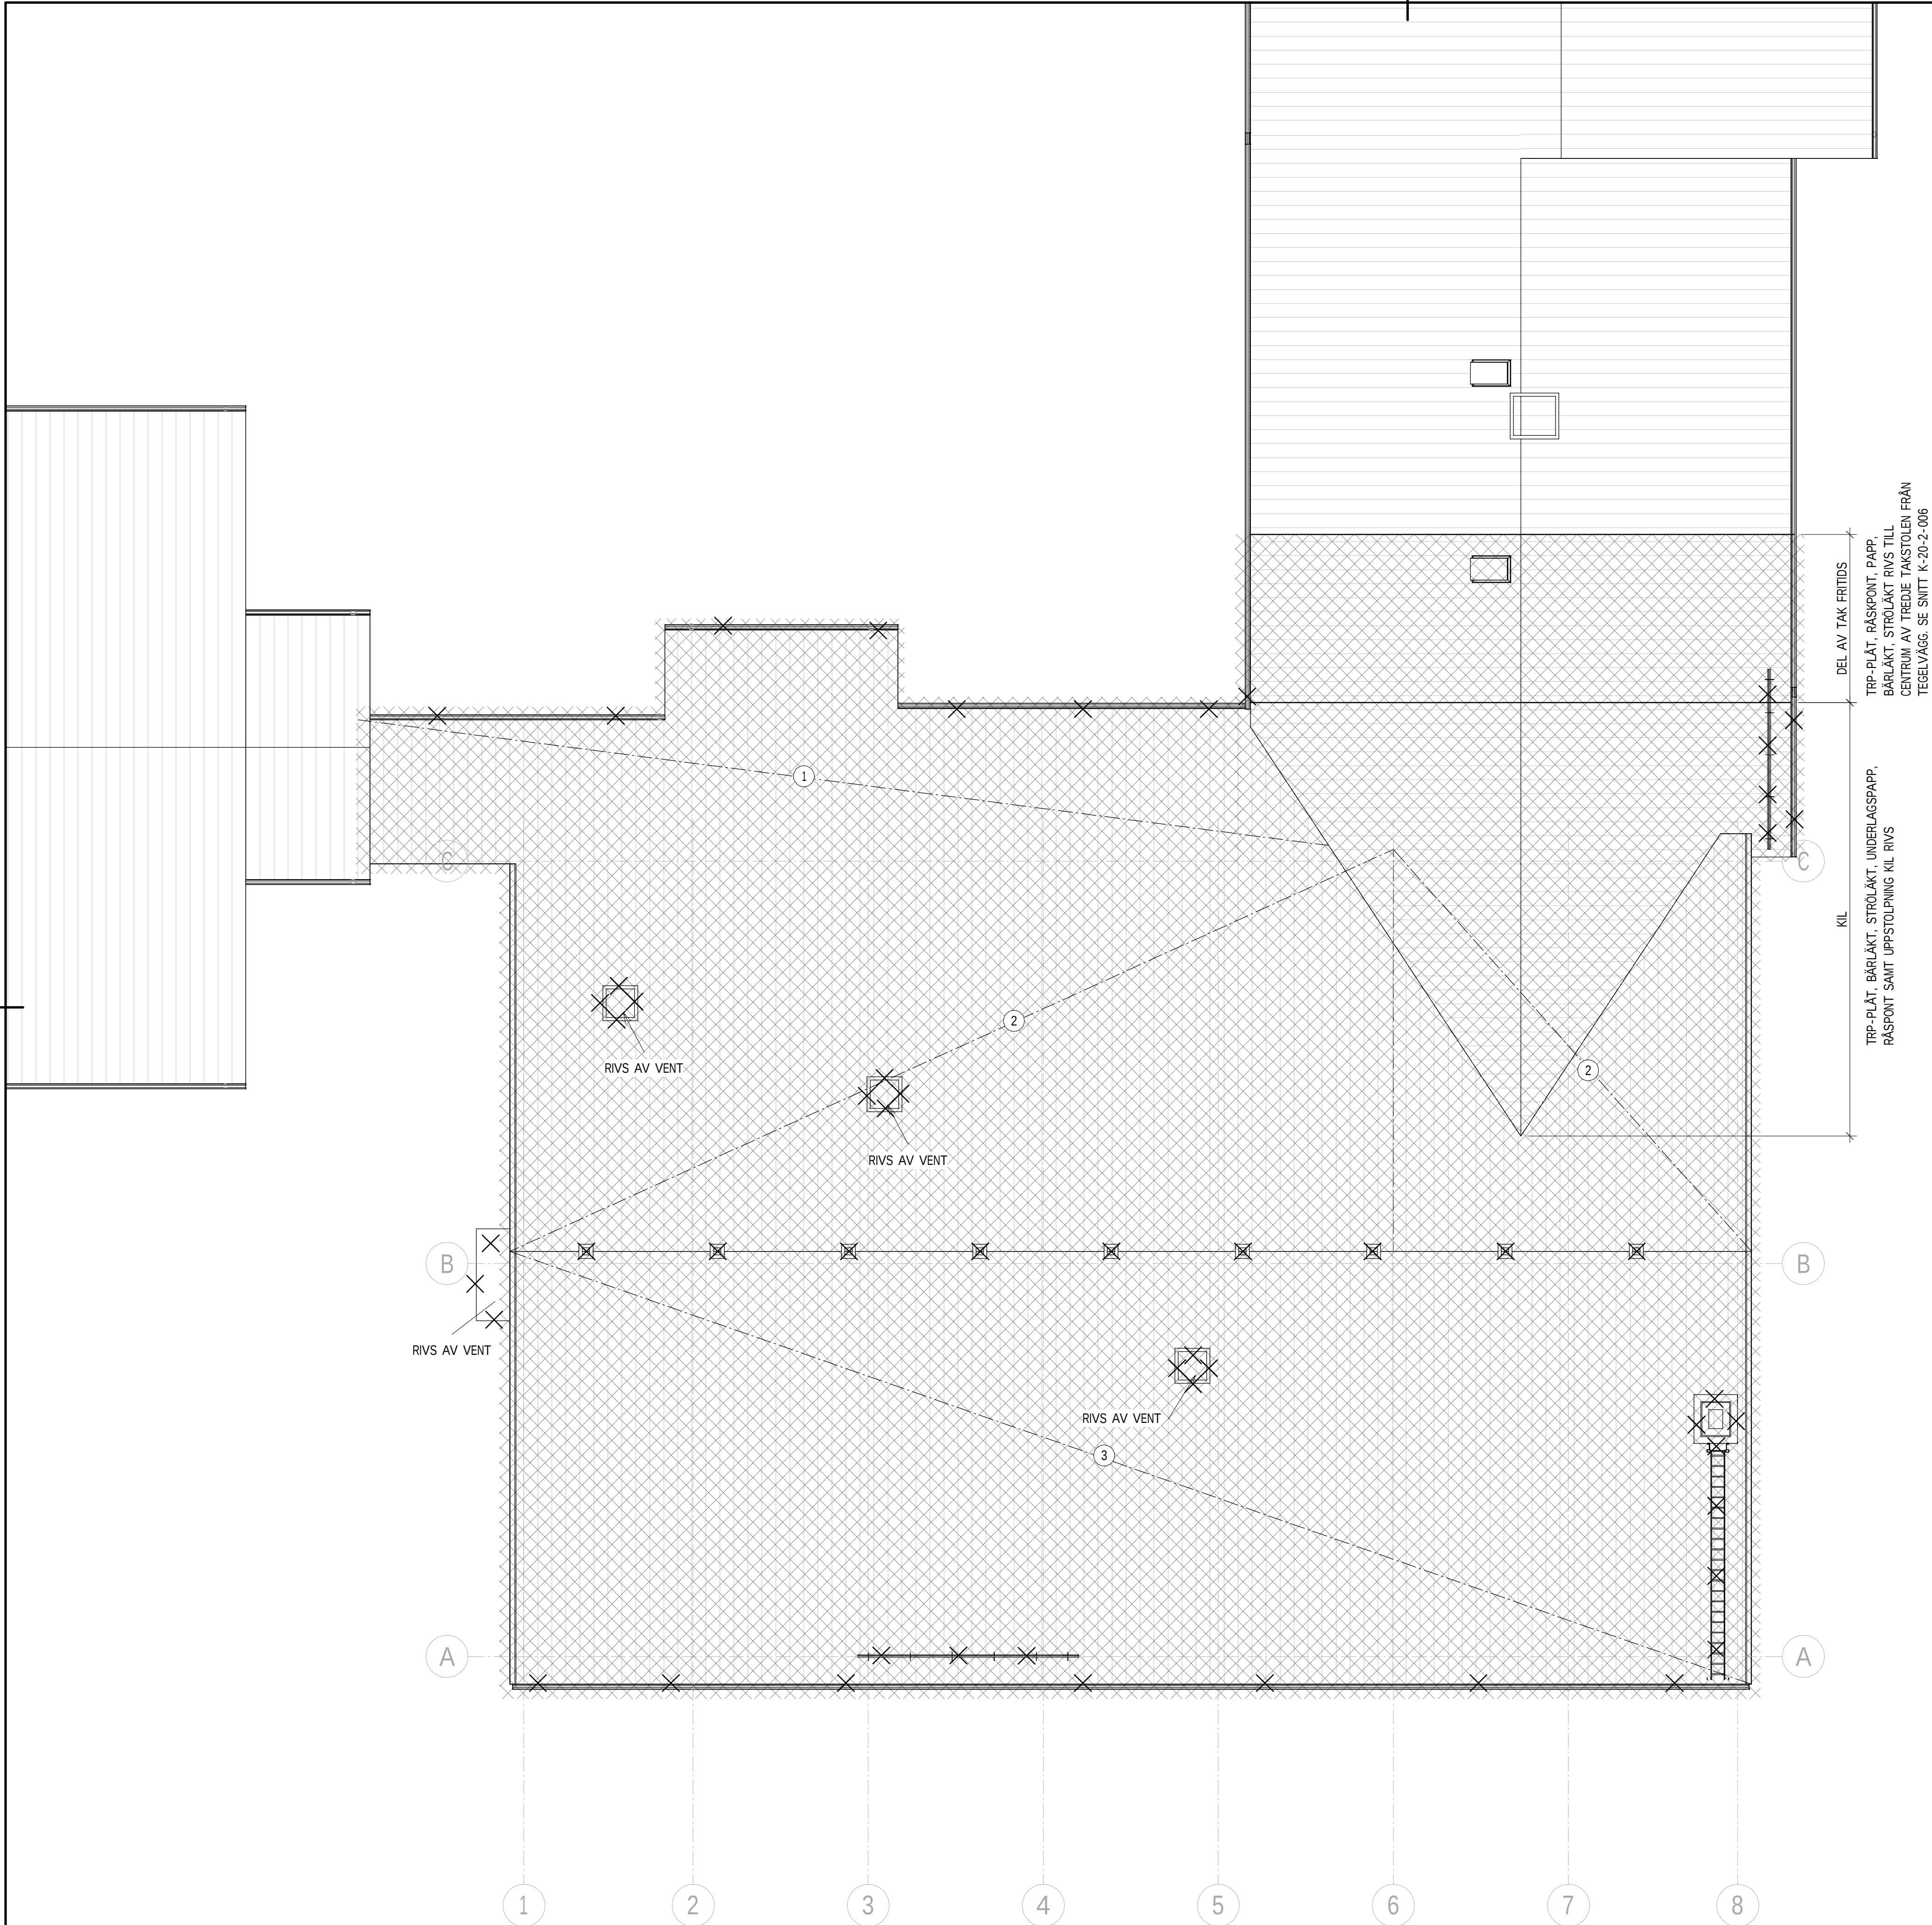

FÖRKLARINGAR

BYGGNAD SOM RIVS
SE RITNINGAR GYMNASIESKOLA DATERADE
1994 OCH MILJÖINVENTERING DATERAD 2022


BYGGNADSDDEL SOM RIVS

- UPPSTOLPAT TAK PÅ BALKAR AV LIMTRÄ, RÅSPONT, UNDERLAGSPAPP SAMT PROFILERAD PLÅT RIVS.
- 240mm LÄTTBETONGPLANK, UPPSTOLPAT TAK, 240mm LÖSULL & 160mm ISOLERSKIVOR, LÅKT, 4,5 MASONITE KONDENSSKYDD SAMT PROFILERAD PLÅT RIVS.
- UPPSTOPLAT TAK 45x145 REGLAR + 145 ISOLERING PÅ LÄTTBETONGPLANK, 45x200 s600 INKL. INFÄSTNINGAR, 200 PAPPKLÄDD MINERALULLSKIVA, 23 RÅSPONT, PAPP SAMT PROFILERAD PLÅT TYP PLANNJA 40 RIVS.

HÄNVISNINGAR

FASADER - BEFINTLIGA FÖRHÅLLANDEN
PLAN - OMBYGGNAD
FASADER - OMBYGGNAD

A-04-3-501
A-40-1-501
A-40-3-501

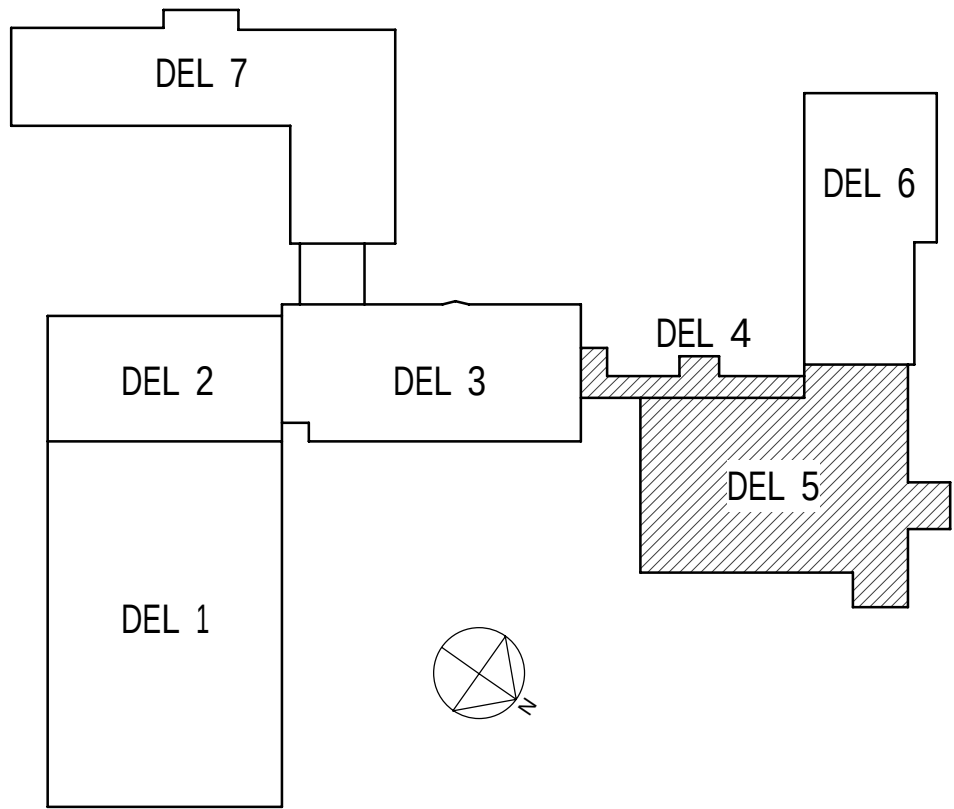

STATUS		
FÖRFRÅGNINGSUNDERLAG		
HANDLING		
BYGGHANDLING		
DATUM	ÖVERSKICK AV	ADRESSER PM
2024-12-20	T. BERGSTRÖM	
BESTÄLLARE		
	ROBERTSFORS KOMMUN	
PROJEKTNAMN		
CENTRALEKÖK		
OMRÅDE		
ROBERTSFORS KOMMUN		
PROJEKTNUMMER	ADRESS	
	YTTRE RINGVÄGEN 4	
DIARIENUMMER	FASTIGHET	
	FORDONET 1	
DISCIPLIN	FÖRETAG	
A	NORCONSULT SVERIGE AB	
UPPDRAGSNUMMER	SKAPAD AV	
1088371	MSR	
TELEFON	KONTAKTPERSON	
010 141 80 00	TOMAS BERGSTRÖM	
BYGGNADSTYP	FÖRSTÄD (RH 2008)	
VÄRINGSPLAN	VÄRINGSDEL	DELOMRÅDE
SYSTEM		
41 YTTERTAK OCH YTTREBJÄLKLÄG		
SPECIFIKATION		
TAKPLAN		
RITNINGSKATEGORI	SKALA	FORMAT
RIVNING	1:100	A1
DOKUMENTNUMMER	ÄNDRING	
A-41-1-001-R		

FILENAMN: N:\1088371\Arbetsmaterial\02 BIM\A3D_Model\Rivningsmodell-2024.rvt