




2024-12-20 10:35:30

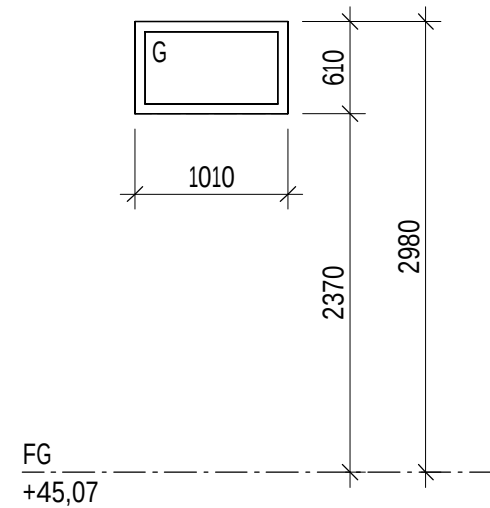


F10a Antal: Enl. tabell
1 Utvändigt fast fönsterparti
2 3-glas isolerruta

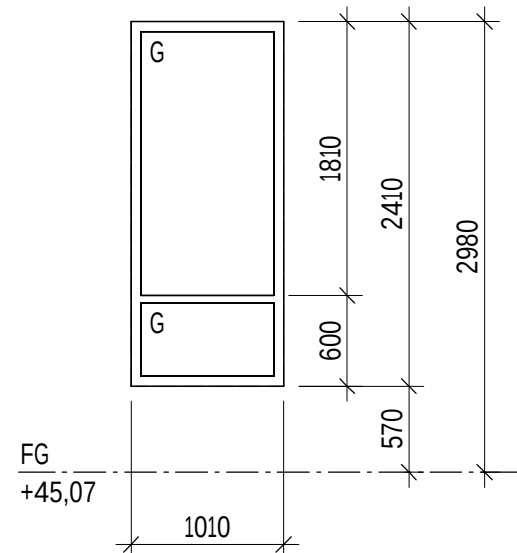

F10b Antal: Enl. tabell
1 Utvändigt fast fönsterparti
2 3-glas isolerruta

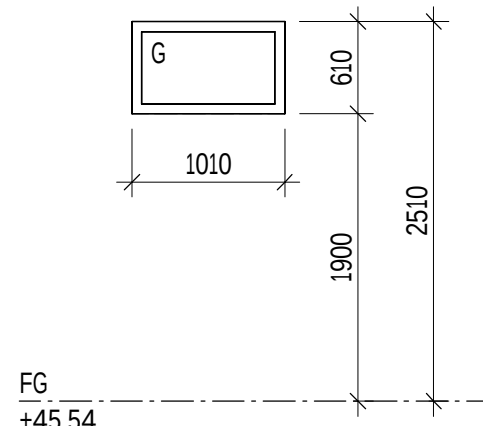


F10c Antal: Enl. tabell
1 Utvändigt fast fönsterparti
2 3-glas isolerruta

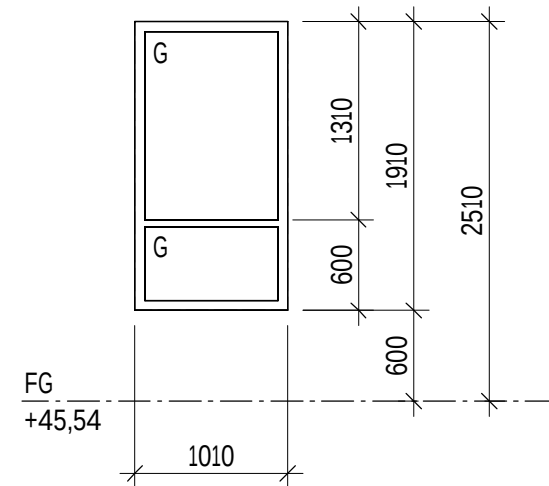


F10d Antal: Enl. tabell
1 Utvändigt fast fönsterparti
2 3-glas isolerruta


F10e Antal: Enl. tabell
1 Utvändigt fast fönsterparti
Brandklass E30
2 3-glas isolerruta

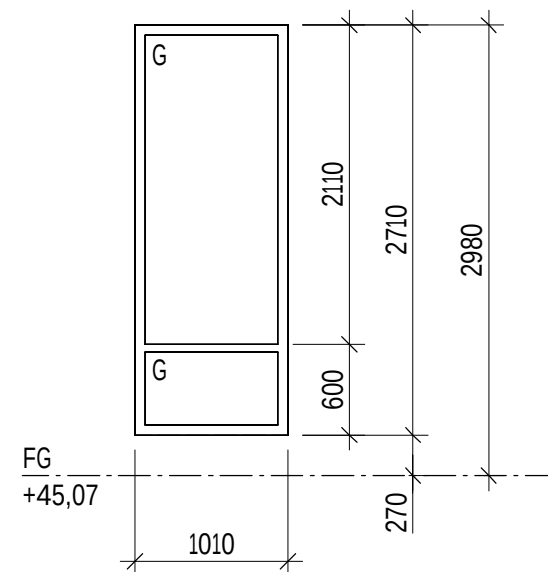


F10f Antal: Enl. tabell
1 Utvändigt fast fönsterparti
2 3-glas isolerruta

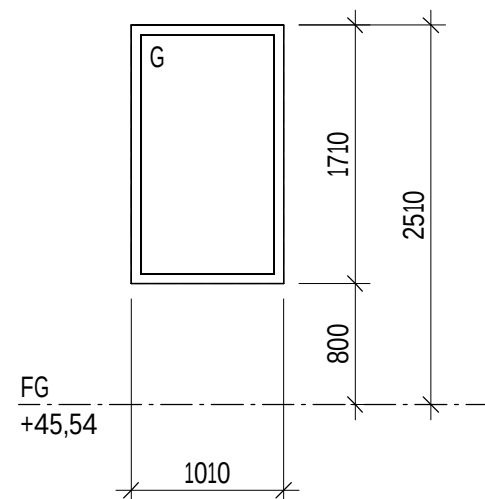


F10g Antal: Enl. tabell
1 Utvändigt fast fönsterparti
2 3-glas isolerruta
25 Yttre solavskärmning i form av vertikalkarmis enl. beskrivning.
Solavskärmning monteras på fönstertyp markerad med * bakom littrat (F10g*).
Se delplaner för antal.

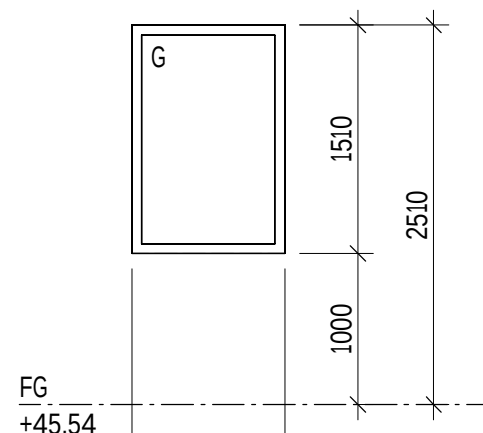

F10h Antal: Enl. tabell
1 Utvändigt fast fönsterparti
2 3-glas isolerruta

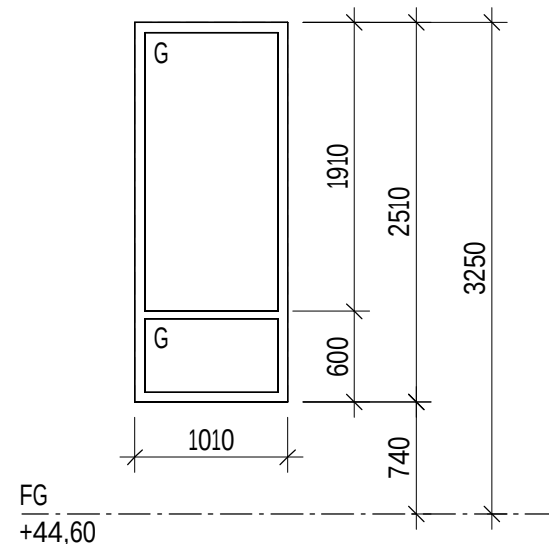

F10i Antal: Enl. tabell
1 Utvändigt fast fönsterparti
2 3-glas isolerruta

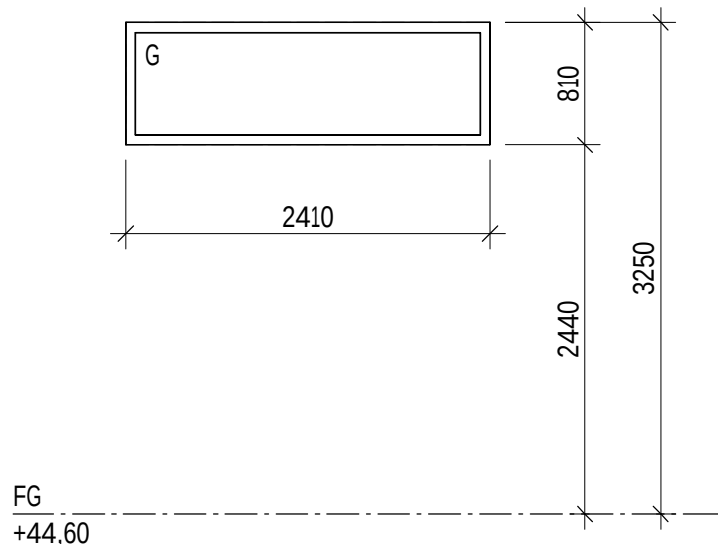

F24a Antal: Enl. tabell
1 Utvändigt fast fönsterparti
2 3-glas isolerruta

FÖNSTER ANTAL			
FÖNSTERTYP	ANTAL	BREDD [mm]	HÖJD [mm]
F10a	6	1010	610
F10b	2	1010	2410
F10c	6	1010	610
F10d	1	1010	1910
F10e	1	1010	1910
F10f	4	1010	2710
F10g	15	1010	1710
F10h	4	1010	1510
F10i	2	1010	2510
F24a	1	2410	810
Grand total	42		

SKALA 1:50 0 1 5 METER

FÖRKLARINGAR

G = Glas
Fönster och fönsterdörrar ses från utsidan.
Hängning anges från gångjärnssidan.
Antal beslag anges per bäge.
Alla mått i millimeter.
Mått avser väggöppningsmått, där annat ej anges.
Karmar märkes enligt ritningens litrering.
Brand och ljudklassade fönster och dörrar märkes enligt gällande normer.

OBS! Mått skall kontrolleras på plats före tillverkning.

KANTNUMMER ÄNGER:

- 1 =Sort/typ
- 2 =Glas
- 21 =Stängningsbeslag
- 22 =Handtag
- 23 =Uppställningsbeslag
- 24 =Låsning
- 25 =Övrigt

FÖRESKRIFTER

SORT/TYP

Utvändiga fönster av Aluminium med 3-glas isolerruta.
Fabrikat Schüco typ AWS 75.SI. eller likv.
Ev. brand, ljudklass och säkerhetsklass enl. resp. littera.

PROFILER

Profiltyp dimensioneras av leverantören utifrån kravspec. för resp. littera.

KARMDIMENSION

Enligt fabr. standard.

VÄRMEISOLERING

U-värde 1,1 W/m²K

PRODUKTSTANDARD, FUNKTIONSEGENSKAPER

Enl. SS-EN 14351-1:2006+A2:2016.

GLAS

Flytglas enligt SS-EN 572-2:2012.
Montage enligt MTK's anvisningar.
Alla luftspalter i förseglade rutor skall vara fyllda med argongas.
Glasytor skall uppfylla kraven för personsäkerhet enligt BBR 8:351, 8:353

YTBEHANDLING/KULÖR

Fönster lackeras i:
Kulör utsida: RAL 7044
Kulör insida: NCS S 0500-N


INFÄSTNING

Ingående beslag, synliga skruvar och infästningselement skall vara av rostfri syrafast kvalitet i klass A4. Ej synliga skruvar och infästningsbeslag i rostfri kvalitet klass A2. Övriga beslag enligt Schücos standard.
Fönstren skall förses med dolda gångjärn typ Schüco Avantec för inåtgående sido/underkantshängda fönster.

Anslutningsdetaljer, plåtklädnings och infästningar skall ingå i glasentreprenaden och vara lackade i samma kulör som fönsterpartierna.

HÄNVISNINGAR

PLAN 1 - ÖVERSIKT, BRAND A-40-1-100
DELPLANER A-40-1-141 -- 154

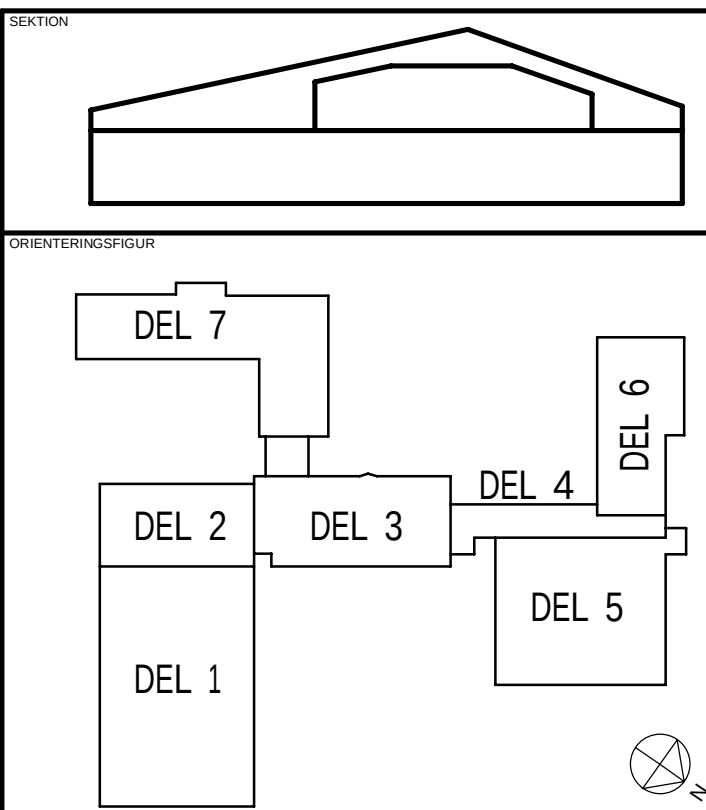

STATUS		
FÖRFRÅGNINGSUNDERLAG		
HANDLING		
BYGGHANDLING		
DATUM	ÖVERSKICK AV	ÄNDRINGAR PM
2024-12-20	T. BERGSTRÖM	
BESTÄLLARE		
 ROBERTSFORS KOMMUN		
PROJEKTNAMN		
CENTRALKÖK		
OMFÄTTE		
ROBERTSFORS KOMMUN		
PROJEKTNUMMER	FÄRHUS	
DIARIENUMMER	YTTRE RINGVÄGEN 4	
DISCIPLIN	FÖRETAG	
A	NORCONSULT SVERIGE AB	
UPPDRAGSRUMMER	SKAPAD AV	
108 83 71	MSR	
TELEFON	KONTAKTPERSON	
010 141 80 00	TOMAS BERGSTRÖM	
BYGGNADSTYP	FLUSHOOD (VIT 2008)	
VÄNINGSPLAN	VÄNINGSDEL	DELOMRÅDE
SYSTEM		
42 YTTERVÄGG		
SPECIFIKATION		
FÖNSTER		
BYGGNADSTYP	SKALA	FORMAT
UPPSTÄLLNINGAR	1:50	A1
DOCUMENTNUMMER	ÄNDRING	
A-42-4-001		

FLN:AMN: C:\Norconsult\Autodesk\Revit\1088371-Centralkök Robertsfors_Centralfrili-2024_mastia.rvt