


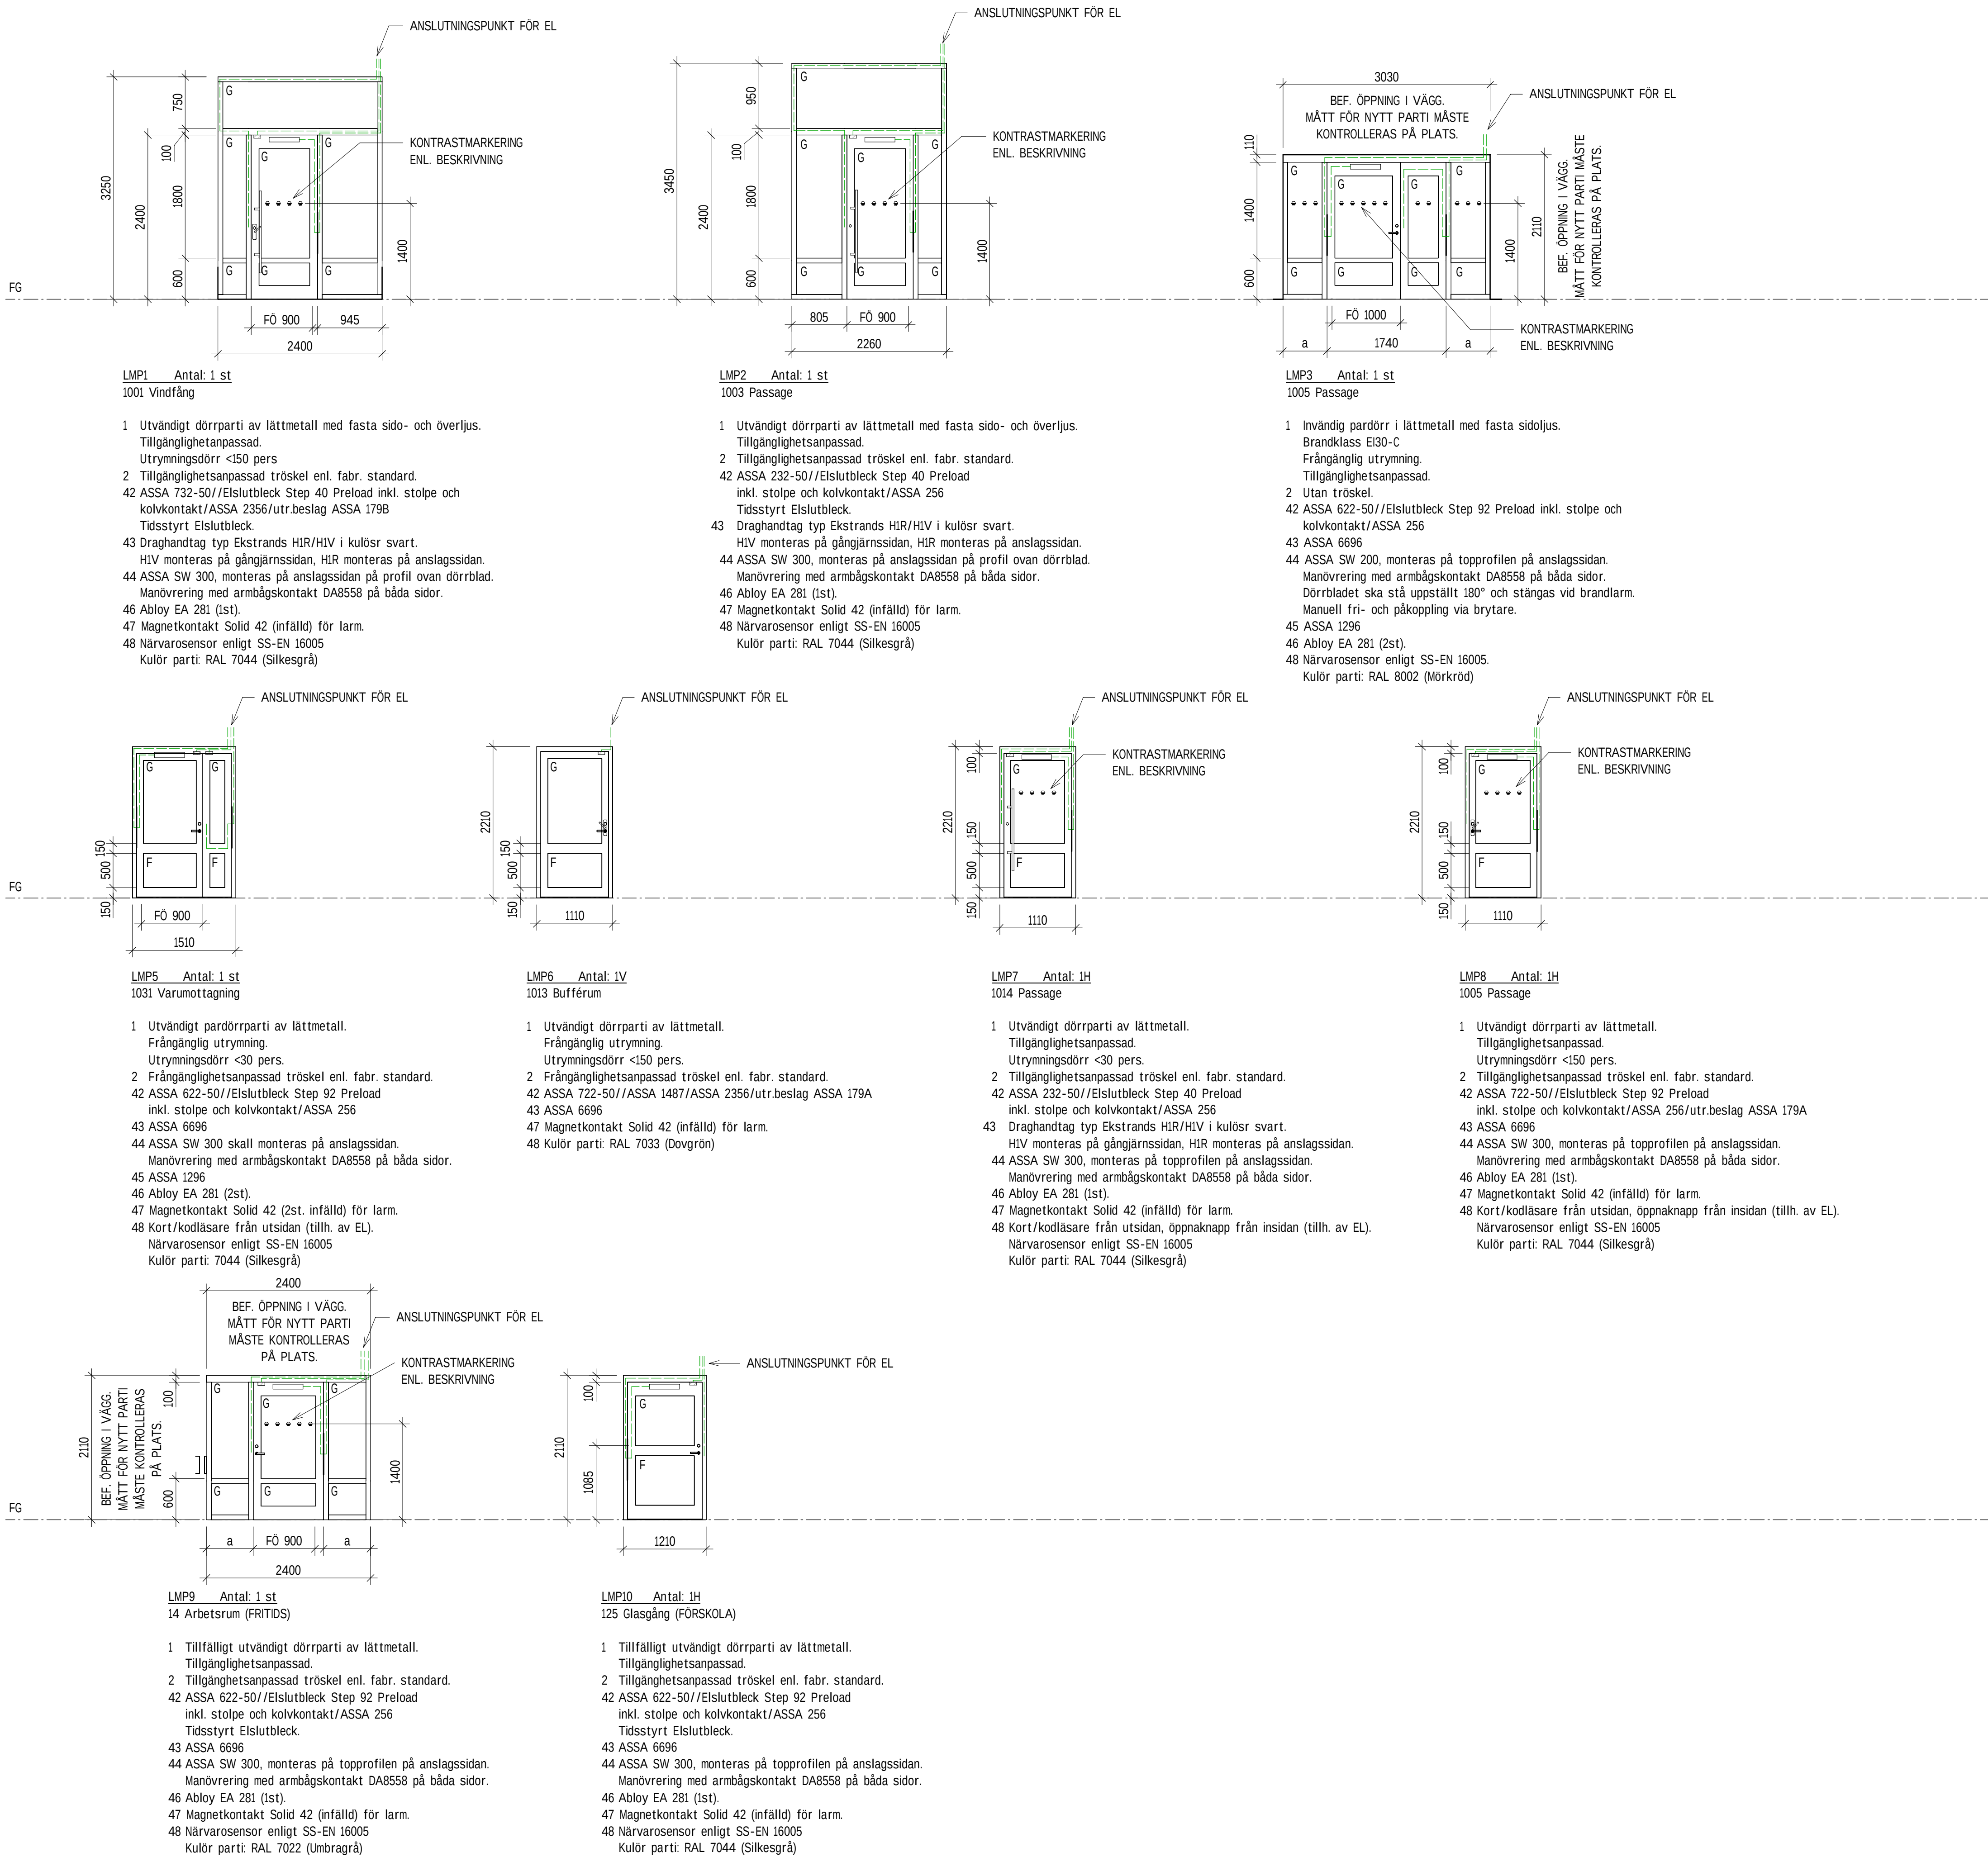

## FÖRKLARINGAR

V = Vänsterhängd  
H = Högerhängd  
G = Glas  
F = Fyllning enligt fabr. standard.  
F0= Fritt öppningsmått vid dörr uppställd 90°

Partier ses från gångjärnssidan.  
Alla mått i millimeter.  
Ytermått avser öppningsmått i vägg, där annat ej anges.  
Karmar märkes enligt ritningens litterering, i förekommande fall med tillagt V eller H.  
Brand och ljudklassade fönster och dörrar märkes enligt gällande normer.  
Mått skall kontrolleras på plats före tillverkning.

### KANTNUMMER ANGER:

1 =Sort/typ  
2 =Tröskel  
42 =Lås/cylinder/slutbleck/behör  
43 =Trycke/draghandtag  
44 =Dörrstängare/dörröppnare  
45 =Kantregel  
46 =Karmöverföring  
47 =Magnetkontakt  
48 =Övrigt

## FÖRESKRIFTER

### SORT/TYP

In. och utvändiga partier av Aluminium typ Schuco eller lik. Ev. brand, ljud, och skyddsklass enl. resp. littera.

### PROFILER

Profiltyp dimensioneras av leverantören utifrån kravspec. för resp. littera.

### VÄRMEISOLERING

U-värde 1,1 W/m²K (Gäller utvändiga partier)

### TRÖSKEL

Tröskel enl. uppställning.

### YTBEHANDLING/KULÖR

Partier lackerad i kulör: Enl. uppställning.

## FÖRESKRIFTER

### GÅNGJÄRN

Enligt fabrikantens standard, kulör lika parti.

### LÄSNING

Nytt låsschema upprättas av entreprenören i samråd med beställaren.  
Cylindrar tillhandahålls av beställaren, monteras av entreprenören.

### ELSLUTBLECK

Elslutbleck utföres med rättvänd funktion 24 VDC om annat ej anges.

### TRYCKE/DRAGHANDTAG

Trycken och skyltar med fast rosett och genomgående monterig.  
Ytbehandling: Prion eller likv.

### DÖRRSTÄNGARE/DÖRRAUTOMATIK/NÄRVAROSENSORER

Erforderliga tillbehör för fastsättning skall ingå i leverans. Kulör silver.  
Närvarosensorer på dörrar i brandcellsgräns skall kopplas ur vid brandlarm.  
Dörrautomatik skall vara försedd med batteribackup.

### GLAS

Klarglas i brand, ljud och skyddsklass enligt littera.  
Glasytor skall uppfylla kraven för person-säkerhet enligt BBR 8:353, lägst klass 2(B)2 enligt SS-EN 12600

### TÄCKPLÅTAR

Samtliga täckplåtar vid ansl. partier, väggar, pelare etc. skall utföras av al-plåt i samma ytbehandling och kulör som parti.

### KANALISATION/KABLAGE

Utföres dold med flexrör och skall försees med dragtråd. Kablage infällt i partier skall avslutas med 3,0 meter fri ledning.

### ÖVRIGT

Dörrar skall som helhet inkl fastsättningslister etc. uppfylla föreskriven brand- och ljudklass. Brand- och ljudklassade dörrar skall försees med typgodkännandebevis eller intyg från fabrikanter att partier uppfyller föreskriven brand- och ljudklass.  
Erforderliga infästningsdetaljer i byggnadssommen monteras av byggnadsentreprenören enligt fabrikantens anvisningar.

## HÄNVISNINGAR

PLAN ÖVERSIKT, BRAND A-40-1-501  
DELPLANER A-40-1-511 -- 514

|                      |                       |            |
|----------------------|-----------------------|------------|
| SEKTION              |                       |            |
|                      |                       |            |
| ORIENTERINGSSKISS    |                       |            |
|                      |                       |            |
| STATUS               |                       |            |
| FÖRFRÅGNINGSUNDERLAG |                       |            |
| HANDLING             |                       |            |
| BYGGHANDLING         |                       |            |
| DATUM                | FÖRFRÅGAVEN           | ANSÖKAN PM |
| 2024-12-20           | T. BERGSTRÖM          |            |
| BESTÄLLARE           |                       |            |
|                      |                       |            |
| PROJEKTNAMN          |                       |            |
| CENTRALKÖK           |                       |            |
| CONTRAGE             |                       |            |
| ROBERTSFORS KOMMUN   |                       |            |
| PROJEKTNUMMER        | ANVÄNDARE             |            |
|                      | YTTRE RINGVÄGEN 4     |            |
| DÖRRKONNUMMER        | FASTIGHET             |            |
|                      | FORDONET 1            |            |
| DISCIPLIN            | FÖRETAG               |            |
| A                    | NORCONSULT SVERIGE AB |            |
| UPPDRAGSRUMMER       | SKAPAD AV             |            |
| 108 83 71            | MSR                   |            |
| TELEFON              | KONTAKTPERSON         |            |
| 010 141 80 00        | TOMAS BERGSTRÖM       |            |
| BYGGNADSRUMMER       | FÖRSTÄLLNING          |            |
|                      |                       |            |
| VÄRNINGSPLAN         | VÄRNINGSDRÖM          | DELOMRÅDE  |
|                      |                       |            |
| SYSTEM               |                       |            |
| 42 YTTERVÄGG         |                       |            |
| SPECIFIKATION        |                       |            |
| LÄTTMETALLPARTIER    |                       |            |
| BYGGNADSRUMMER       | SKALA                 | FORMAT     |
| UPPSTÄLLNING         | 1:50                  | A1         |
| DOCUMENTNUMMER       | AVGIFTER              |            |
| A-42-4-002           |                       |            |

SKALA 1:50 0 1 5 METER

