




VERTIKALDETALJER

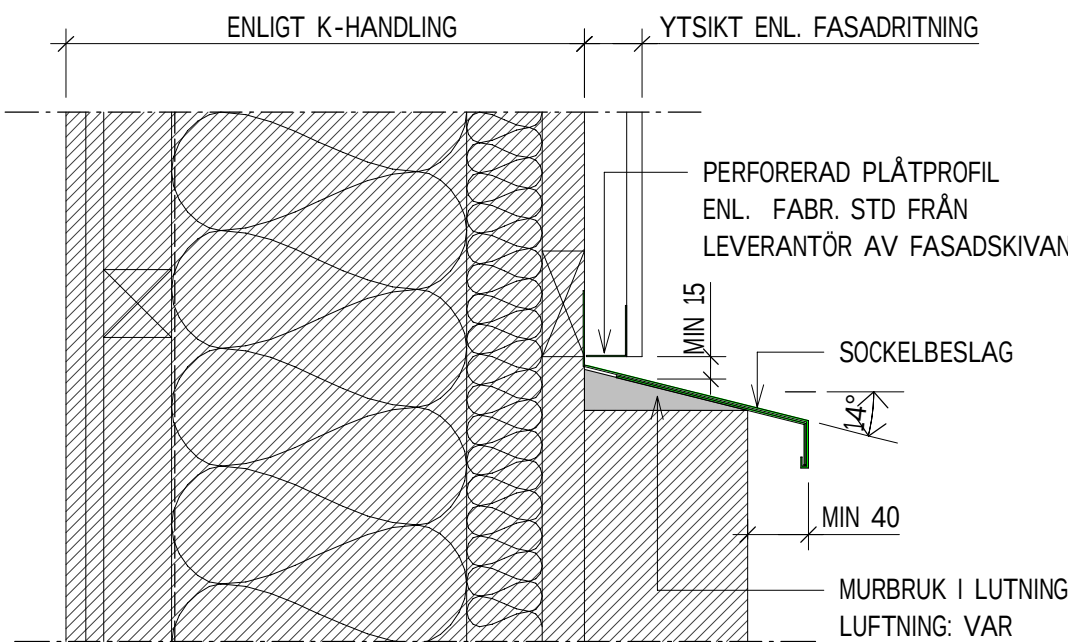


VD1 PRINCIPDETALJ
1:5
HÖJD TEGELSOCKEL I LIV MED HÖJD DET VD3

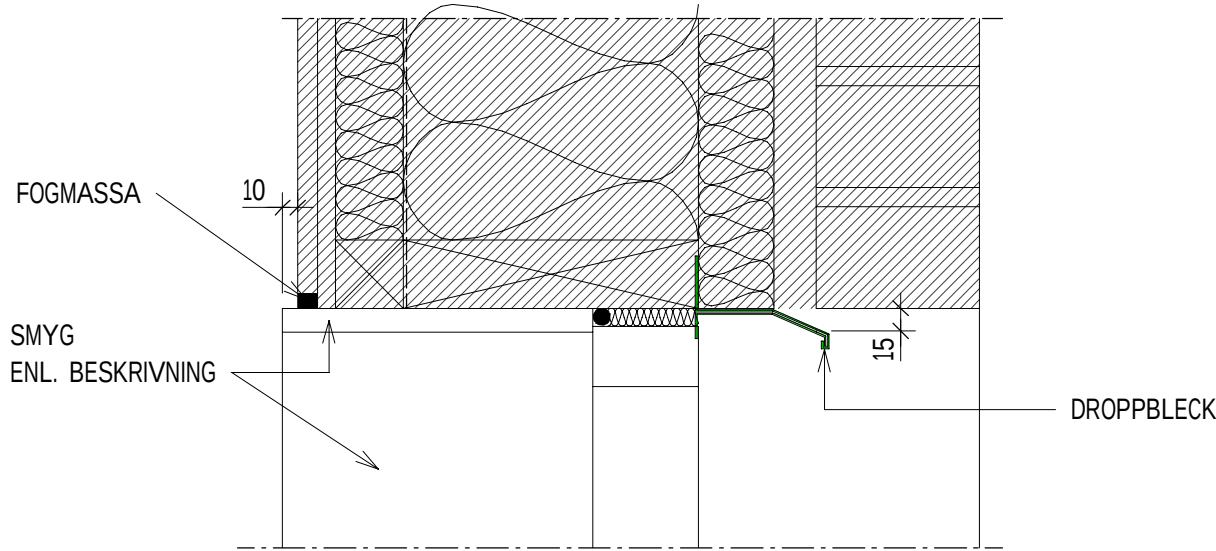


VD2 PRINCIPDETALJ
1:5 FÖNSTER

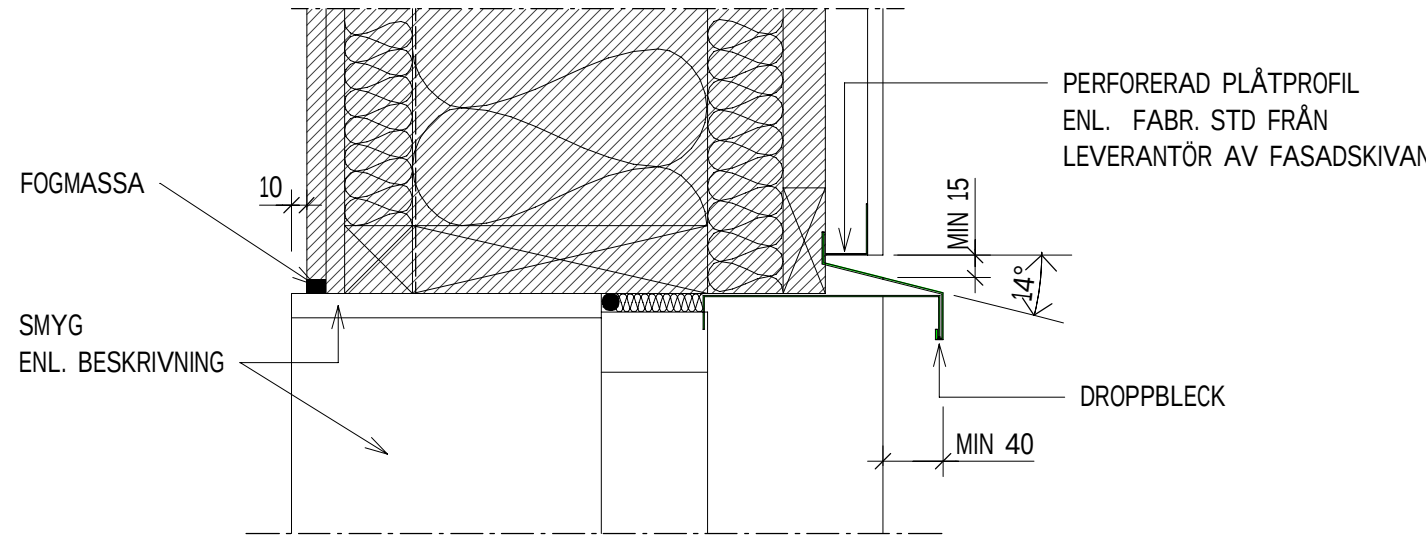


VD4 PRINCIPDETALJ
1:5 FÖNSTER

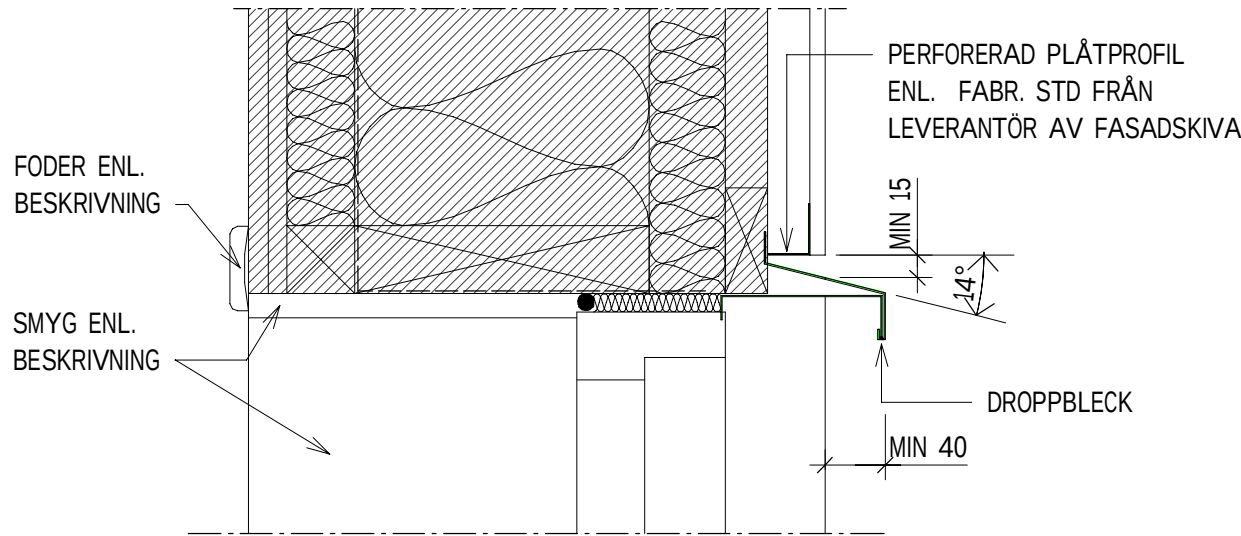


VD6 PRINCIPDETALJ
1:5 STÅLDÖRR

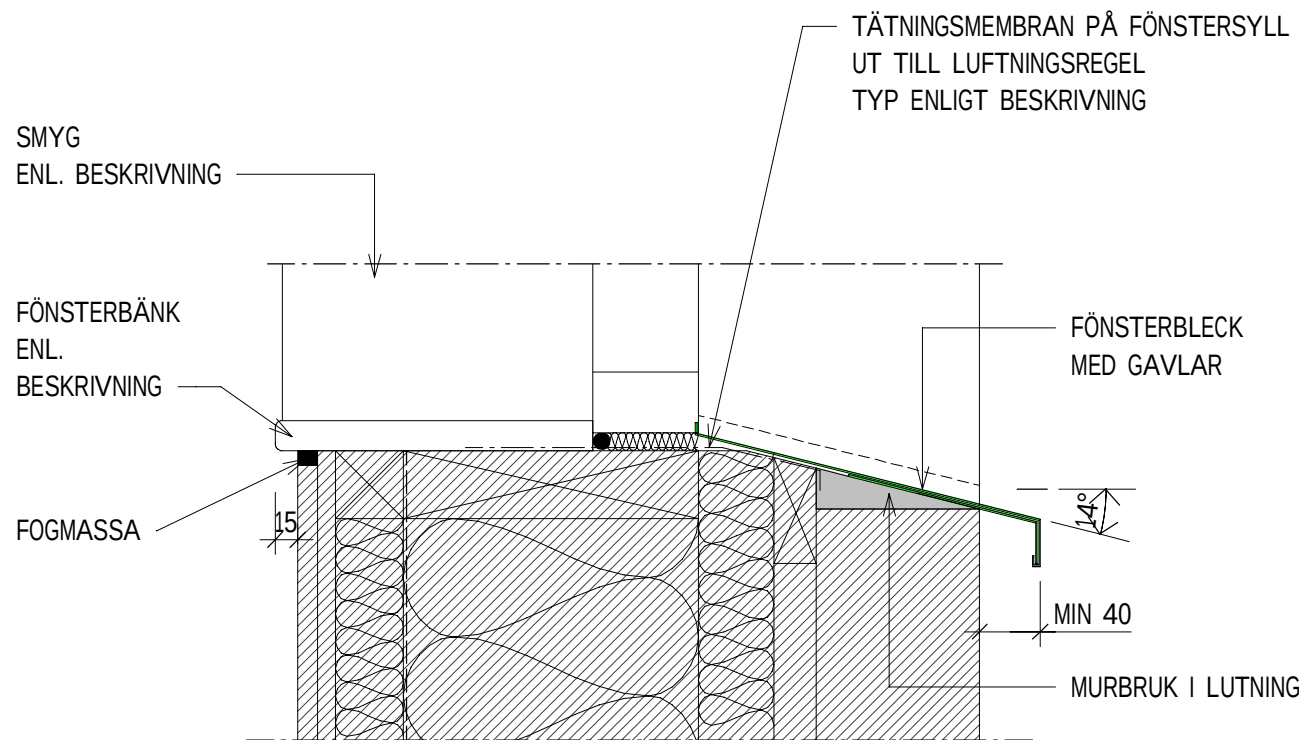


VD3 PRINCIPDETALJ
1:5 FÖNSTER

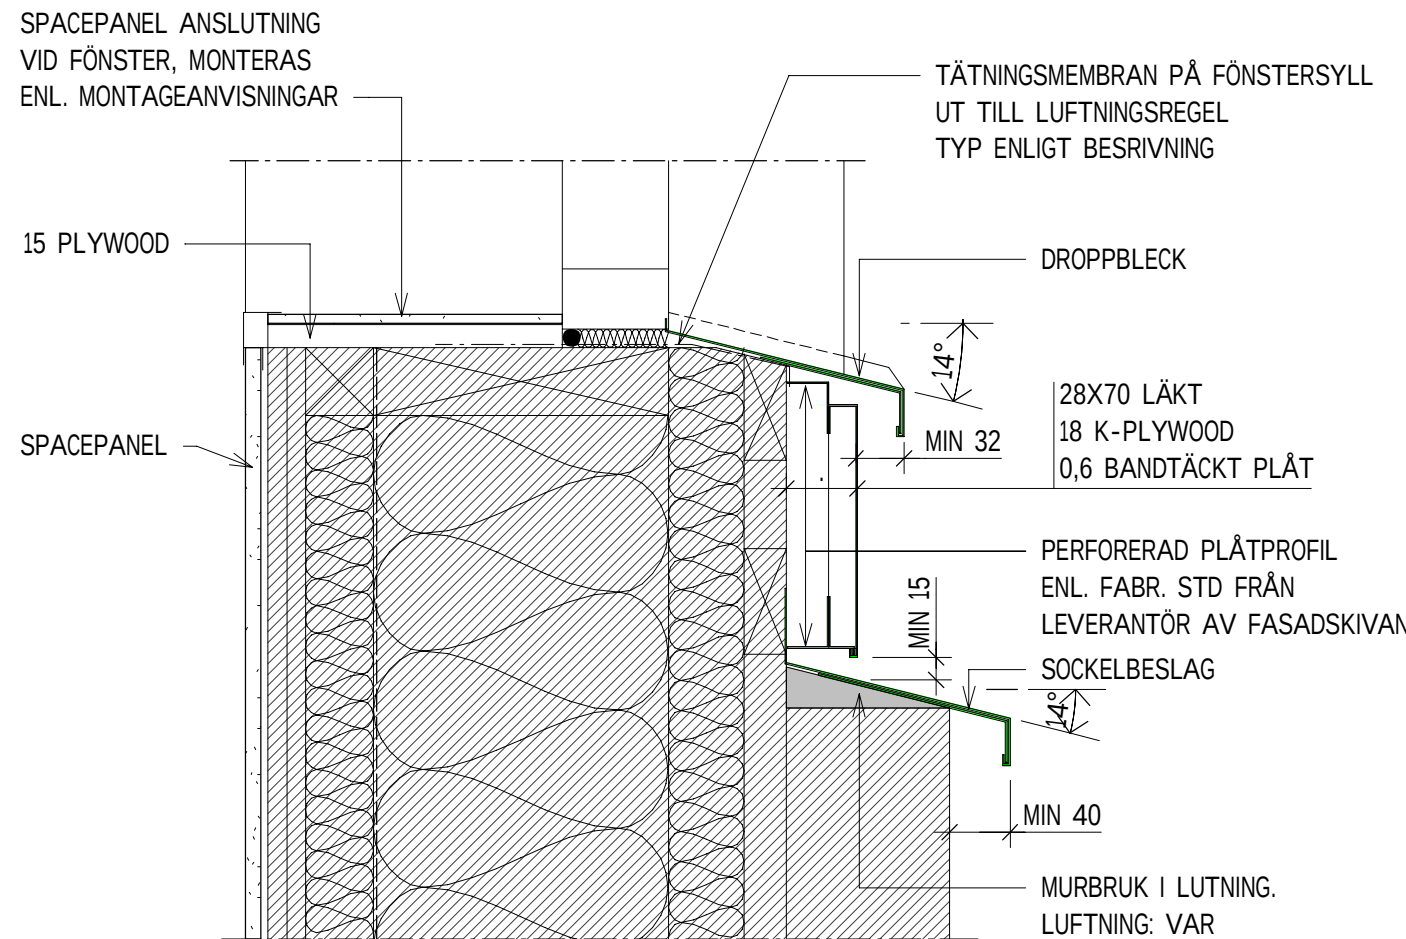


VD5 PRINCIPDETALJ
1:5 FÖNSTER
HÖJD TEGELSOCKEL I LIV MED HÖJD DET VD3

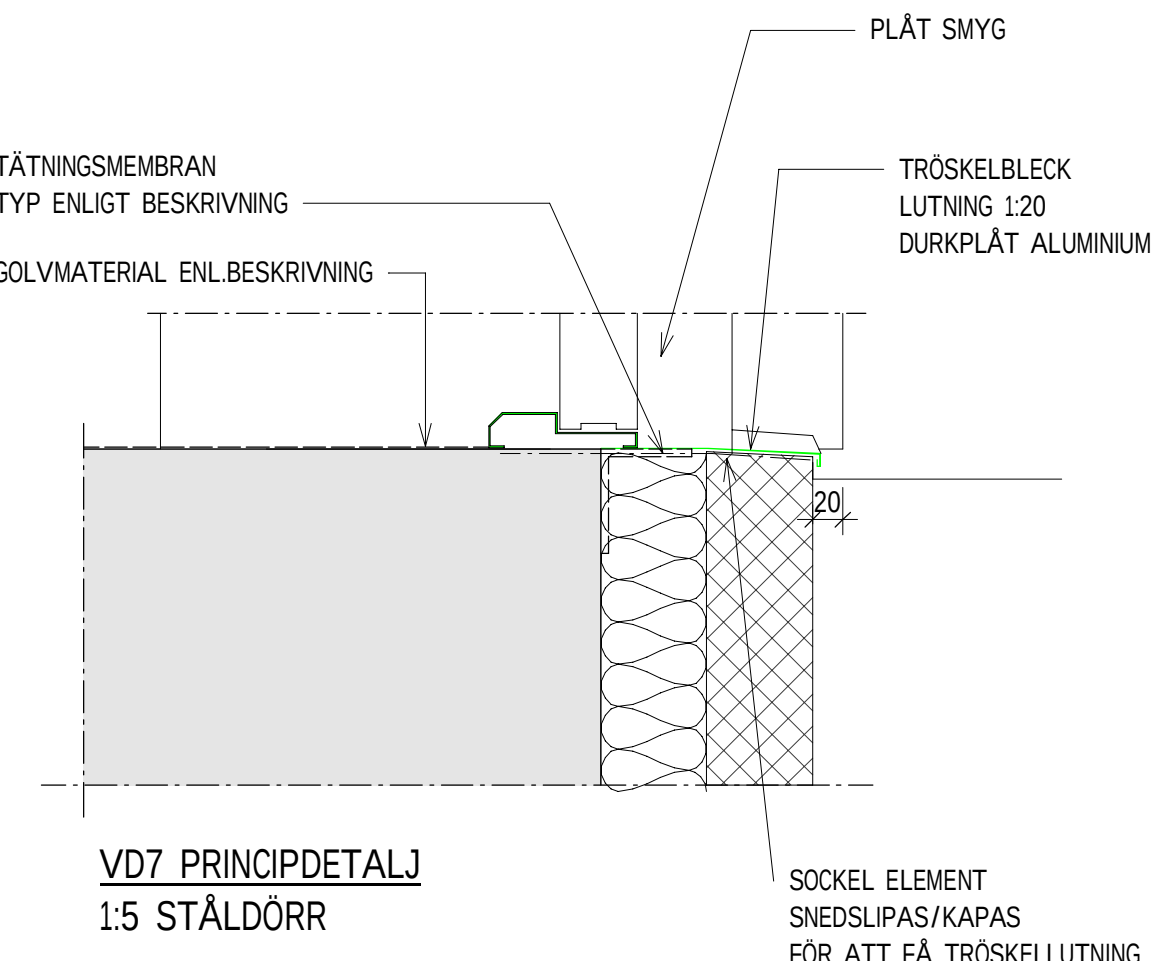


VD7 PRINCIPDETALJ
1:5 STÅLDÖRR

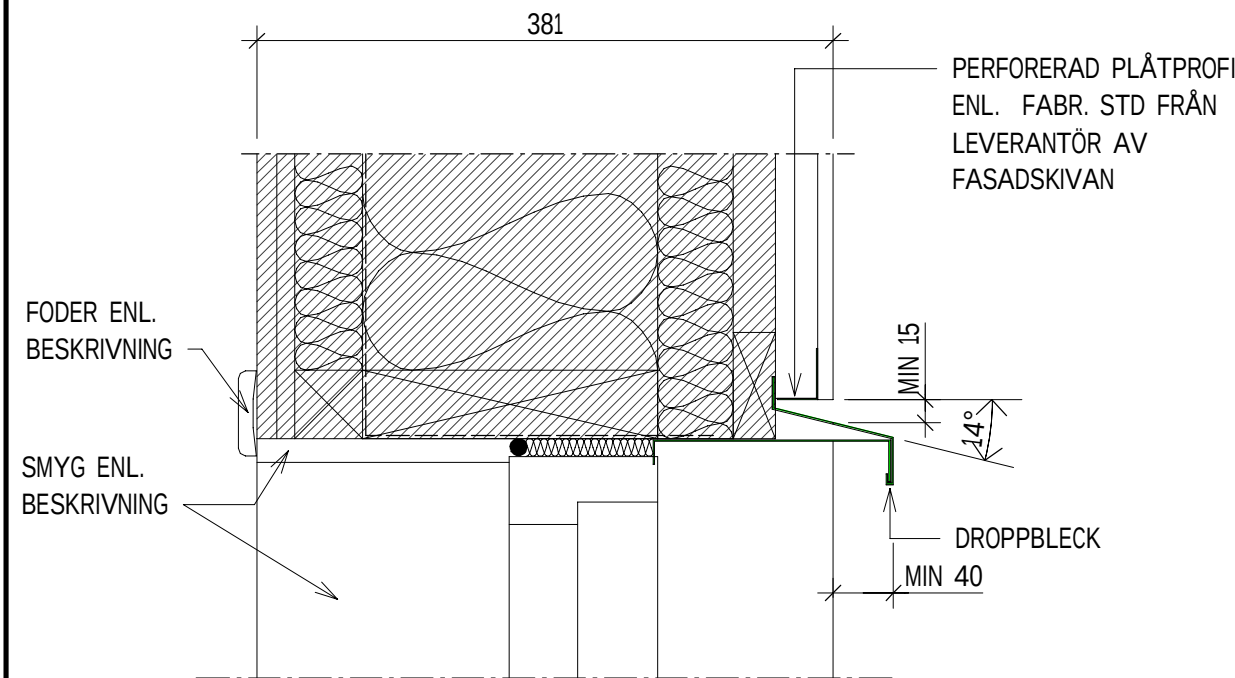


VD8 PRINCIPDETALJ
1:5
DÖRR FLÅKTRUM PLAN 2

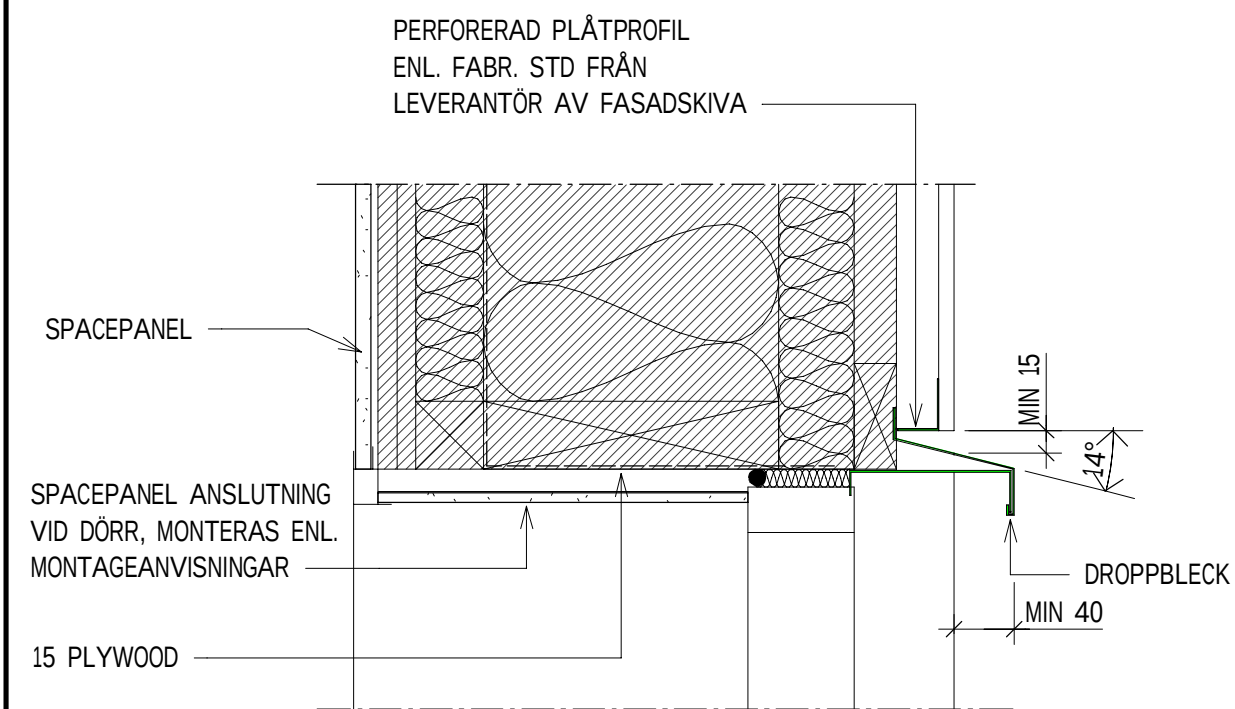


VD9 PRINCIPDETALJ
1:5 METALLPARTI

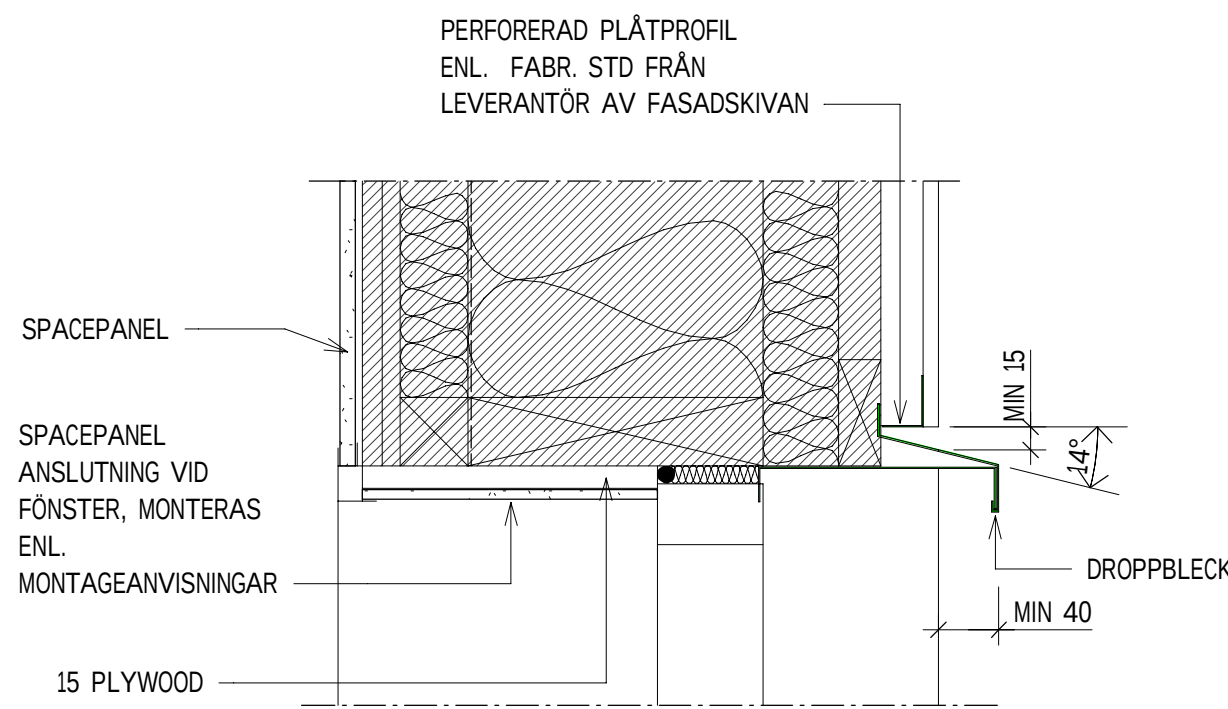


VD11 PRINCIPDETALJ
1:5 FÖNSTER

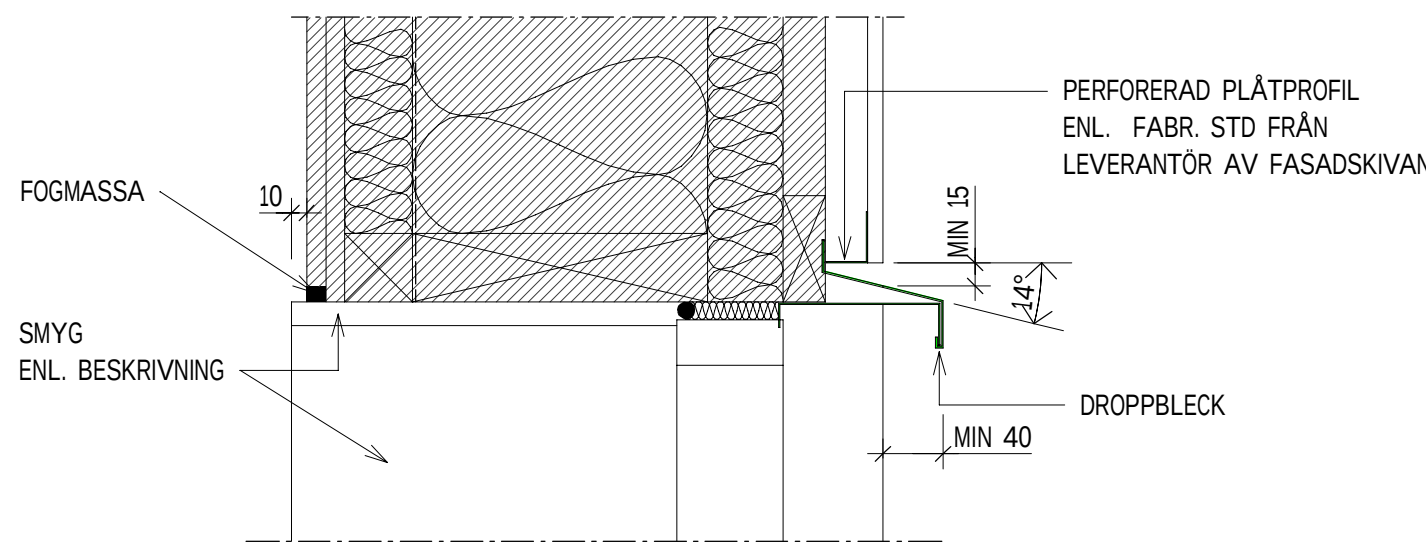


VD13 PRINCIPDETALJ
1:5 METALLPARTI

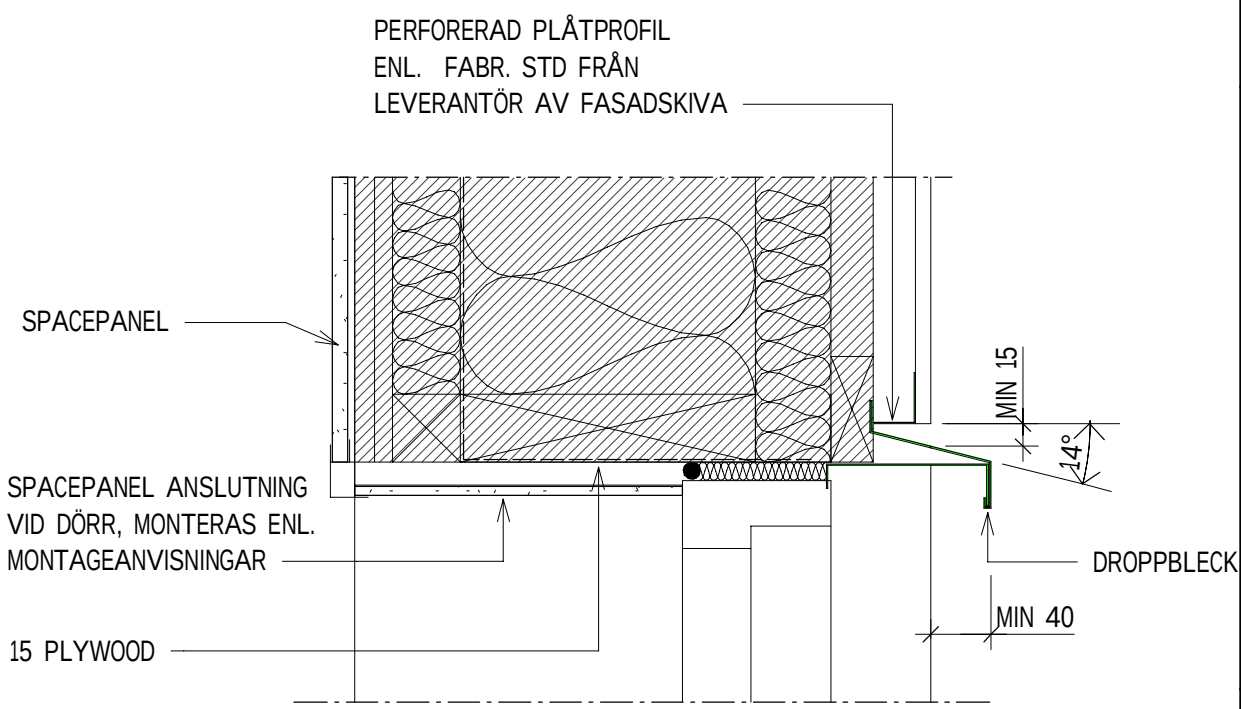


VD15 PRINCIPDETALJ
1:5 STÅLDÖRR

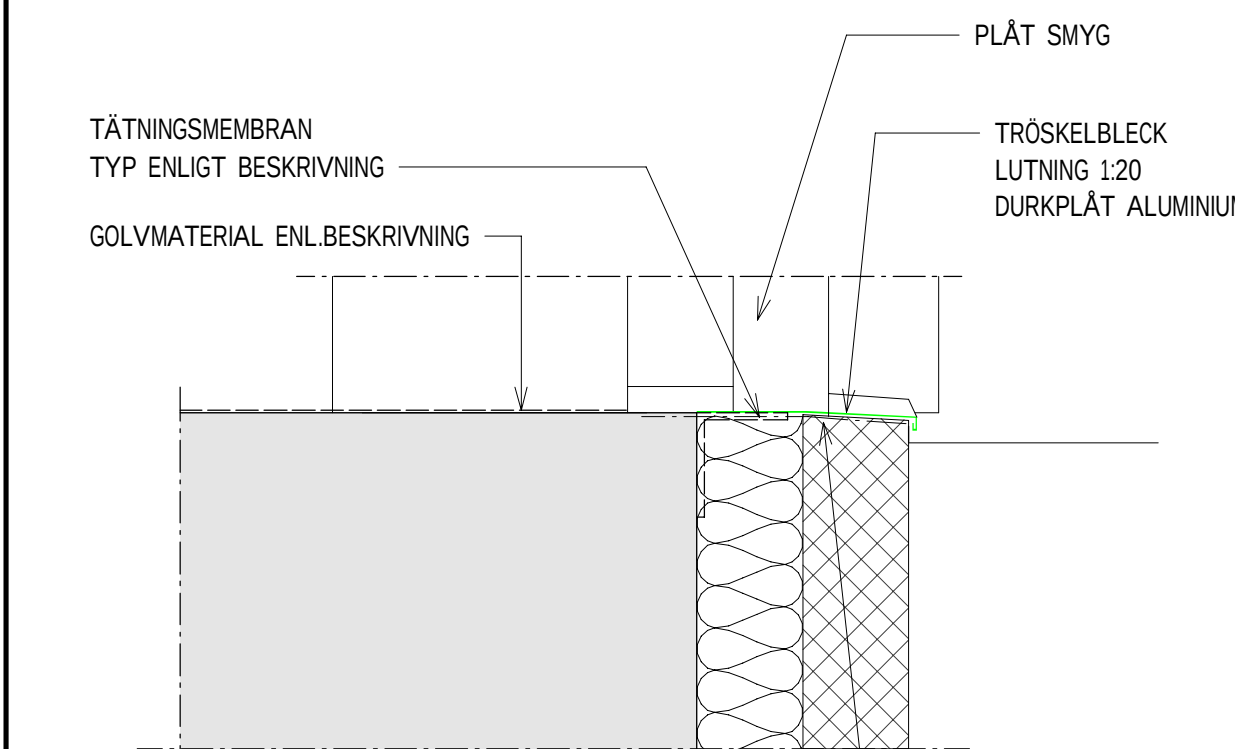


VD10 PRINCIPDETALJ
1:5 METALLPARTI

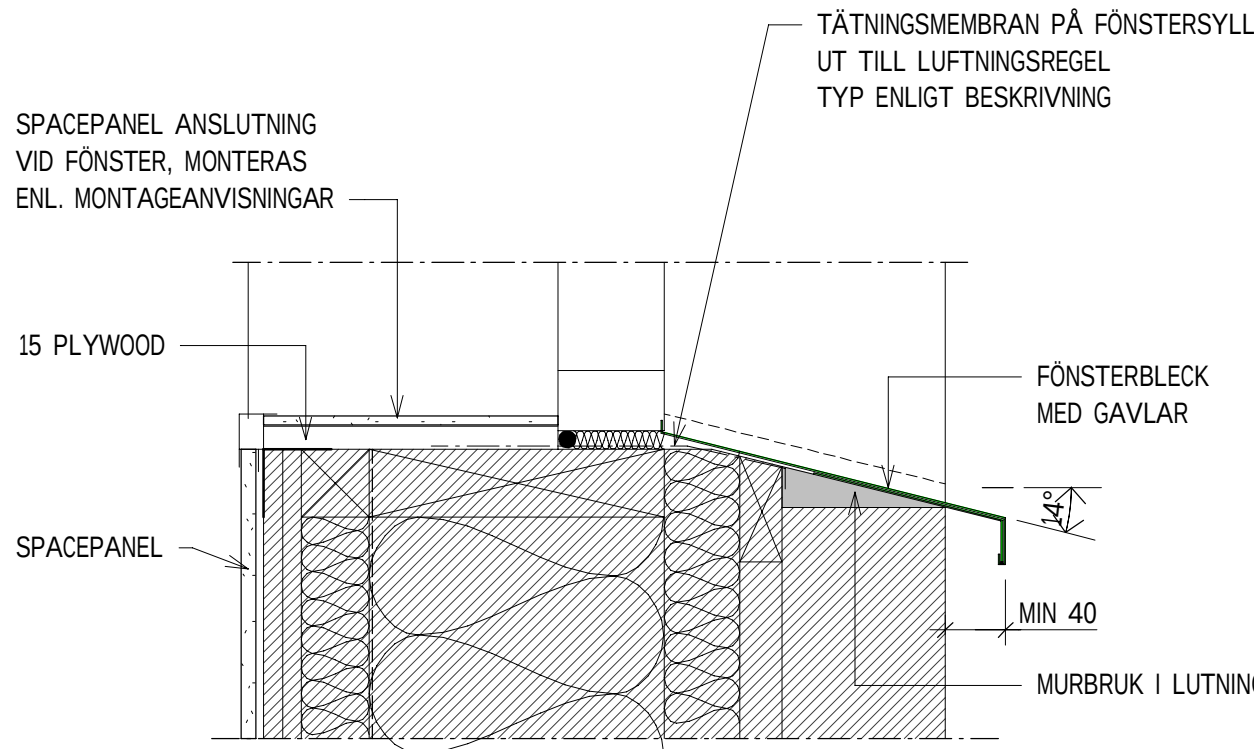

VD12 PRINCIPDETALJ
1:5 FÖNSTER

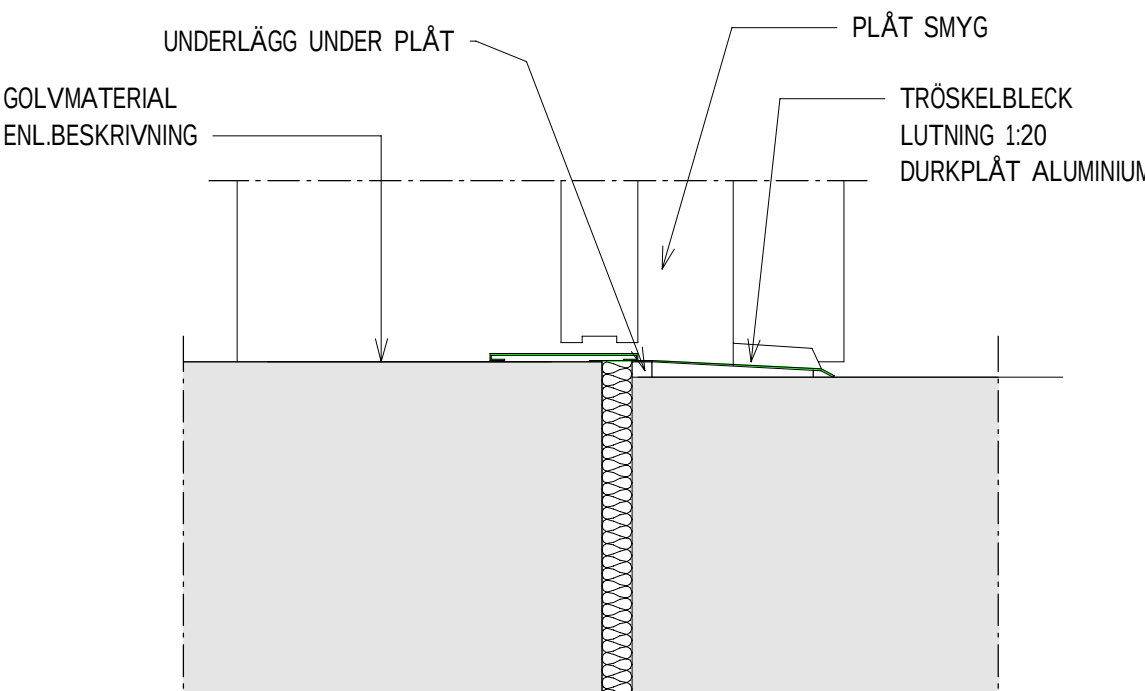

VD14 PRINCIPDETALJ
1:5 STÅLDÖRR SOPRUM

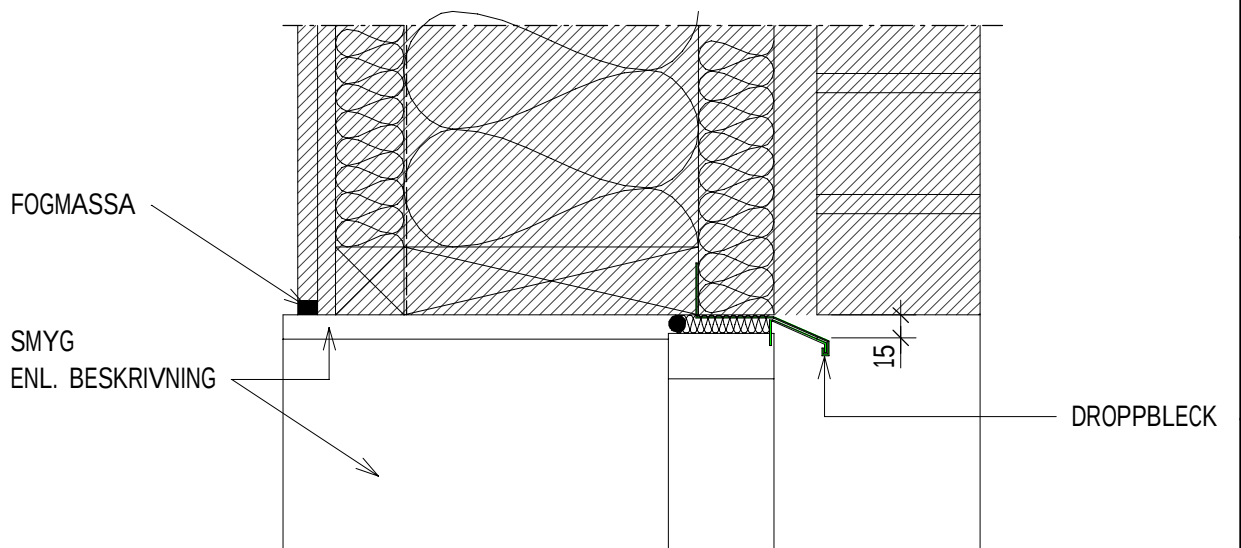

VD16 PRINCIPDETALJ
1:5 METALLPARTI


FÖRKLARINGAR

ALLA MÄTT ANGES I MILLIMETER

= ENL. K

HÄNVISNINGAR

FASADER - ÖVERSIKT A-40-3-001
VERTIKALA OCH HORIZONTELLA DETALJER A-42-6-001--003

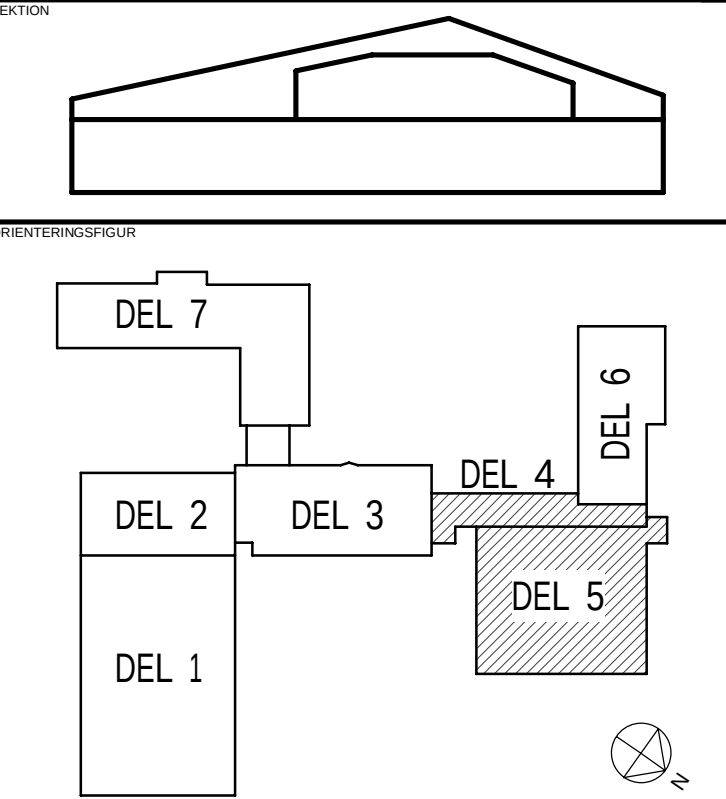

FÖRFRÅGNINGSUNDERLAG

BYGGHANDLING

DATUM: 2024-12-20 FÖRFRÅGAD AV: T. BERGSTRÖM

BESTÄLLARE: ROBERTSFORS KOMMUN



CENTRALKÖK

ROBERTSFORS KOMMUN

PROJEKTNUMMER: YTTRE RINGVÄGEN 4

DIARIENUMMER: FORDONET 1

DISCIPLIN: A FÖRETAG: NORCONSULT SVERIGE AB

UPPDRAGSNUMMER: 108 83 71 SKAPAD AV: CHE

TELEFON: 010 141 80 00 KONTAKTPERSON: TOMAS BERGSTRÖM

BYGGNADSTYP: FLUGHUS (VIN 2008)

VÄRINGSPLAN: VÄRINGSDEL: DELOMRÅDE:

SYSTEM: 42 YTTERVÄGG

SPECIFIKATION: YTTERVÄGGSDETALJER

DETALJ: 1:5

FORMAT: A1

DOCUMENTNUMMER: A-42-6-001

SKALA 1:5

0 100 500 MILLIMETER