




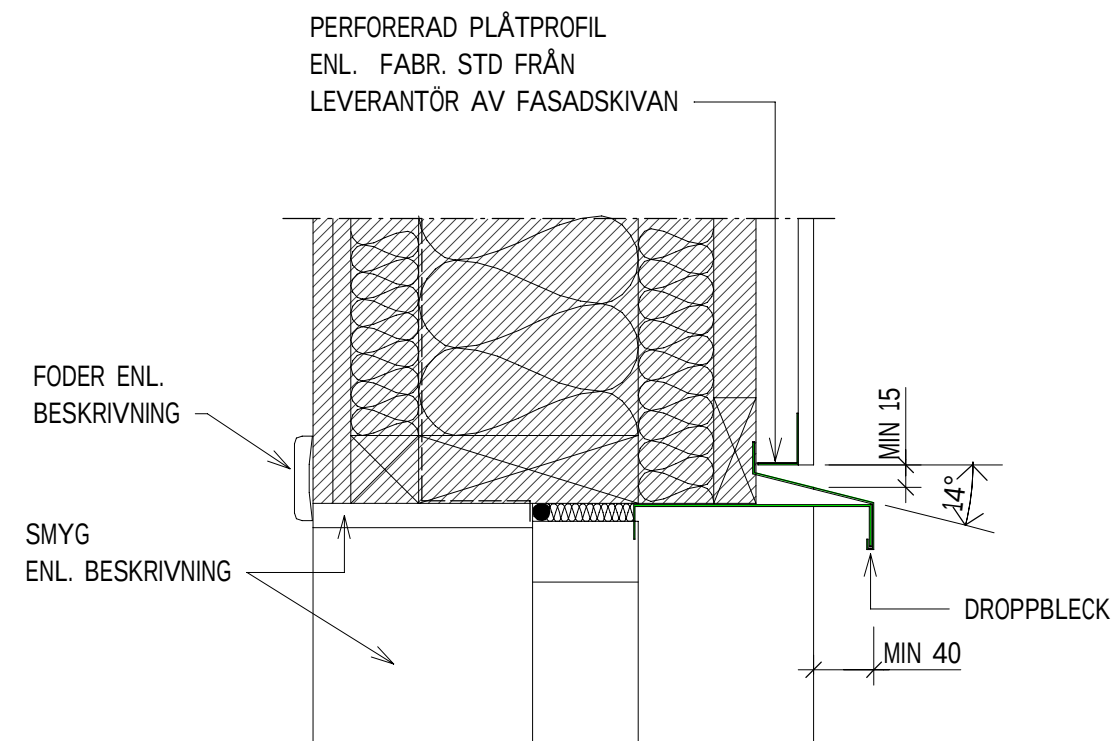

VD17 PRINCIPDETALJ
1:5 FÖNSTER SOPRUM

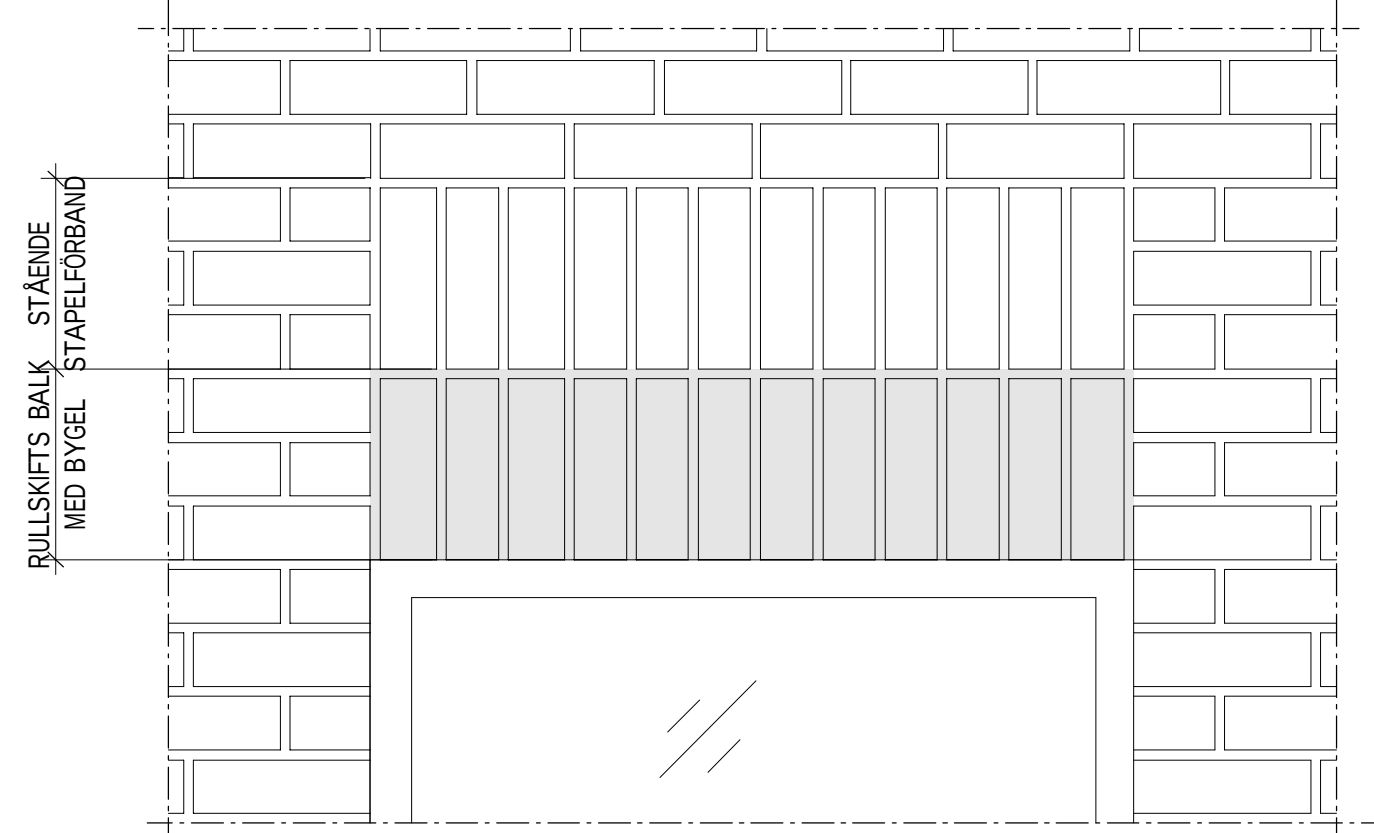

EV1 PRINCIP ELEVATION
1:10
RULLSKIFTS BALK - MED BYGEL

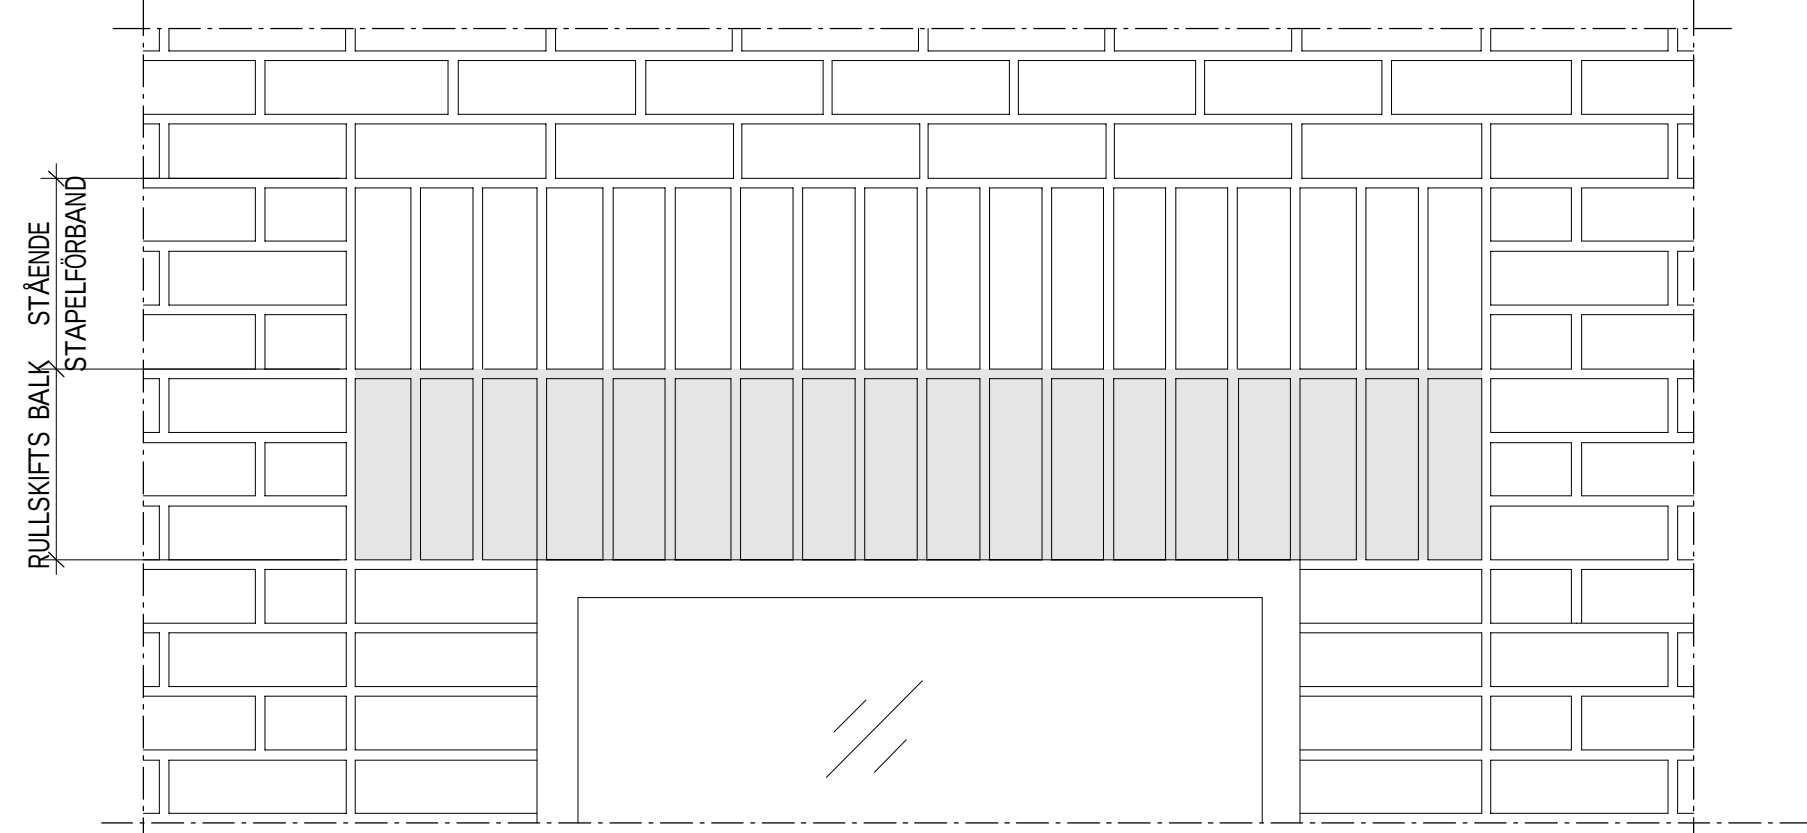

EV2 PRINCIP ELEVATION
1:10
RULLSKIFTS BALK


FÖRKLARINGAR

ALLA MÄTT ANGES I MILLIMETER




HÄNVISNINGAR


FASADER - ÖVERSIKT A-40-3-001
VERTIKALA OCH HORIZONTALA DETALJER A-42-6-001--003

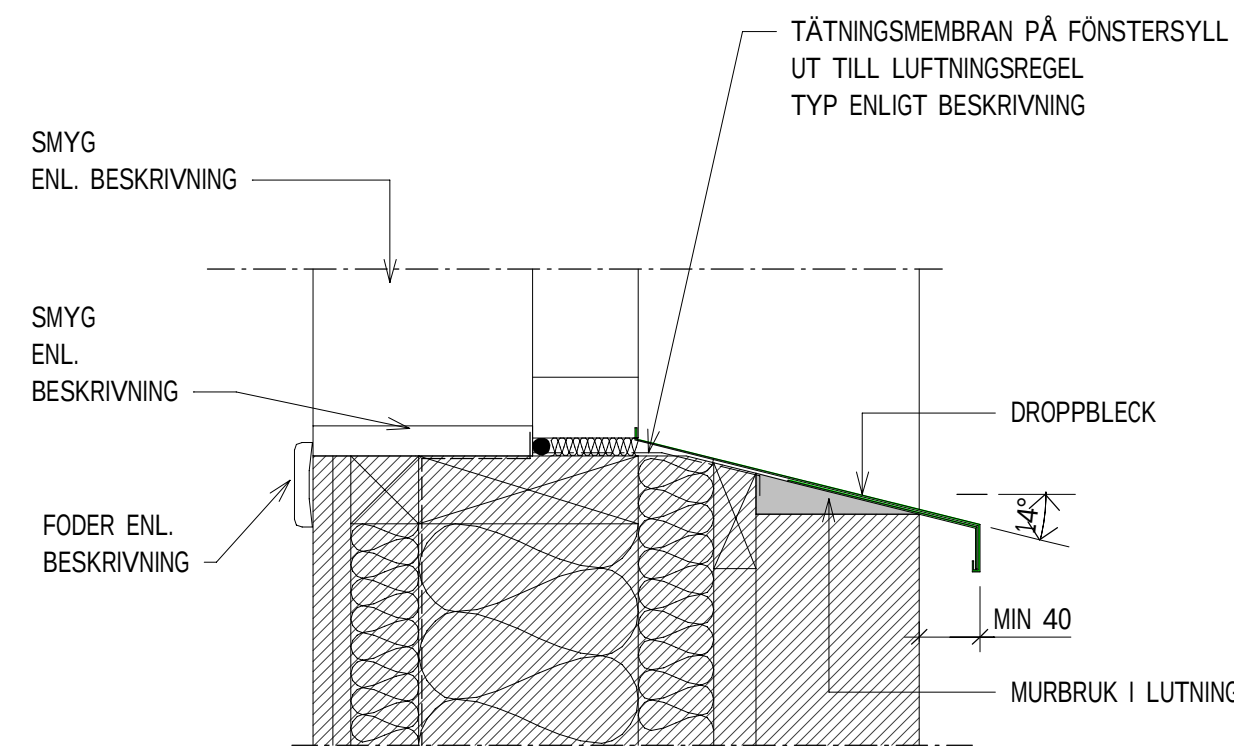


VD18 PRINCIPDETALJ
1:5 FÖNSTER SOPRUM

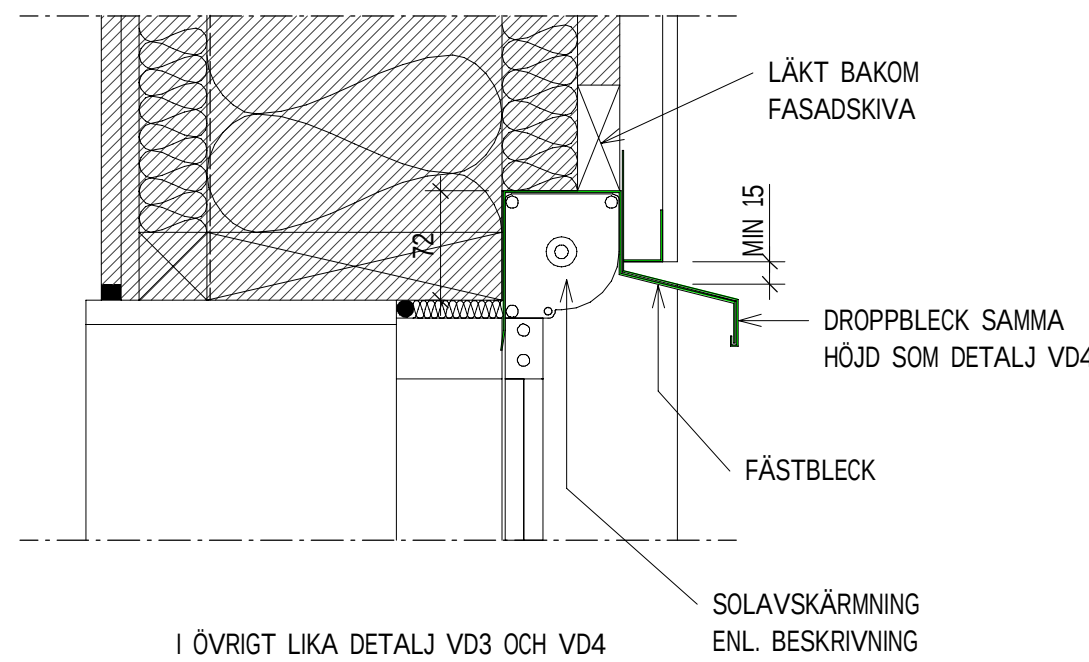


VD21 PRINCIPDETALJ
1:5 FÖNSTER MED VERTIKALMARKIS

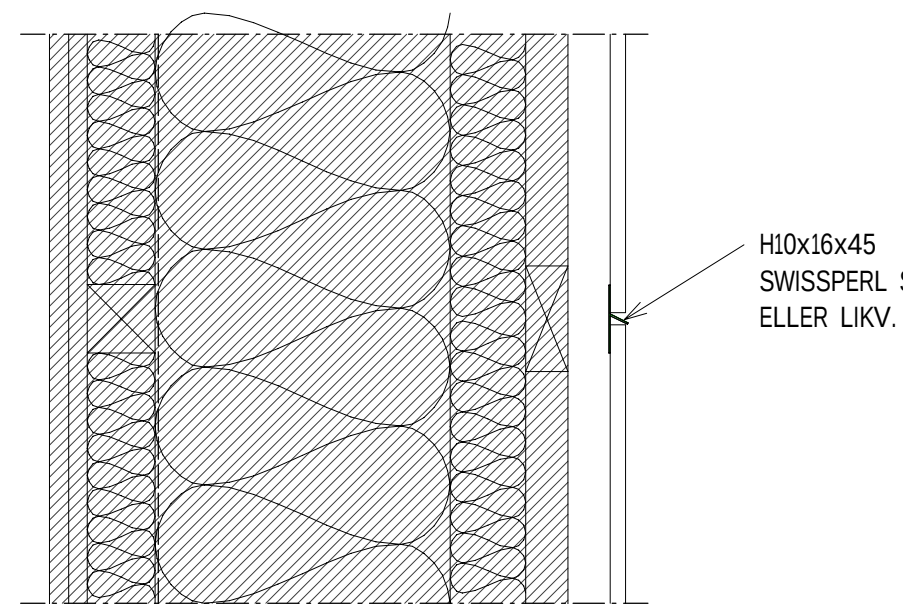


VD20 PRINCIPDETALJ
1:5 LIST MELLAN FASADSKIVOR

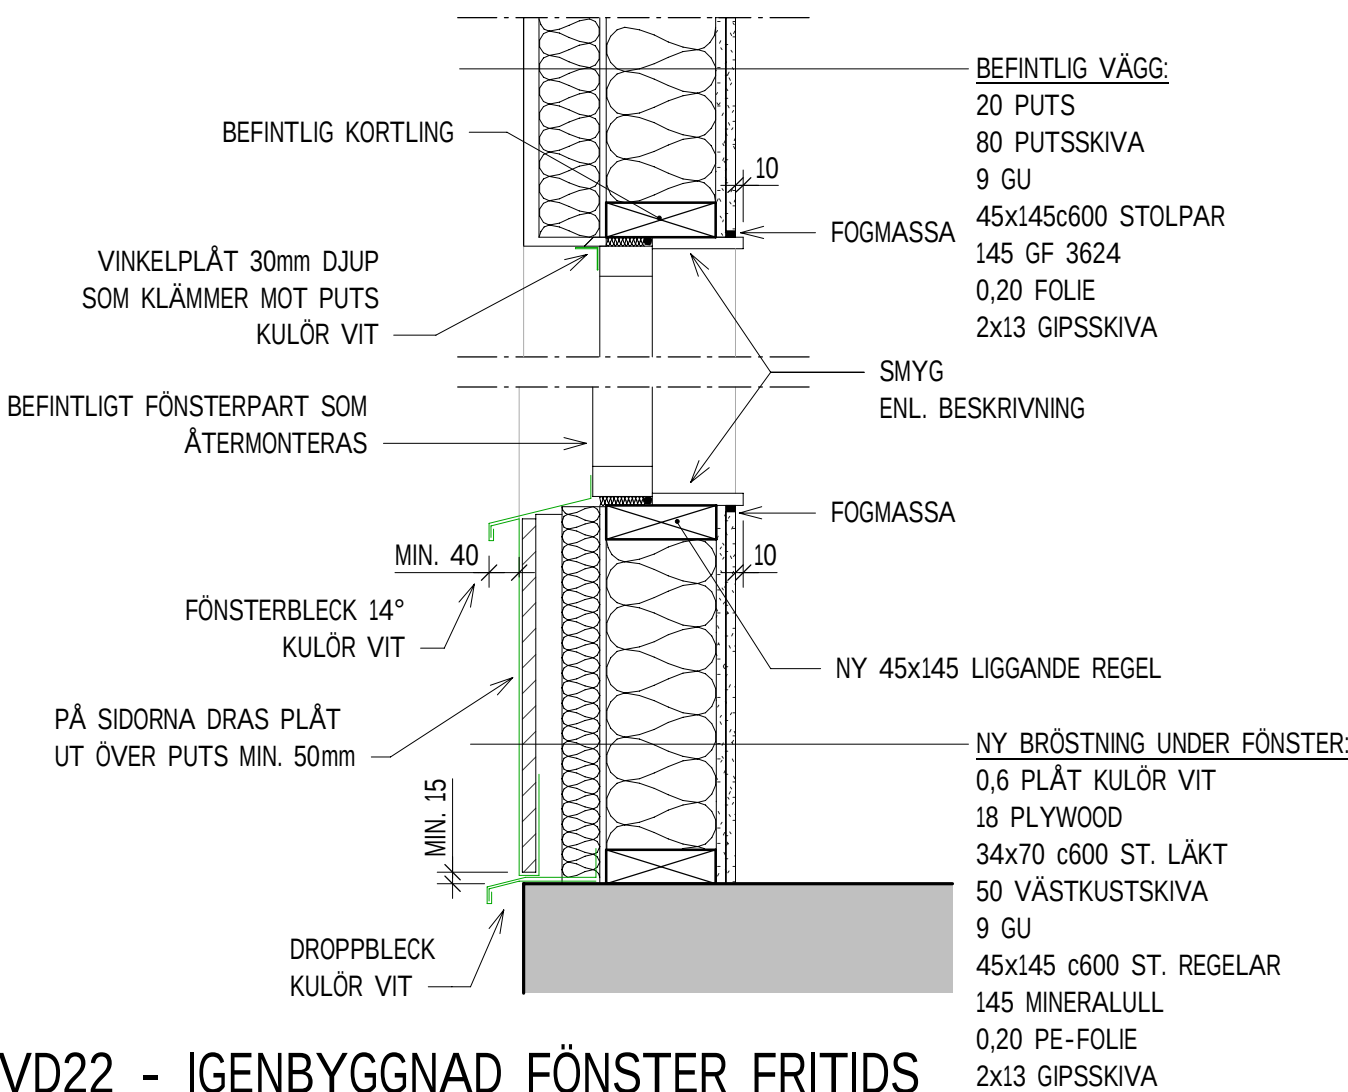


VD22 - IGENBYGGNAD FÖNSTER FRITIDS
1:10

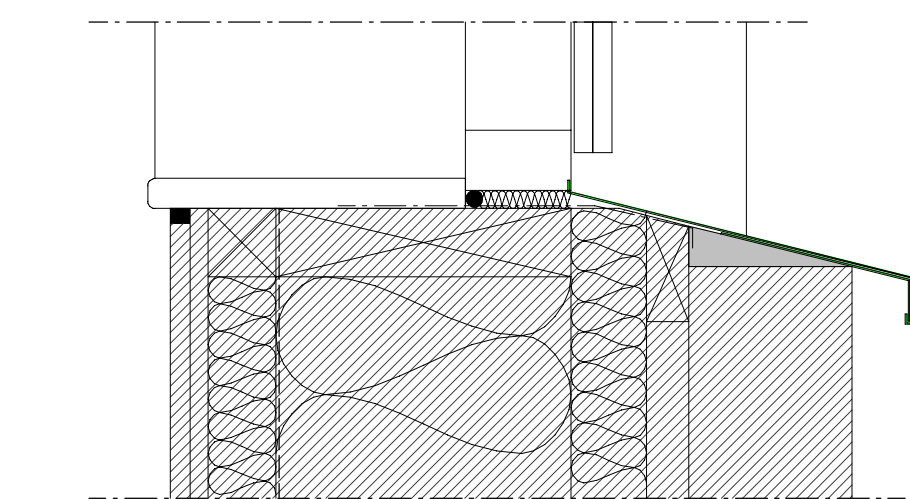


VD23 - IGENBYGGNAD FÖNSTER TRAPPHUS
1:10

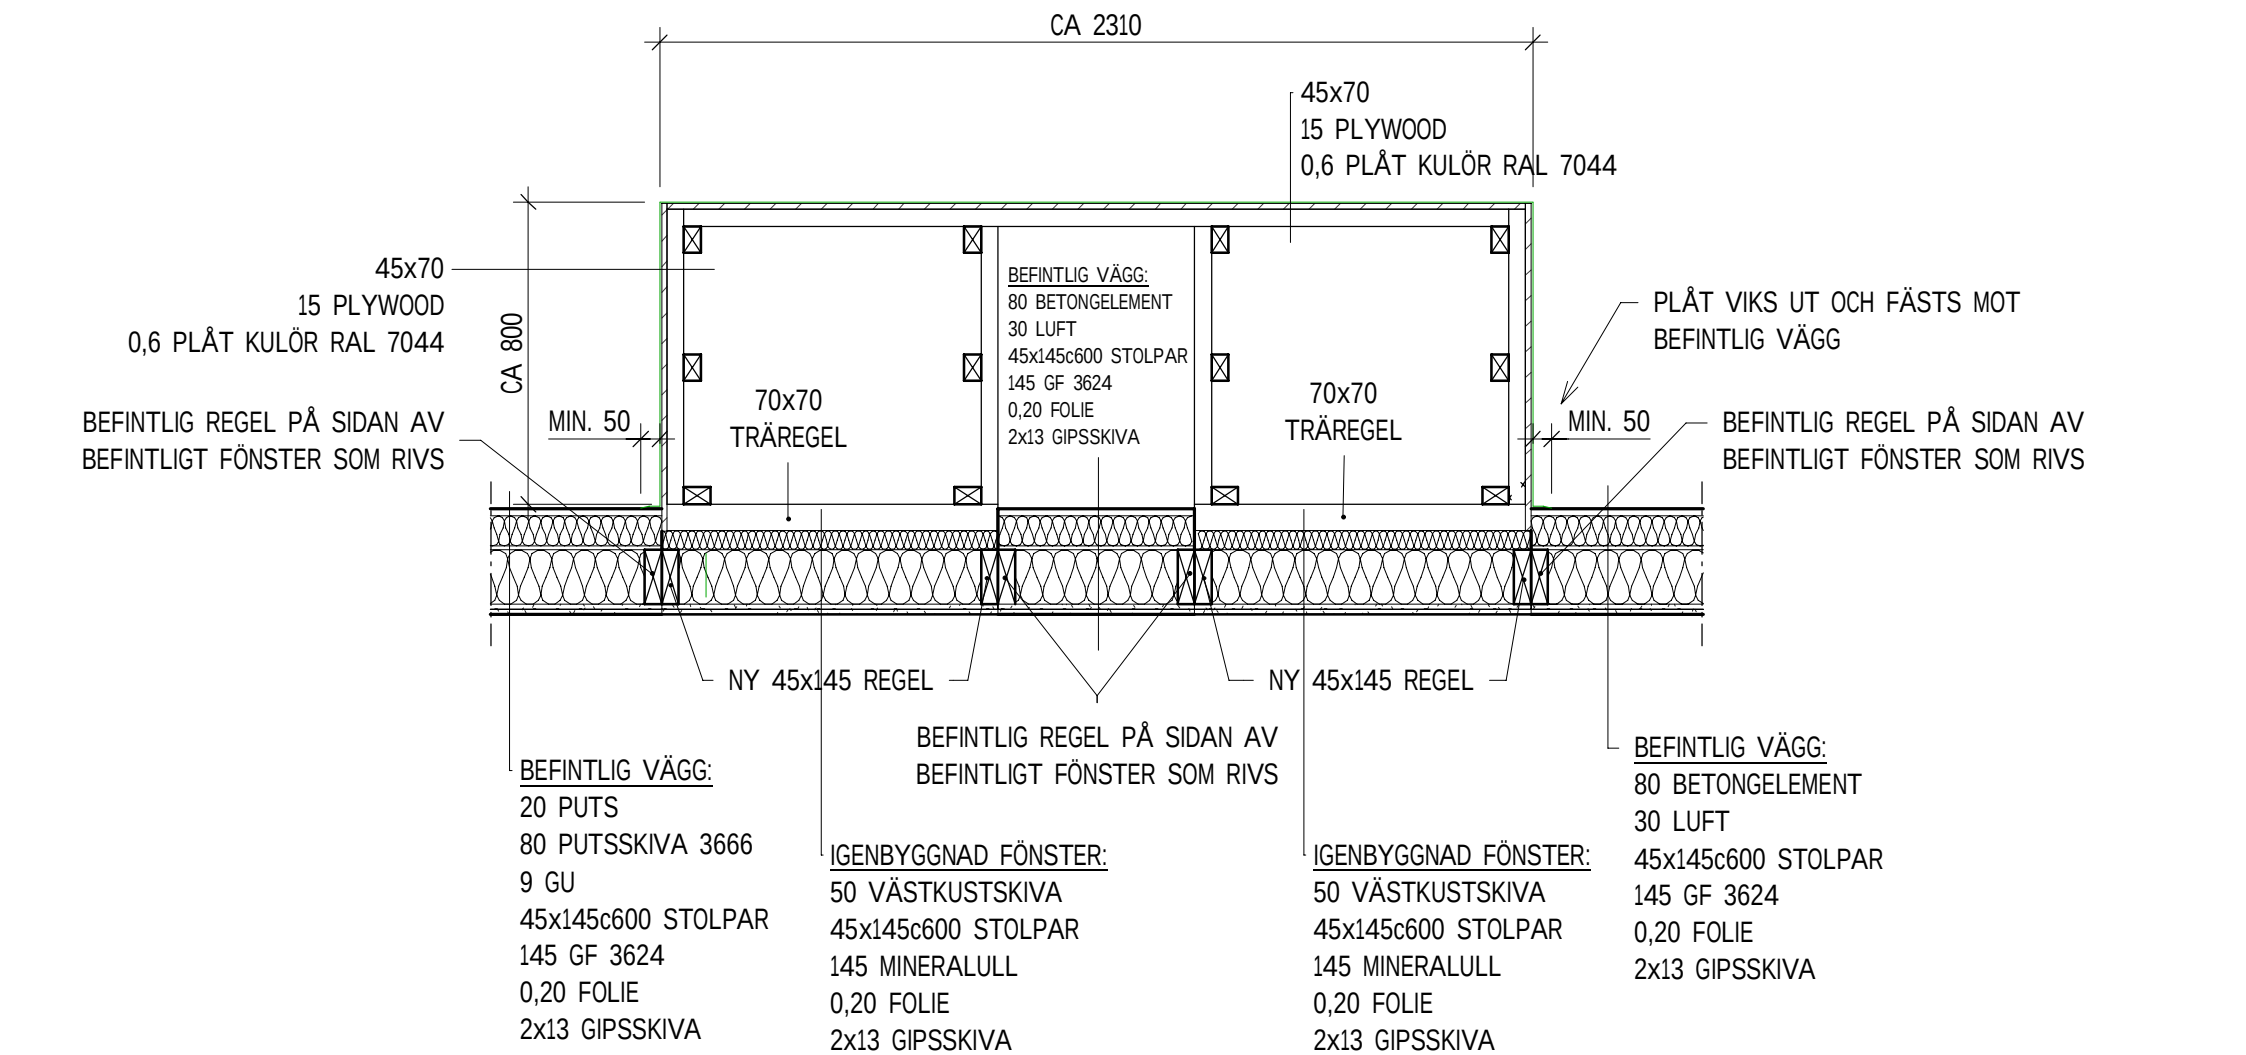

IGENBYGGNAD MOT UC, PLAN
1:20

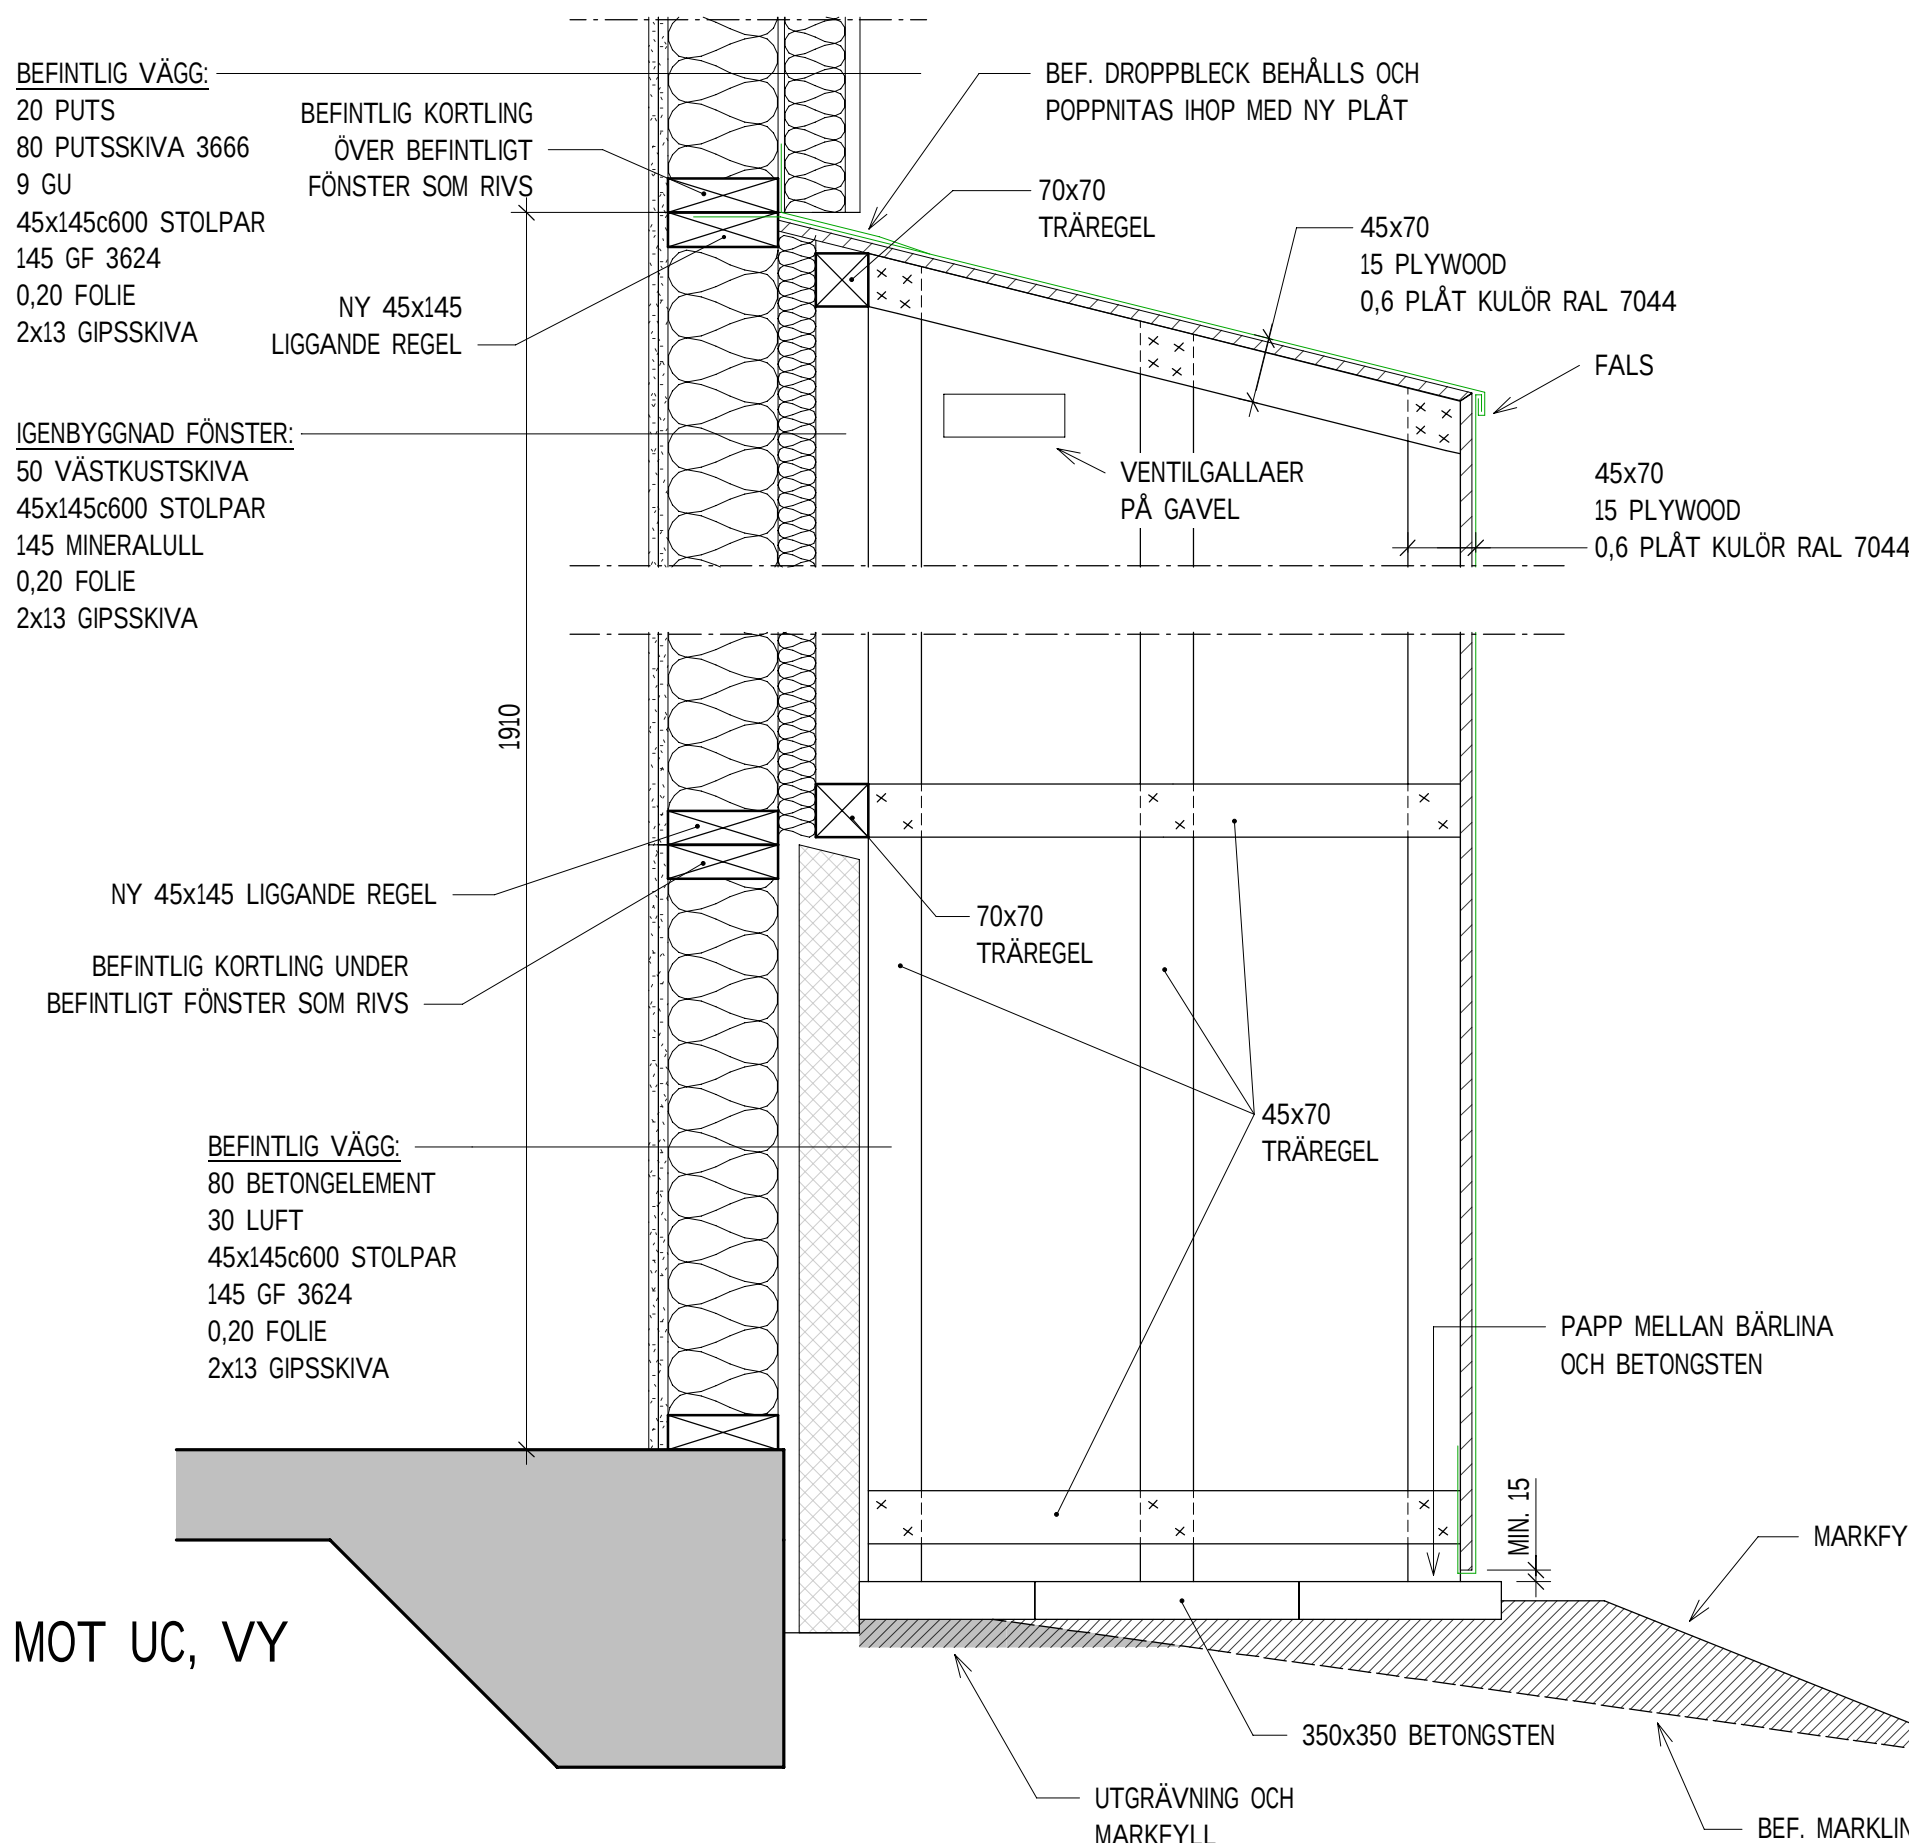

IGENBYGGNAD MOT UC, VY
1:10

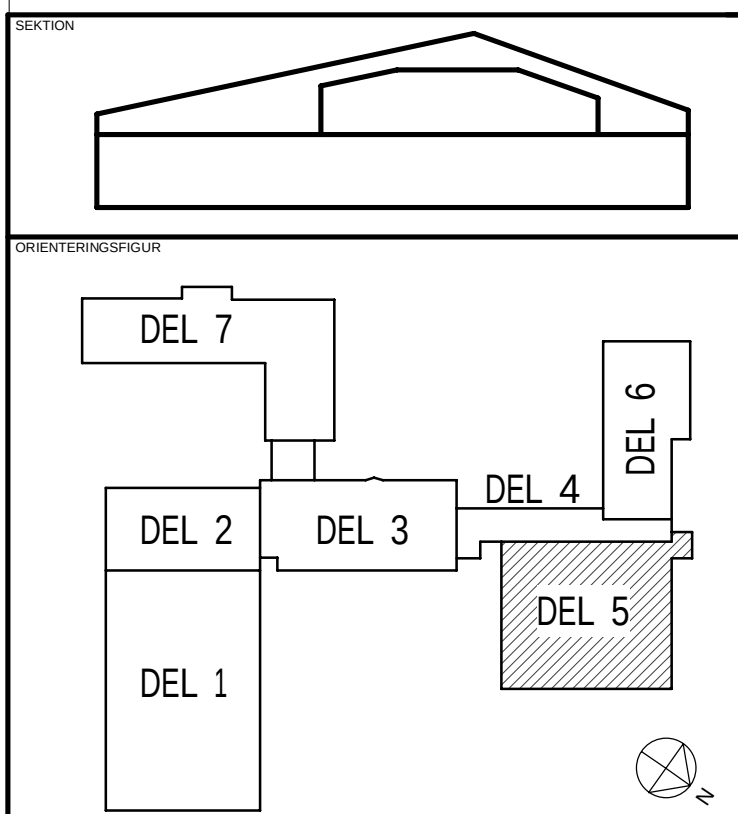

STATUS: FÖRFRÅGNINGSUNDERLAG
HANDLING: BYGGHANDLING
DATUM: 2024-12-20
FÖRBEREDAV: T. BERGSTRÖM
ADRESS: PM



PROJEKTNAMN: CENTRAKÖK
CONTRAGE: ROBERTSFORS KOMMUN

PROJEKTNUMMER: YTTRE RINGVÄGEN 4
DIARIENUMMER: FASTISST: FORDONET 1

DISCIPLIN: A
FÖRETAG: NORCONSULT SVERIGE AB
UPPGÄRDSNUMMER: 108 83 71
FÖRETAGS: SKAPAD AV: CHE

TELEFON: 010 141 80 00
KONTAKTPERSON: TOMAS BERGSTRÖM
BYGGNADSTYP: FÖRSTAD (VIT 2008)

VÄNINGSPLAN: VÄNINGSRELL: DELOMRÅDE: 42 YTTRE VÄGG

SYSTEM: YTTRE VÄGGSDETALJER
SPECIFIKATION: DETALJ
SKALA: 1:5
FORMAT: A1
ANORDNING: A-42-6-002

SKALA 1:5 0 100 500 MILLIMETER