FÖRKLARINGAR

Undertakshöjder anges i millimeter ÖFG.
OBS! Beakta nivåskillnader och förändring av plushöjder vid montering.

TA = Takanslutning

= Kyl-/frysrumstak

= Ventilationdon enl. V

= Armaturer enl. EL

= Undertaksplatta som ej clipsas fast, för enkel demontering

= Luftridå enl. VS

HÄNVISNINGAR

PLAN - ÖVERSIKT, BRAND	A-40-1-100
UNDERTAKSDETALJER	A-43-6-011

FÖRESKRIFTER

Undertak av fabr. Ecophon eller likv.
Bärverk- och bärverksinfästning skall demonteras så att armaturskenor och armatur kan infästas.
Undertaksmontör skall utföra all håltagning för ventilation, armaturer, rör etc. i undertak.
Mängder framräknas från installationsritningar.

Anslutningsdetaljer som inte är redovisade skall utföras enligt undertaksleverantörens anvisningar.

UNDERTAKSTYPER:

TYP UT1: Demonterbart undertak Ecophon Hygiene Preformance Kant A.
Ytskikt Akutex HS, KULÖR: White 500 (NCS S 0500-N).
FORMAT: 600x600x20 mm
TAKHÖJD: Nedpendlat enl. planritning.
SYNLIGT BÄRVERK: Connect T24 C3, KULÖR: Vit 01.
ABSORBTIONSKLASS: A
MONTAGESÄTT: M395C3
Connect avslutningslist mot väggar, balkar och pelare.
Undertaksplattor clipsas enl. fabr. anvisningar där ej annat anges.

TYP UT2: Demonterbart undertak Ecophon Focus Kant A.
Ytskikt Akutex FT, KULÖR: White Frost (NCS S 0500-N).
FORMAT: 600x600x20 mm
TAKHÖJD: Nedpendlat enl. planritning.
SYNLIGT BÄRVERK: Connect T24, KULÖR: Vit 01.
ABSORBTIONSKLASS: A
MONTAGESÄTT: M01
Connect vägglist mot väggar, balkar och pelare.

TYP UT3: Demonterbart undertak Ecophon Focus Kant E.
Ytskikt Akutex FT, KULÖR: White Frost (NCS S 0500-N).
FORMAT: 600x600x20 mm
TAKHÖJD: Nedpendlat enl. planritning.
SYNLIGT BÄRVERK: Connect T24, KULÖR: Vit 01.
ABSORBTIONSKLASS: A
MONTAGESÄTT: M12
Connect skugglist mot väggar, balkar och pelare.

TYP UT4: Demonterbart undertak Ecophon Master Kant E.
Ytskikt Akutex FT, KULÖR: White Frost (NCS S 0500-N).
FORMAT: 600x600x40 mm
TAKHÖJD: Nedpendlat enl. planritning
SYNLIGT BÄRVERK: Connect T24, KULÖR: Vit 01.
ABSORBTIONSKLASS: A
MONTAGESÄTT: M12
Connect skugglist mot väggar, balkar och pelare.

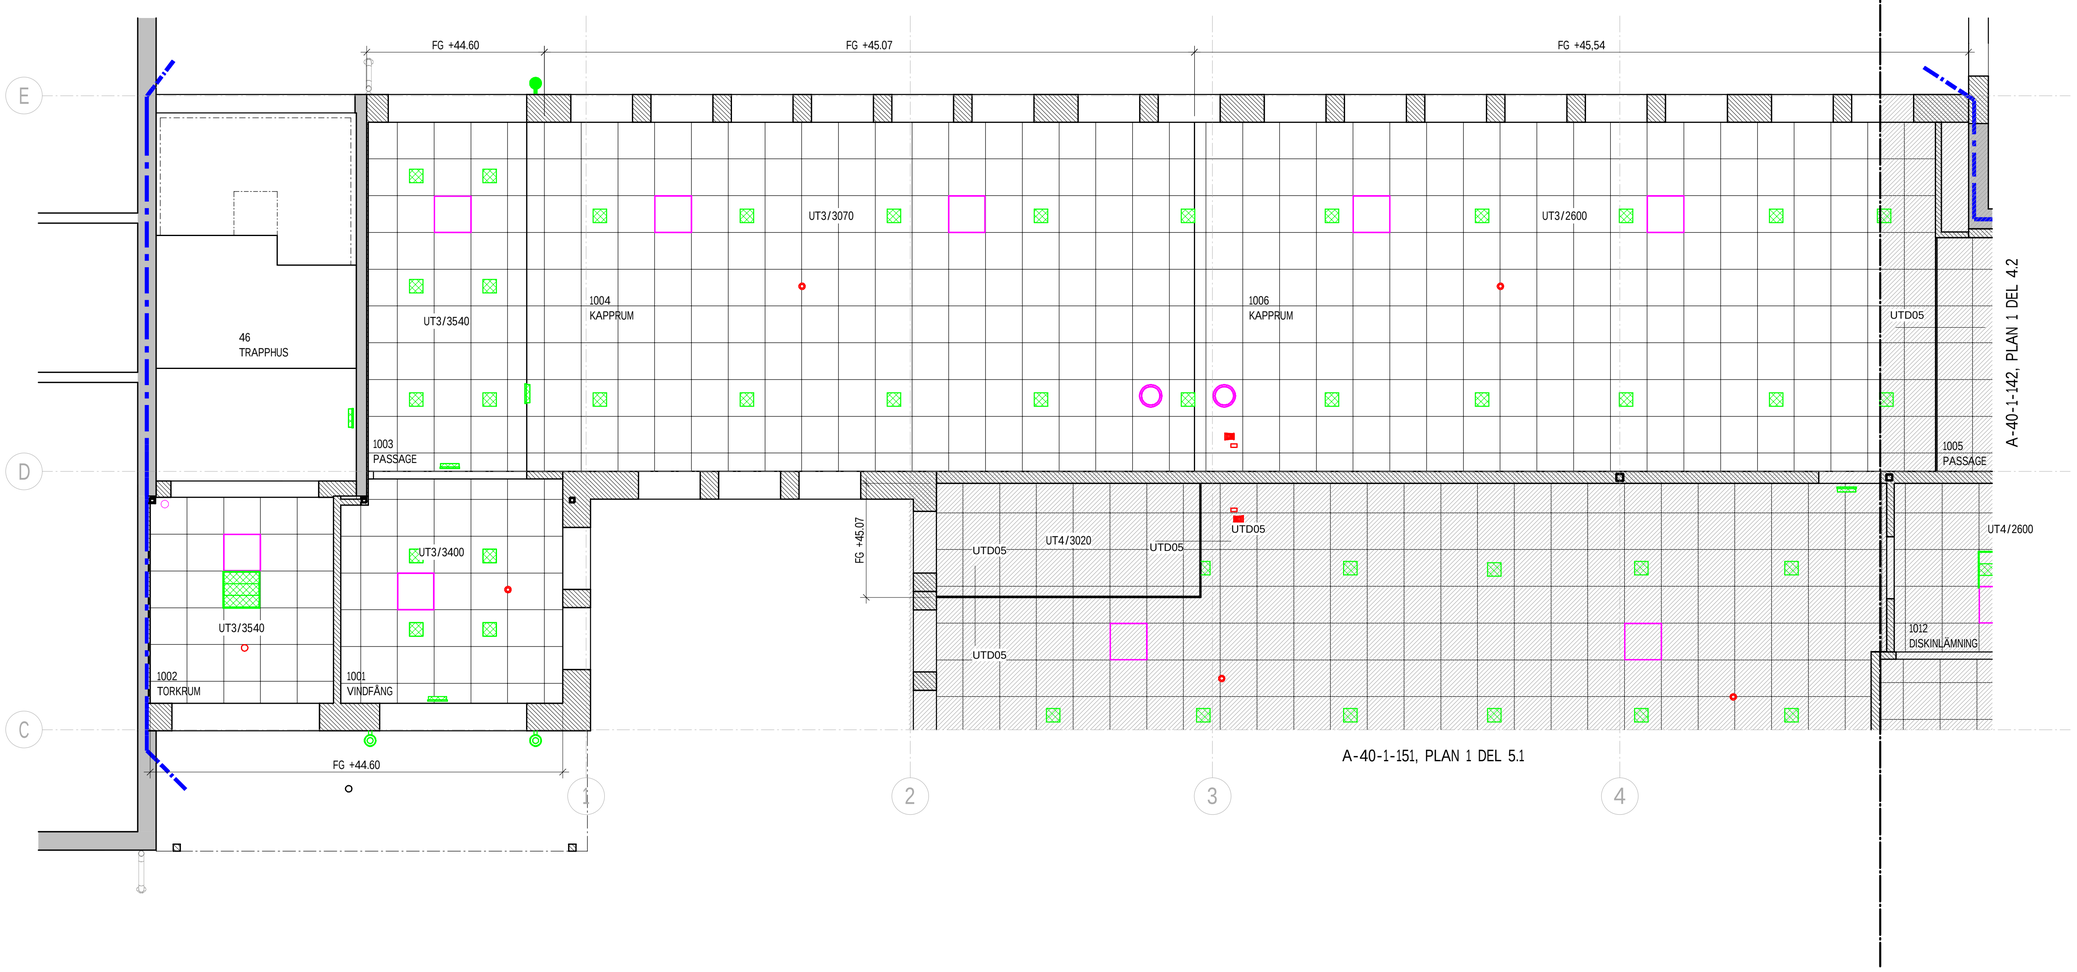

SKALA 1:50 0 1 5 METER

RITNING KRÄVER FÄRGUTSKRIFT FÖR KORREKT UTSEENSE

SEKTION

ORIENTERINGSFIGUR

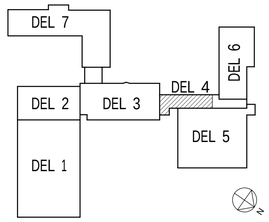

STATUS
FÖRFRÅGNINGSUNDERLAG

HANDLING
BYGGHANDLING

DATUM	GODKÄND AV	ÄNDRINGS PM
2024-12-20	T. BERGSTRÖM	

BESTÄLLARE
ROBERTSFORS KOMMUN

PROJEKTNAMN
CENTRALKÖK

OMRÅDE
ROBERTSFORS KOMMUN

PROJEKTNUMMER	ADRESS: YTTRE RINGVÄGEN 4
DIARIENUMMER	FASTIGHET: FORDONET 1
DISCIPLIN: A	FÖRETAG: NORCONSULT SVERIGE AB
UPPRAGSNUMMER: 108 83 71	SKAPAD AV: SBS
TELEFON: 010 141 80 00	KONTAKTPERSON: TOMAS BERGSTRÖM
BYGGNADSVERK	PLUSHÖJD (RH 2000): +44.60, +45.07, +45.54 (FG)
VÅNINGSPLAN: 1 / VÅNINGSDEL	DELOMRÅDE: DEL 4.1

SYSTEM
43 INRE RUMSBILDANDE BYGGDELAR

SPECIFIKATION
PLAN 1 UNDERTAK, DEL 4.1

RITNINGSKATEGORI	SKALA	FORMAT
PLAN	1:50	A1

DOKUMENTNUMMER: A-43-1-141
ÄNDRING:

2024-12-20 12:06:41

FILNAMN: C:\Norconsult\Autodesk\Rev\t1088371-Centralkök Robertsfors_centralli-2024_malsta.rvt