

FÖRKLARINGAR

Undertakshöjder anges i millimeter ÖFG.
OBS! Beakta nivåskillnader och förändring av plus-
höjder vid montering.

- TA

= Takanslutning
- = Kyl-/frysrumstak
- = Ventilationsdon enl. V
- = Armaturer enl. EL
- = Undertaksplatta som ej
clipsas fast, för enkel
demontering
- = Luftridå enl. VS

HÄNVISNINGAR

PLAN - ÖVERSIKT, BRAND
UNDERTAKSDETALJER

A-40-1-100
A-43-6-011

FÖRESKRIFTER

Undertak av fabr. Ecophon eller likv.
Bärverk- och bärverksinfästning skall demonteras
så att armaturskenor och armatur kan infästas.
Undertaksmontör skall utföra all håltagning för
ventilation, armaturer, rör etc. i undertak.
Mängder framräknas från installationsritningar.

Anslutningsdetaljer som inte är redovisade skall utföras
enligt undertaksleverantörens anvisningar.


UNDERTAKSTYPER:

TYP UT1: Demonterbart undertak Ecophon Hygiene
Performance Kant A.
Ytskikt Akutex HS, KULÖR: White 500 (NCS S 0500-N).
FORMAT: 600x600x20 mm
TAKHÖJD: Nedpendlat enl. planritning.
SYNLIGT BÄRVERK: Connect T24 C3, KULÖR: Vit 01.
ABSORBTIONSKLASS: A
MONTAGESÄTT: M395C3
Connect avslutningslist mot väggar, balkar och pelare.
Undertaksplattor clipsas enl. fabr. anvisningar där ej annat
anges.


TYP UT2: Demonterbart undertak Ecophon Focus Kant A.
Ytskikt Akutex FT, KULÖR: White Frost (NCS S 0500-N).
FORMAT: 600x600x20 mm
TAKHÖJD: Nedpendlat enl. planritning.
SYNLIGT BÄRVERK: Connect T24, KULÖR: Vit 01.
ABSORBTIONSKLASS: A
MONTAGESÄTT: M01
Connect vägglist mot väggar, balkar och pelare.

TYP UT3: Demonterbart undertak Ecophon Focus Kant E.
Ytskikt Akutex FT, KULÖR: White Frost (NCS S 0500-N).
FORMAT: 600x600x20 mm
TAKHÖJD: Nedpendlat enl. planritning.
SYNLIGT BÄRVERK: Connect T24, KULÖR: Vit 01.
ABSORBTIONSKLASS: A
MONTAGESÄTT: M12
Connect skugglist mot väggar, balkar och pelare.

TYP UT4: Demonterbart undertak Ecophon Master Kant E.
Ytskikt Akutex FT, KULÖR: White Frost (NCS S 0500-N).
FORMAT: 600x600x40 mm
TAKHÖJD: Nedpendlat enl. planritning
SYNLIGT BÄRVERK: Connect T24, KULÖR: Vit 01.
ABSORBTIONSKLASS: A
MONTAGESÄTT: M12
Connect skugglist mot väggar, balkar och pelare.

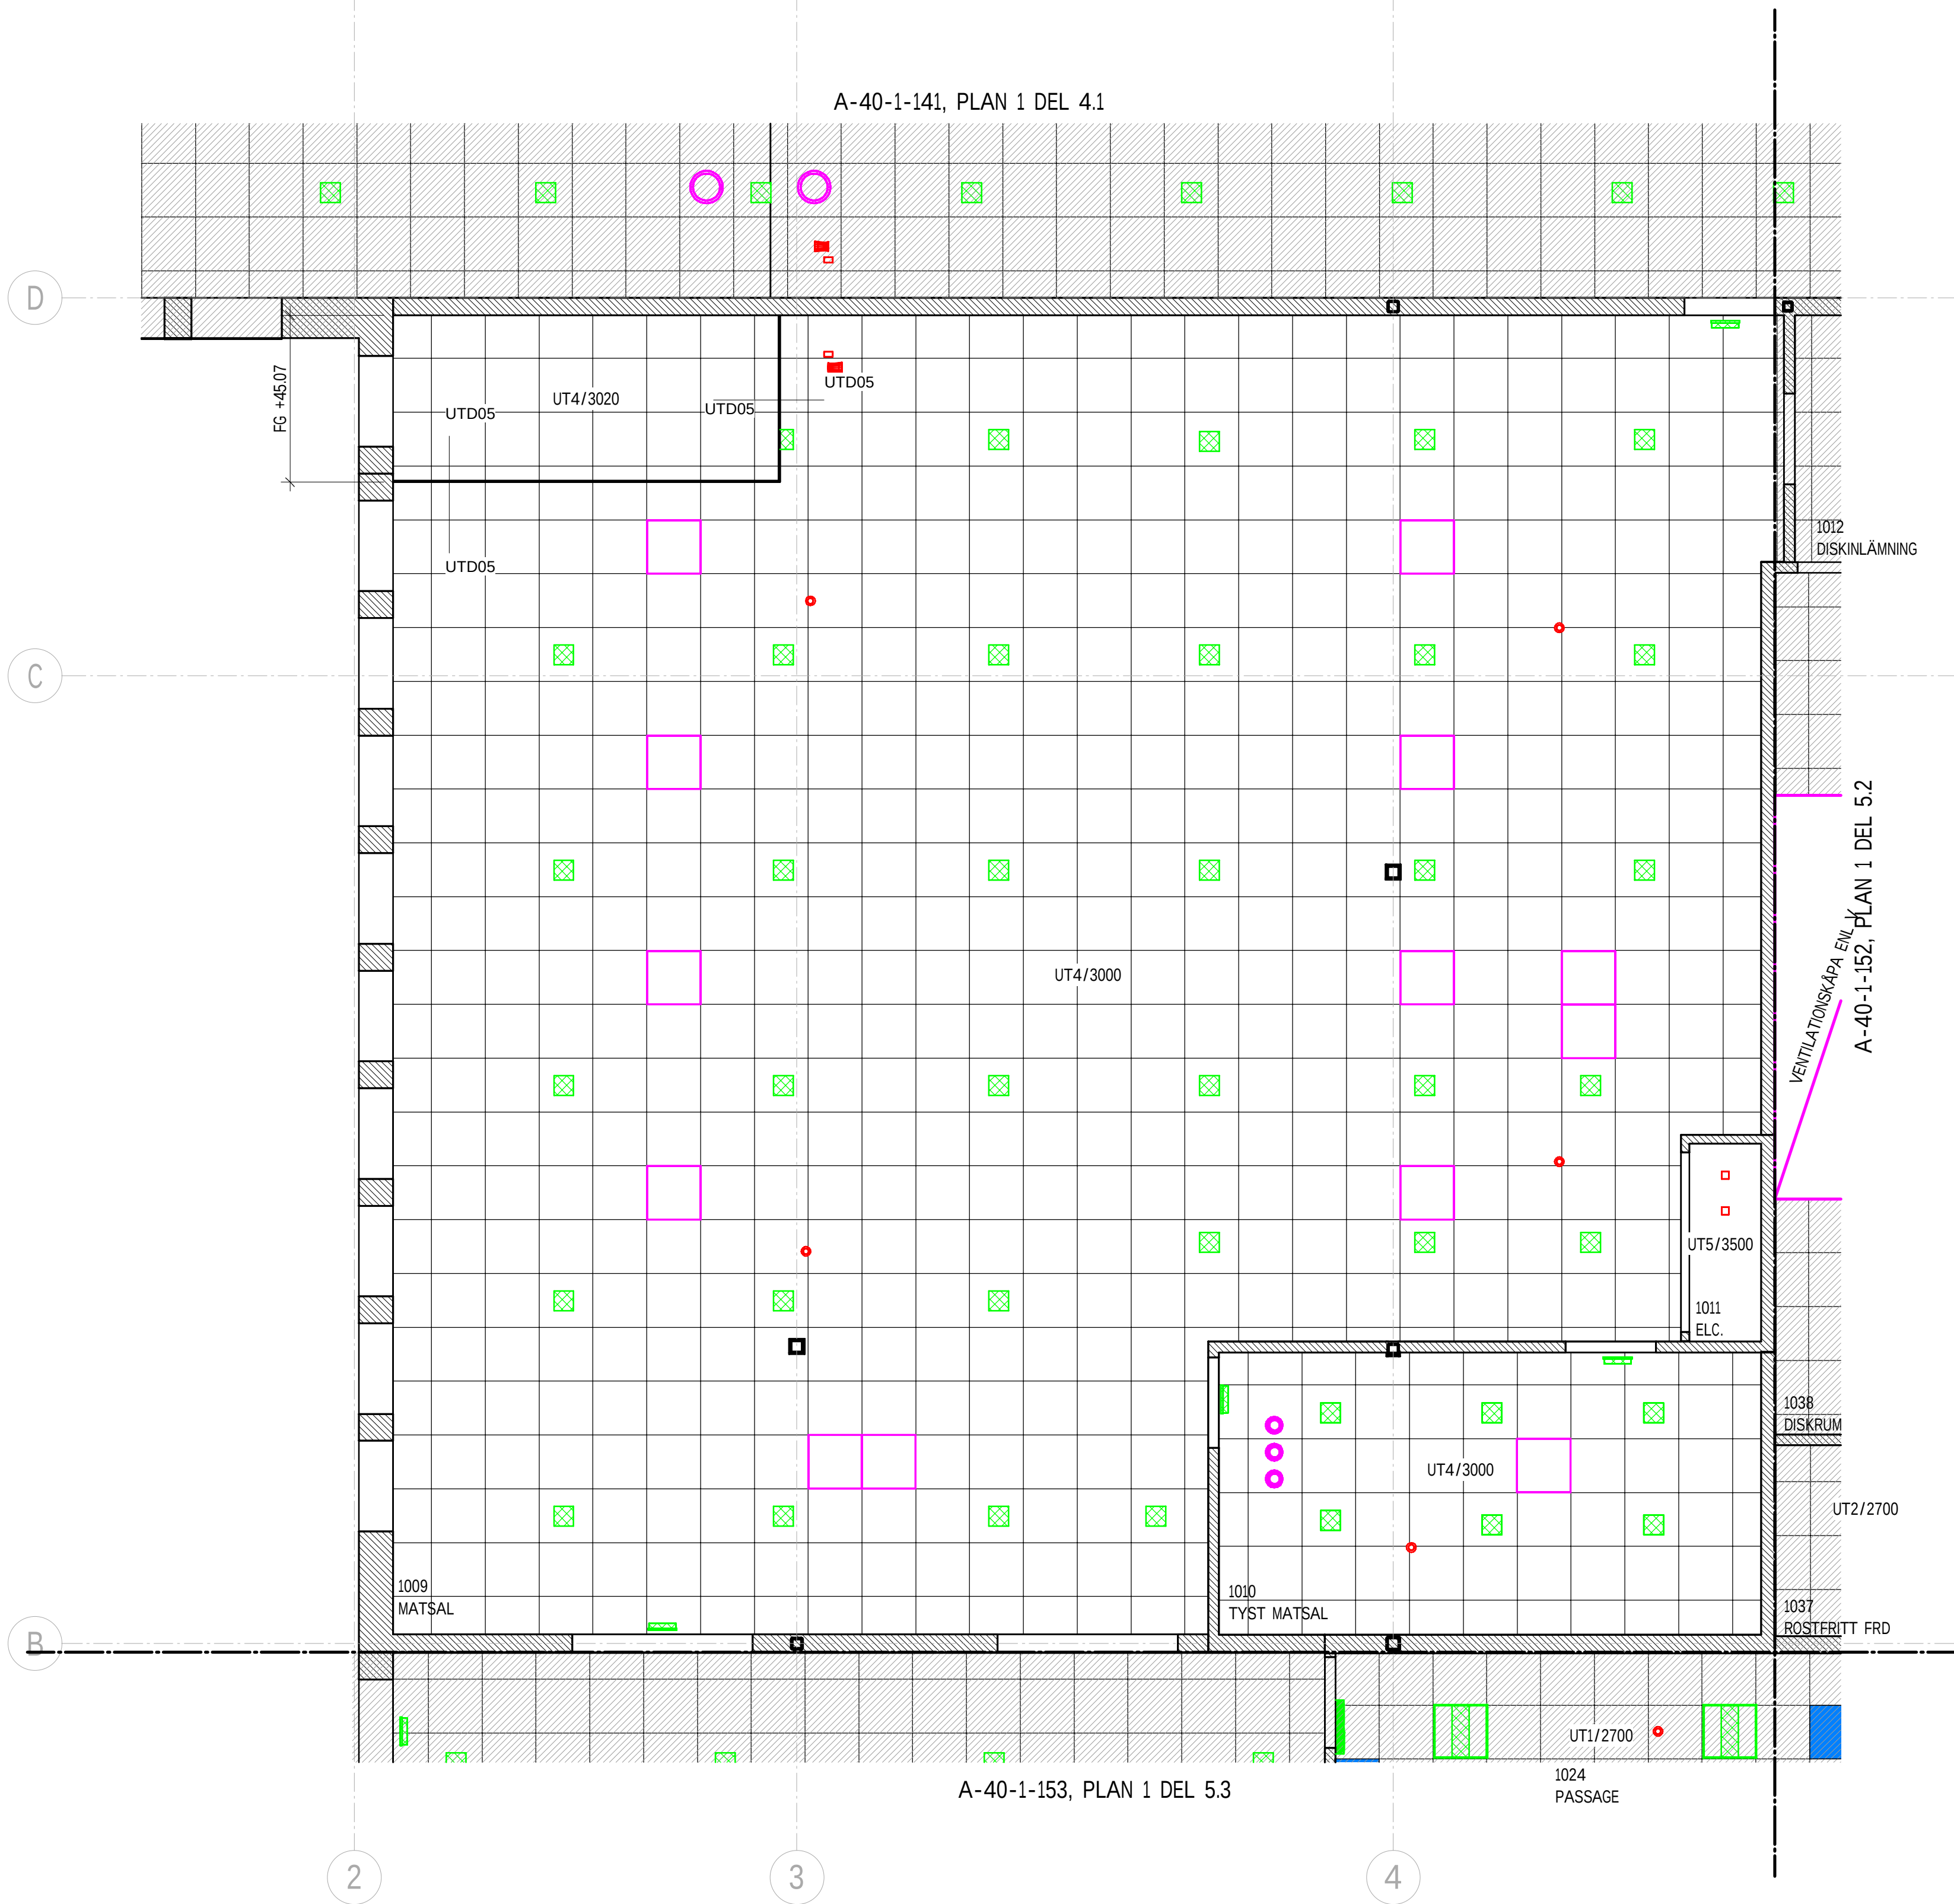

RITEGNING KRÄVER FÄRGUTSKRIFT FÖR KORREKT UTSEENSE

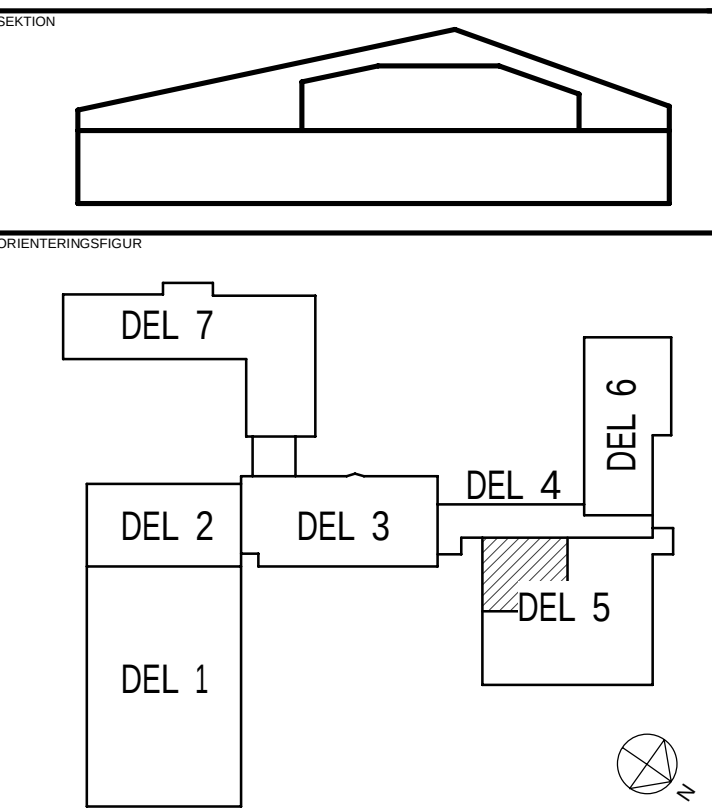

STATUS
FÖRFRÅGNINGSUNDERLAG

HANDLING
BYGGHANDLING

DATUM
2024-12-20

UTARBETAD AV
T. BERGSTRÖM

ANSVARIG PM



PROJEKTNAMN			
CENTRALKÖK			
OMFÄTTE			
ROBERTSFORS KOMMUN			
PROJEKTNUMMER		ADRESS	
		YTTRE RINGVÄGEN 4	
DOKUMENTNUMMER		FASTIGHET	
		FORDONET 1	
DISCIPLIN		FÖRETAG	
A		NORCONSULT SVERIGE AB	
UPPRORSGRUPPNUMMER		SKAPAD AV	
108 83 71		SBS	
TELEFON		KONTAKTPERSON	
010 141 80 00		TOMAS BERGSTRÖM	
BYGGNADSTYP		KÖLÖR/ÖFÖRÖR	
		PLUSGUDEN (RH 2003)	
		+45.07, +45.54 (FG)	
VÄRNINGSPÅN		DELÖMÅDE	
1		DEL 5.1	
SYSTEM			
43 INRE RUMSBILDANDE BYGGDELAR			
SPECIFIKATION			
PLAN 1 UNDERTAK, DEL 5.1			
TEGNINGSKATEGORI		SKALA	FORMAT
PLAN		1:50	A1
DOKUMENTNUMMER		ANSVARIG	
A-43-1-151			