

FÖRKLARINGAR

Undertakshöjder anges i millimeter ÖFG.
OBS! Beakta nivåskillnader och förändring av plus-
höjder vid montering.

- TA

= Takanslutning
- = Kyl-/frysrumstak
- = Ventilationsdon enl. V
- = Armaturer enl. EL
- = Undertaksplatta som ej
clipsas fast, för enkel
demontering
- = Luftridå enl. VS

HÄNVISNINGAR

PLAN - ÖVERSIKT, BRAND
UNDERTAKSDETALJER

A-40-1-100
A-43-6-011

FÖRESKRIFTER

Undertak av fabr. Ecophon eller likv.
Bärverk- och bärverksinfästning skall demonteras
så att armaturskenor och armatur kan infästas.
Undertaksmontör skall utföra all håltagning för
ventilation, armaturer, rör etc. i undertak.
Mängder framräknas från installationsritningar.

Anslutningsdetaljer som inte är redovisade skall utföras
enligt undertaksleverantörens anvisningar.


UNDERTAKSTYPER:

TYP UT1: Demonterbart undertak Ecophon Hygiene
Performance Kant A.
Ytskikt Akutex HS, KULÖR: White 500 (NCS S 0500-N).
FORMAT: 600x600x20 mm
TAKHÖJD: Nedpendlat enl. planritning.
SYNLIGT BÄRVERK: Connect T24 C3, KULÖR: Vit 01.
ABSORBTIONSKLASS: A
MONTAGESÄTT: M395C3
Connect avslutningslist mot väggar, balkar och pelare.
Undertaksplattor clipsas enl. fabr. anvisningar där ej annat
anges.


TYP UT2: Demonterbart undertak Ecophon Focus Kant A.
Ytskikt Akutex FT, KULÖR: White Frost (NCS S 0500-N).
FORMAT: 600x600x20 mm
TAKHÖJD: Nedpendlat enl. planritning.
SYNLIGT BÄRVERK: Connect T24 C3, KULÖR: Vit 01.
ABSORBTIONSKLASS: A
MONTAGESÄTT: M01
Connect vägglist mot väggar, balkar och pelare.

TYP UT3: Demonterbart undertak Ecophon Focus Kant E.
Ytskikt Akutex FT, KULÖR: White Frost (NCS S 0500-N).
FORMAT: 600x600x20 mm
TAKHÖJD: Nedpendlat enl. planritning.
SYNLIGT BÄRVERK: Connect T24 C3, KULÖR: Vit 01.
ABSORBTIONSKLASS: A
MONTAGESÄTT: M12
Connect skugglist mot väggar, balkar och pelare.

TYP UT4: Demonterbart undertak Ecophon Master Kant E.
Ytskikt Akutex FT, KULÖR: White Frost (NCS S 0500-N).
FORMAT: 600x600x40 mm
TAKHÖJD: Nedpendlat enl. planritning
SYNLIGT BÄRVERK: Connect T24 C3, KULÖR: Vit 01.
ABSORBTIONSKLASS: A
MONTAGESÄTT: M12
Connect skugglist mot väggar, balkar och pelare.

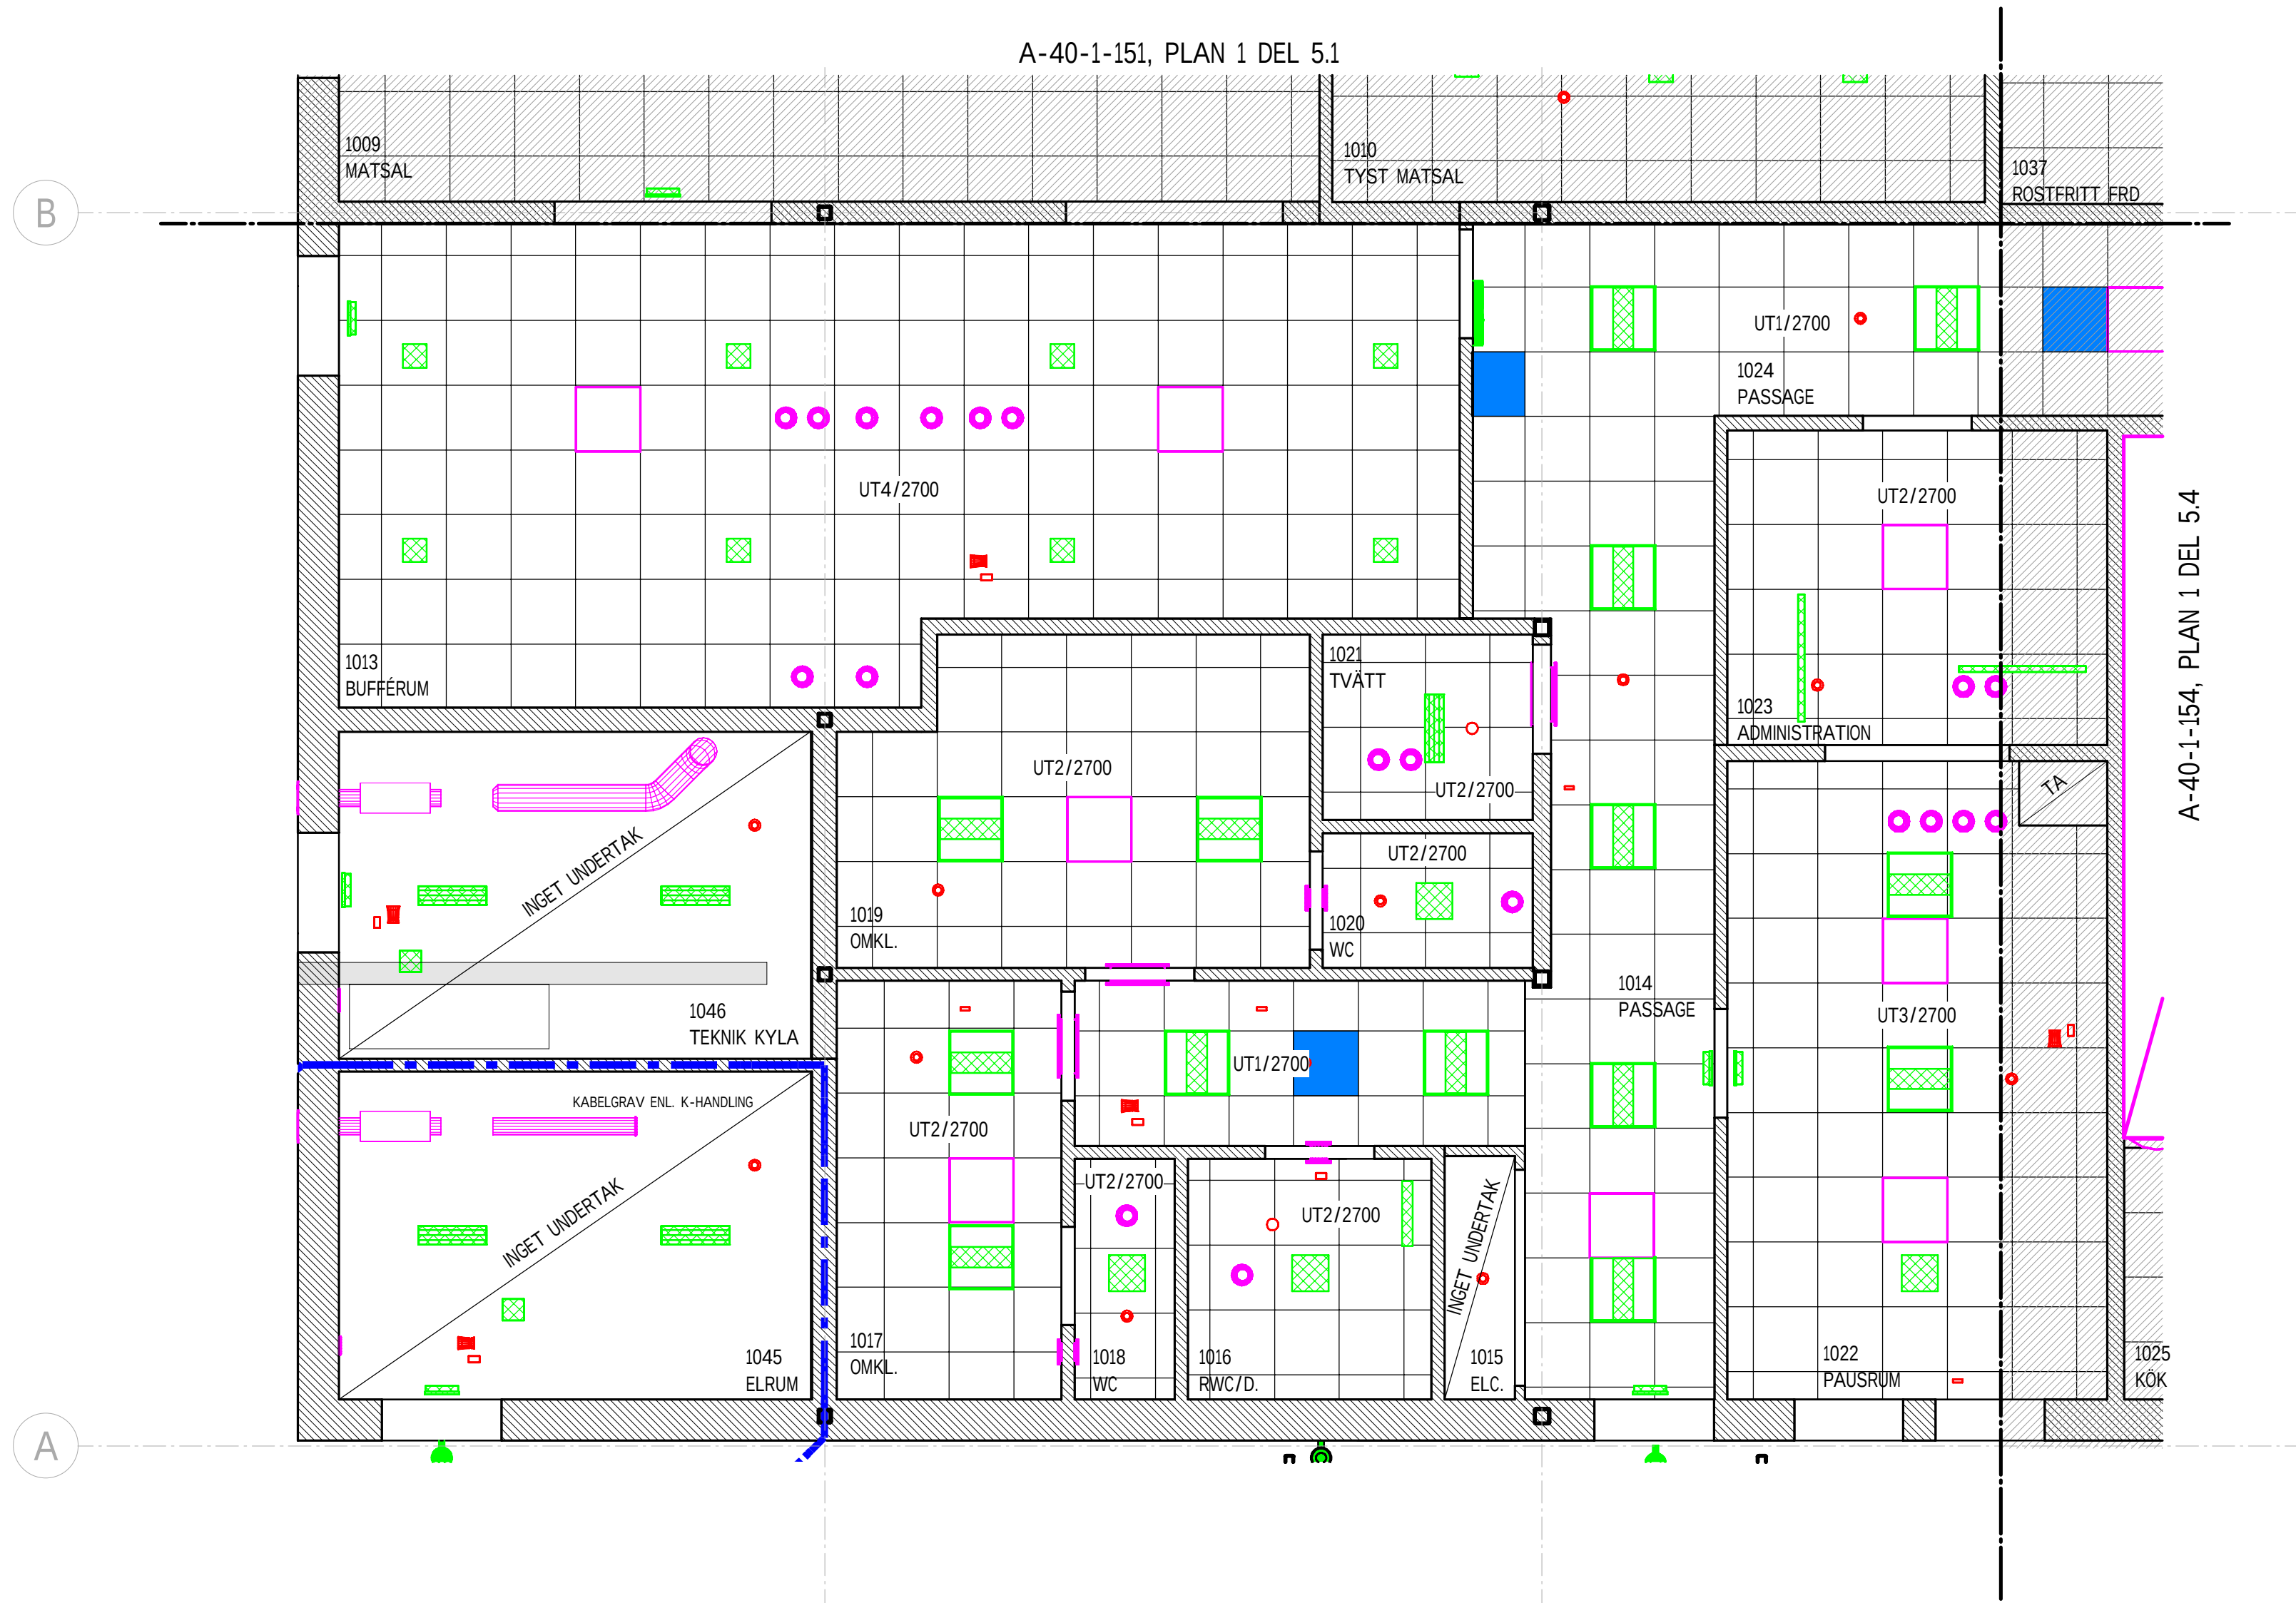

RITEG KRAVER FÄRGUTSKRIFT FÖR KORREKT UTSEENSE

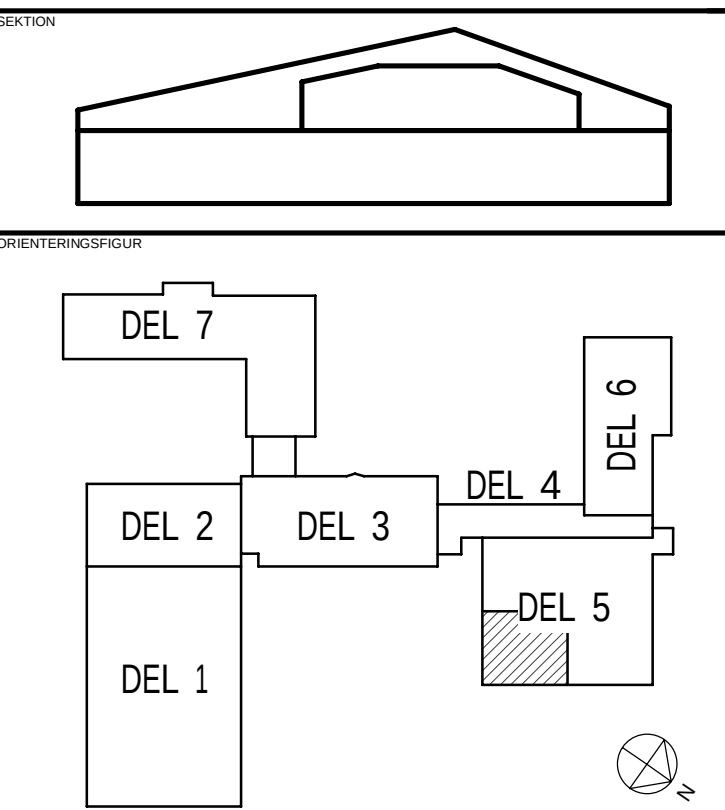

STATUS

FÖRFRÅGNINGSUNDERLAG

HANDLING

BYGGHANDLING

DATUM 2024-12-20

UTARBETAD AV T. BERGSTRÖM

ADRESSERAD PM

BESTÄLLARE



PROJEKTNAMN

CENTRALEKÖK

OMRÅDE

ROBERTSFORS KOMMUN

PROJEKTNUMMER

ADRESS

YTTRE RINGVÄGEN 4

DIARIENUMMER

FASTIGHET

FORDONET 1

DISCIPLIN

FÖRETAG

NORCONSULT SVERIGE AB

UPPDRAGSRUMMER

SKAPAD AV

108 83 71

SBS

TELEFON

KONTAKTPERSON

010 141 80 00

TOMAS BERGSTRÖM

BYGGNADSTYP

KLIMATKRAV

+45,54 (FG)

VÄNINGSPLAN

VÄNINGSDEL

DEL 5.3

SYSTEM

43 INRE RUMSBILDANDE BYGGDELAR

SPECIFIKATION

PLAN 1 UNDERTAK, DEL 5.3

BYGGNADSTYP

PLAN

SKALA

1:50

FORMAT

A1

BYGGNADSTYP

A-43-1-153

SKALA 1:50 0 1 5 METER