

FÖRKLARINGAR

V = Vänsterhängd
H = Högerhängd
Dörrar ses från gångjärnssidan.
Antal beslag anges per dörrblad.
Alla mått i millimeter.
Yttermått avser väggöppningsmått, där annat ej anges.
Karmar märkes enligt ritningens liltrering, i förekommande fall med tillagt V eller H.
Brand och ljudklassade dörrar märkes enligt gällande normer.
Mått skall kontrolleras på plats före tillverkning.

FÖRESKRIFTER

Sort/Typ
Enligt uppställning.

Tröskel
Enligt uppställning.

Urtag
Karmar förborras för infästning.
Täckproppar i kulör lika karm.

Ytbehandling/Kulör
Karm ytbehandlas på fabrik enl. SS 184280:2013
Kulör karm: Enligt uppställning
Kulör dörrblad: Enligt uppställning

Gångjärn
Enligt fabr. standard.
Fabrikant svarar för dimensionering av antal och storlek på gångjärn.




Låsning
Låschema upprättas av entreprenören i samråd med beställaren.
Cylindrar tillhandahålles av beställaren, monteras av entreprenören.

Övrigt
Karmar skall förse med tätningslister enligt fabr. standard för aktuell ljud och brandklass.
Där ej karndjup överensstämmer med vägg tjocklek utföres salning av MDF - skiva, kulör lika karm.

Dörrar skall som helhet inkl. fastsättningslister etc. uppfylla föreskriven brand- och ljudklass.
Brand- och ljudklassade dörrar skall förse med typgodkännandebevis eller intyg från fabrikanter att partier uppfyller föreskriven brand- och ljudklass.

HÄNVISNINGAR

PLAN 1, DEL 4.2 A-40-1-142
PLAN 1, DEL 5.1 A-40-1-151
PLAN 1, DEL 5.3 A-40-1-153

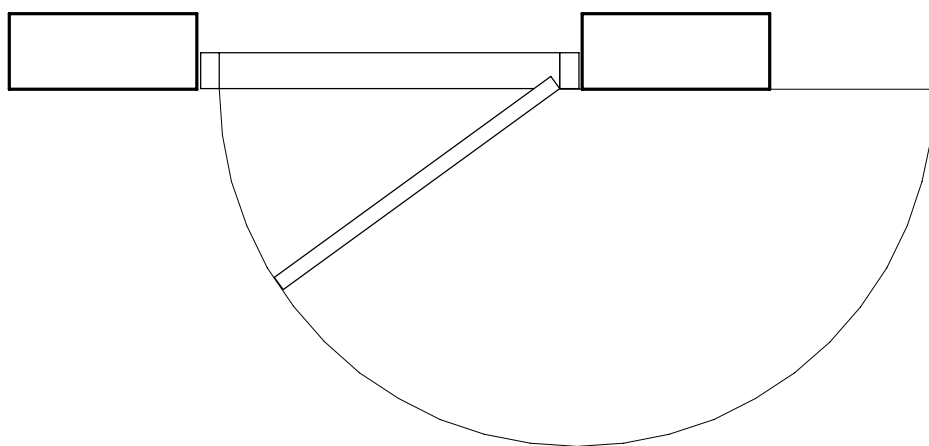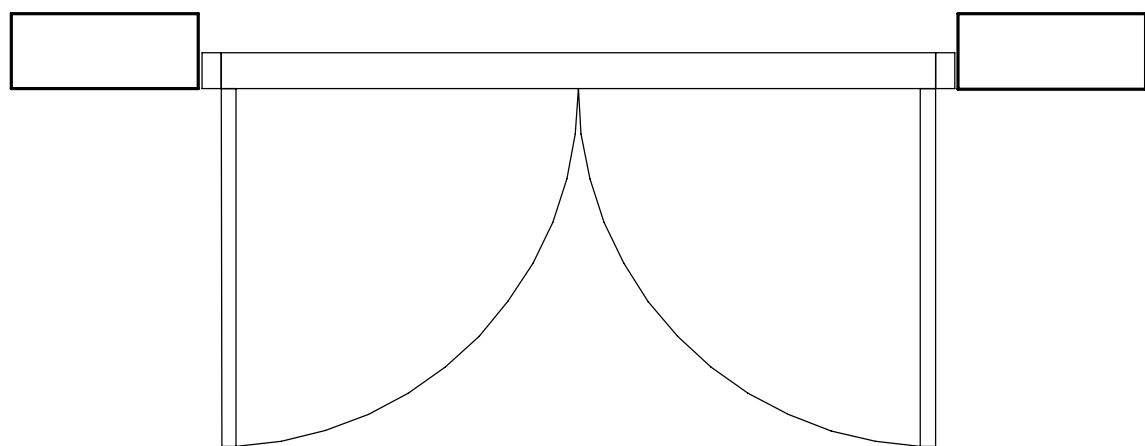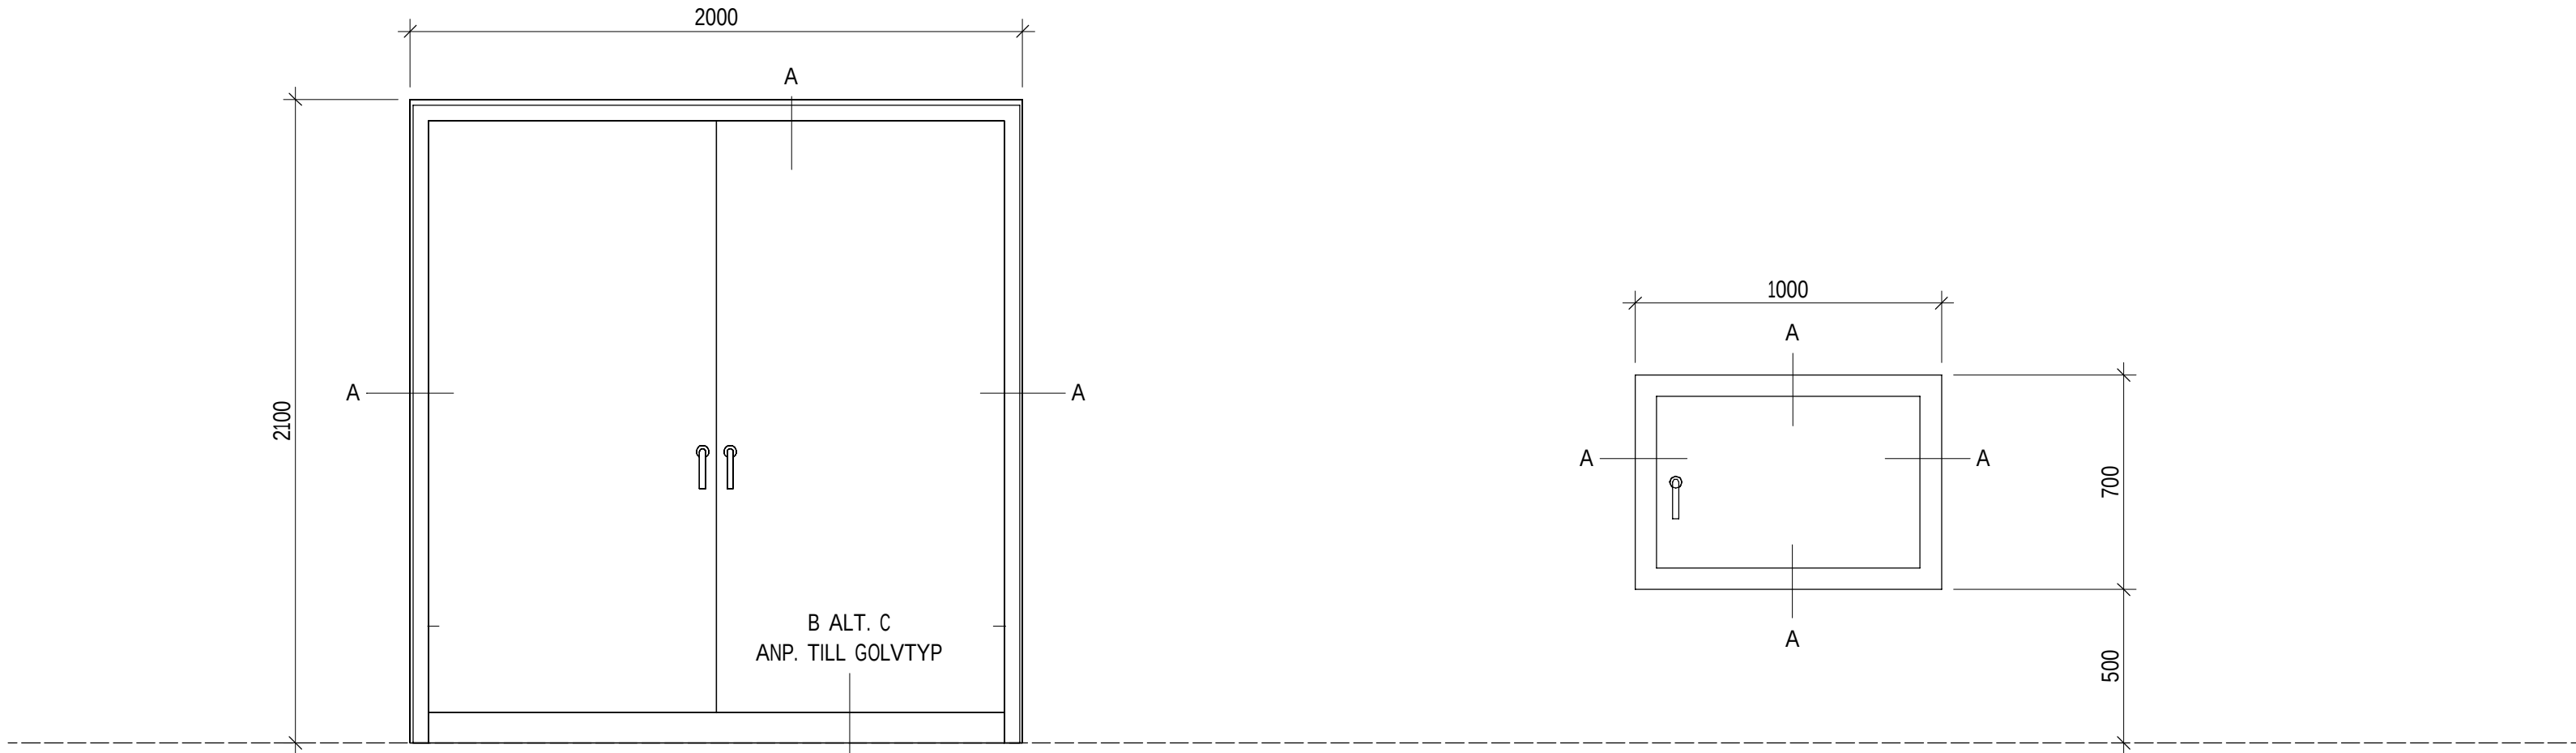


ELC1 ANTAL: 2st
1011, 1015 ELC


Sort/typ: Invändig elcentralfront i trä av fabrikat Skellefteå snickericentral eller likv. Lucktjocklek 19 mm enl. fabr. std.
Tröskel: Enligt detalj B
Karm: Folierad MDF enligt leverantörens standard, 40x92 mm
Kulör karm/dörrblad: NCS S 1002-Y
Lås/cylinder/slutbleck/behör: ASSA 593/ASSA 5801

ELC2 ANTAL: 1st
1005 PASSAGE


Sort/typ: Invändig elcentralfront i trä av fabrikat Skellefteå snickericentral eller likv. Lucktjocklek 19 mm enl. fabr. std.
Tröskel: Enligt detalj A
Karm: Folierad MDF enligt leverantörens standard, 40x92 mm
Kulör karm/dörrblad: NCS S 0500-N
Lås/cylinder/slutbleck/behör: ASSA 593/ASSA 5801

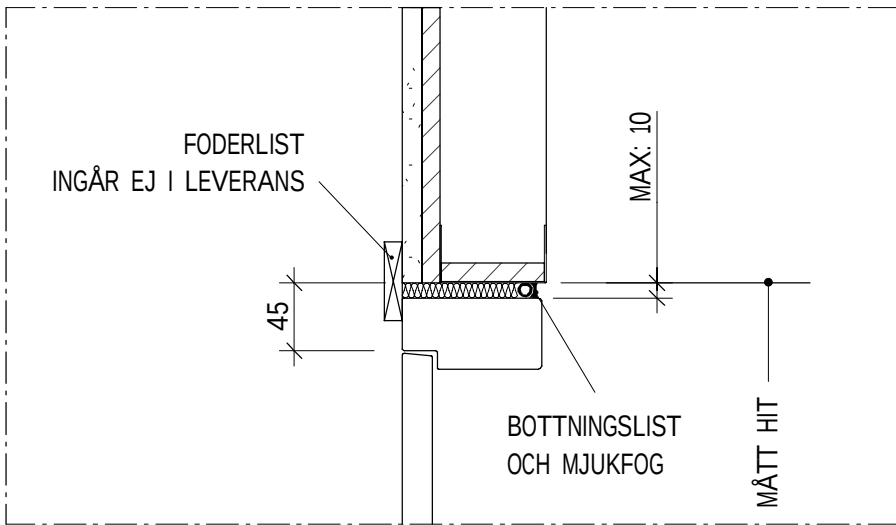

DET.A
1 : 5

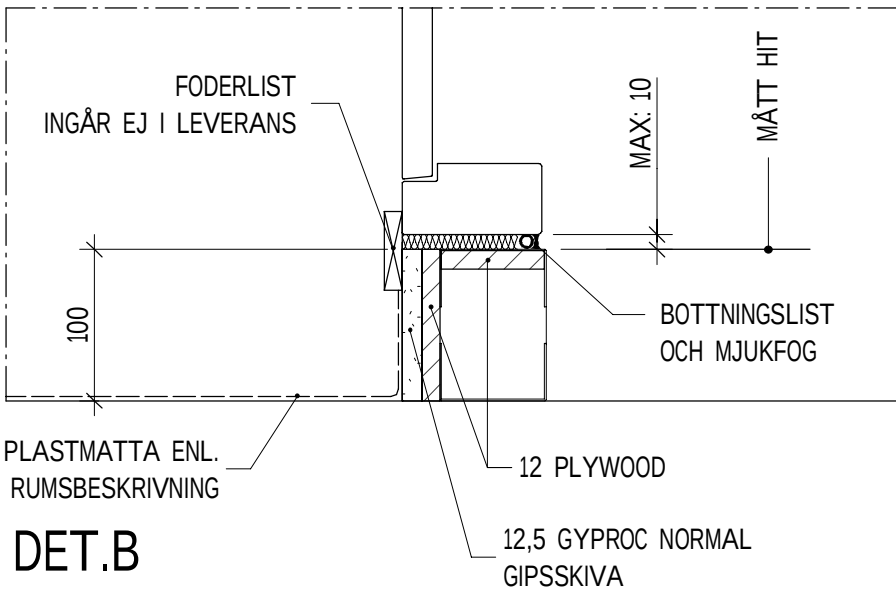

DET.B
1 : 5

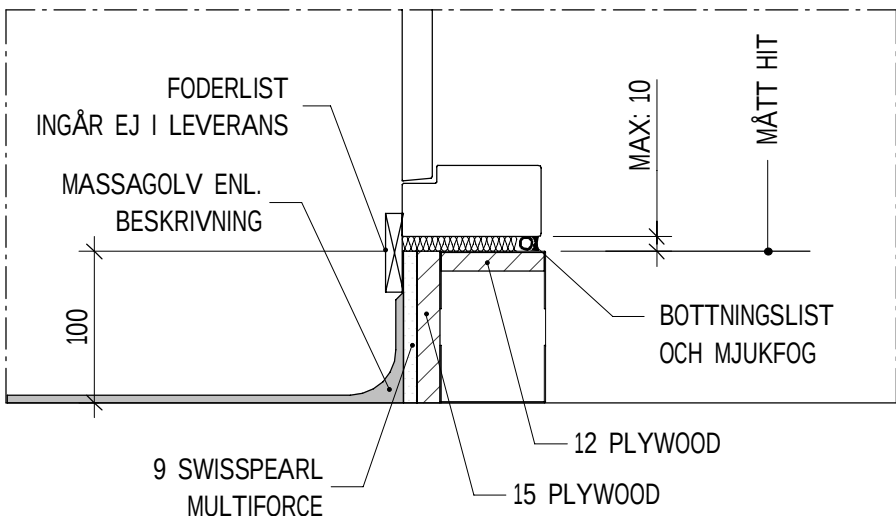

DET.C
1 : 5

SKALA 1:20 0 1 2 METER

SEKTION

ORIENTERINGSKUR

STATUS

HANDLING

DATUM

LOKALISERING

ANSVARIGS PM

BESTÄLLARE

PROJEKTNAMN

KONTRAKT

PROJEKTNUMMER

DIREKTÖRSNUMMER

DISCIPLIN

UPPRORAGSRUMMER

TELEFON

BYGGHÄNSKIV

VÄRNINGSPLAN

VÄRNINGSDI

DELOMRÅDE

SYSTEM

SPECIFIKATION

BYGGHÄNSKIV

UPPSTÄLLNING

SKALA

FORMAT

BYGGHÄNSKIV

FÖRFRÅGNINGSUNDERLAG

BYGGHANDLING

2024-12-20

T. BERGSTRÖM

ANSVARIGS PM

ROBERTSFORS KOMMUN

CENTRALEKÖK

ROBERTSFORS KOMMUN

YTTRE RINGVÄGEN 4

FORDONET 1

NORCONSULT SVERIGE AB

MSR

TOMAS BERGSTRÖM

FLUGHÄNSKIV (VIT 2008)

DELOMRÅDE

43 INRE RUMSBILDANDE BYGGDELAR

ELCENTRALFRONTER

UPPSTÄLLNING

1:5/1:20

A1

A-43-4-041