




INKLÄDNADER

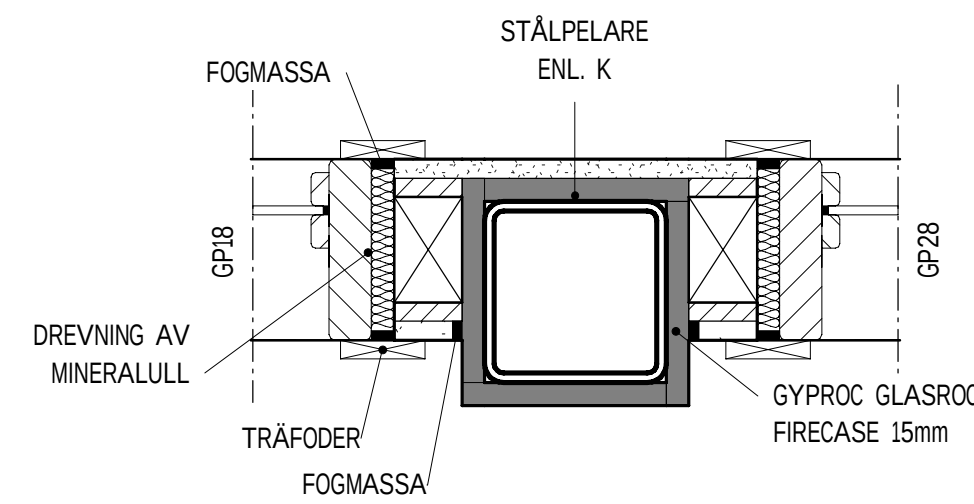


IK1 - STÅLPELARE MELLAN GLASPARTIER
1 : 5

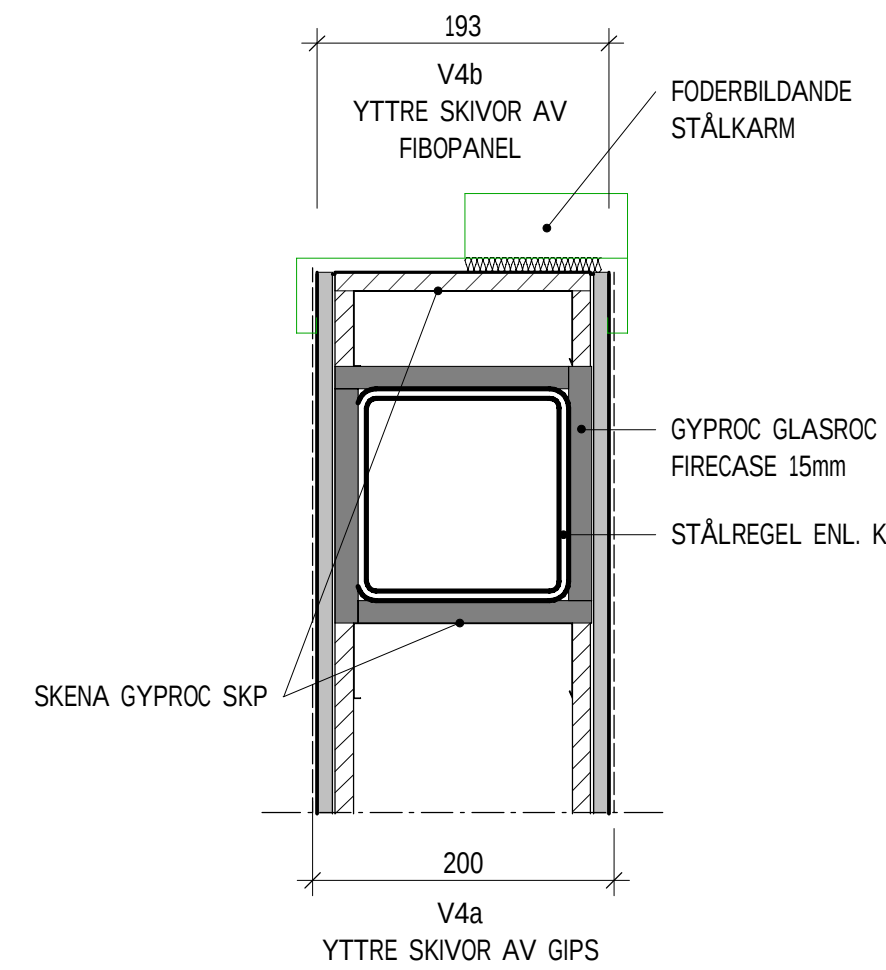


IK2 - STÅLPELARE I INNERVÄGG
1:5

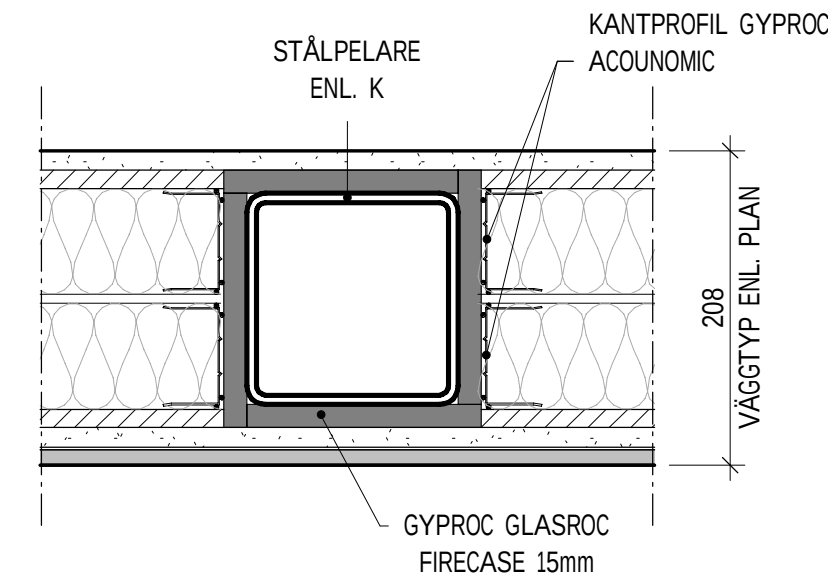


IK3 - STÅLPELARE I DUBBELREGLVÄGG
1 : 5

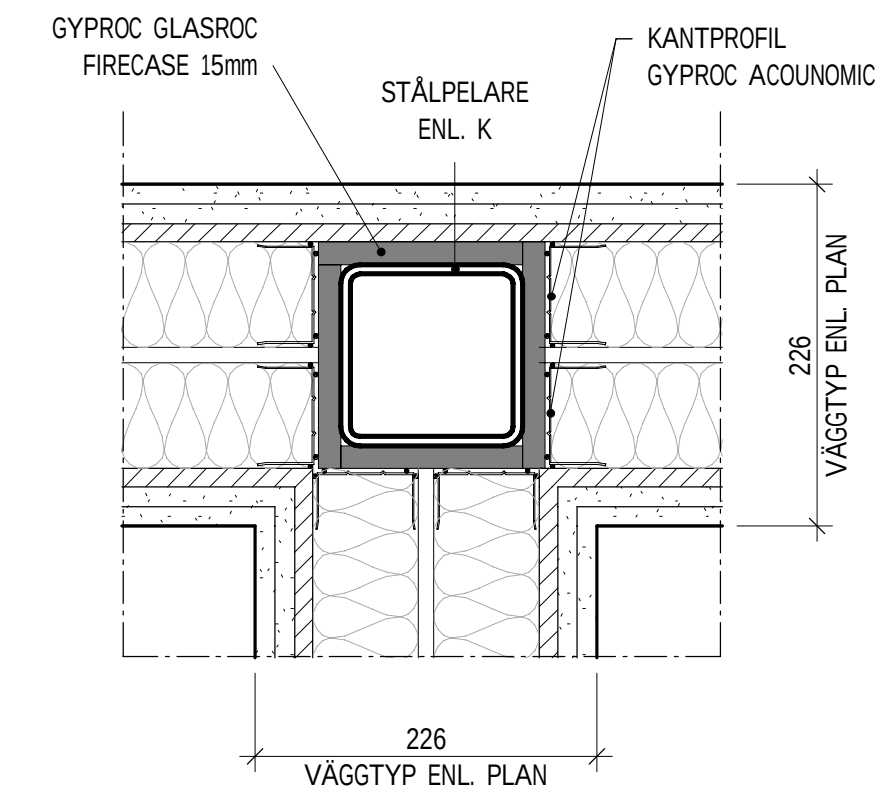

IK4 - STÅLPELARE I VÄGGKORSNING
1 : 5

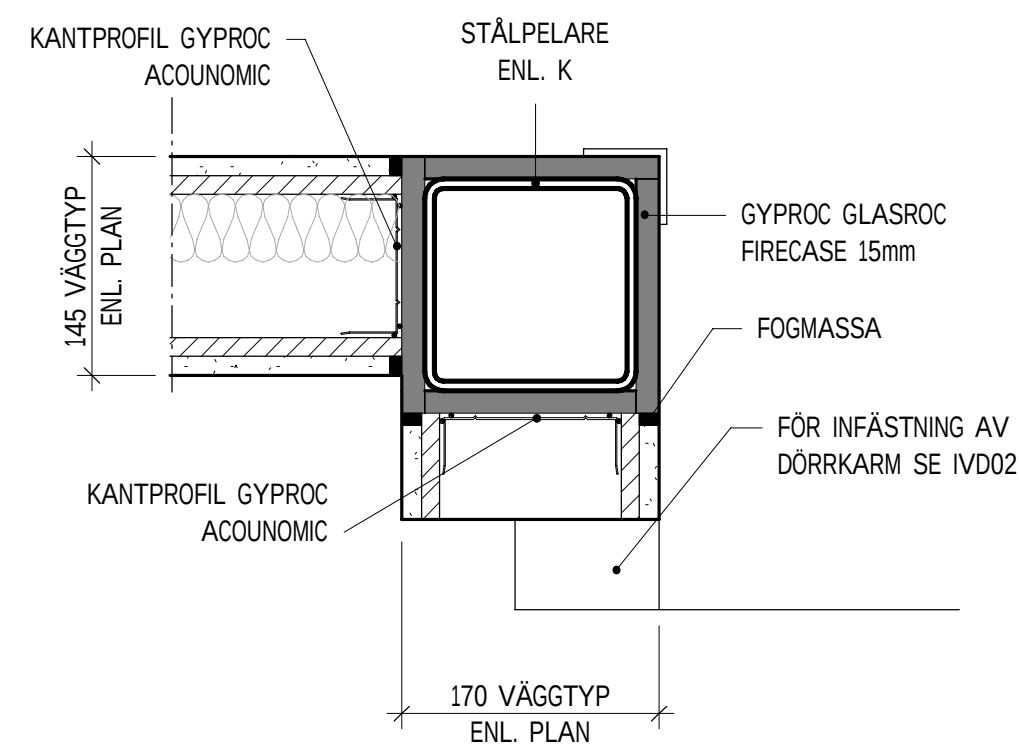


IK5 - STÅLPELARE I INNERVÄGGSHÖRN
1 : 5

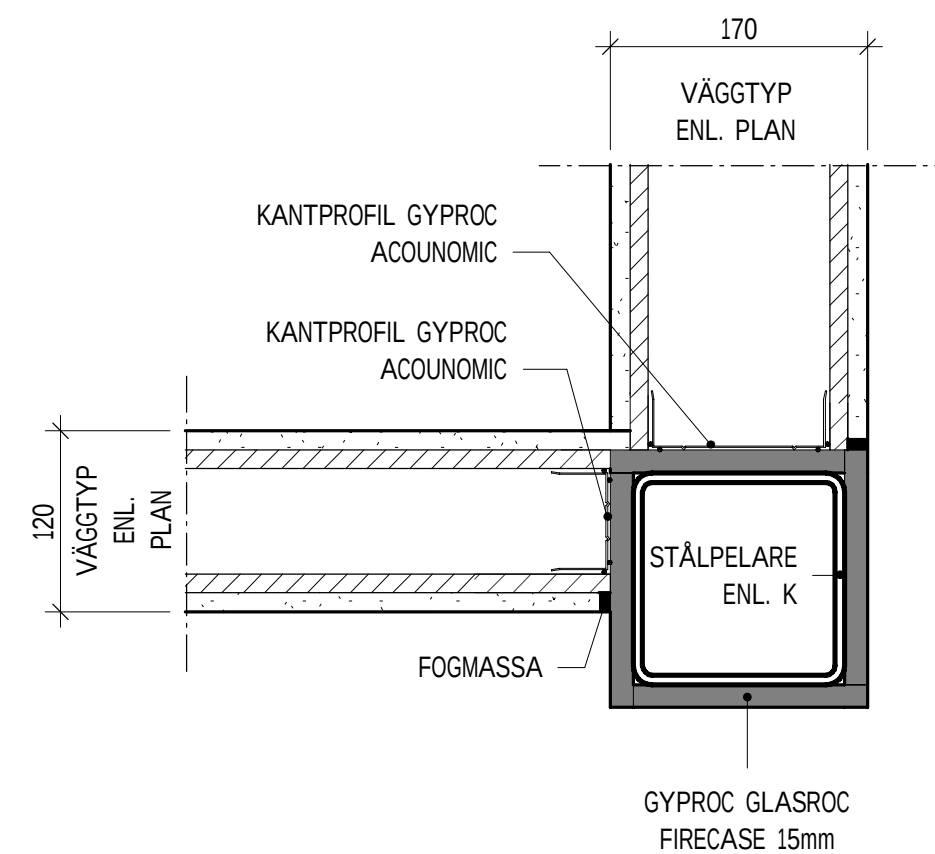


IK6 - HALVT UTSTICKANDE PELARE


1:5

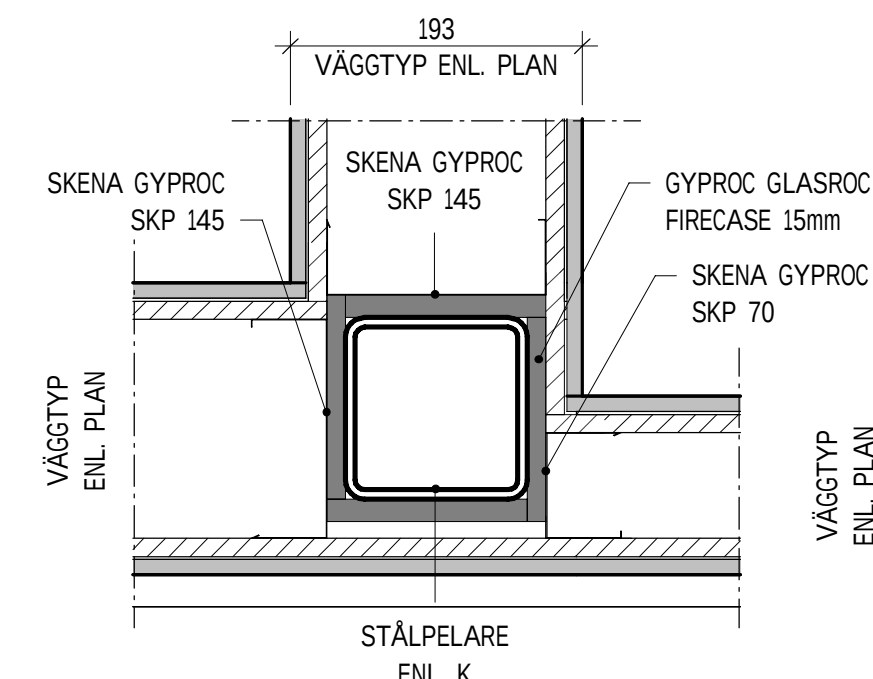


IK7 - STÅLPELARE I VÄGGKORSNING KÖK
1 : 5

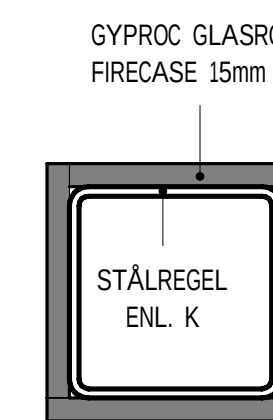


IK8 - PRINCIPDETALJ FRISTÅENDE STÅLPELARE
1 : 5

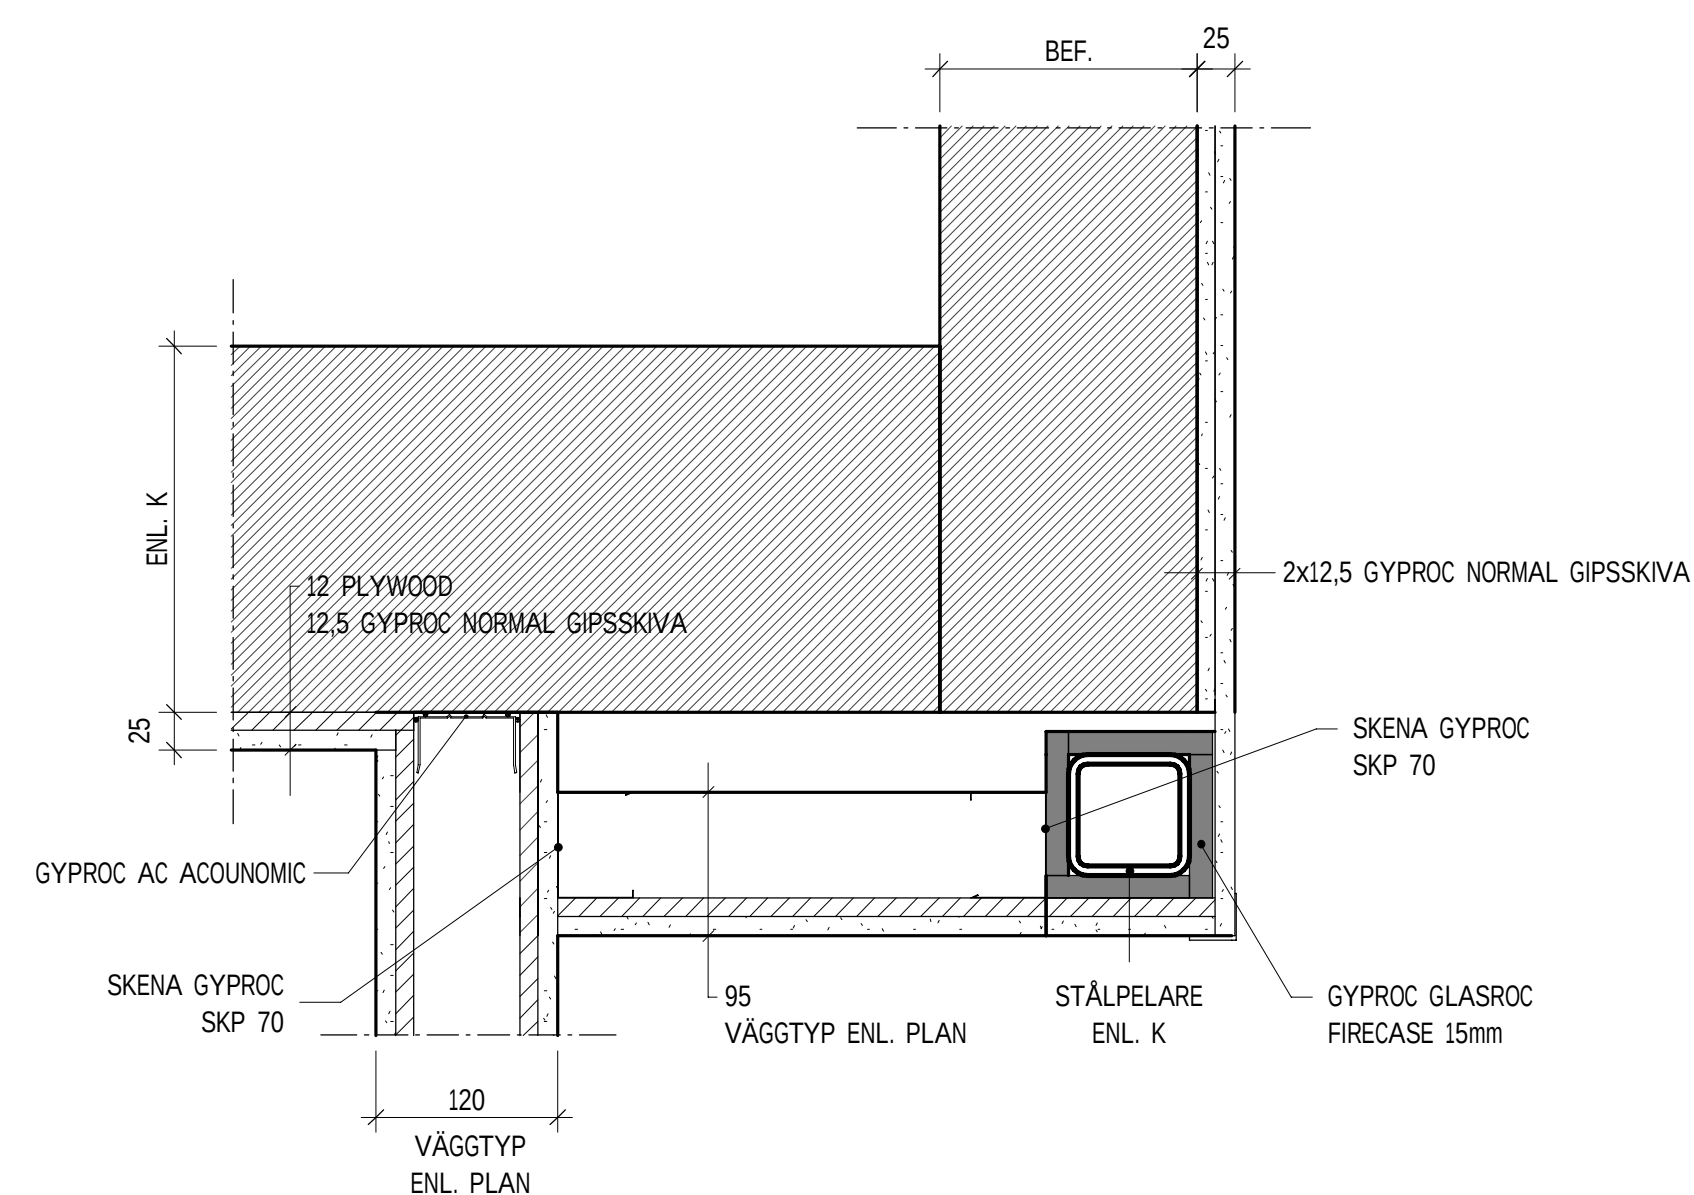

IK9 - STÅLPELARE VID BEFINTLIG VÄGG
1 : 5

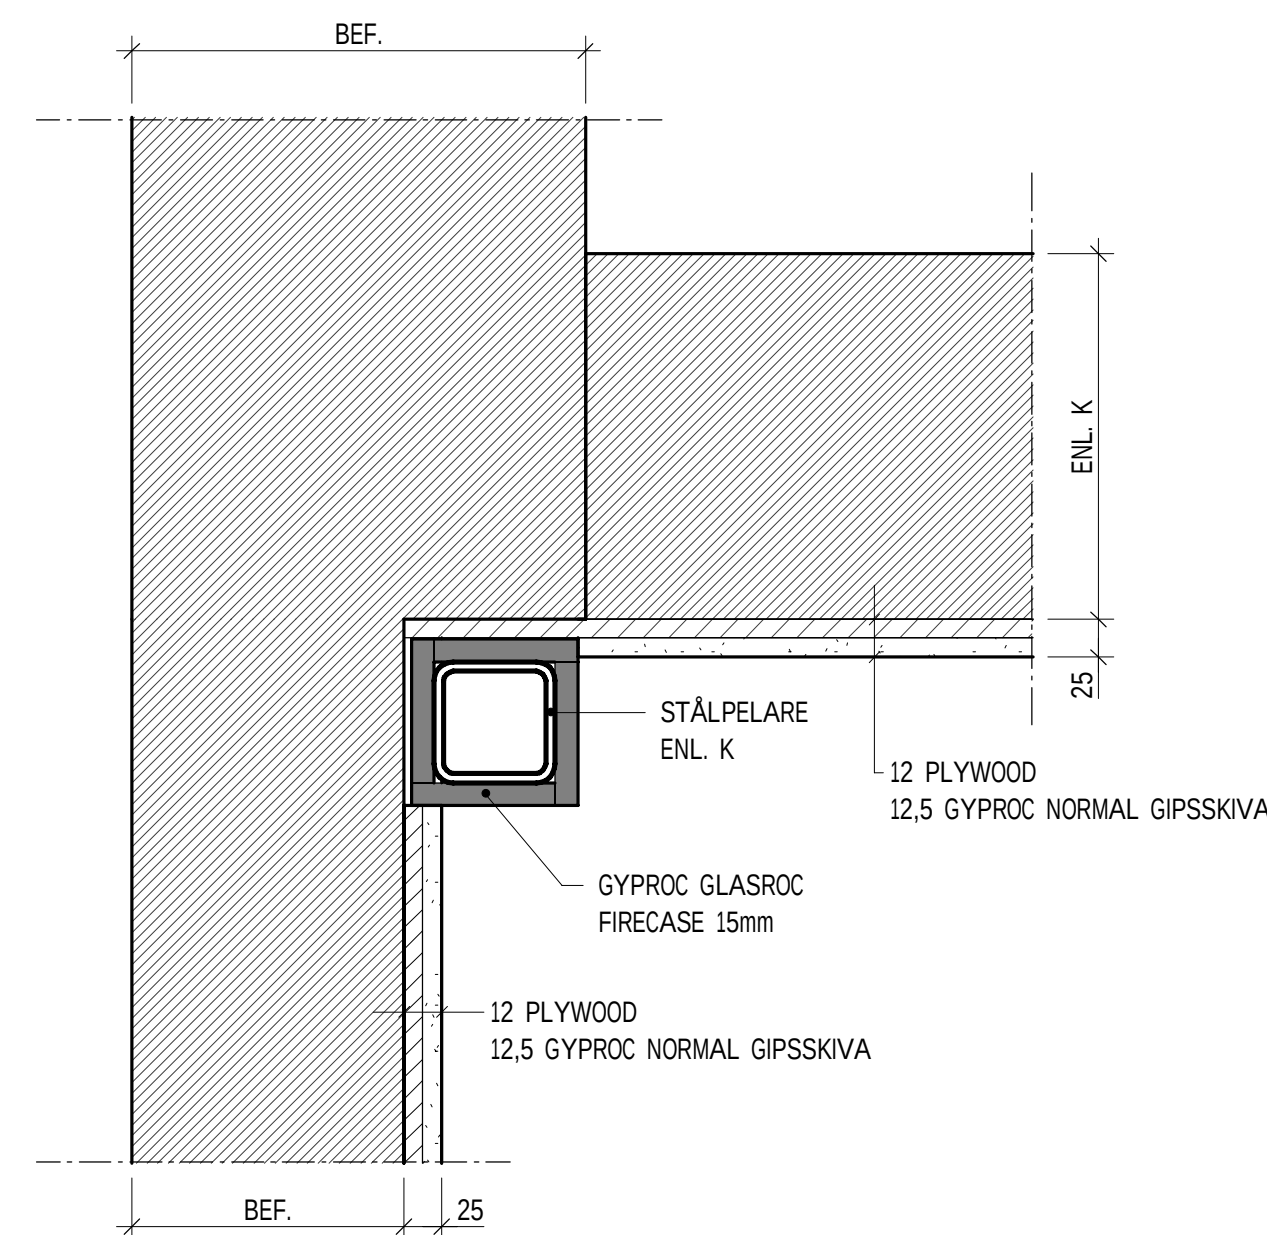

IK10 - STÅLPELARE VID BEF. VÄGGHÖRN
1 : 5

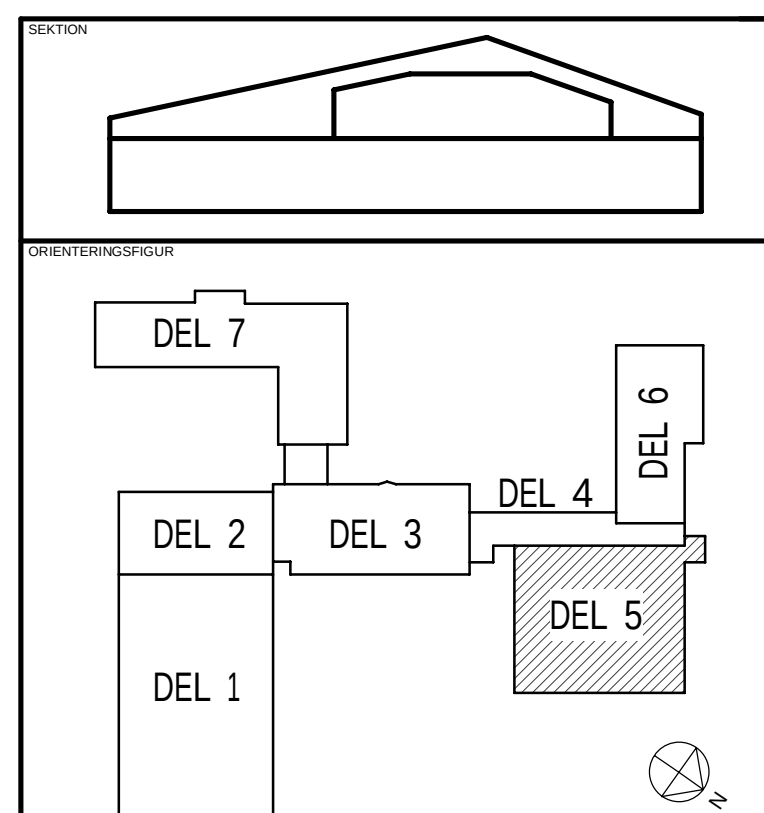

STATUS		
FÖRFRÅGNINGSUNDERLAG		
HANDLING		
BYGGHANDLING		
DATUM	GÖRKÄND AV	ÄNDRINGS PM
2024-12-20	T. BERGSTRÖM	



PROJEKTNAMN

CENTRAALKÖK

OMRÅDE
ROBERTSFORS KOMMUN

PROJEKTNUMMER	ADRESS
	YTTRE RINGVÄGEN 4
DIARIENUMMER	FASTIGHET
	FORDONET 1

	FORDONET 1
DISCIPLIN A	FORETAG NORCONSULT SVERIGE AB

UPPDRAGSNUMMER	SKAPAD AV
108 83 71	MSR
TELEFON	KONTAKTPERSON
	"

010 141 80 00 TOMAS BERGSTROM	
BYGGNADSVK	PLUSHOJD (RH 2000)

VÄNINGSPLAN	VÄNINGSDEL	DELOMRÅDE
-------------	------------	-----------

43 INRE RUMSBILDANDE BYGGDELAR

RITNINGSKATEGORI			SKALA	FORMAT
DETALJ			1:5	A1

DOKUMENTNUMMER	ÄNDERUNG
A-43-6-001	