




HORISONTALDETALJER

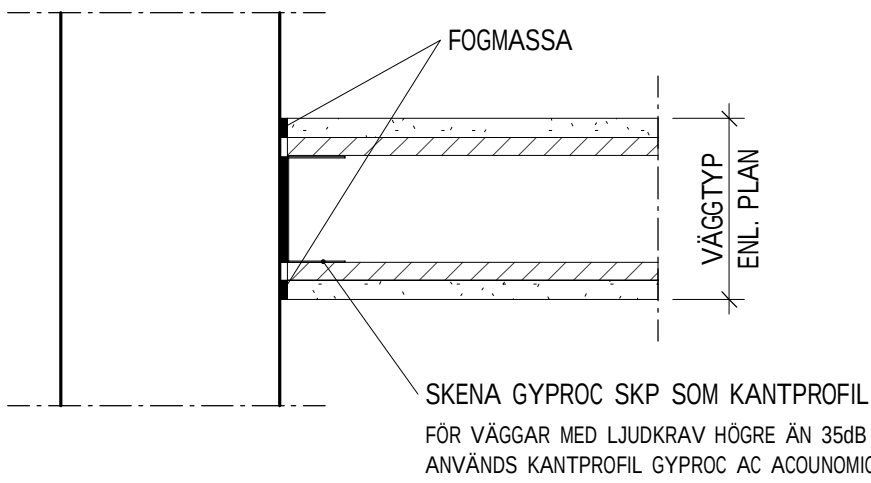


IVD01 - PRINCIPDETALJ MÖTE INNERVÄGG
1 : 5

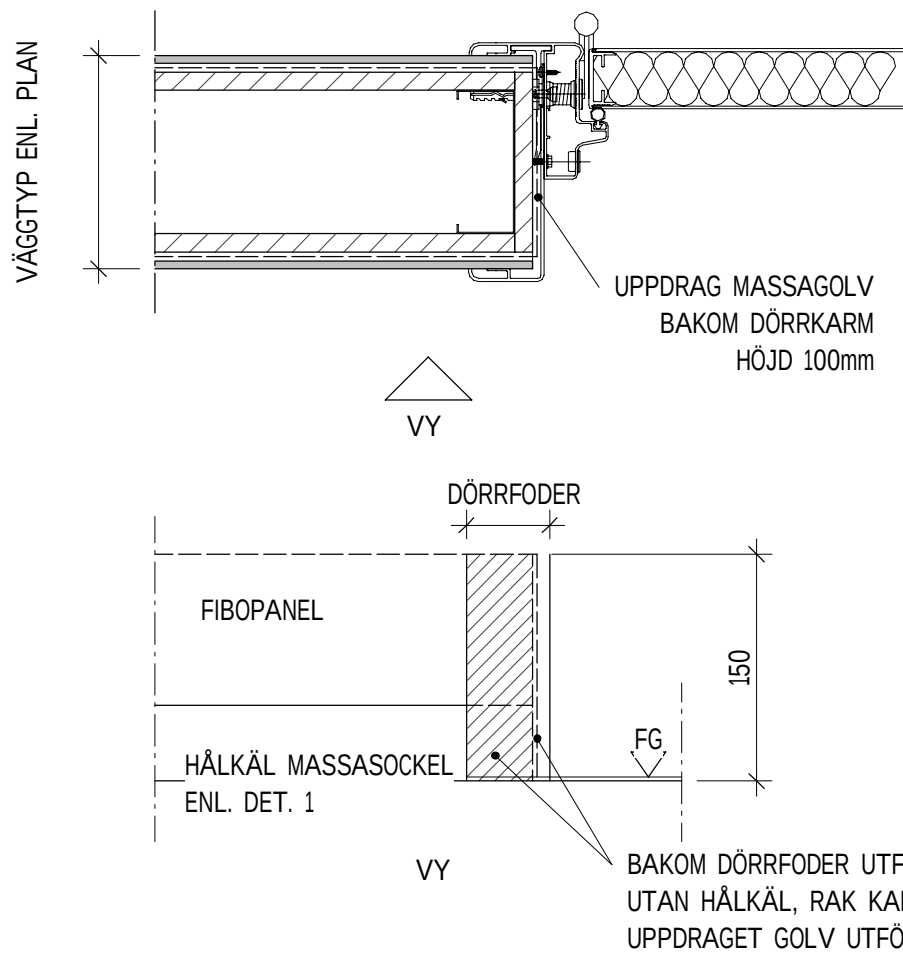


IVD03 - PRINCIPDETALJ INFÄSTNING DÖRRKARM AV GLASFIBER
1 : 5

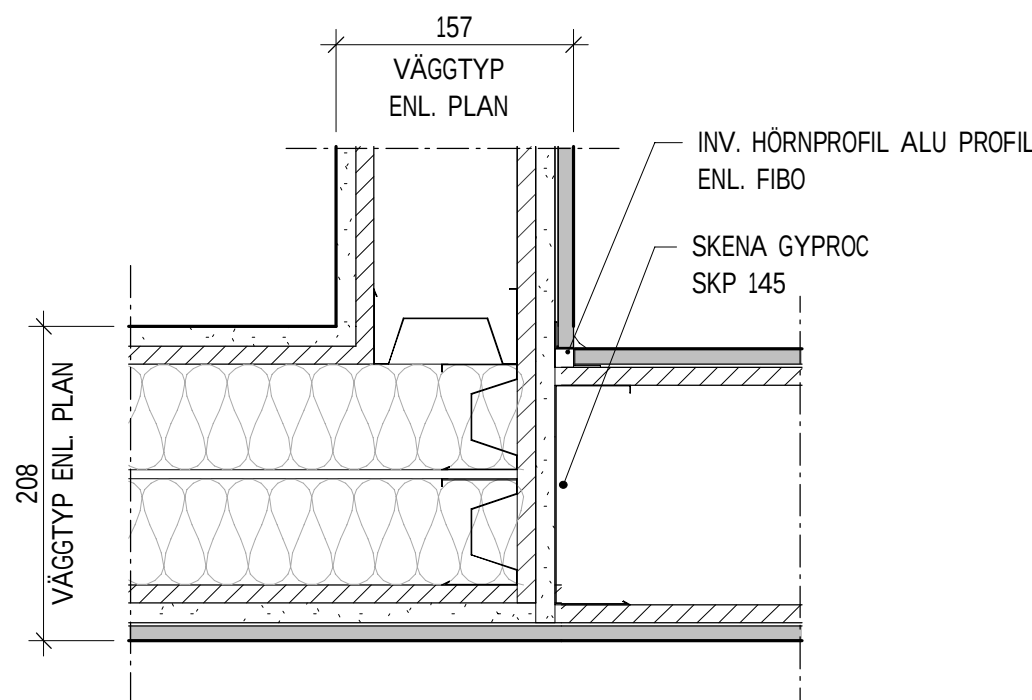


IVD05 - MÖTE 3 VÄGGAR
1 : 5

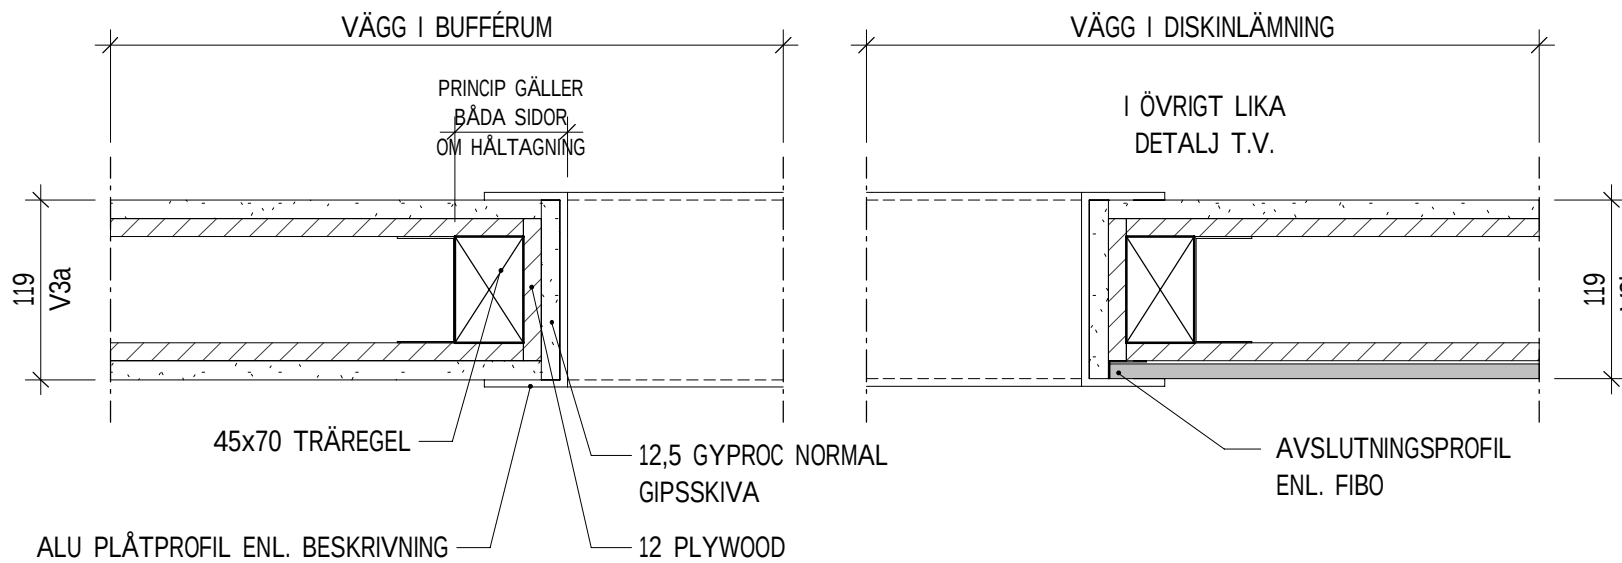


IVD07 - HÅLTAGNING VÄGG
1 : 5

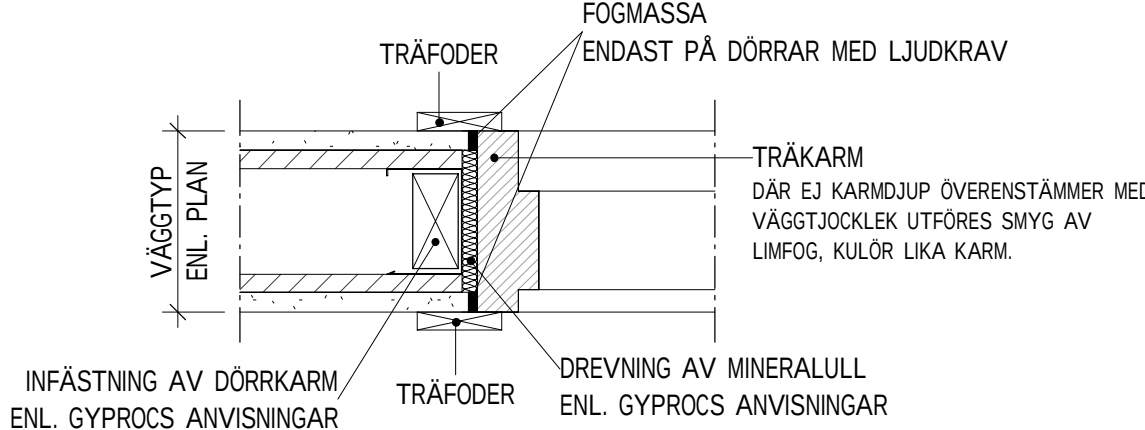

IVD02 - PRINCIPDETALJ INFÄSTNING DÖRRKARM AV TRÄ I INNERVÄGG AV STÅL
1 : 5

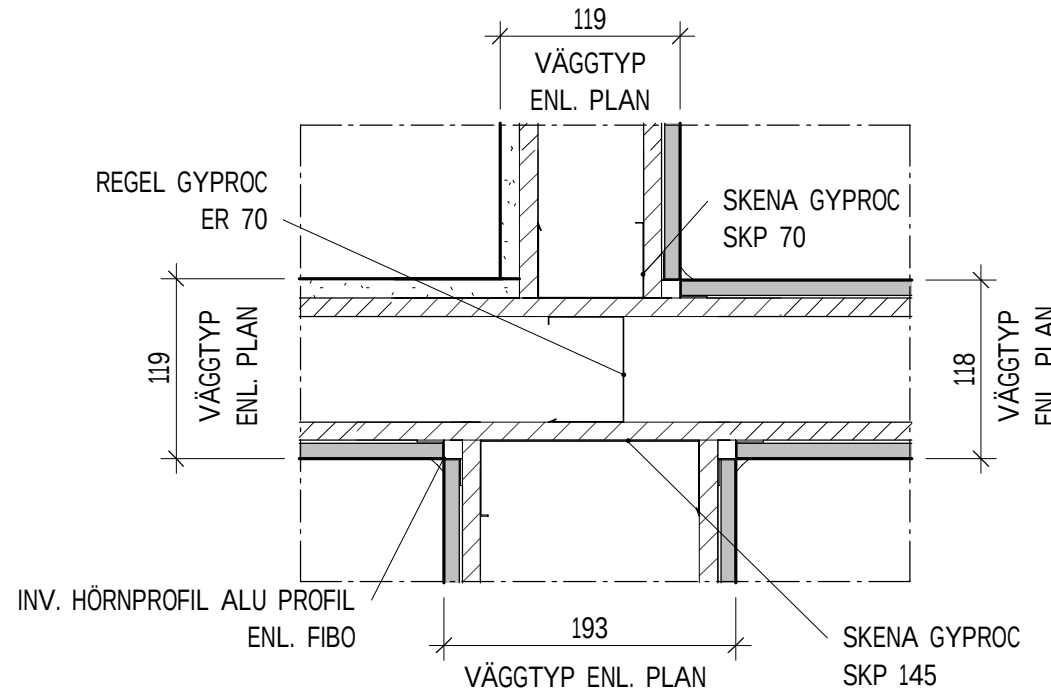


IVD04 - MÖTE 4 VÄGGAR
1 : 5

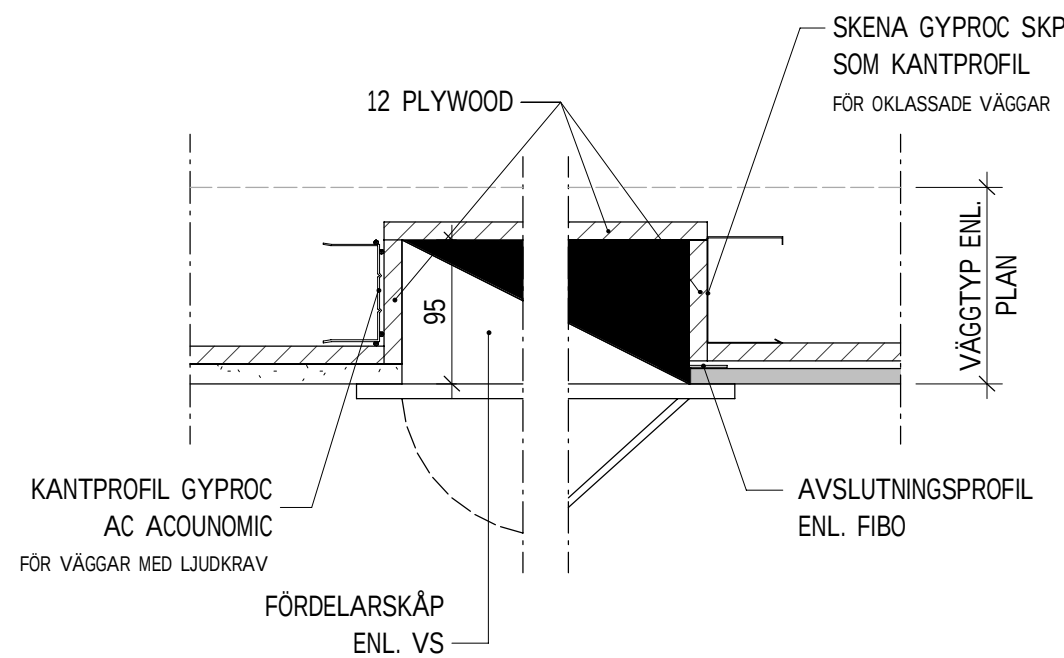


IVD06 - INKLÄDNAD FÖRDELARSKÅP
1 : 5



VERTIKALDETALJER

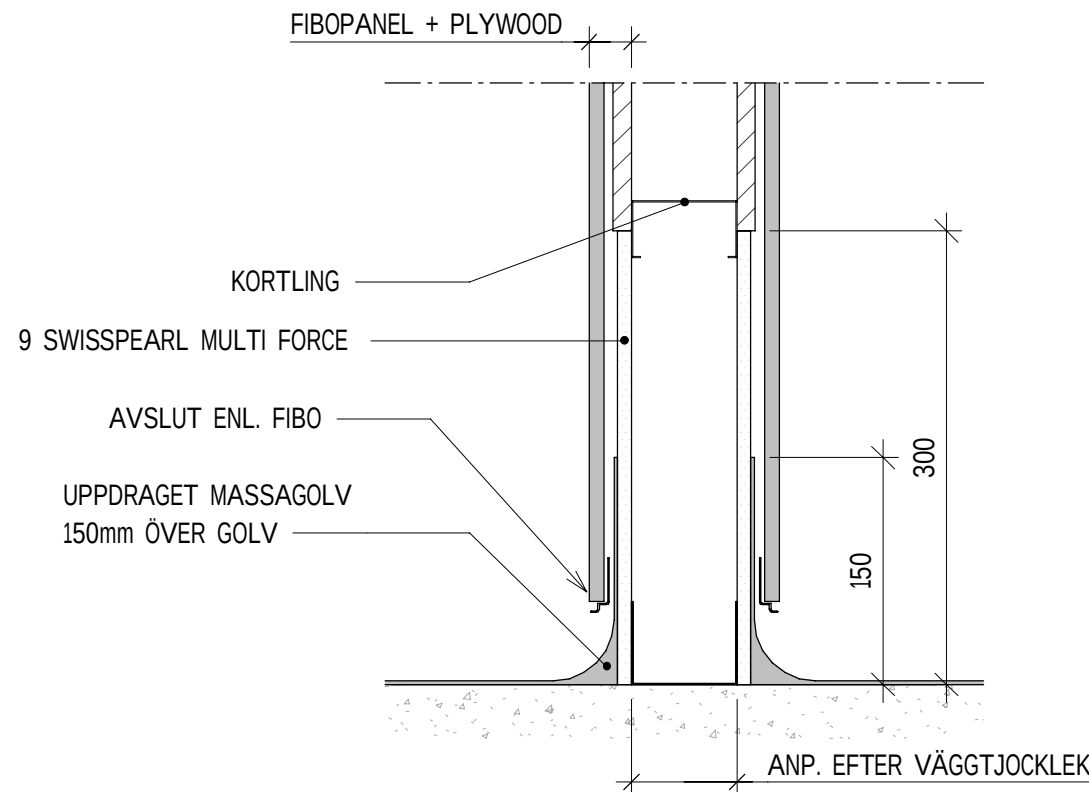


IVD10 - PRINCIPDETALJ MASSAGOLV MOT INNERVÄGG
1 : 5

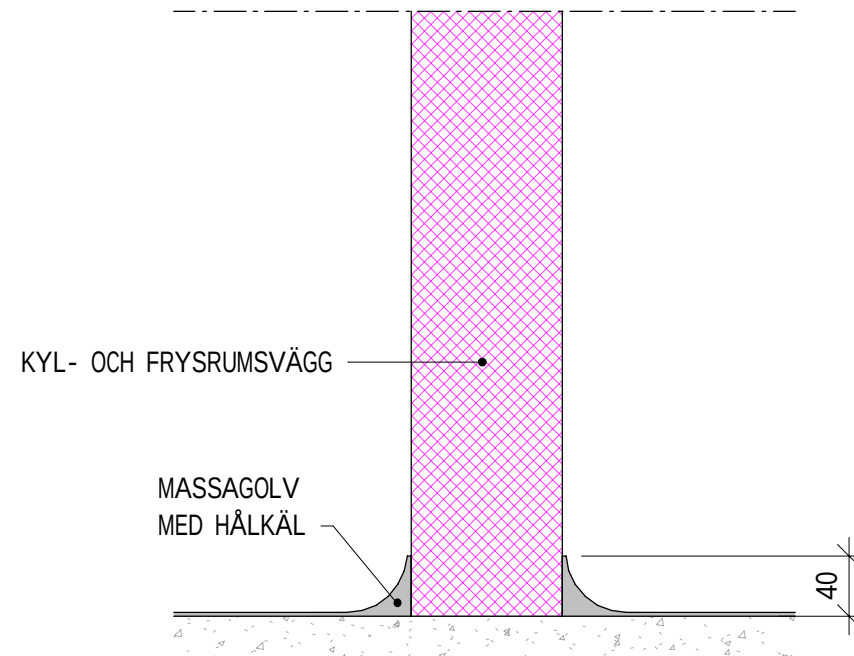


IVD12 - PRINCIPDETALJ MASSAGOLV MOT KYL-/FRYSRUMSVÄGG
1 : 5

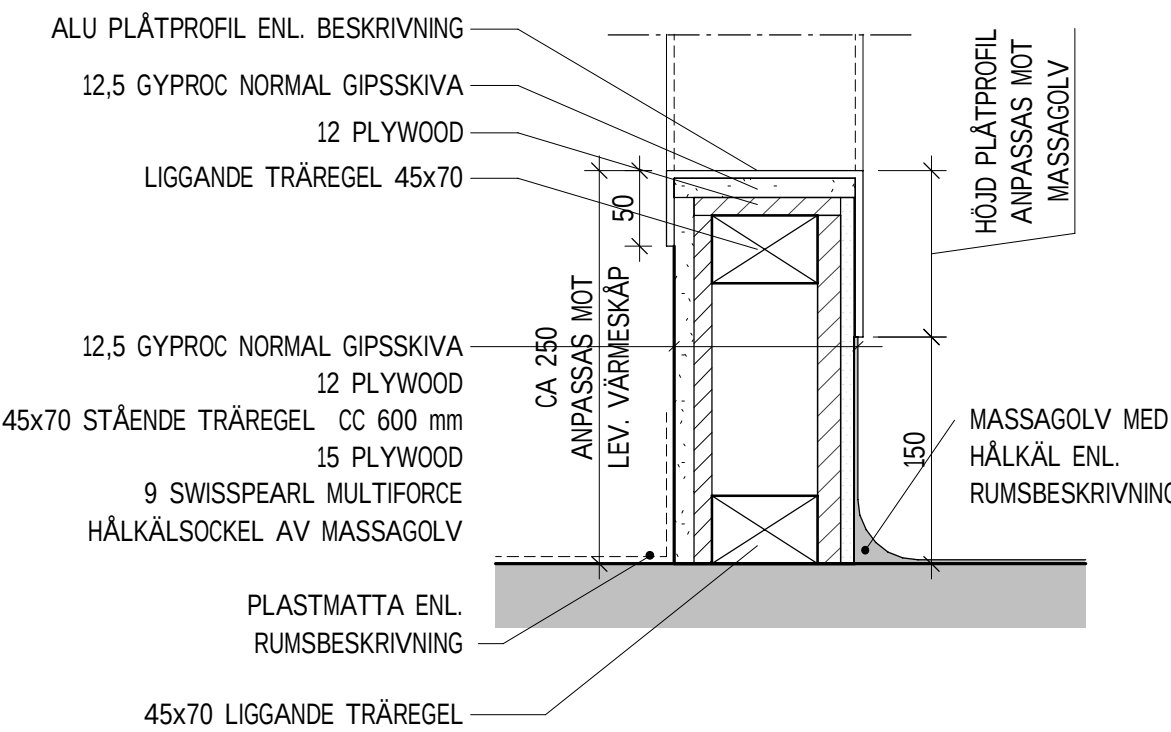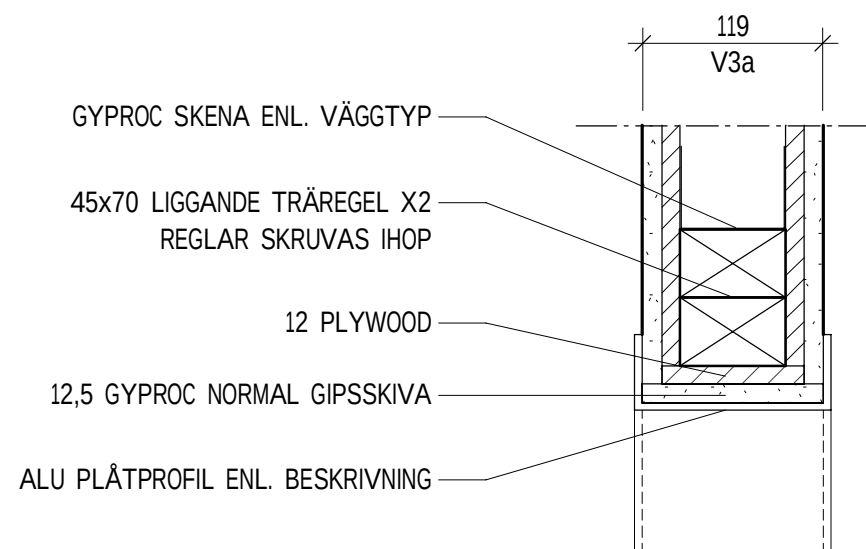



IVD14 - HÅLTAGNING VÄGG VÄRMESKÅP
1 : 5

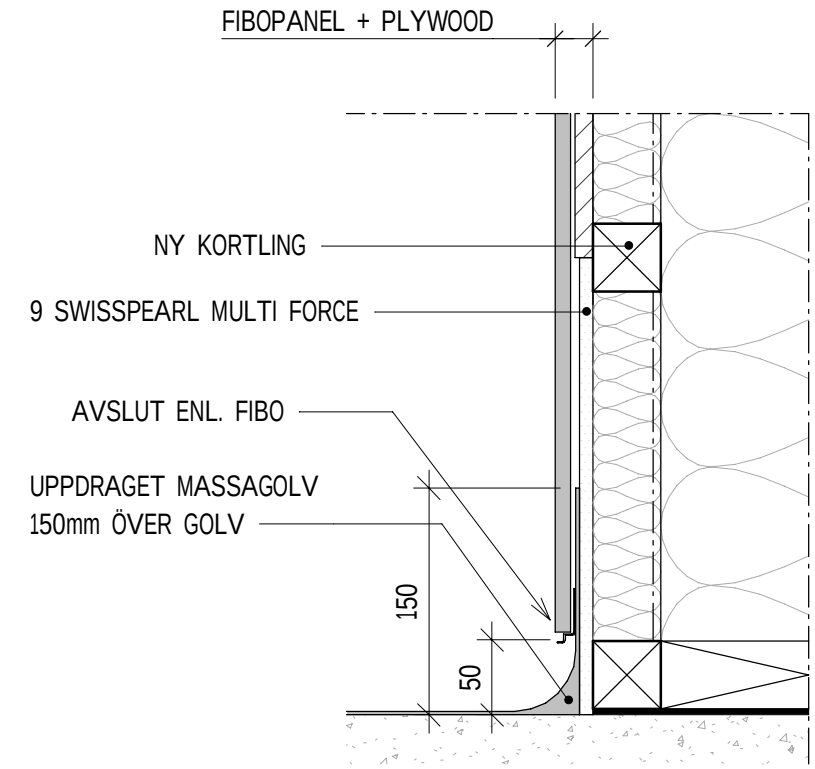

IVD11 - PRINCIPDETALJ MASSAGOLV MOT YTTERVÄGG
1 : 5

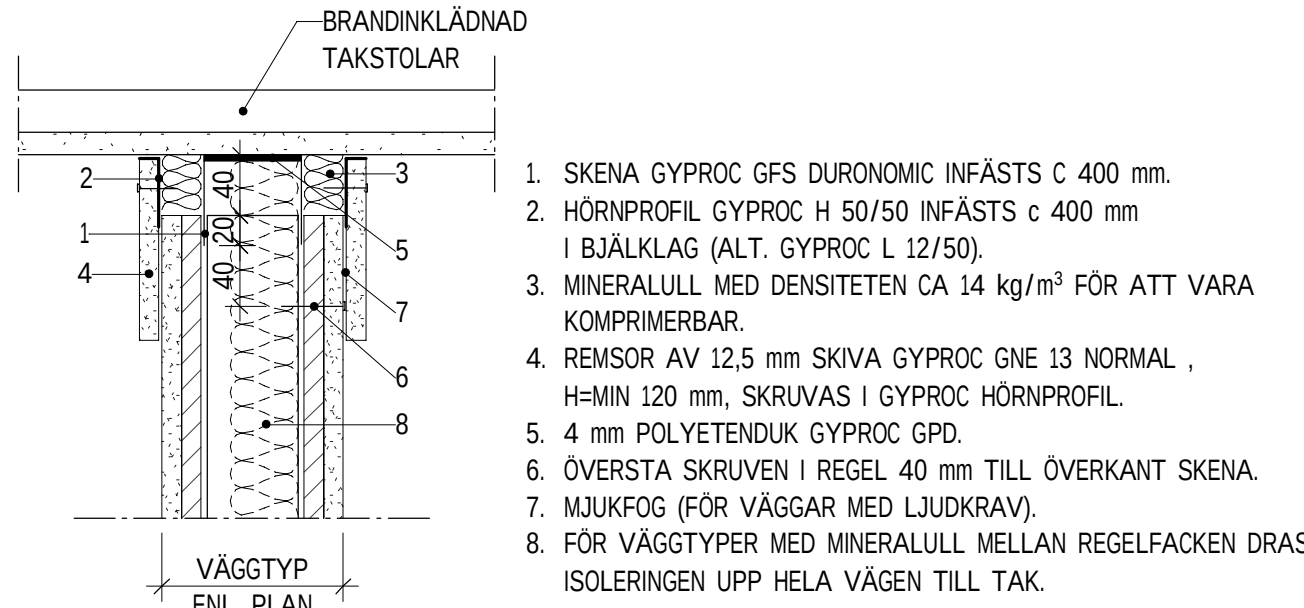

IVD13 - PRINCIPDETALJ TELESKOPANSLUTNING INNERVÄGG
1 : 5

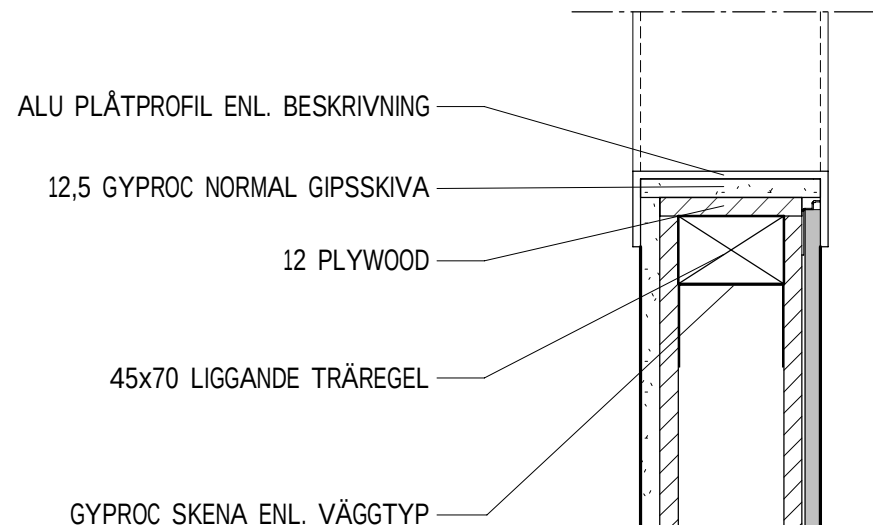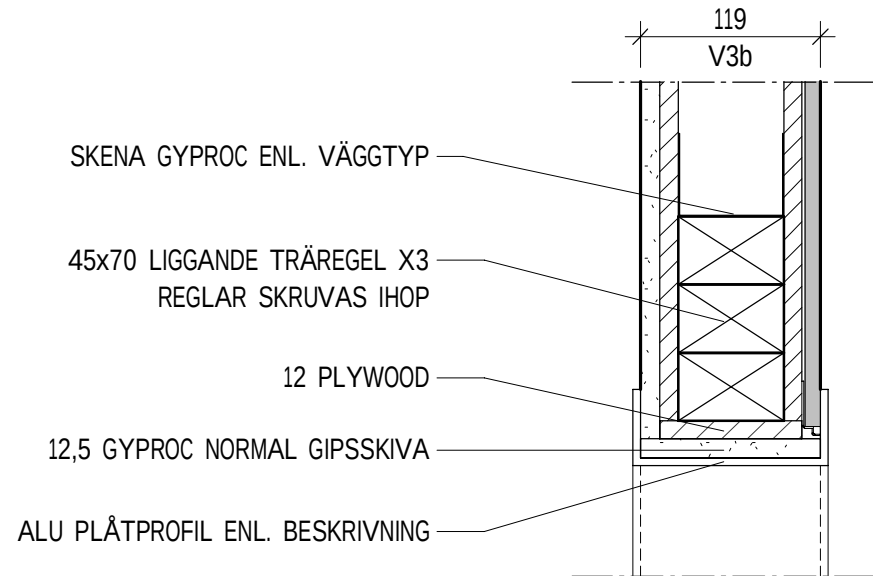

IVD15 - HÅLTAGNING VÄGG DISKBAND
1 : 5

SEKTION		
ORIENTERINGSSKISS		
STATUS		
FÖRFRÅGNINGSUNDERLAG		
HANDLING		
BYGGHANDLING		
DATUM	FÖRORDNAD AV	ANSVARIG PM
2024-12-20	T. BERGSTRÖM	
BESTÄLLARE		
ROBERTSFORS KOMMUN		
PROJEKTNAMN		
CENTRALKÖK		
OMRÅDE		
ROBERTSFORS KOMMUN		
PROJEKTNUMMER	FÄRHUS	
YTTRE RINGVÄGEN 4		
DIREKTÖRSNUMMER	FASTIGHET	
FORDONET 1		
DISCIPLIN	FÖRETAG	
A	NORCONSULT SVERIGE AB	
UPPRORAGSNUMMER	SKAPAD AV	
108 83 71	MSR	
TELEFON	KONTAKTPERSON	
010 141 80 00	TOMAS BERGSTRÖM	
BYGGNADSRUM	FÖLJESKISS (RIT 2008)	
VÄRINGSPLAN	VÄRINGSDEL	DELOMRÅDE
SYSTEM		
43 INRE RUMSBILDANDE BYGGDELAR		
SPECIFIKATION		
INVÄNDIGA DETALJER		
DETALJ	SKALA	FORMAT
	1:5	A1
DOCUMENTNUMMER	ANSVARIG	
A-43-6-002		

SKALA 1:5 0 100 500 MILLIMETER