


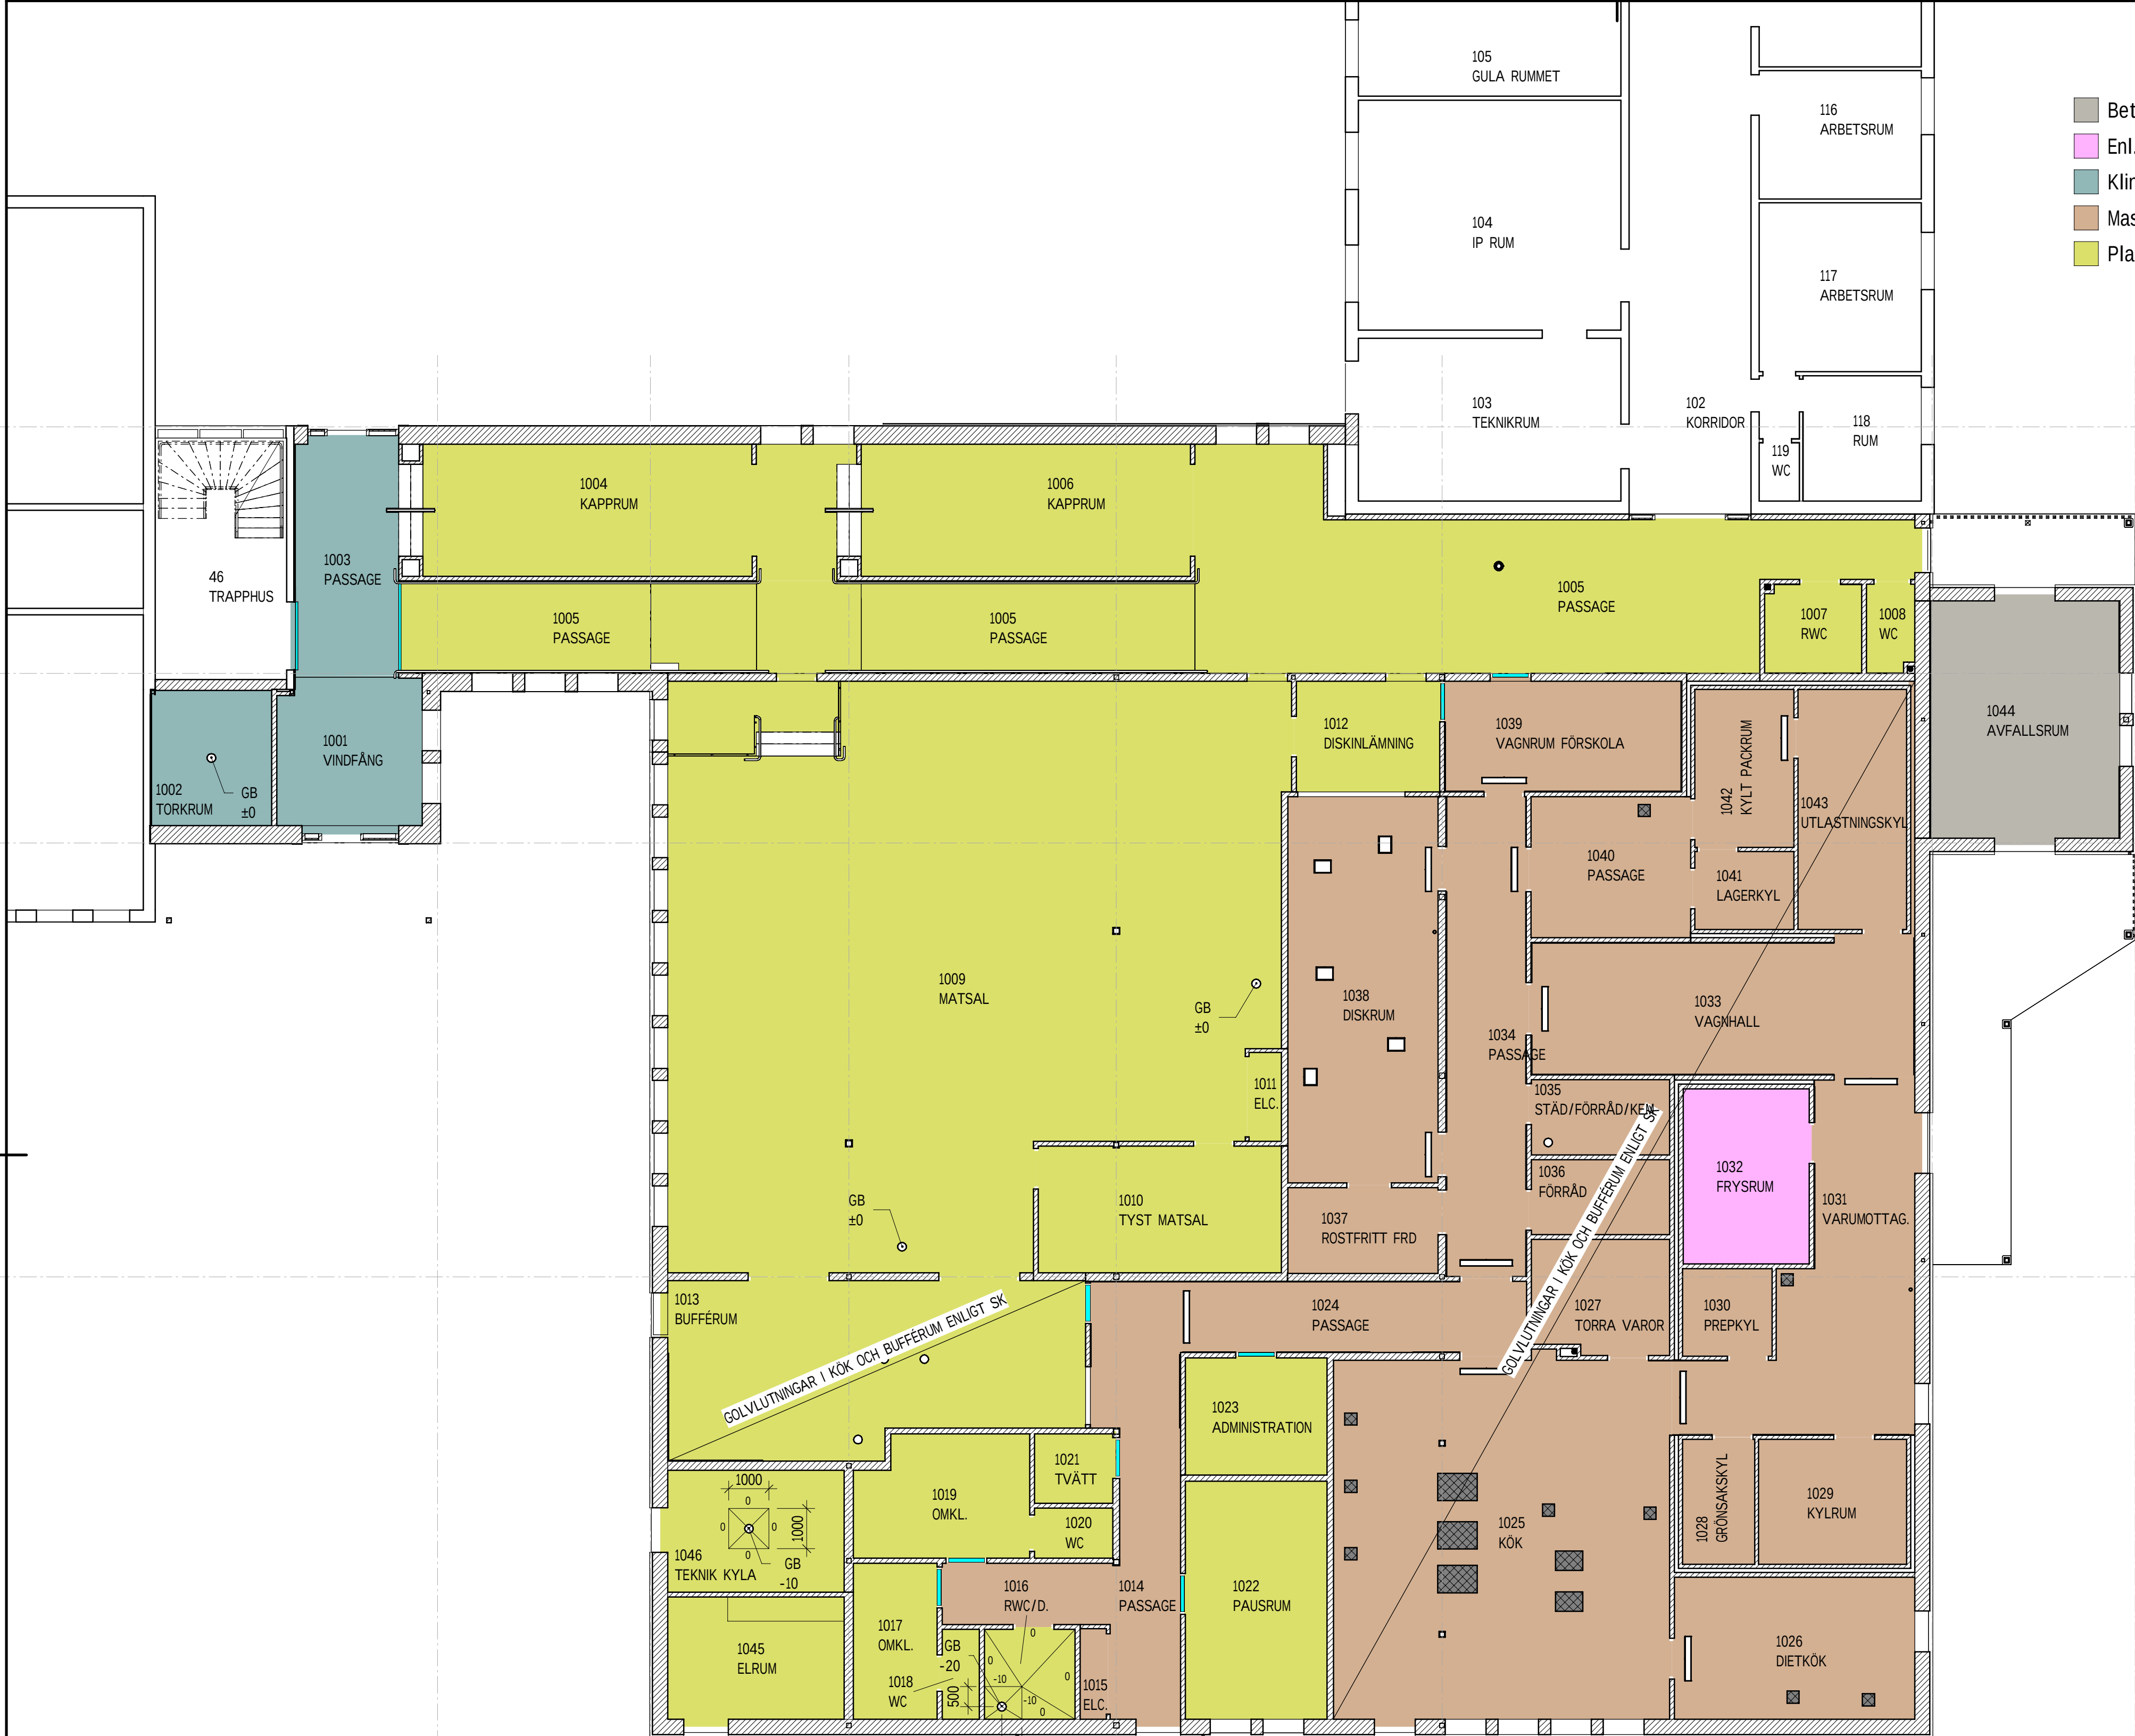

- Betong
- Enl. Kylentreprenad
- Klinker
- Massagolv
- Plastmatta

FÖRKLARINGAR

- AVSLUTNINGSLIST ENL. BESKRIVNING SE PRINCIPDETALJ
- GB = GOLVBRUNN, GOLVANSLUTNINGAR ENL. FABRIKANTENS ANVISNINGAR


FÖRESKRIFTER

UPPBYGGNAD GOLVTYPER


KLINKER:
7mm KLINKER
5mm FIX
5mm AVJÄMNINGSMASSA

MASSAGOLV:
4mm PLASTBASERAD MASSA
13mm AVJÄMNINGSMASSA
(17mm AVJÄMNINGSMASSA I FALL UNDER BÄNKAR MM.)


PLASTMATTA:
2mm PLASTMATTA
15mm AVJÄMNINGSMASSA

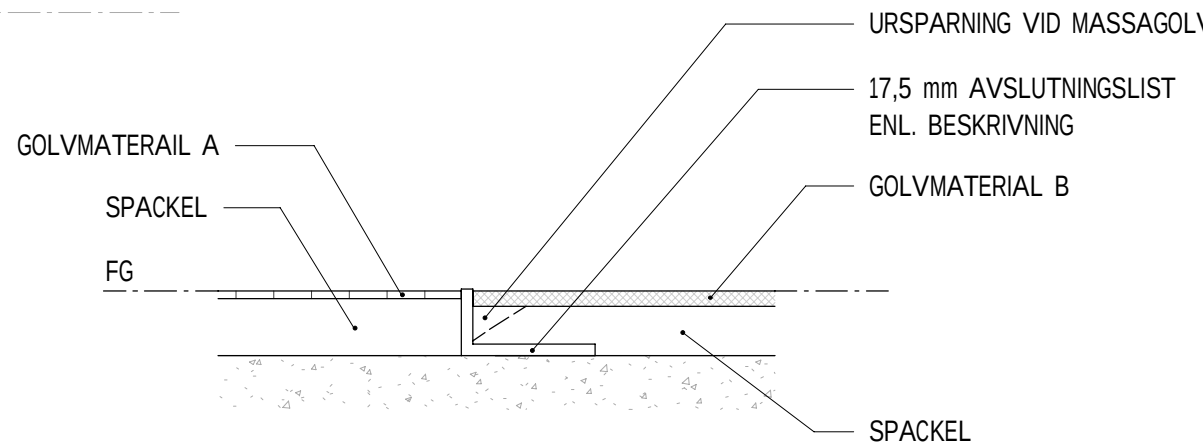


PRINCIPDETALJ MATERIALBYTE GOLV
1 : 2

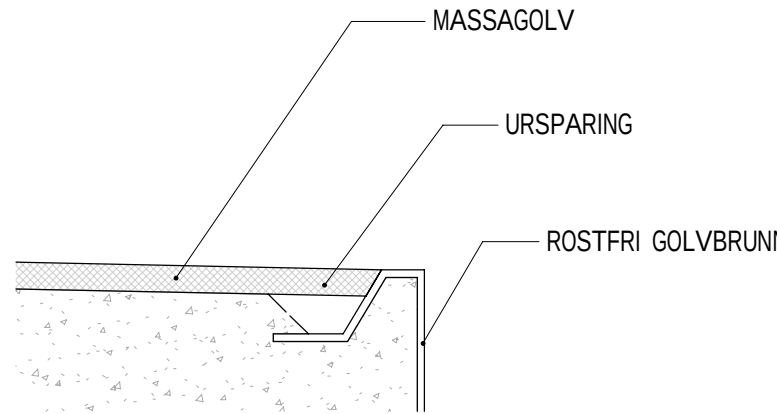

PRINCIPDETALJ RF GOLVBRUNN I MASSAGOLV
1 : 2

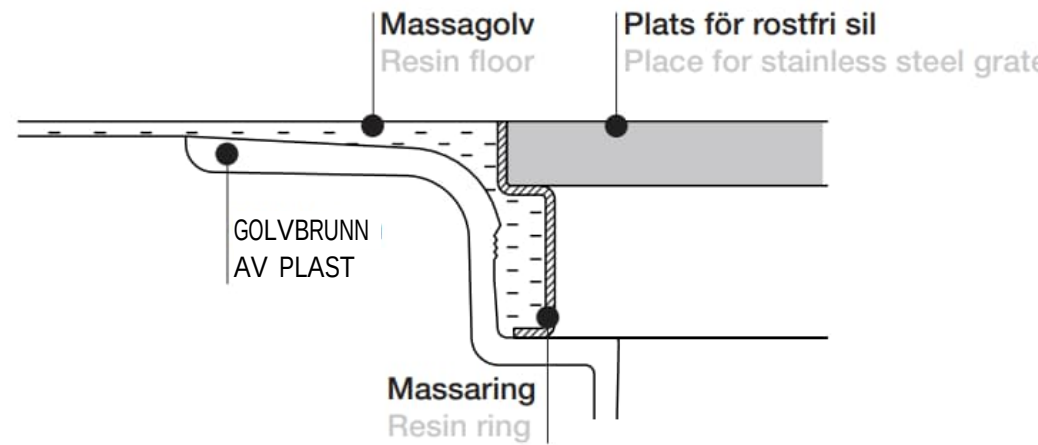

PRINCIPDETALJ GOLVBRUNN AV PLAST I MASSAGOLV
ENL. FABRIKANTENS ANVISNING. EJ SKALENLIG

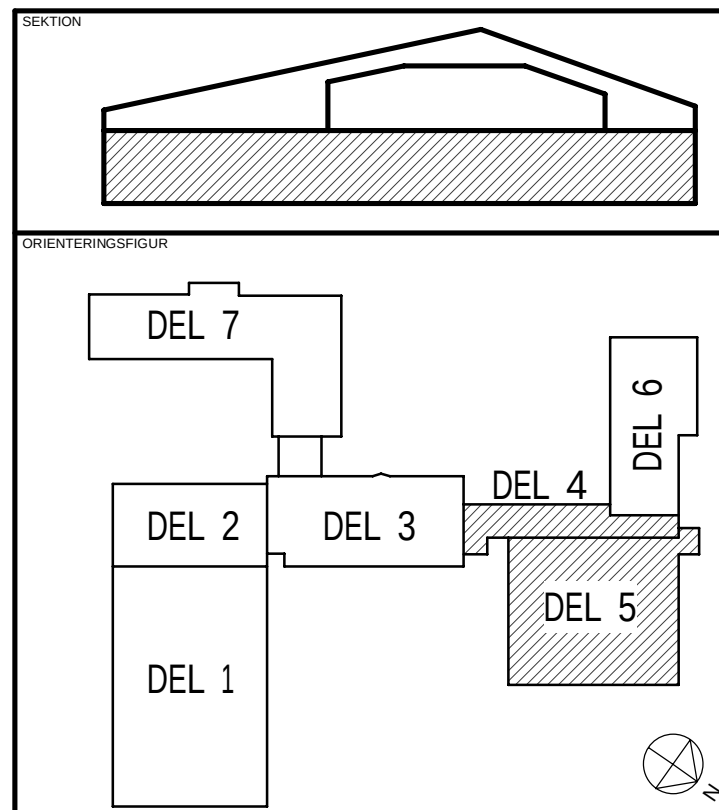

FÖRFRÅGNINGSUNDERLAG

BYGGHANDLING

DATUM: 2024-12-20
FÖRFRÅGAD AV: T. BERGSTRÖM
ANSÖKAN NR: 2024-12-20

BESTÄLLARE: ROBERTSFORS KOMMUN



CENTRALEKÖK

ROBERTSFORS KOMMUN

PROJEKTNUMMER: YTTRE RINGVÄGEN 4

DIARIENUMMER: FORDONET 1

DISCIPLIN: NORCONSULT SVERIGE AB

UPPDRAGSNUMMER: 108 83 71

TELEFON: 010 141 80 00

BYGGNADSTYP: PLASTRÖR (VIT 2008)

VÄRNINGSPÅN: 1

SYSTEM: 44 INVÄNDIGA YTSKIET

SPECIFIKATION: GOLVPLAN

PLAN: A-44-1-100