




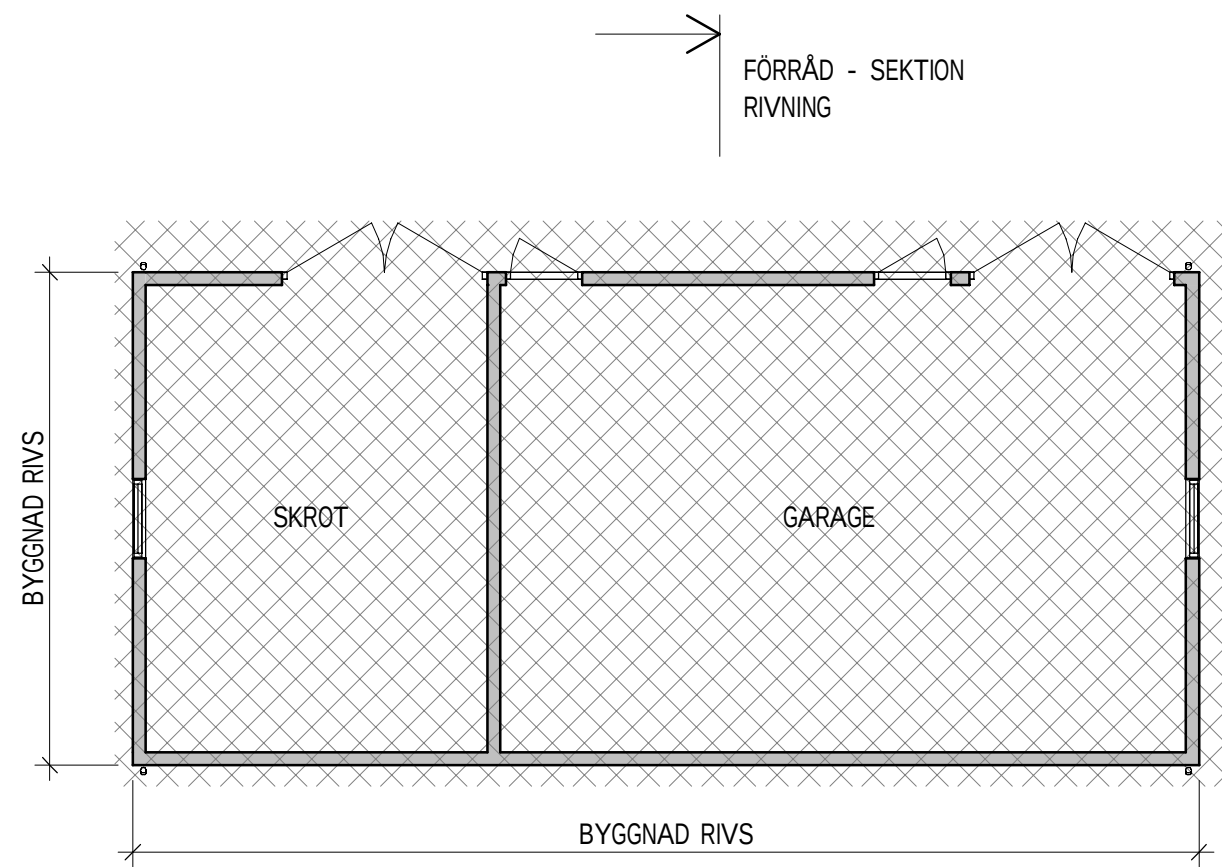


FÖRRÅD - PLAN

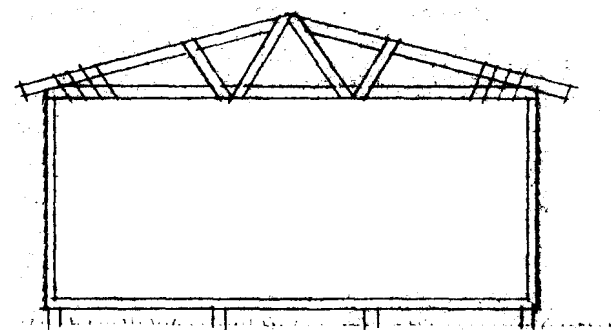


SEKTION

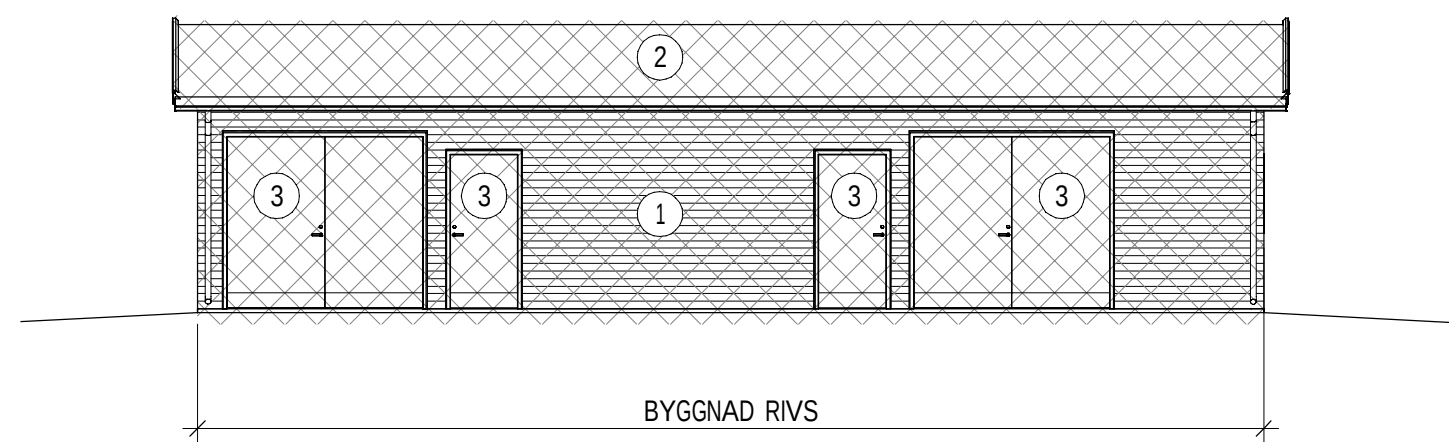


FÖRRÅD - FASAD MOT SYDVÄST
1 : 100

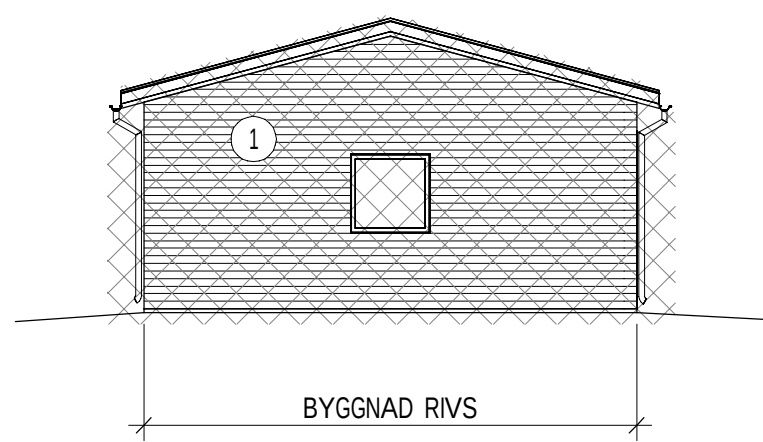

FÖRRÅD - FASAD MOT NORDVÄST
1 : 100

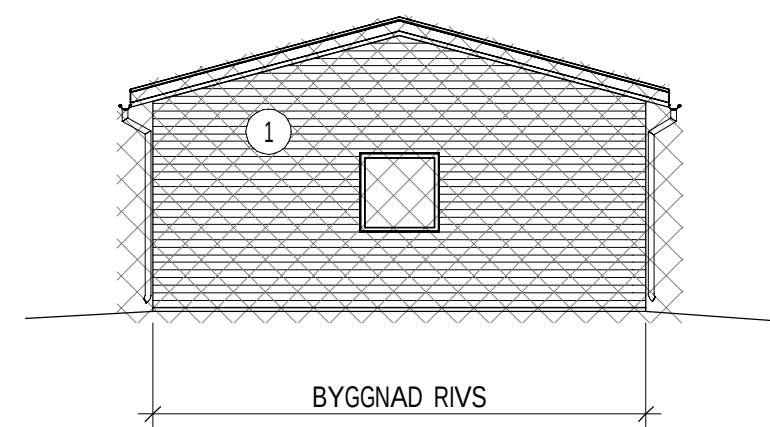

FÖRRÅD - FASAD MOT SYDÖST
1 : 100

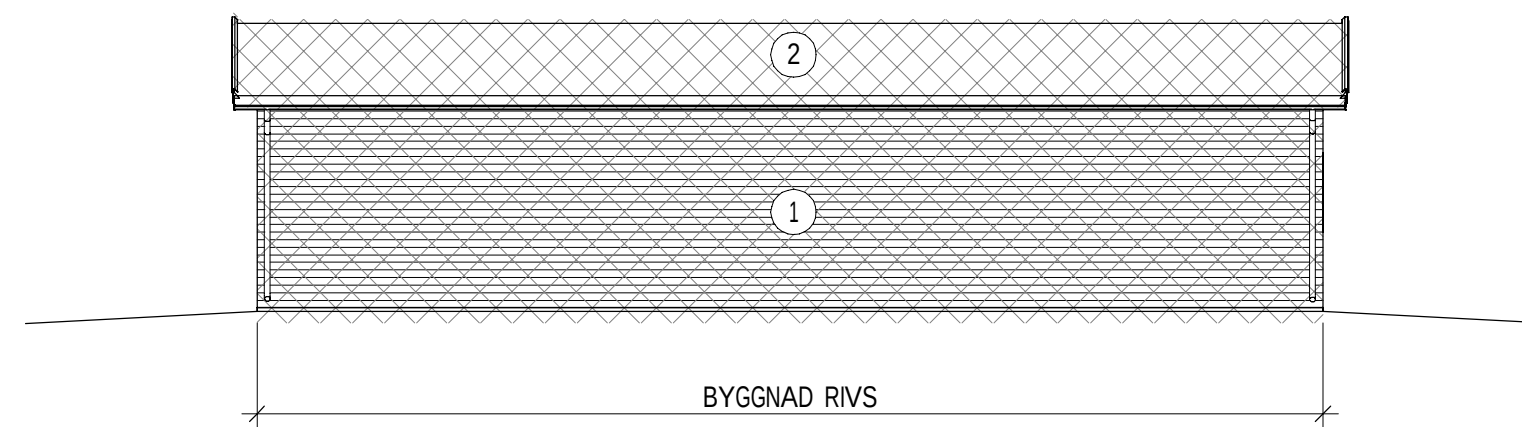

FÖRRÅD - FASAD MOT NORDÖST
1 : 100

SKALA 1:100 0 1 10 METER

FÖRKLARINGAR



BYGGNAD SOM RIVS

- 1 FASAD AV LIGGANDE TRÅPANEL RIVS.
- 2 TAK AV PROFILERAD PLÅT RIVS.
- 3 MASSIVA TRÅPORTAR OCH DÖRRAR MED SPARKSKYDD AV PLÅT RIVS

TAKAVVATTNING OCH ÖVRIGA PLÅTAR PÅ FASAD RIVS

GENERELLT:
BYGGNAD UPPFÖRD MED STOPPRESNING SAMT
UTVÄNDIG LIGGANDE PANEL AV 1"x6" PÅ
FÖRVÄNDRING MED GERADE HÖRN.

HÄNVISNINGAR

SITUATIONSPLAN - RIVNING A-01-1-101-R

STATUS		
FÖRFRÅGNINGSUNDERLAG		
HANDLING		
BYGGHANDLING		
DATUM	2024-12-20	ANSÖKAN AV
2024-12-20	T. BERGSTRÖM	ADRESSER PM
BESTÄLLARE		
ROBERTSFORS KOMMUN		
PROJEKTNAMN		
CENTRALEKÖ		
OMRÅDE		
ROBERTSFORS KOMMUN		
PROJEKTNUMMER	1088371	ADRESS
1088371	YTTRE RINGVÄGEN 4	
DIARIENUMMER	FASTIGHET	
	FORDONET 1	
DISCIPLIN	FÖRETAG	
A	NORCONSULT SVERIGE AB	
UPPDRAGSNUMMER	SKAPAD AV	
1088371	MSR	
TELEFON	KONTAKTPERSON	
010 141 80 00	TOMAS BERGSTRÖM	
BYGGNADSTYP	PLÅTSTÖP (RIT 2008)	
VÄRNINGSPÅN	VÄRNINGSDI	DELOMRÅDE
SYSTEM		
45 HUSKOMPLETTERINGAR		
SPECIFICATION		
FÖRRÅD		
RIVNING		SKALA
		1:100
DOKUMENTNUMMER		FORMAT
A-45-1-100-R		A1
		ANVÄNDNING

