




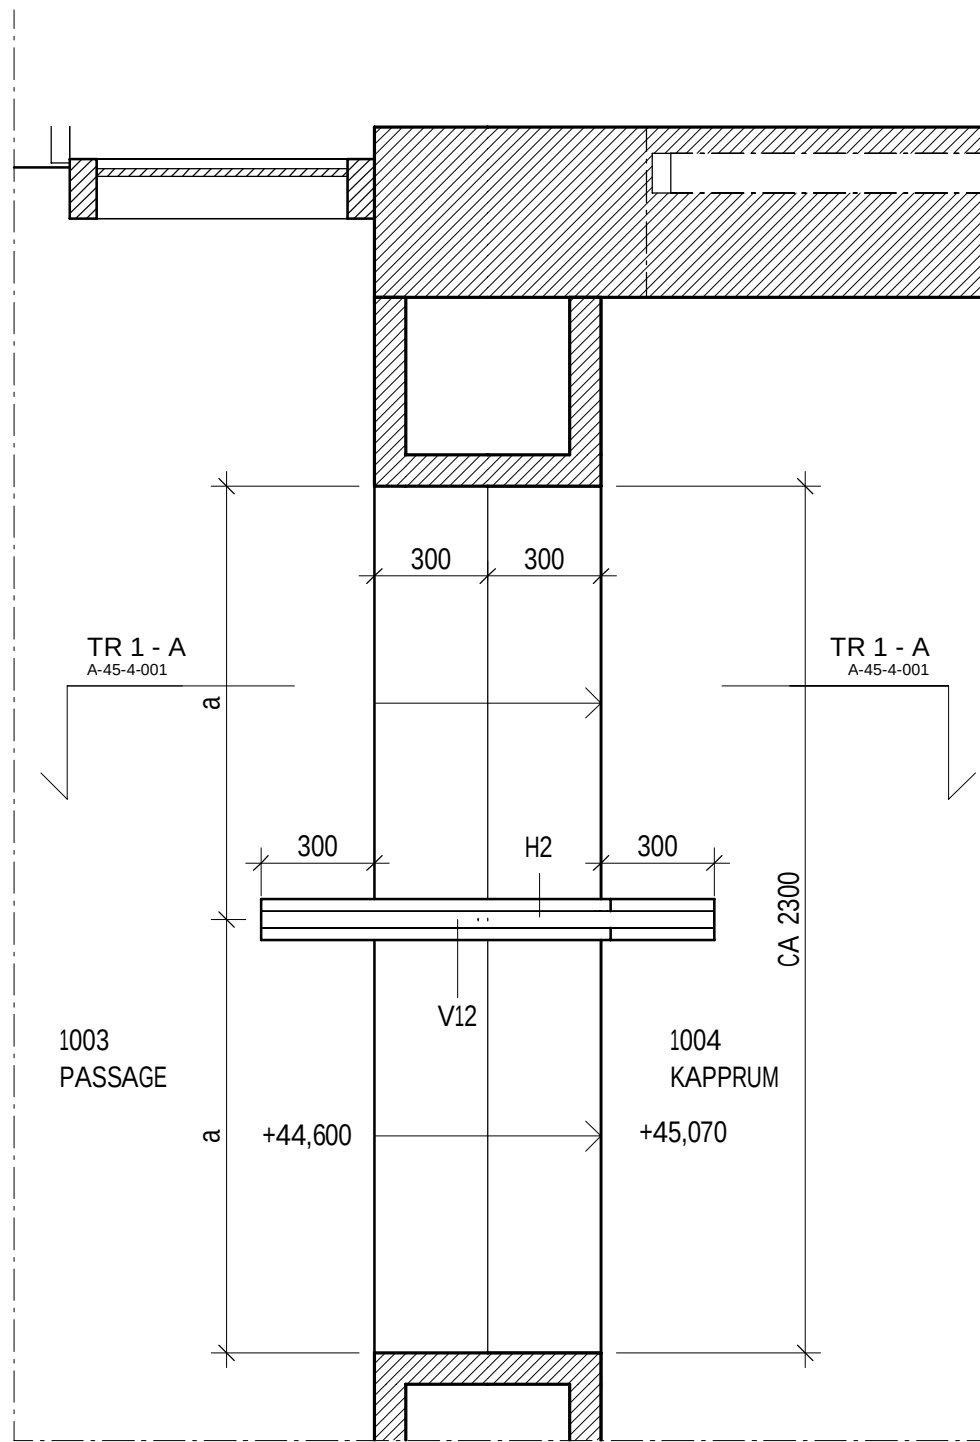


TRAPPA 1 - PLAN
1 : 20

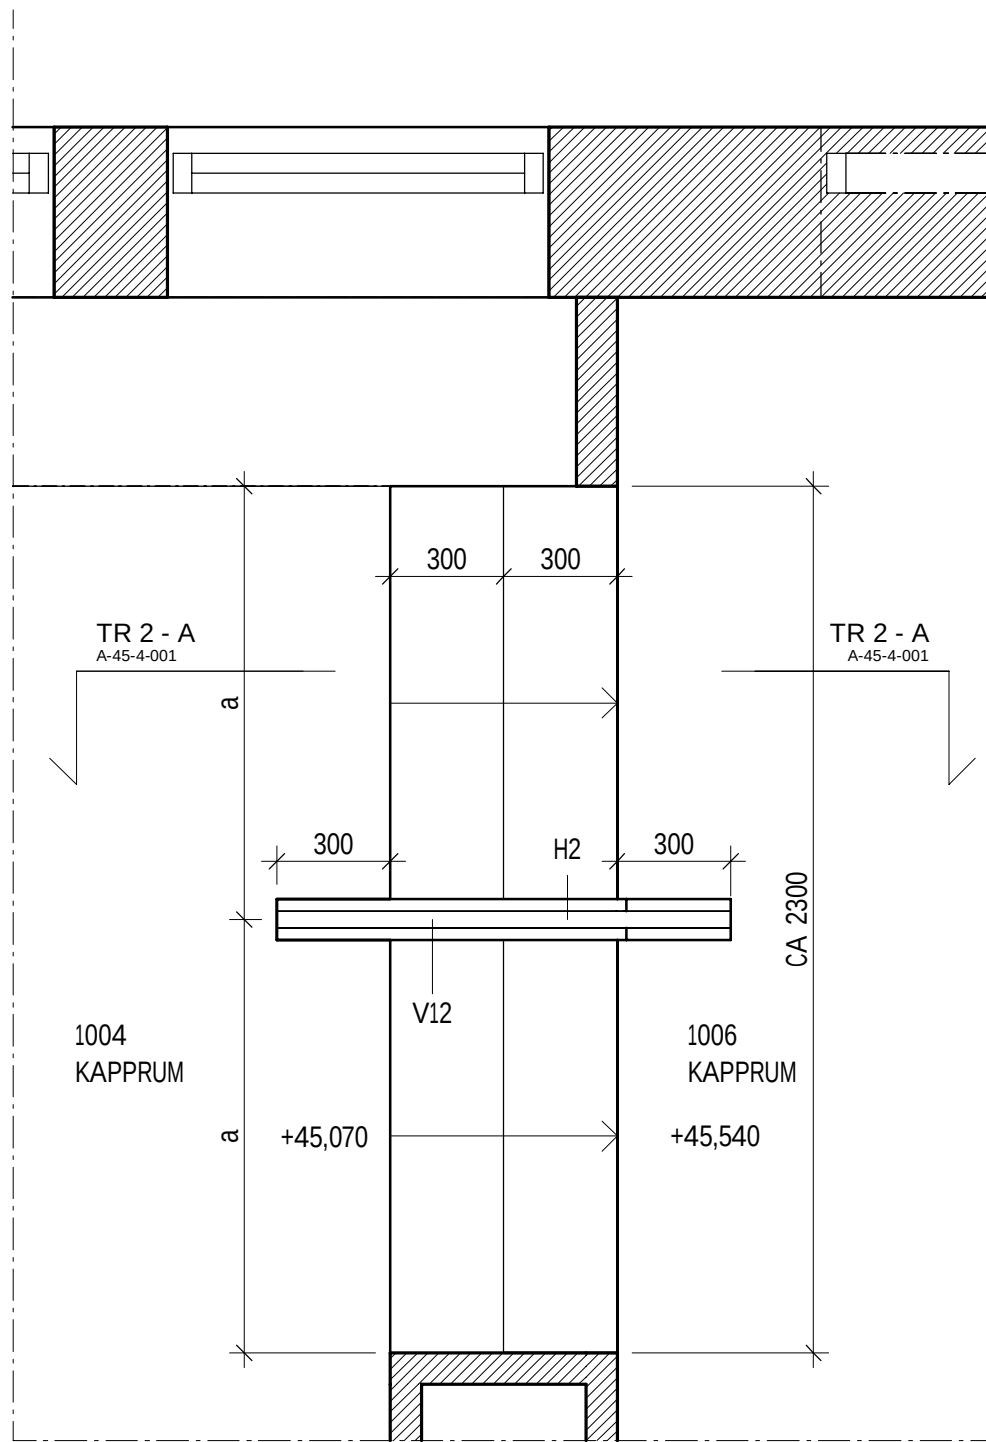


TRAPPA 2 - PLAN
1 : 20

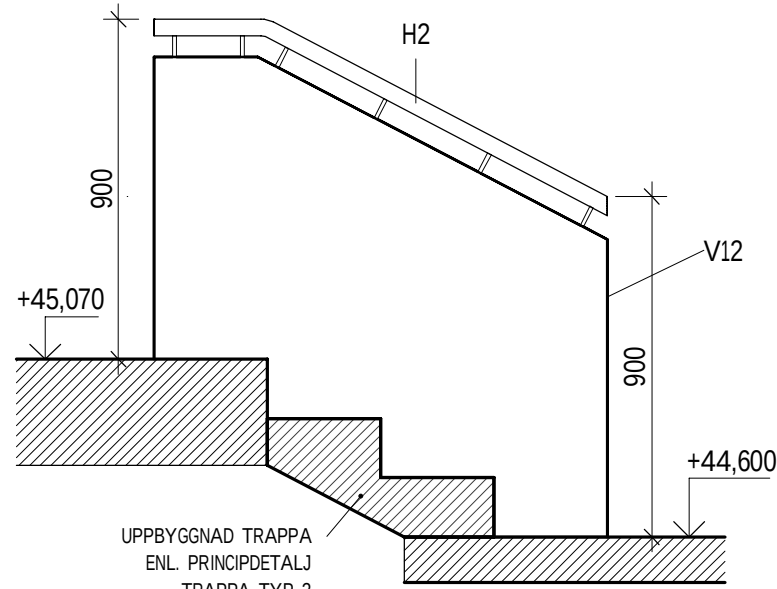

TRAPPA 1 - SEKTION A
1 : 20

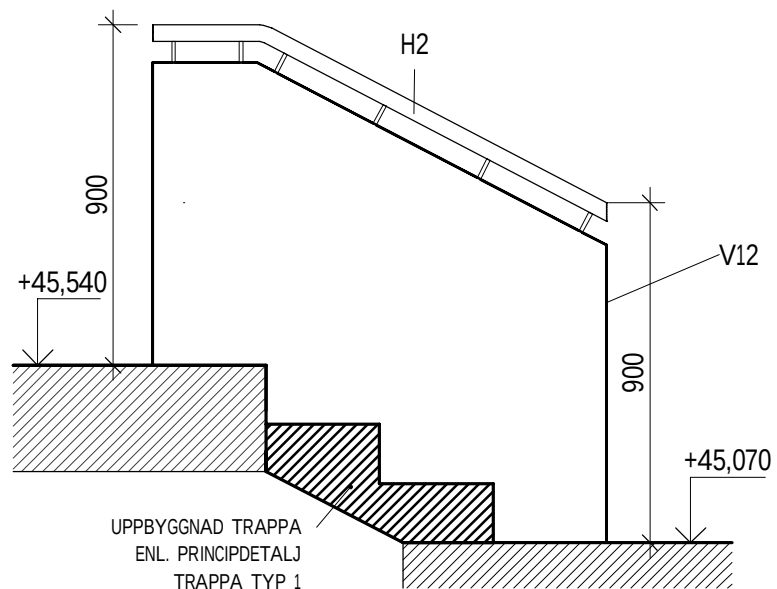


TRAPPA 2 - SEKTION A
1 : 20

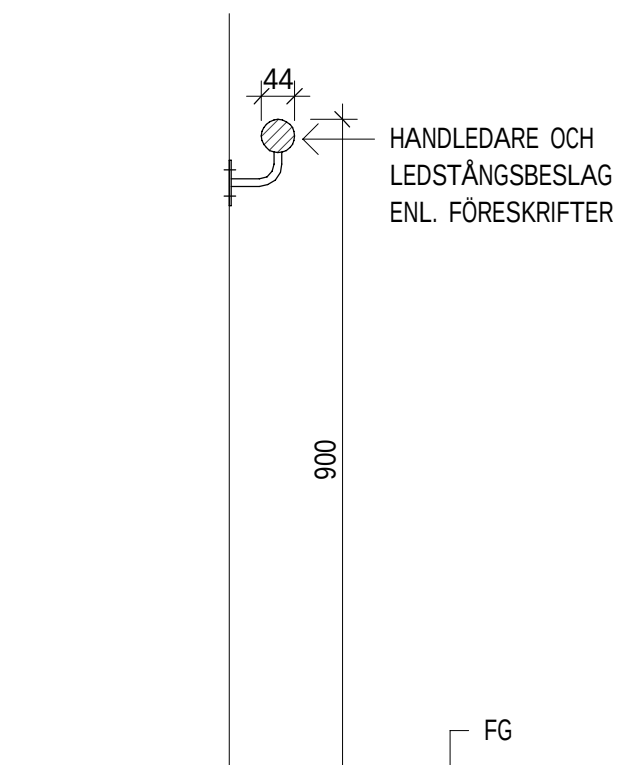


PRINCIP HANDELDARE H1
1 : 10


3ST INFÄSTNINGAR PER TRAPPA
(EN PER KANT OCH EN I MITTEN)
MED VB TYP JOMA VINKEL 410
M. 10MM BULTHÅL
FÄSTIS TILL BETONG 1ST TYP
HILTI HUS3-H 8x55,
TILL TRÅ 2ST ANKARSKRUV
4,5x32.

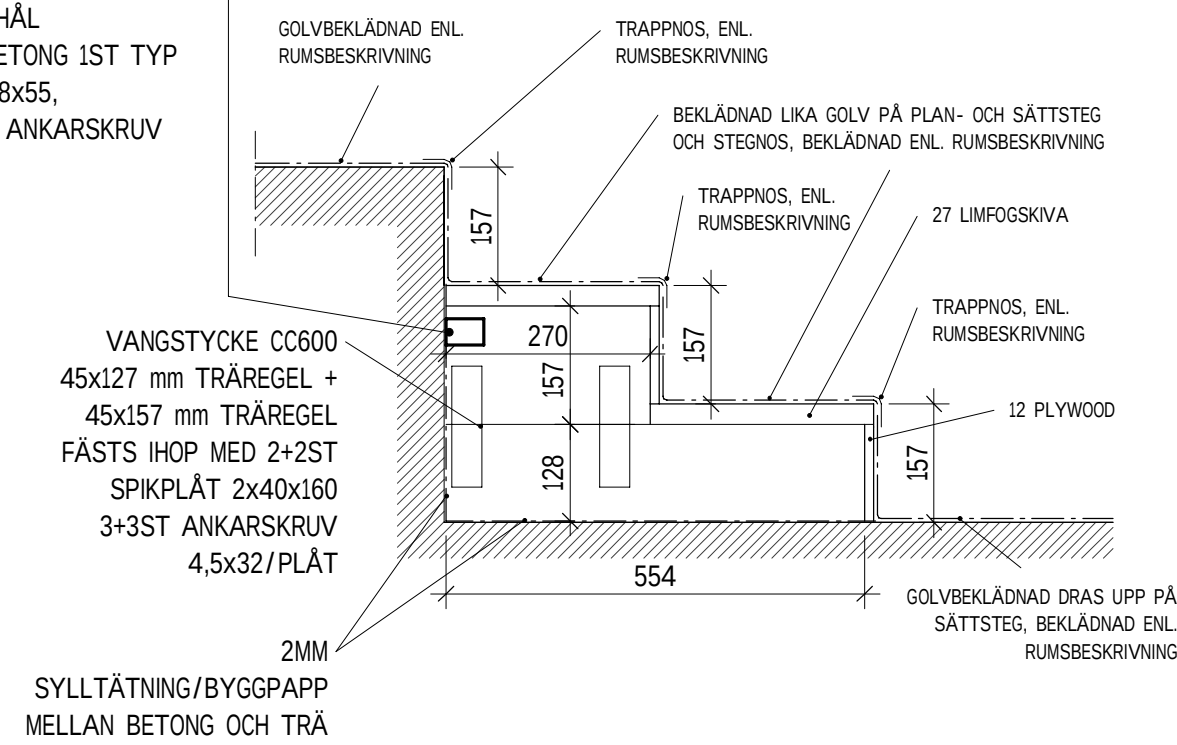


PRINCIPDETALJ TRAPPA TYP 1
1 : 10

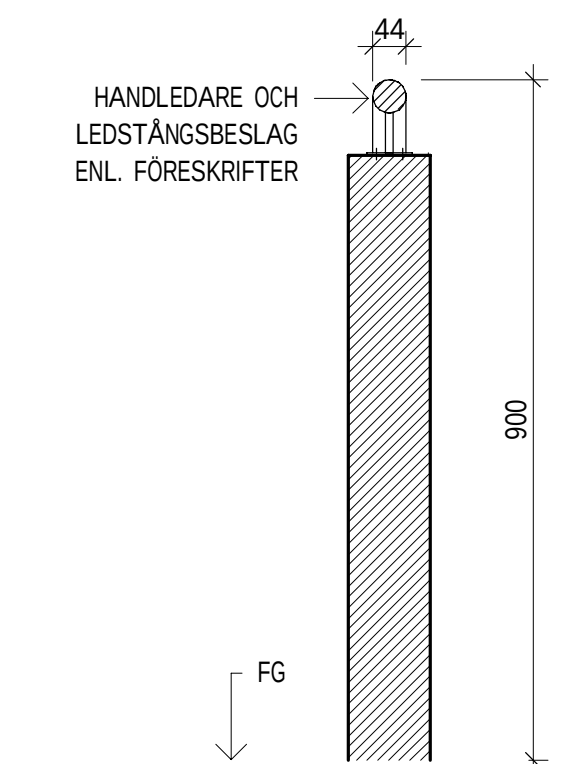

PRINCIPSEKTION HANDELDARE H2
1 : 10

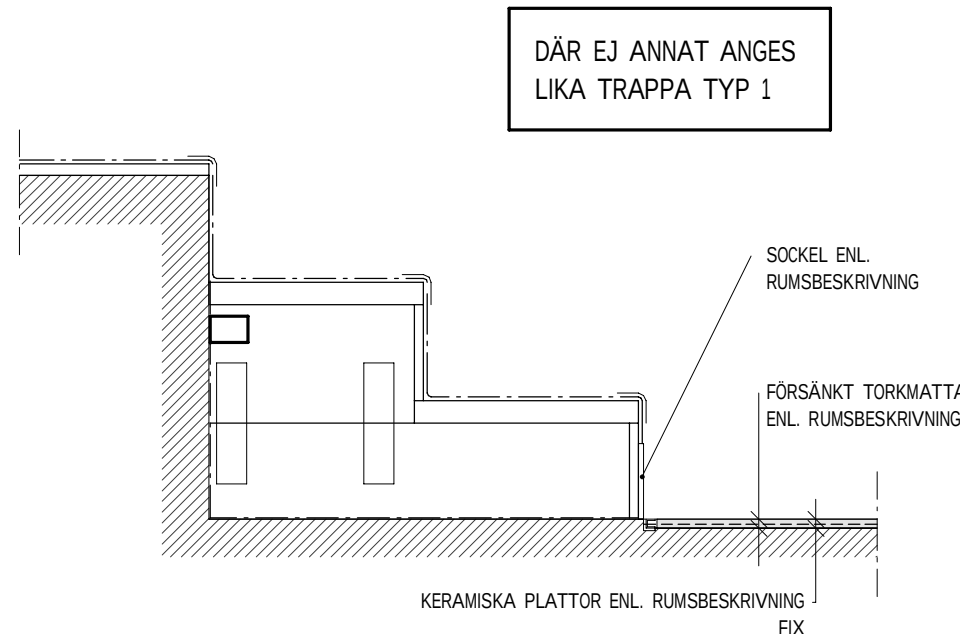

PRINCIPDETALJ TRAPPA TYP 2
1 : 10

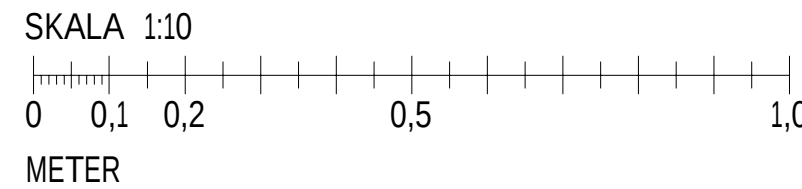

FÖRKLARINGAR

Samtliga mått anges i millimeter.
Mått kontrolleras på plats innan tillverkning.

FÖRESKRIFTER

Leverantören dimensionerar och anpassar räckan samt infästning.
Räckan ska uppfylla krav på personsäkerhet och barnsäkerhet enl. gällande BBR.

HANDELDARE H1

Handledare av ek typ Wiklunds Ledstångssnickeri eller likv.
Laseras i kulör NCS S 6005-Y20R eller närmsta färg.
Ledstångsbeslag i rostfritt stål enl. fabrikantens standard.
Infästning enl. fabrikantens standard.

HANDELDARE H2

Handledare av ek typ Wiklunds Ledstångssnickeri eller likv.
Laseras i kulör NCS S 6005-Y20R eller närmsta färg.
Ledstångsbeslag i rostfritt stål enl. fabrikantens standard.
Infästning enl. fabrikantens standard.

RÄCKE R1

Balkongräcke i sträckmetall, RT300H Sträckmetall, fabrikant standard enl. Weland eller likv.
OBS! Utan handledare ovanpå.
Stolpe, infästning och beslag enl. fabrikantens standard.
Sidomontage & fästdon för betong enl. fabrikantens standard.
Maskvidd: 42x18 mm
Mönster: stående mönster
Kulör: RAL 9002


RÄCKE R2

Balkongräcke i sträckmetall, RT300H Golvräcke, fabrikant standard enl. Weland eller likv.
OBS! Utan handledare ovanpå.
Stolpe, infästning och beslag enl. fabrikantens standard.
Golvräcke & fästdon för betong enl. fabrikantens standard.
Maskvidd: 42x18 mm
Mönster: stående mönster
Kulör: RAL 9002


HÄNVISNINGAR

PLAN - ÖVERSIKT, BRAND A-40-1-001
PLAN 1, DEL 4.1 A-40-1-141
PLAN 1, DEL 5.1 A-40-1-151


GRUNDPLAN ÖVERSIKT K-15-1-100

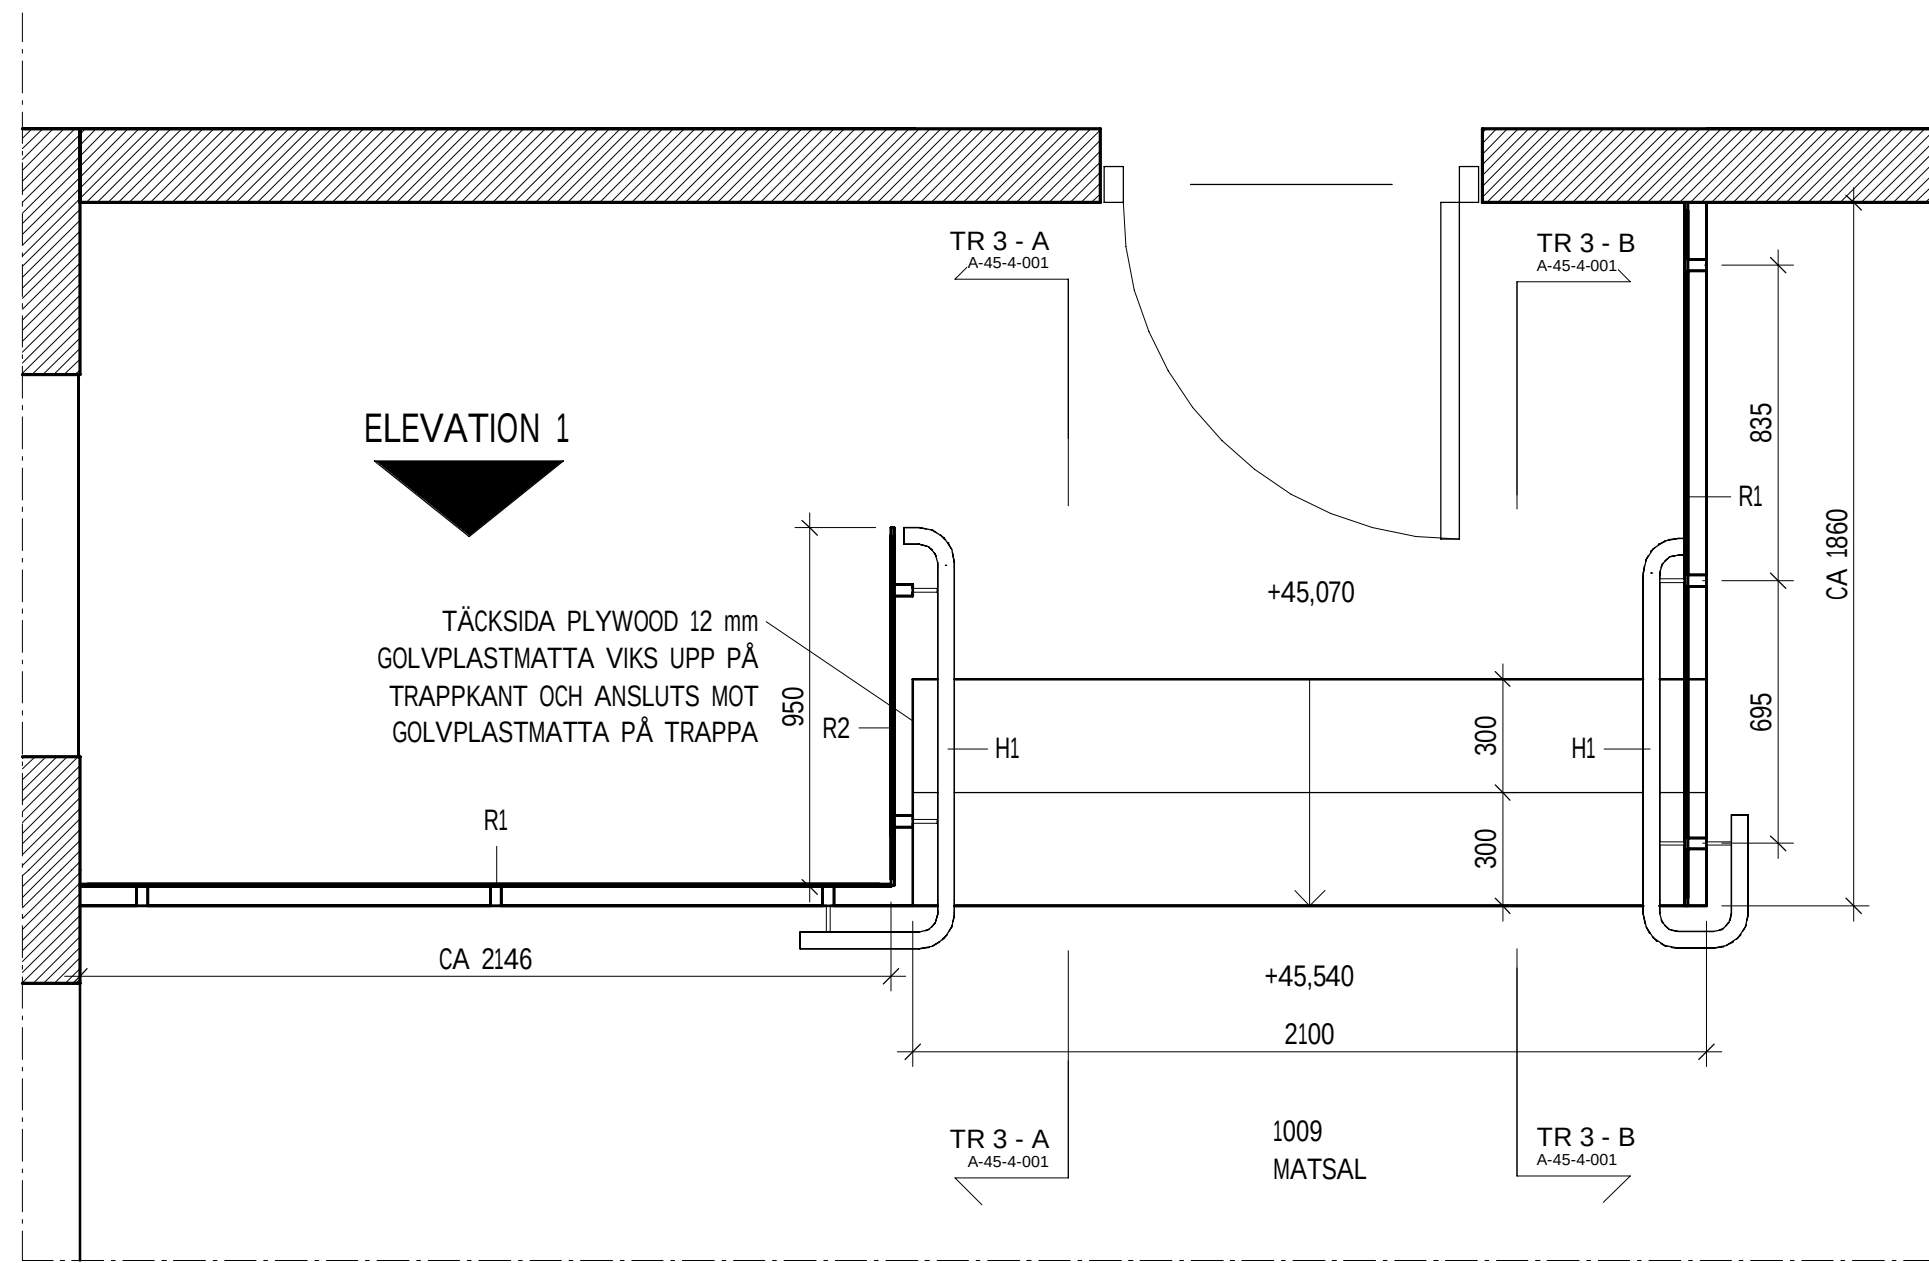


TRAPPA 3 - PLAN
1 : 20

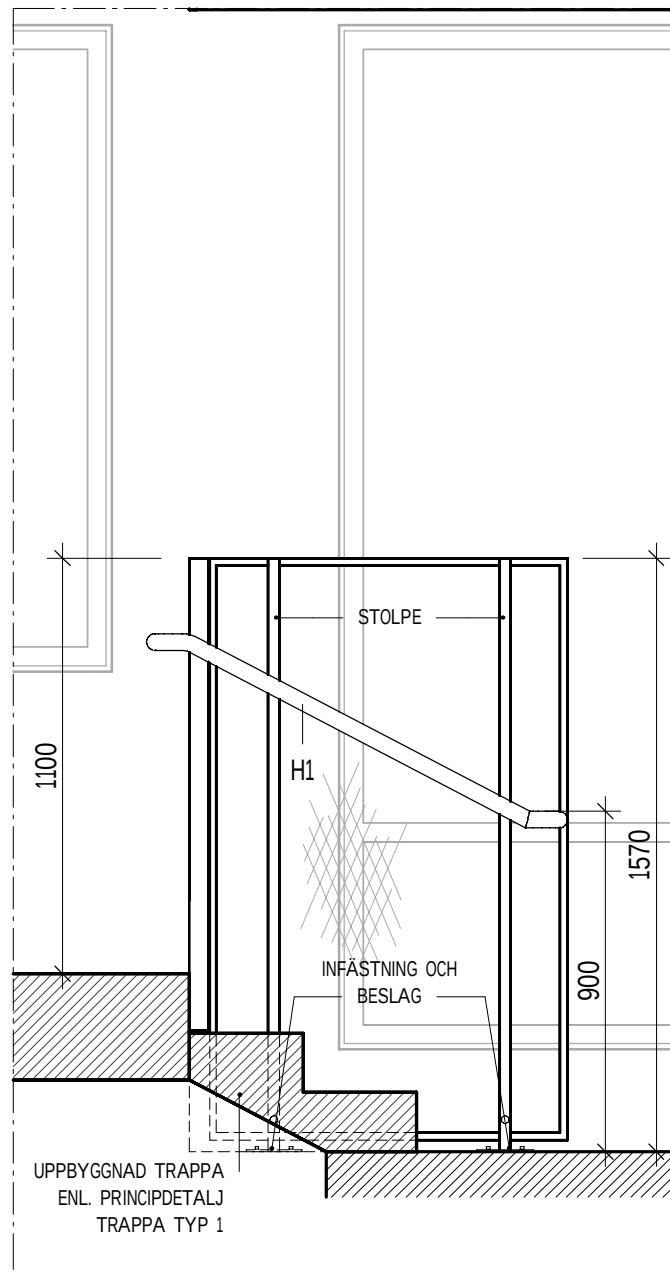


TRAPPA 3 - SEKTION A
1 : 20

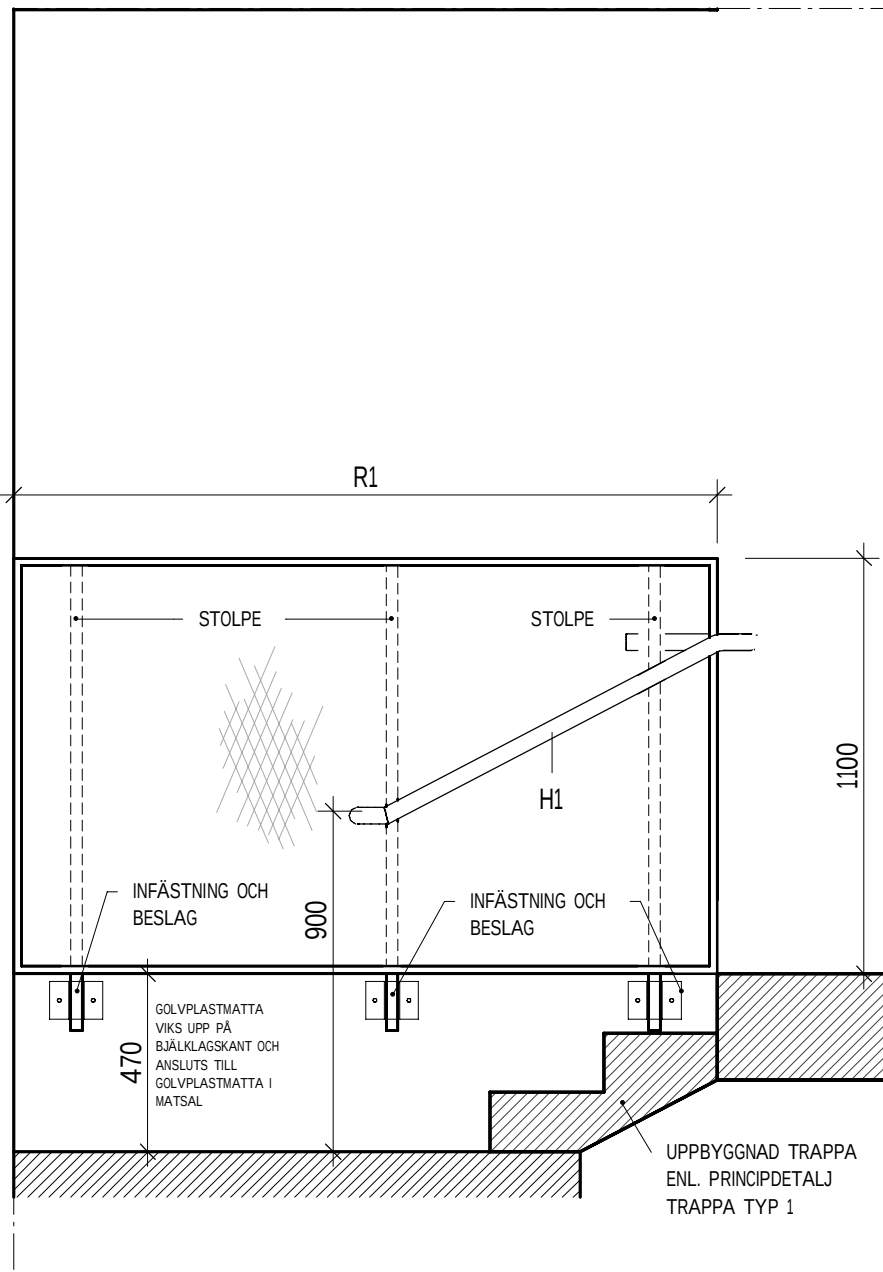

TRAPPA 3 - SEKTION B
1 : 20

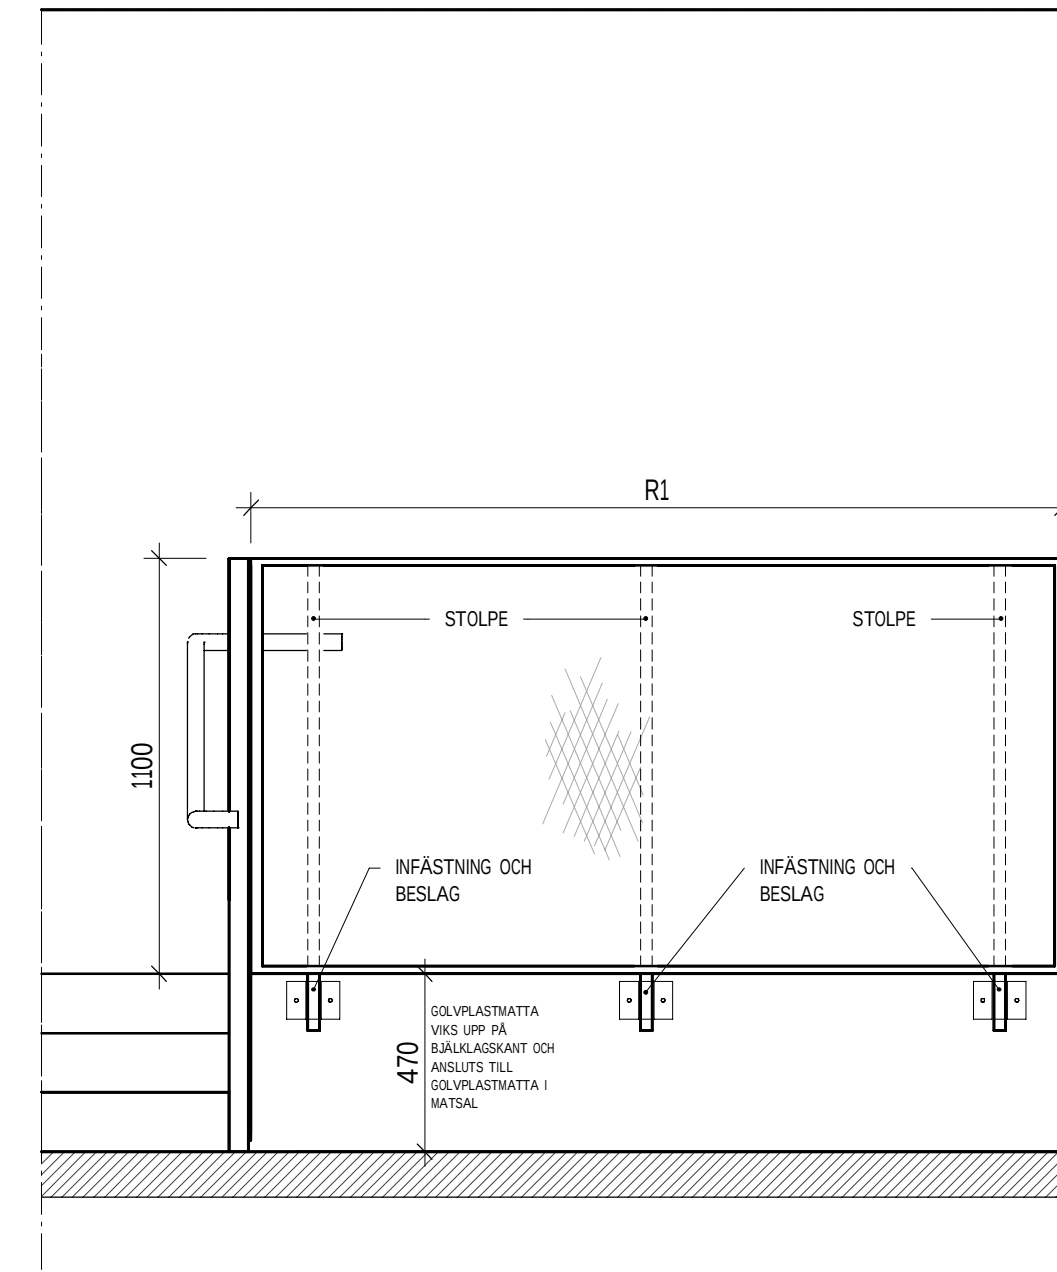

ELEVATION 1 - RÄCKE TYP R1
1 : 20

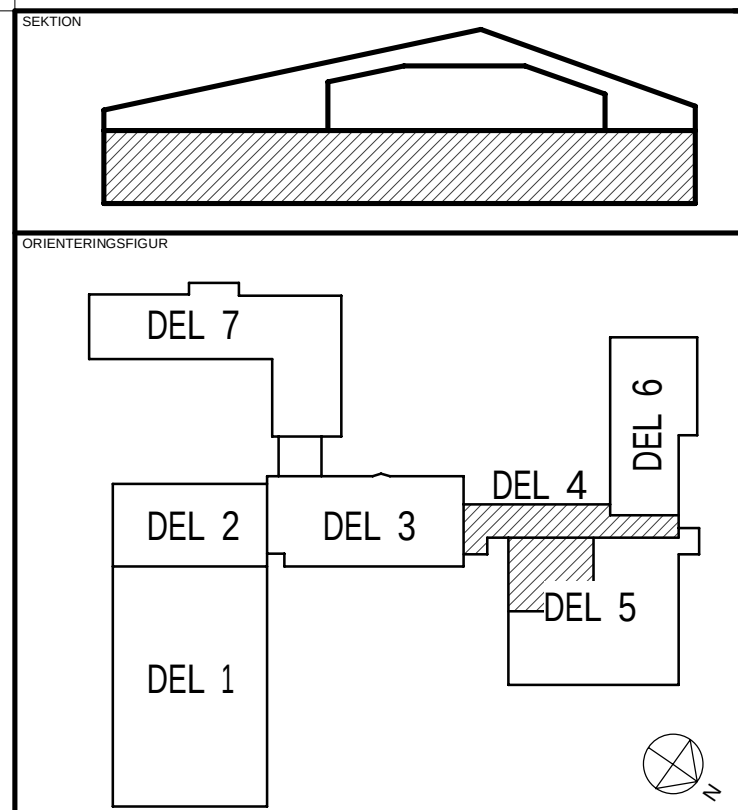

FÖRFRÅGNINGSUNDERLAG

HANDLING BYGGHANDLING
DATUM 2024-12-20 FÖRSTÄLLNING T. BERGSTRÖM
BESTÄLLARE



CENTRALKÖK

PROJEKTNAMN ROBERTSFORS KOMMUN
PROJEKTNUMMER
FÖRSTÄLLNING YTTRE RINGVÄGEN 4
DIARIENUMMER FORDONET 1
DISCIPLIN
UPPDRAGSNUMMER NORCONSULT SVERIGE AB
108 83 71
TELEFON
010 141 80 00
BYGGNADSTYRELSE
KONTAKTPERSON
TOMAS BERGSTRÖM
FÖRSTÄLLNING (VIT 2008)

SYSTEM 45 HUSKOMPLETTERINGAR
SPECIFIKATION TRAPPA, HANDELDARE, RÄCKE
UPPSTÄLLNING 1:20
A-45-4-001

FORMAT A1
ANVÄNDNING