




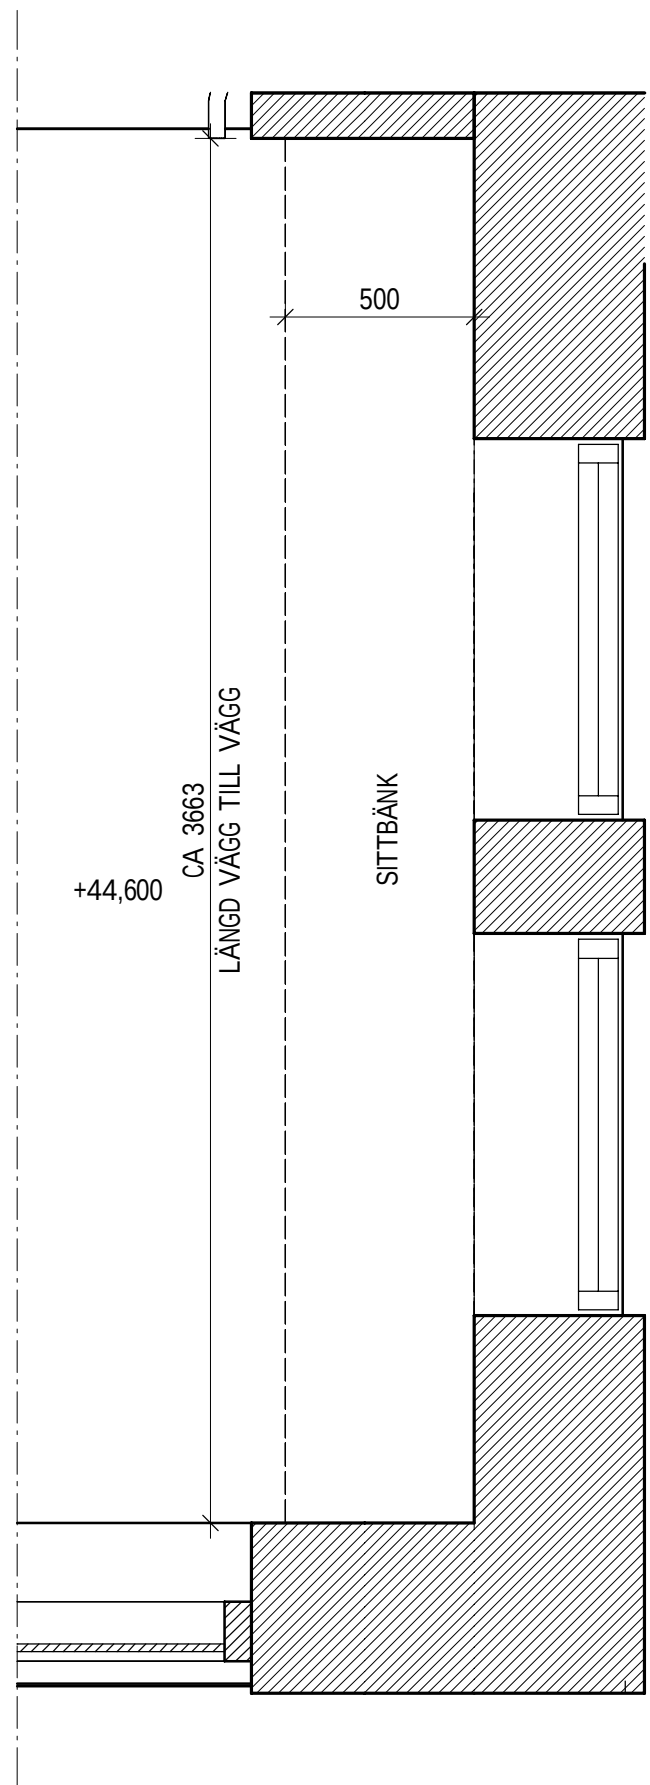



SITTBÄNK I VINDFÅNG 1001 - PLAN
1 : 20

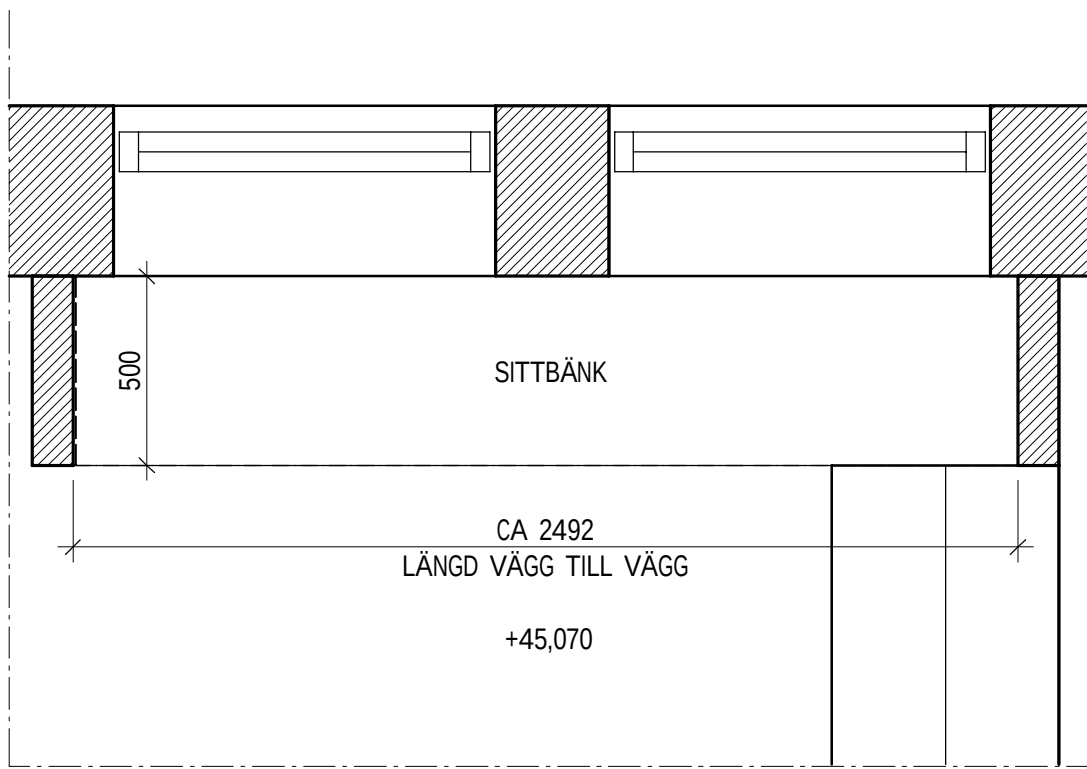

SITTBÄNK I KAPPRUM 1004 - PLAN
1 : 20

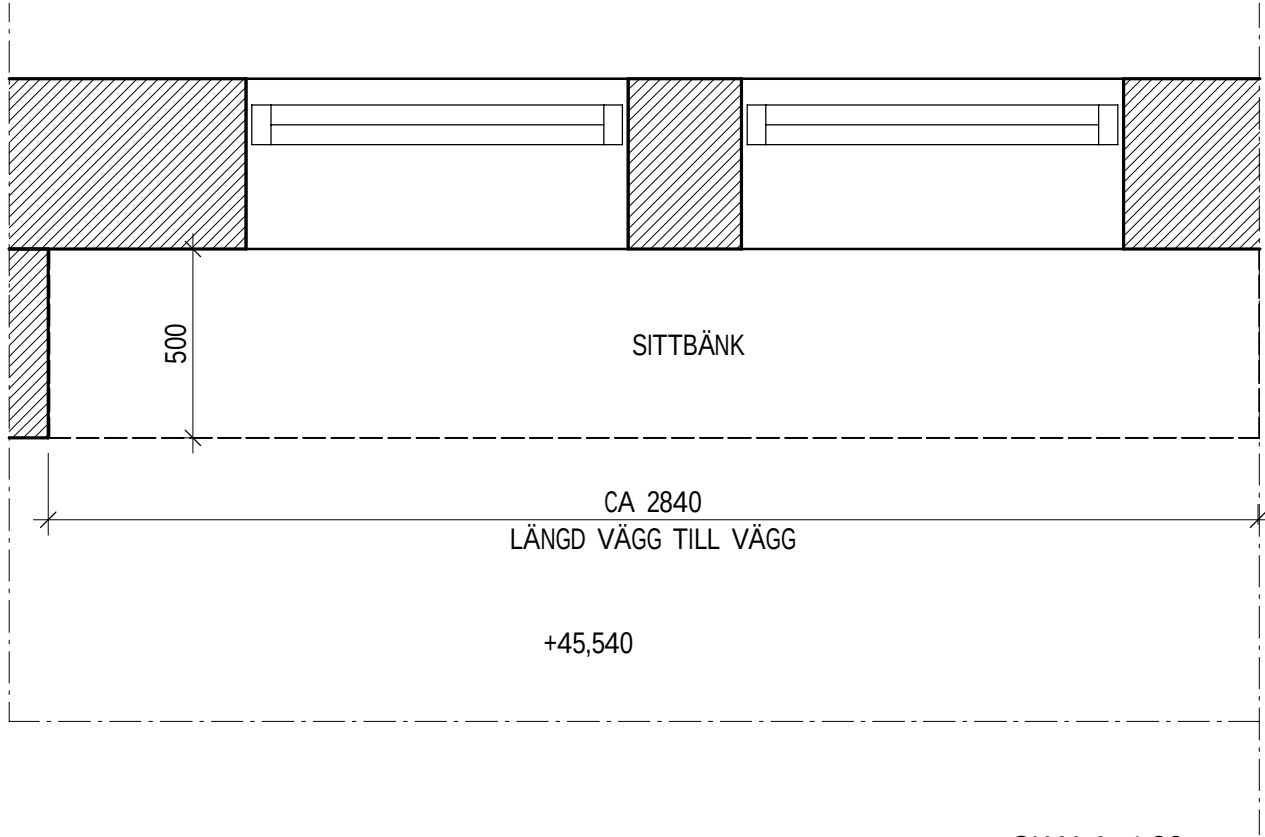

SITTBÄNK I KAPPRUM 1006 - PLAN
1 : 20

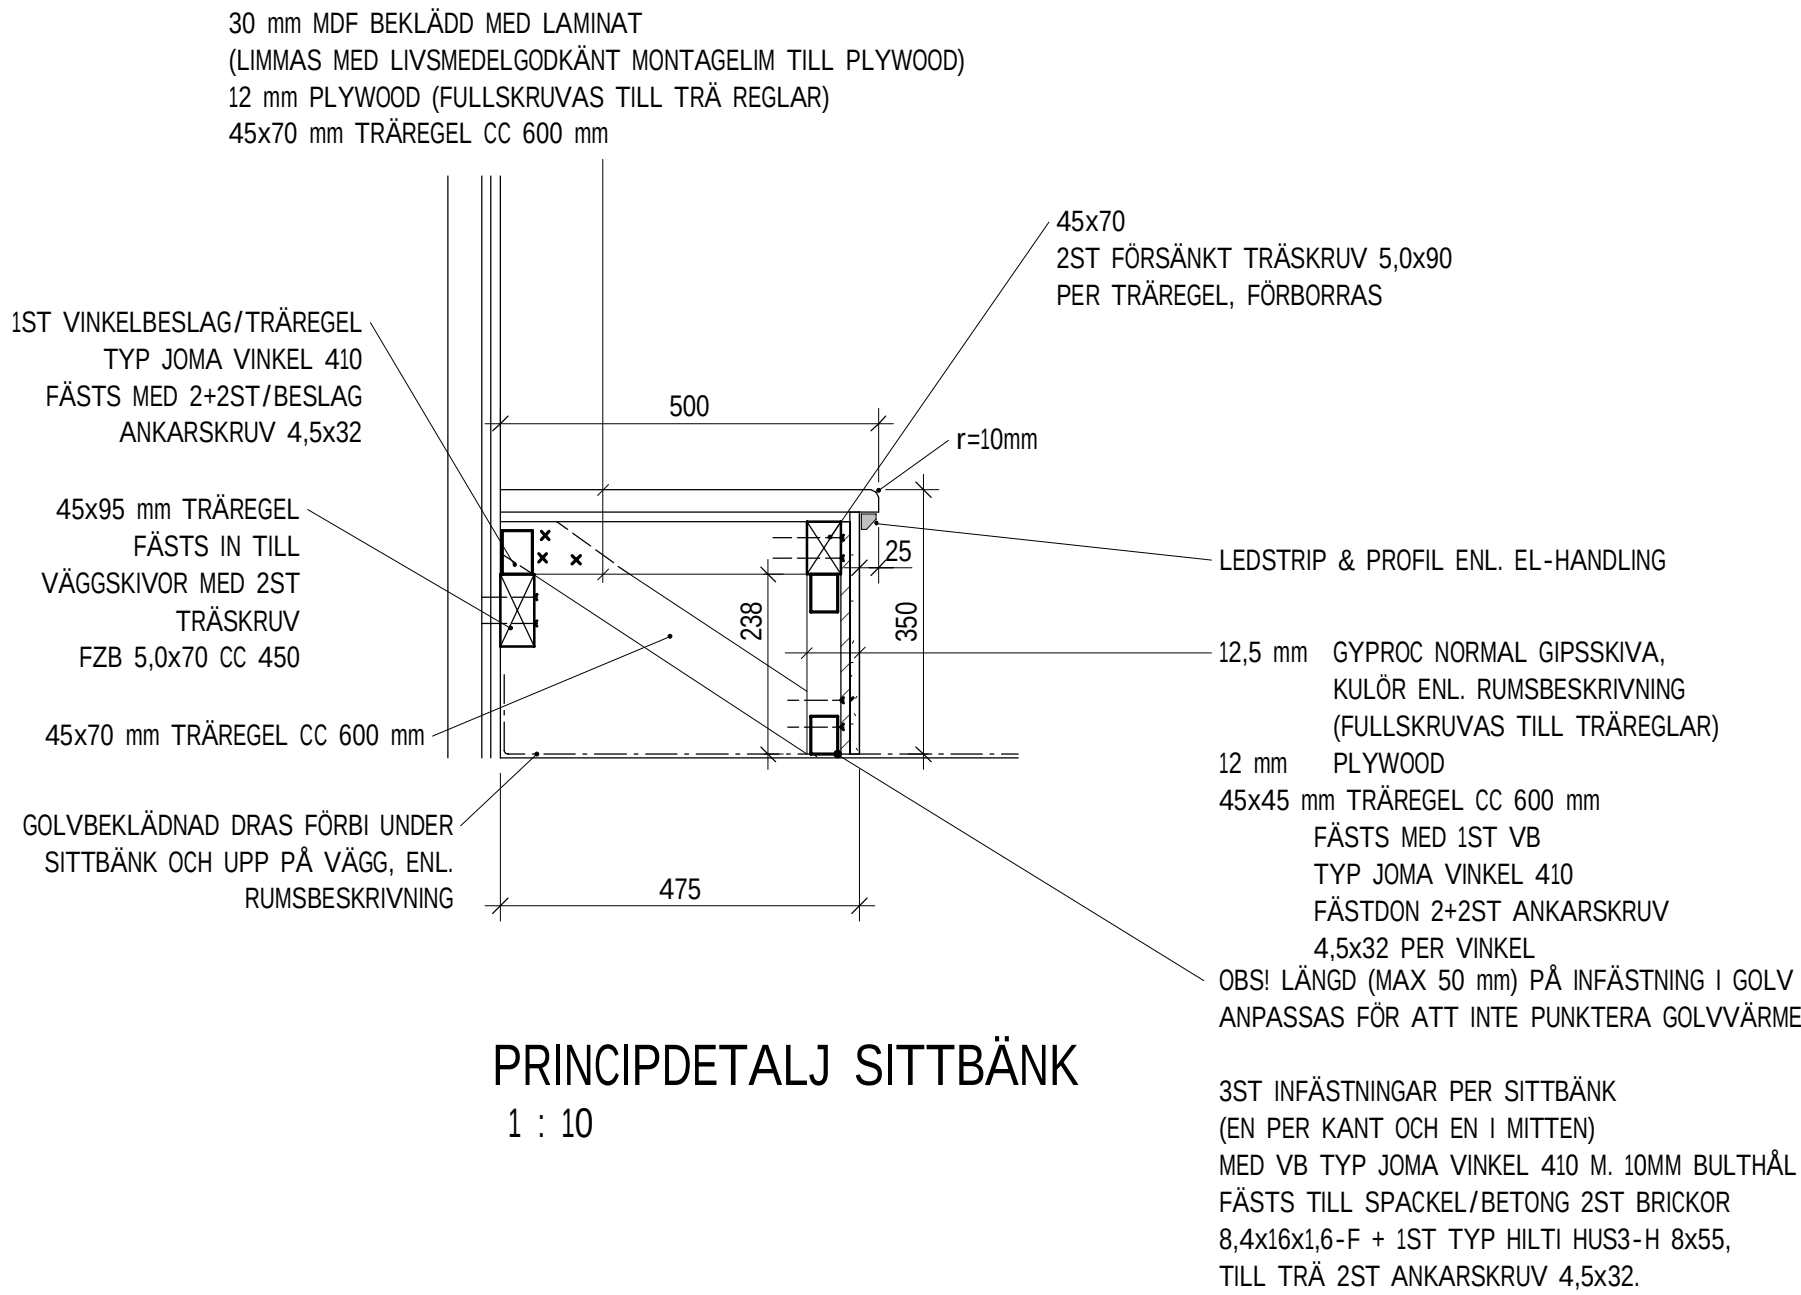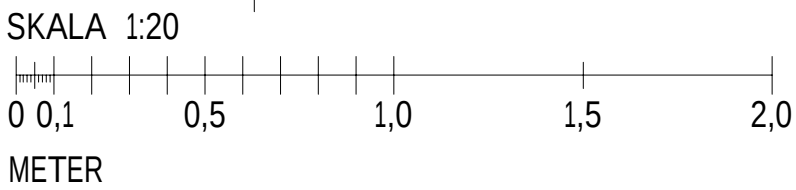


PRINCIPDETALJ SITTBÄNK
1 : 10


FÖRKLARINGAR
Samtliga mått anges i millimeter.
Mått kontrolleras på plats innan tillverkning.

FÖRESKRIFTER


HÄNVISNINGAR
PLAN - ÖVERSIKT, BRAND A-40-1-001

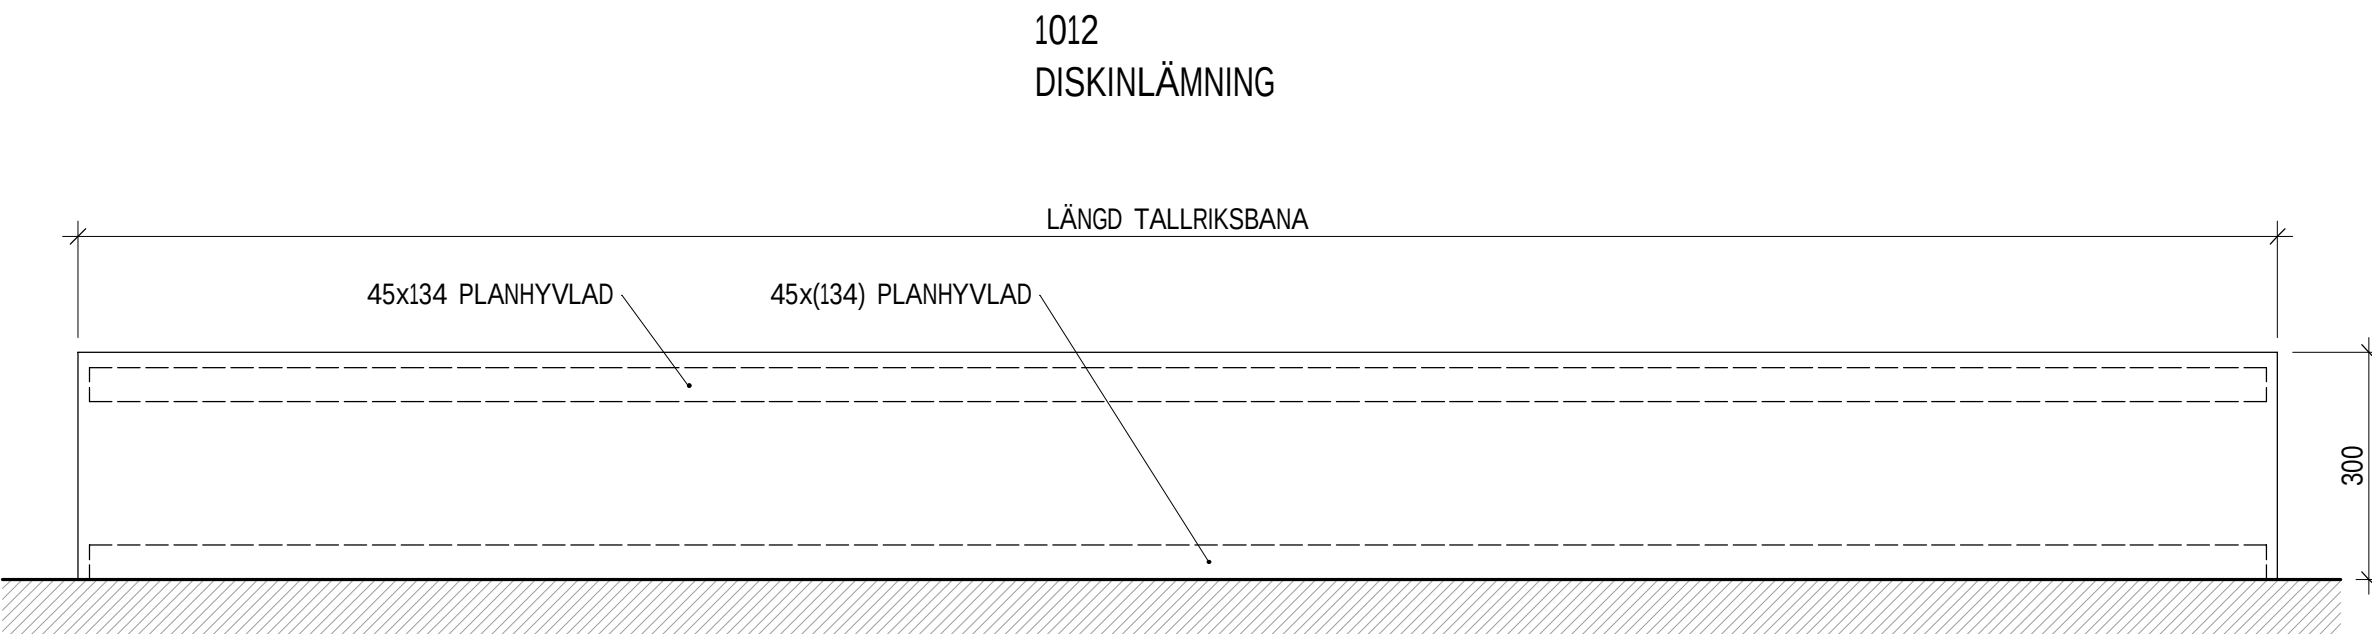


PLAN

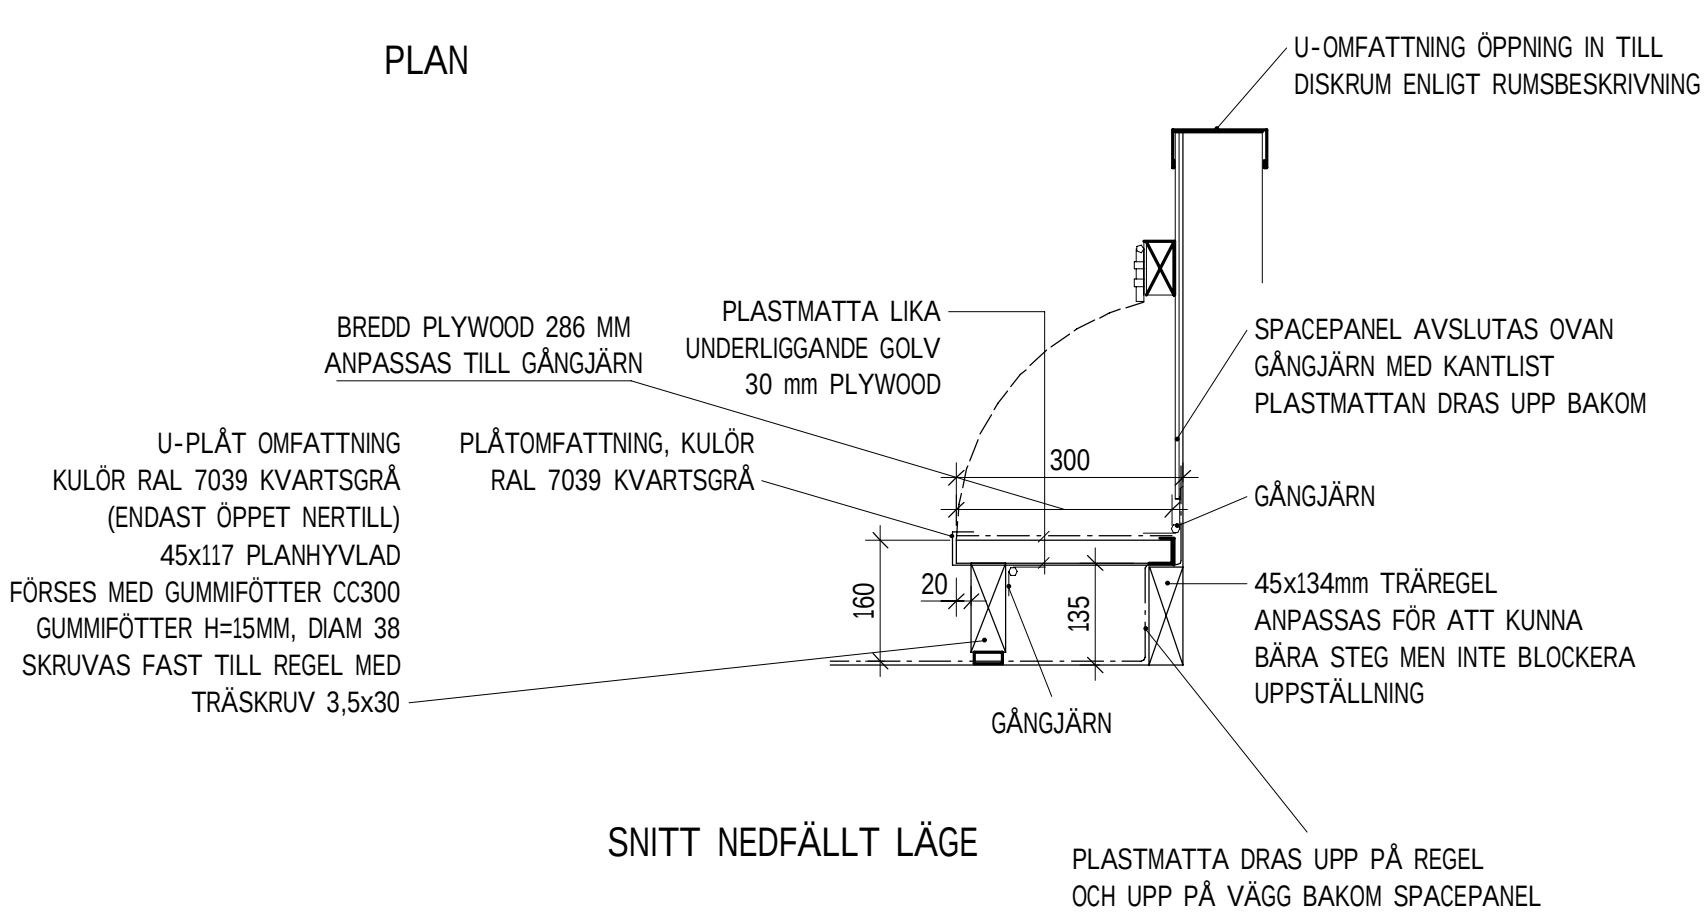

PRINCIPDETALJ STEG I DISKRUM
1 : 10

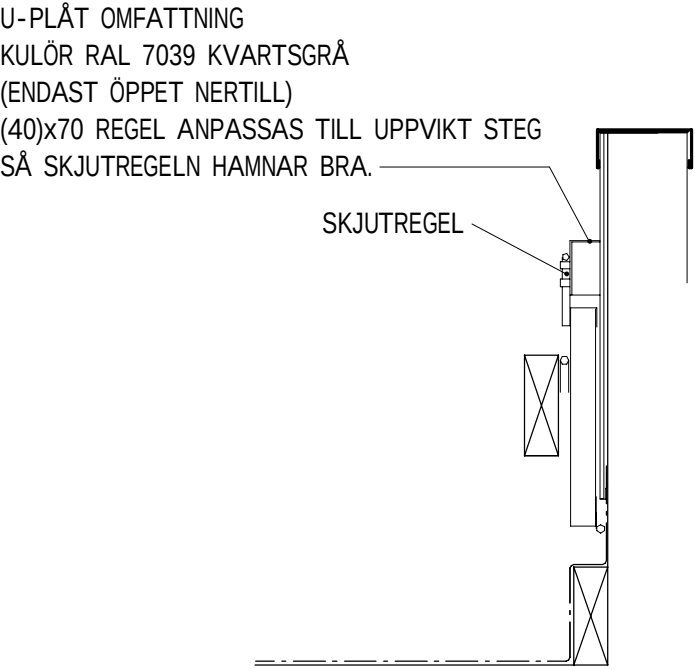

SNITT UPPFÄLLT LÄGE

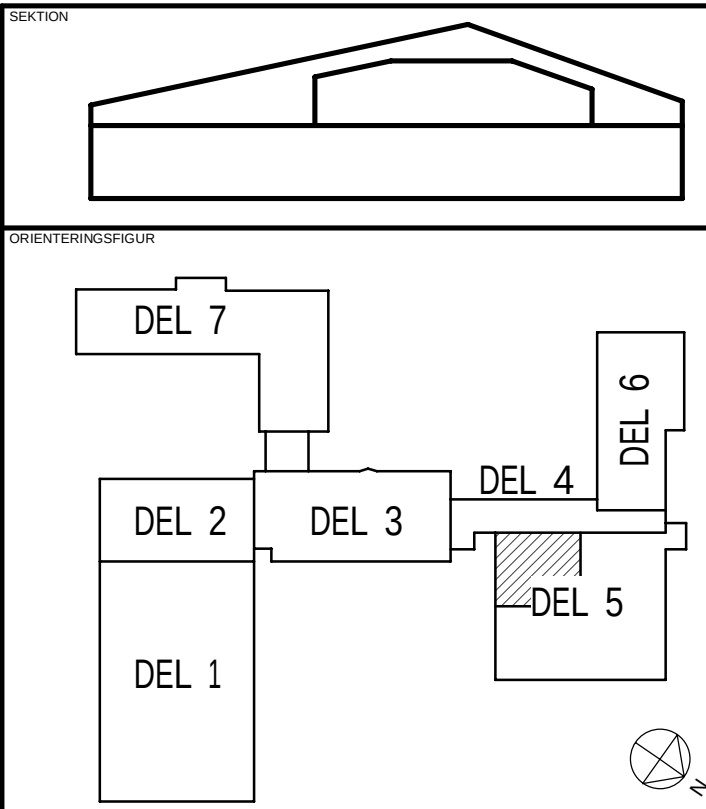

1012 DISKINLÄMNING

BYGGHANDLING

2024-12-20 T. BERGSTRÖM

ROBERTSFORS KOMMUN

CENTRALEKÖK

ROBERTSFORS KOMMUN

YTTRE RINGVÄGEN 4

FORDONET 1

NORCONSULT SVERIGE AB

SB

TOMAS BERGSTRÖM

1:10/1:20 A1

A-45-4-002