
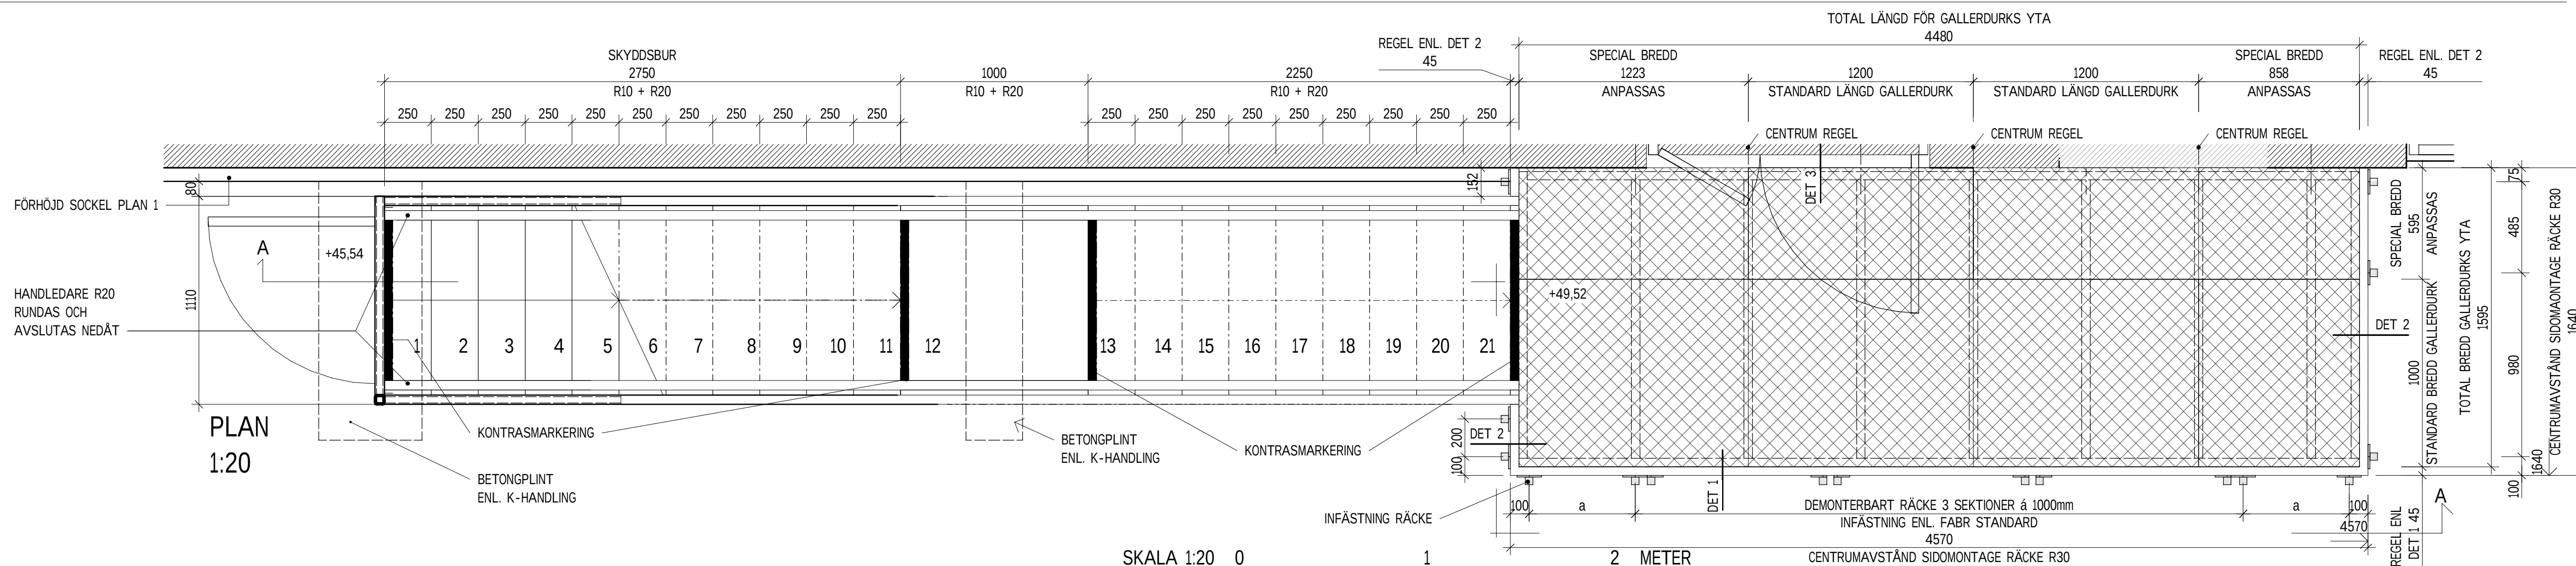
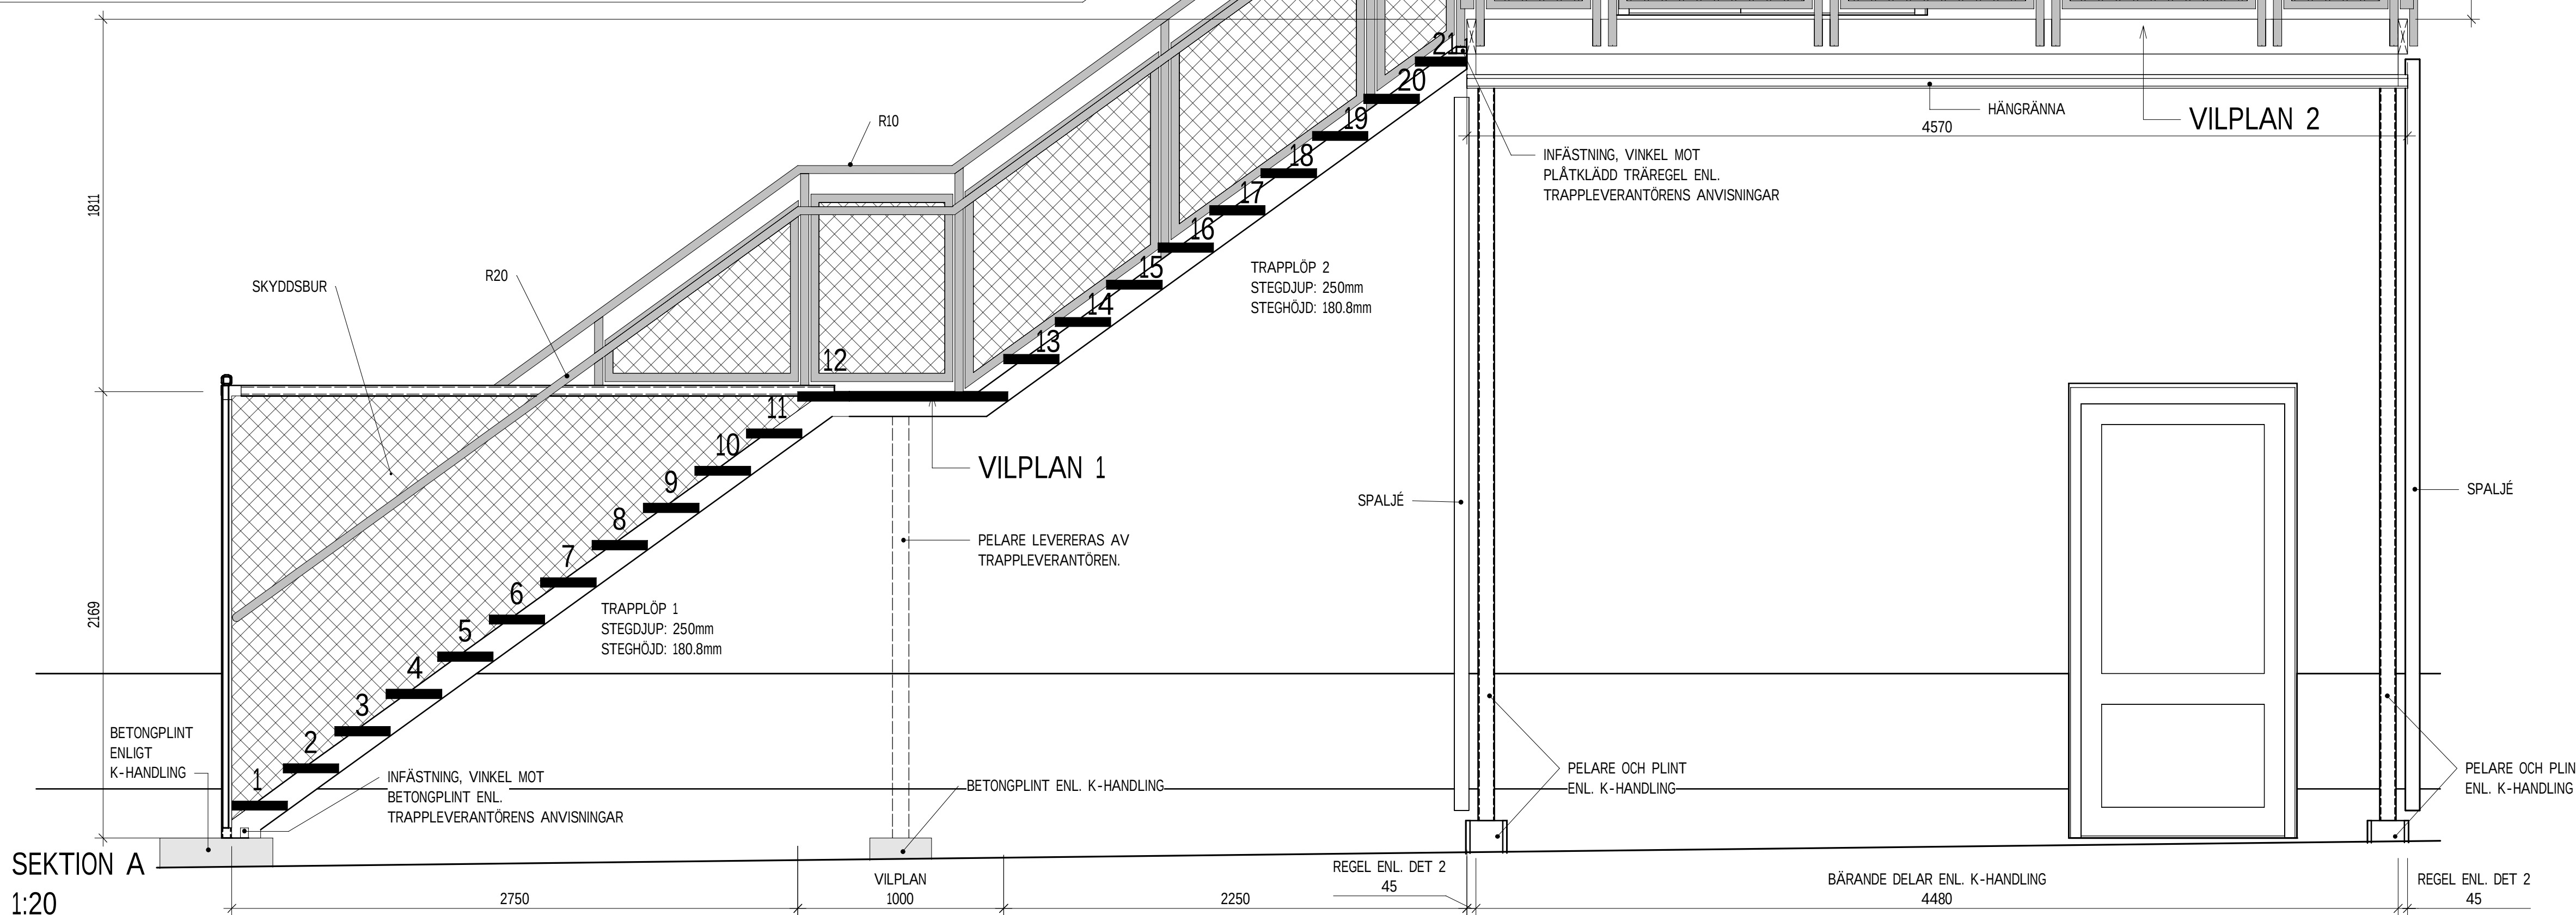
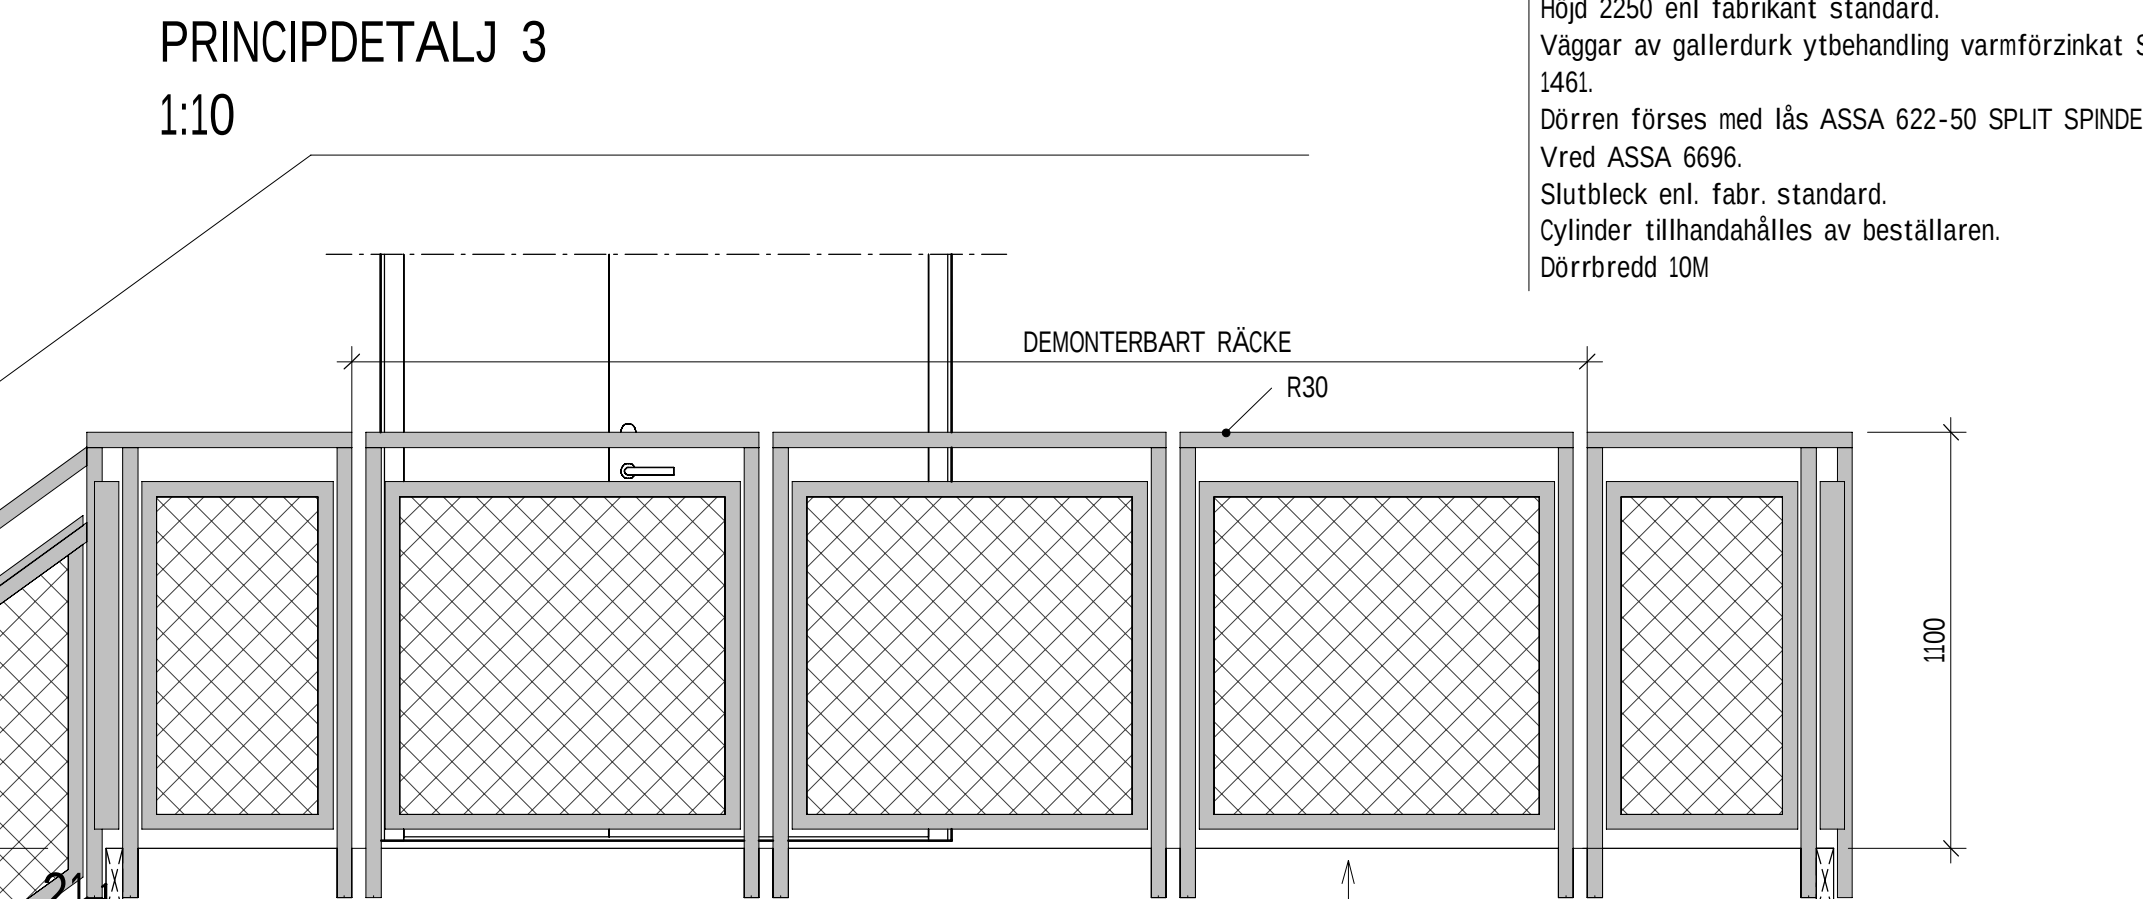
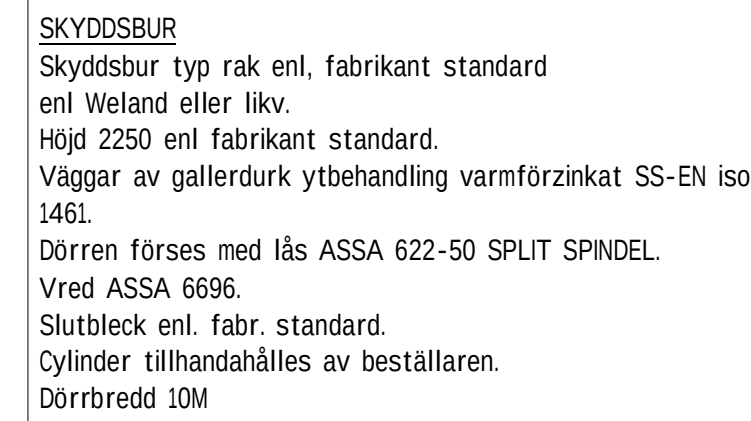
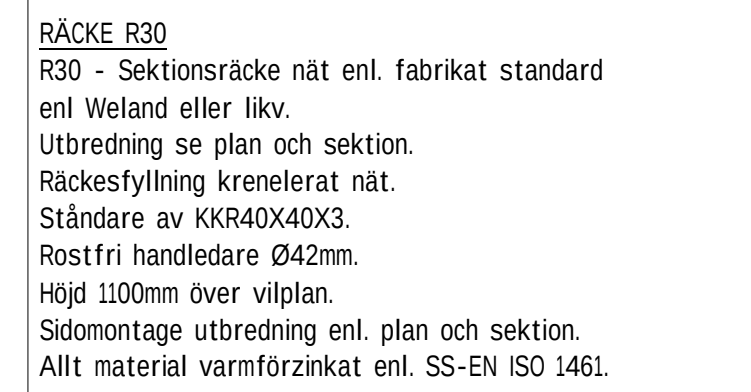
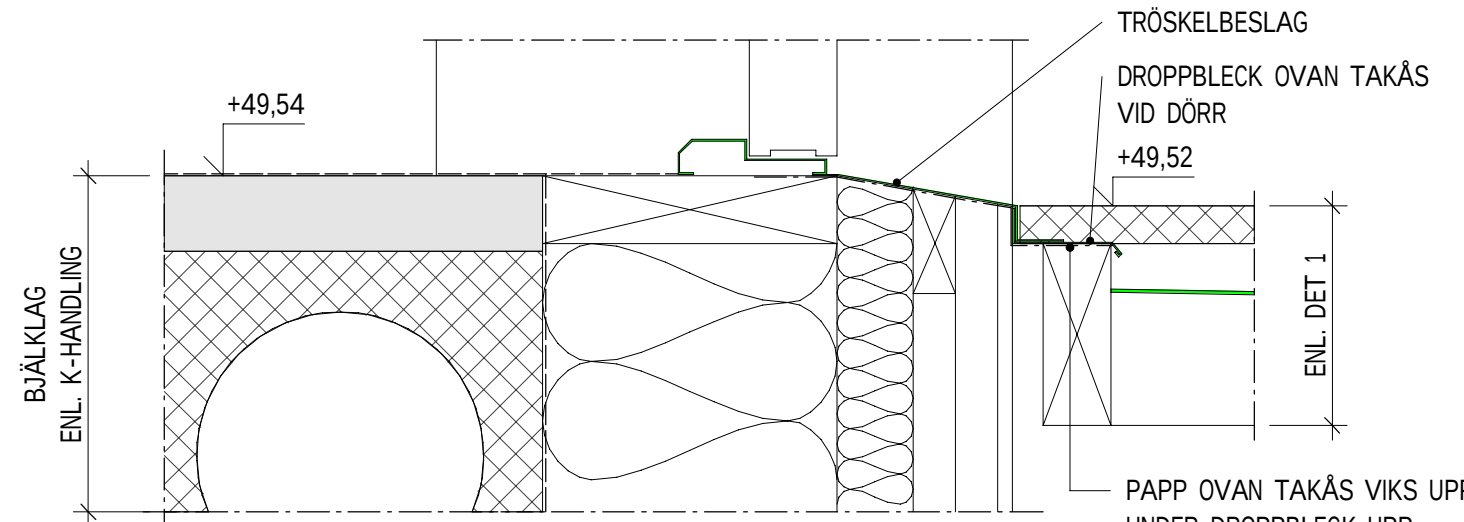


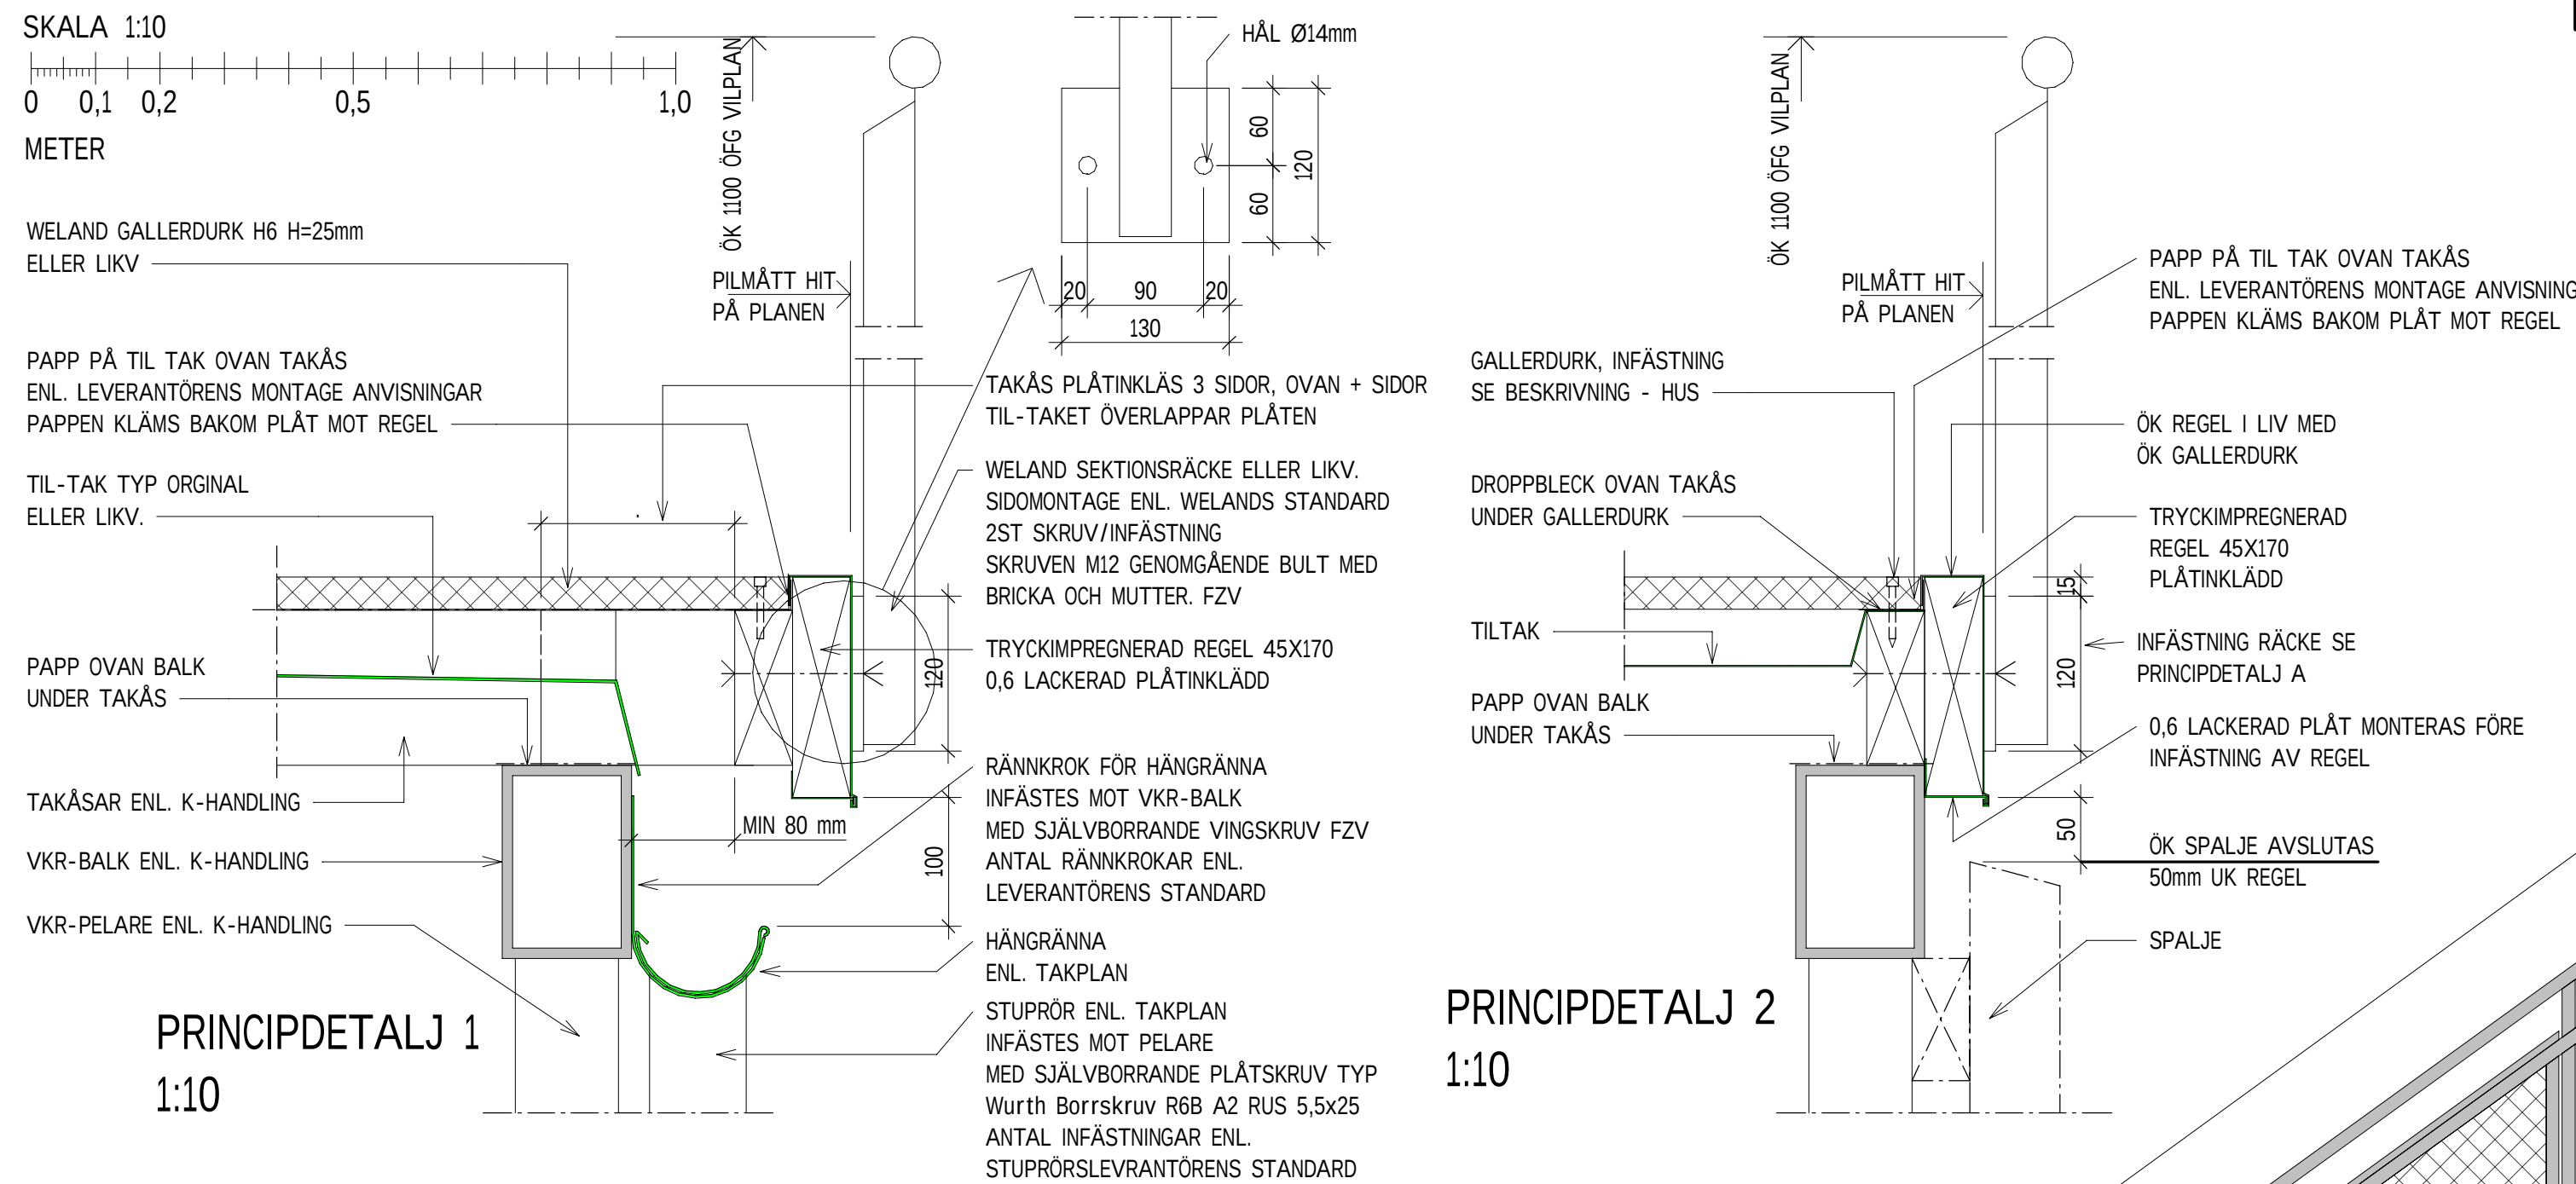

FÖRKLARINGAR

Samtliga mått anges i millimeter.
Mått kontrolleras på plats innan tillverkning.

██████████ = Kontrastmarkering i svartlacerad stansad plåt halksäker på första och sista steget fabrikat standard enl. Weland eller likv. markerat på plan.

FÖRESKRIFTER

Trappleverantören dimensionerar bärigheten och levererar pelare, balkar med erforderlig infästnings skruv.

RAK TRAPPA

Rak trappa med vilpan utförs enl. fabrikat Weland eller likv.
 Trappbredd = 1110mm (sättsteg + vagnsteg)
 Trapplopp 1 - utliggning 2750mm höjden 2169mm.
 Ist vilpan längd 1000mm.
 Trapplopp 2 - utliggning 2250mm höjden 1811mm.
 Sättsteg som skruvas till stegen enl. fabr. std steg av
 gallerduk Th6-S din 1000mm x 250mm enl. fabrikantens std.
 masköppning c/c 34x775mm med säkerhetsfrankant.
 (halskydd).
 Räcke på båda sidor,
 Ytbehandling varmförzinkad.
 Första steget etj steg ner från vilpan 2.

RÄCKE R10

R10 - Sektionsräcke typ nät fabrikat standard
enl. Weland eller likv.
Utbredning se plan och sektion.
Räckesfyllning krenelerat nät.
Ståndare av KKR40X40X3.
Rostfri handledare Ø42mm.
Höjd 1100mm över trappsteg.
Toppmontage utbredning enl. plan och sektion.
Allt material varmförzinkat enl. SS-EN ISO 1461


HANDLEDARE R20

R20 - Handledare av rostfritt utförande enligt fabrikant standard, rör 42mm typ Welands eller likv. 900mm över vilplan och trappsteg, utbredning se plan och sektion.
Handledare ska rundas in mot skyddsbursvägg vid trappans slut. Vid trappans början skall handledaren rundas in mot räcket.
Infästning i skyddsbursväggen och sektionsräcke enl. fabrikantens standard.

HÄNVISNINGAR

PLAN - ÖVERSIKT, BRAND	A-40-1-001
SPALJÉ	A-45-4-004

GRUNDPLAN ÖVERSIKT	K-15-1-100
SEKTION, DETALJER	K-20-6-001

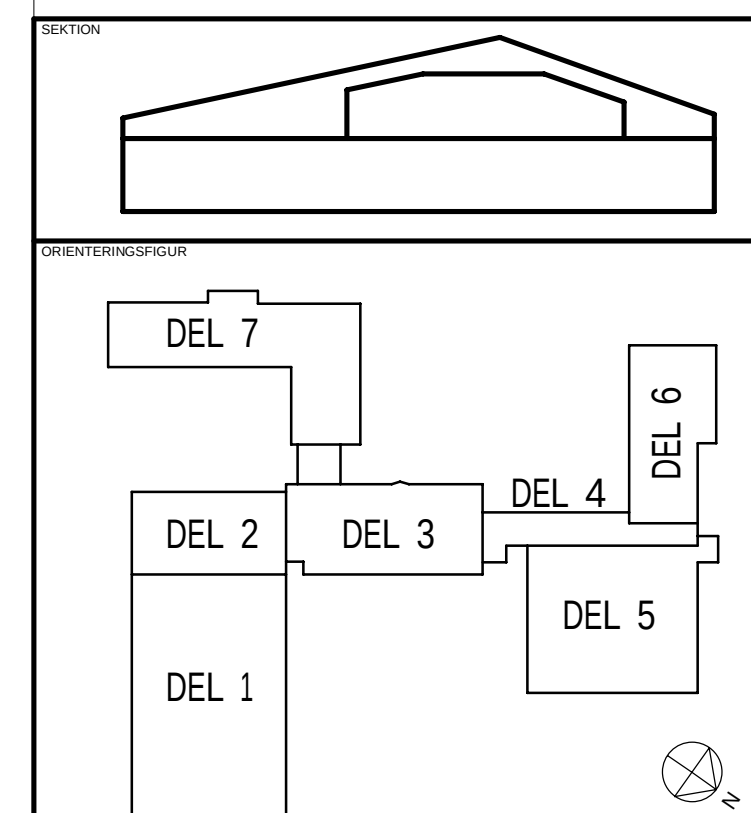

STATUS
FÖRBÄGNSINGSINDERLAG

FORFRAGNINGSSUNDL	
HANDLING	BYGGHANDLING

DATUM	GÖDKÄND AV	ANDRINGS F
2024-12-20	T. BERGSTRÖM	
BESTÄLL ADR		

INSTALLARE



PROJEKTNAMN

CENTRAALKÖK

OMRÅDE	ROBERTSFORS KOMMUN
PROJEKTHÄNSKED	ADRESS

PROJEKTNUMMER	ADRESS
	YTTRE RINGVÄGEN 4
DIARIENUMMER	FASTIGHET
	FÖRÖNDET 1

	FORDONET 1
DISCIPLIN A	FORETAG NORCONSULT SVERIGE

UPPDRAGSNUMMER	SKAPAD AV
108 83 71	CHE
TELEFON	KONTAKTPERSON

010 141 80 00	TOMAS BERGSTROM
BYGGNADSVK	PLUSHÖJD (RH 2000)

VÄNINGSPLAN	VÄNINGSDEL	DELOMRÅDE
SYSTEM		

45 HUSKOMPLETTERINGAR

RITNINGSKATEGORI	SKALA	FORMAT
PLAN, SEKTION	1:20	A1

DOKUMENTNUMMER	A-45-4-003	ÄNDRING
----------------	------------	---------