




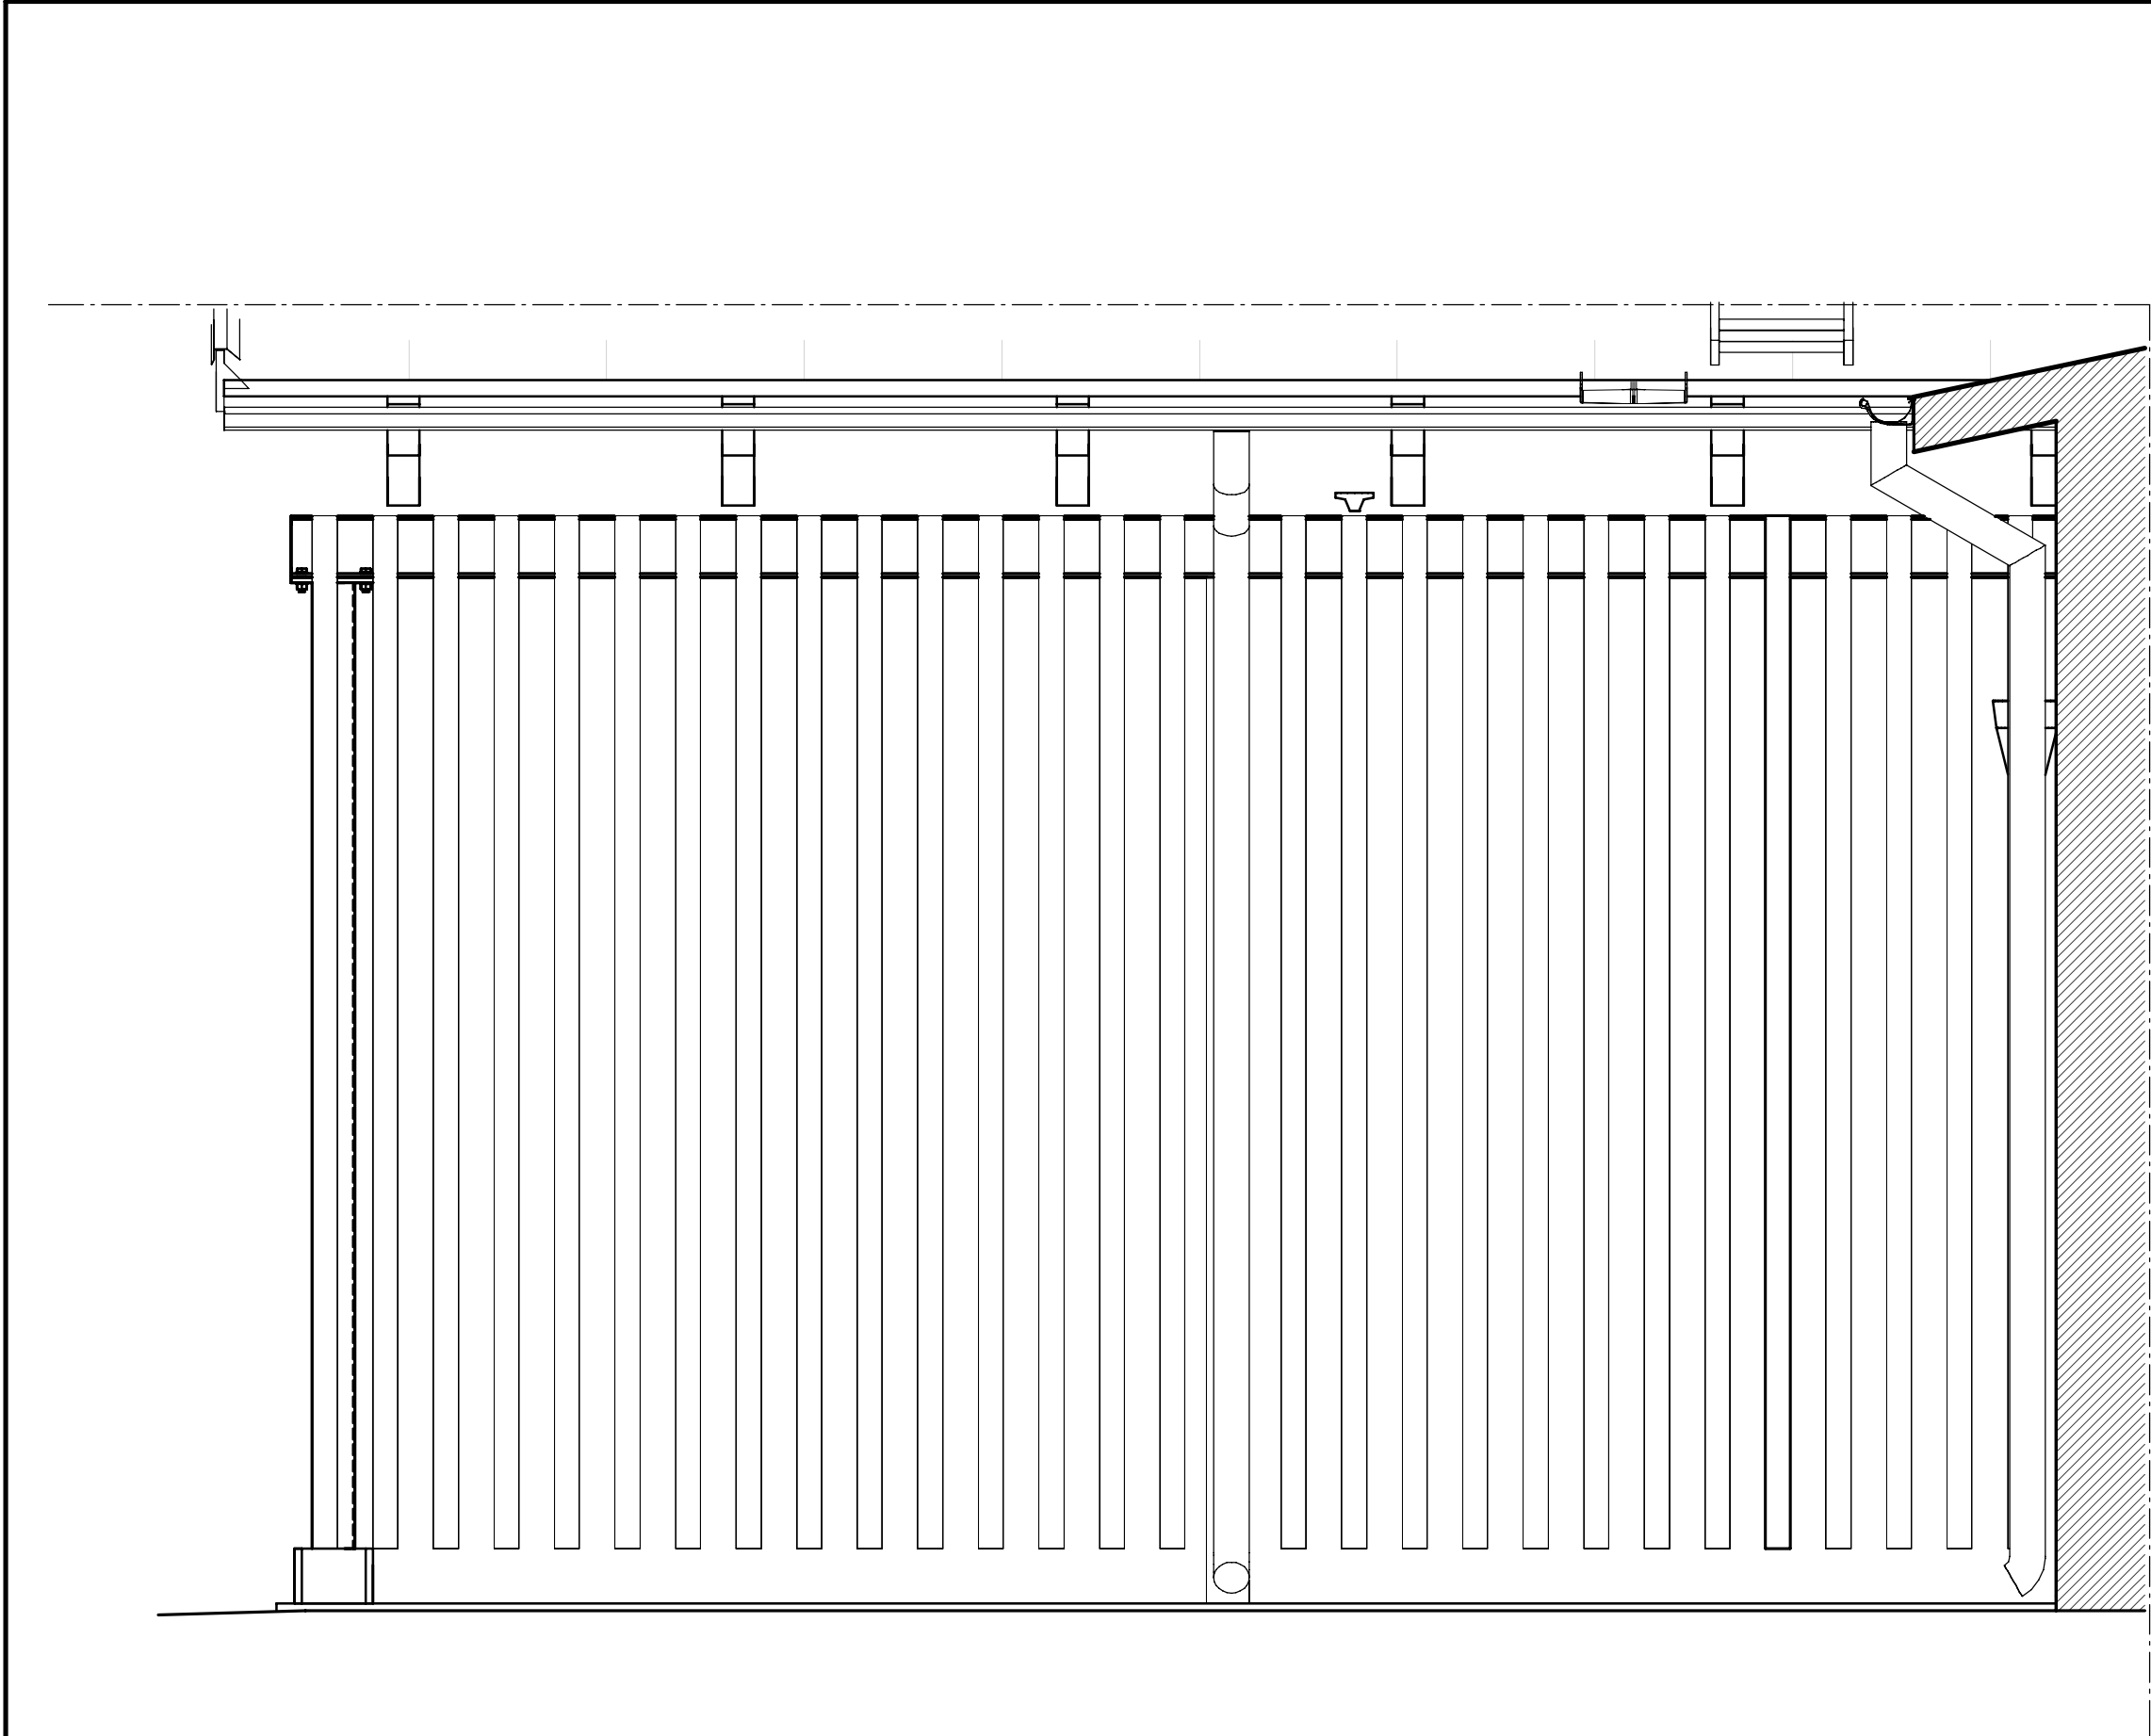


Elevation - SPALJÉ 1
1 : 20

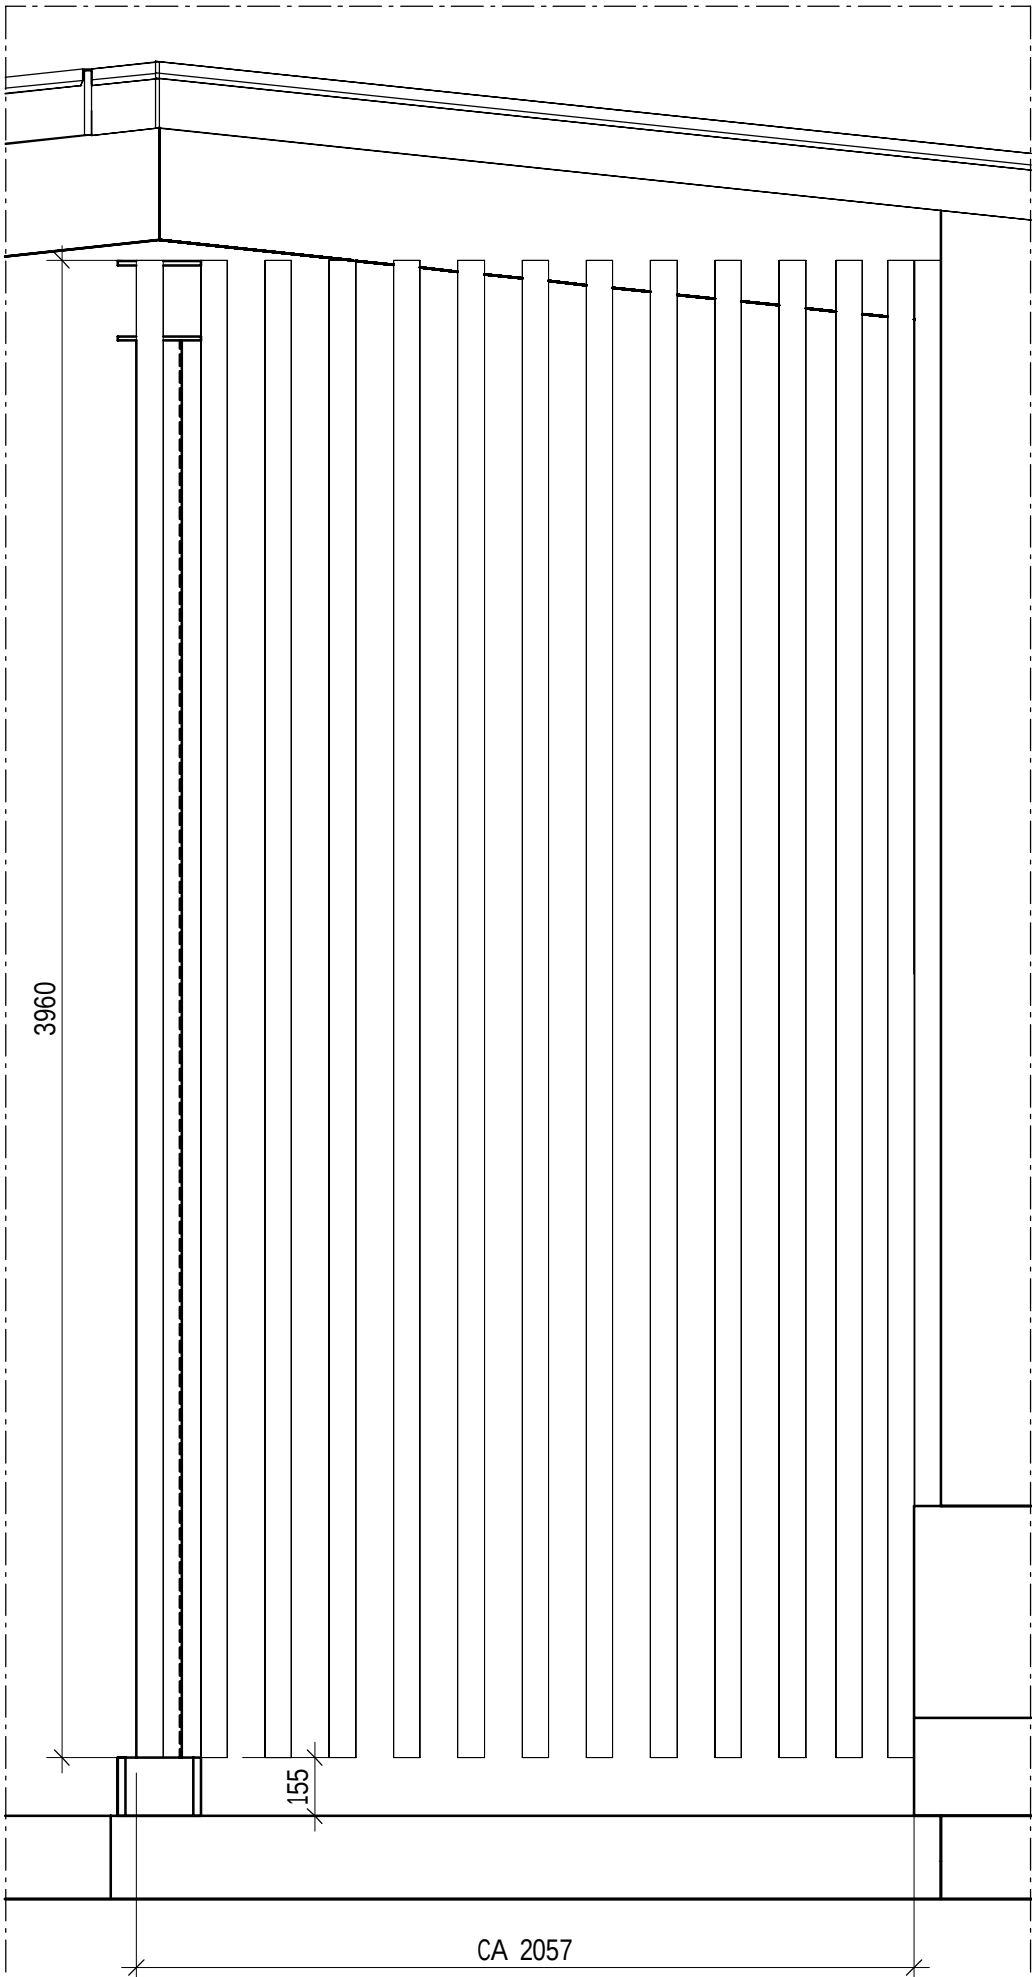


Elevation - SPALJÉ 2
1 : 20

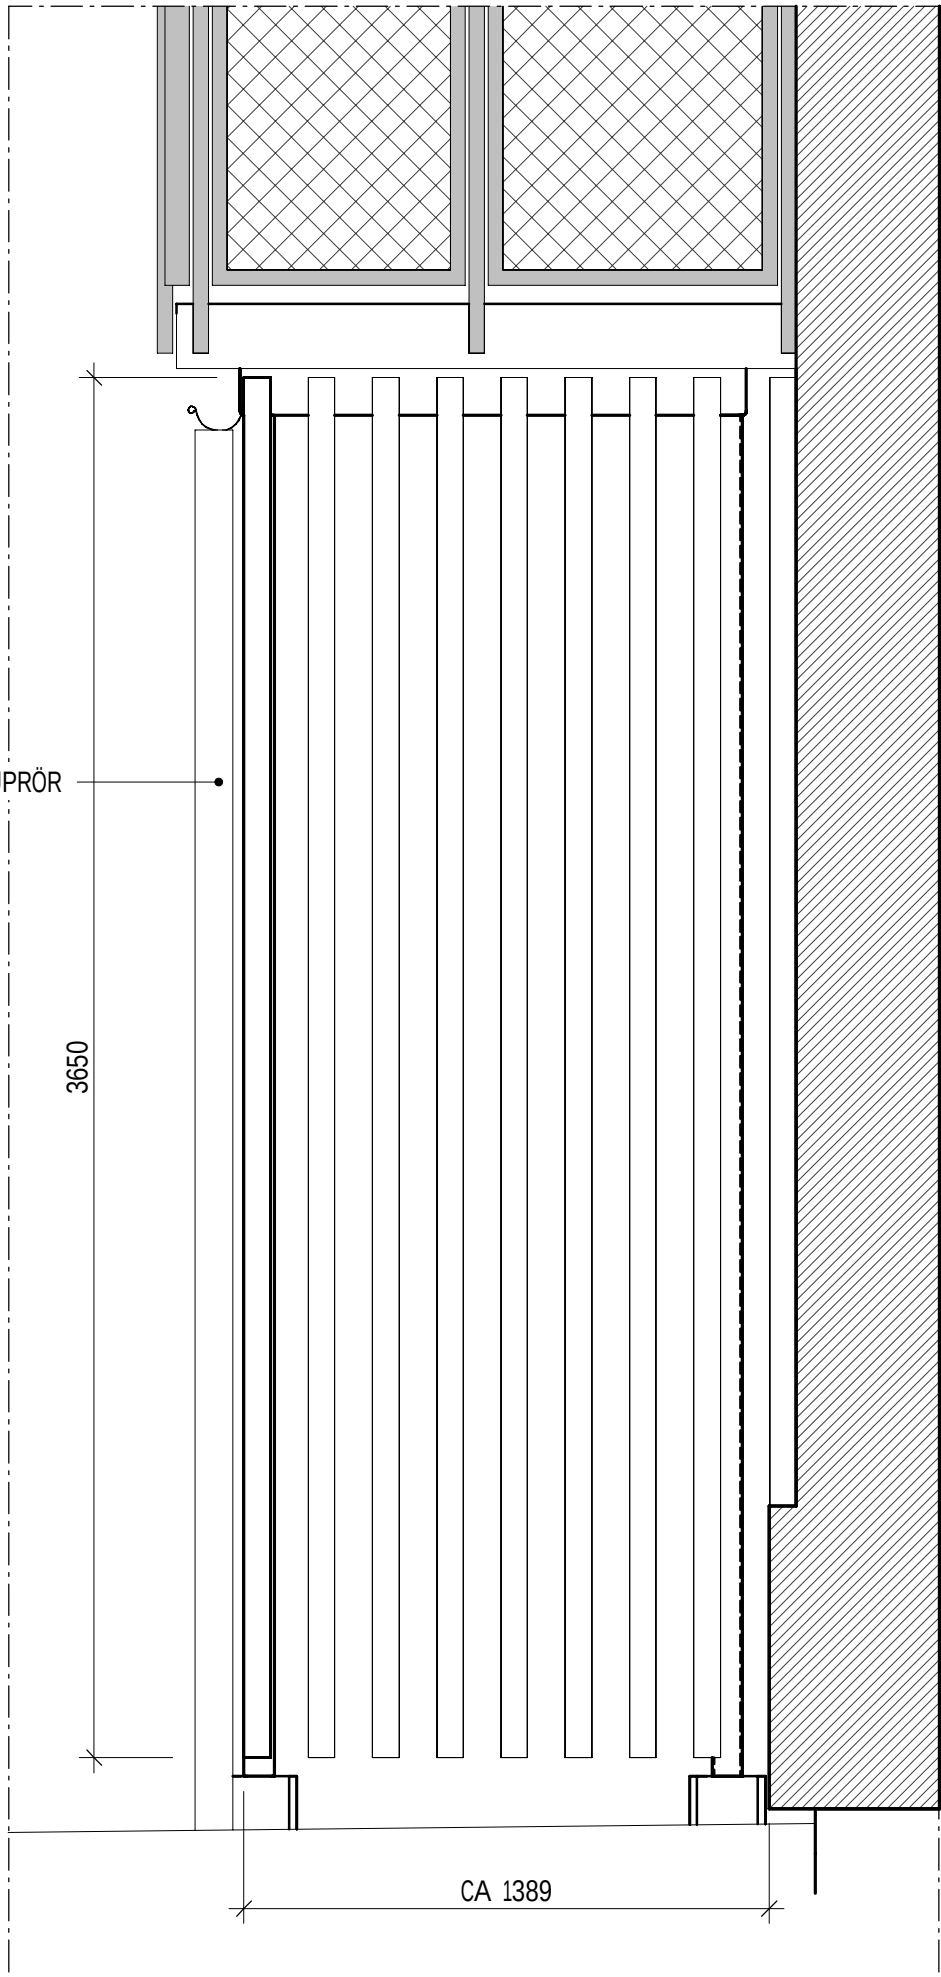




Elevation - SPALJÉ 3b
1 : 20

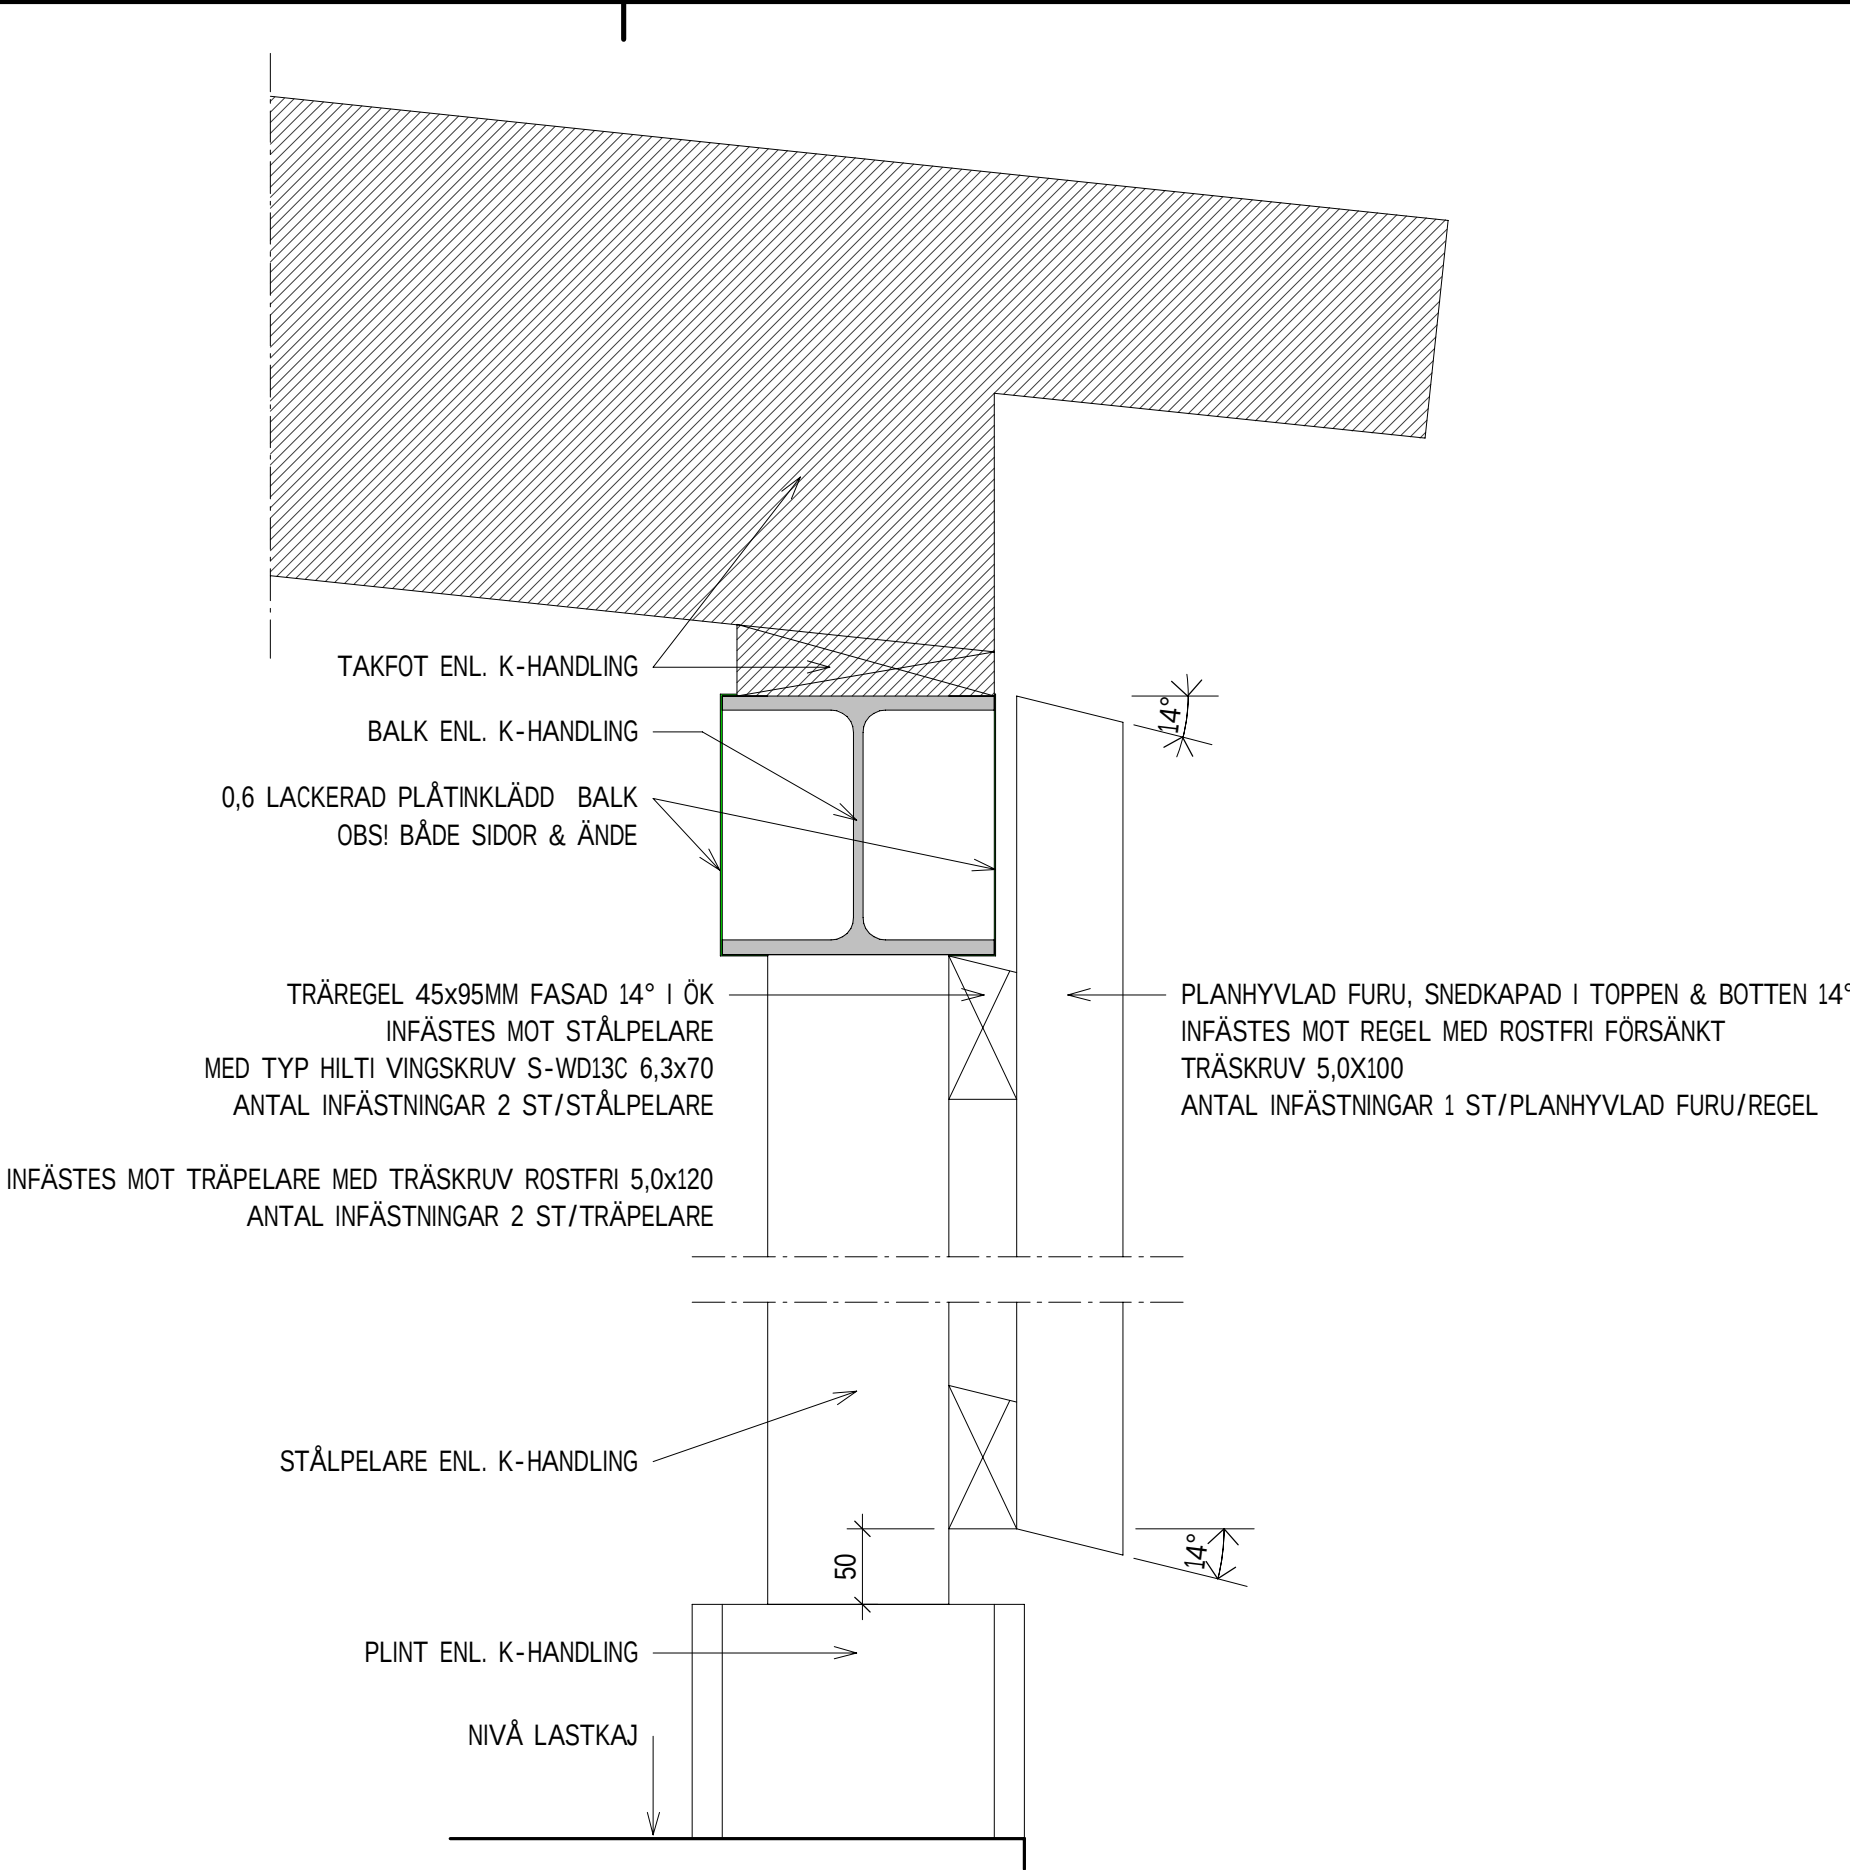

VERTIKAL PRINCIPDETALJ SPALJÉ 1
1 : 5

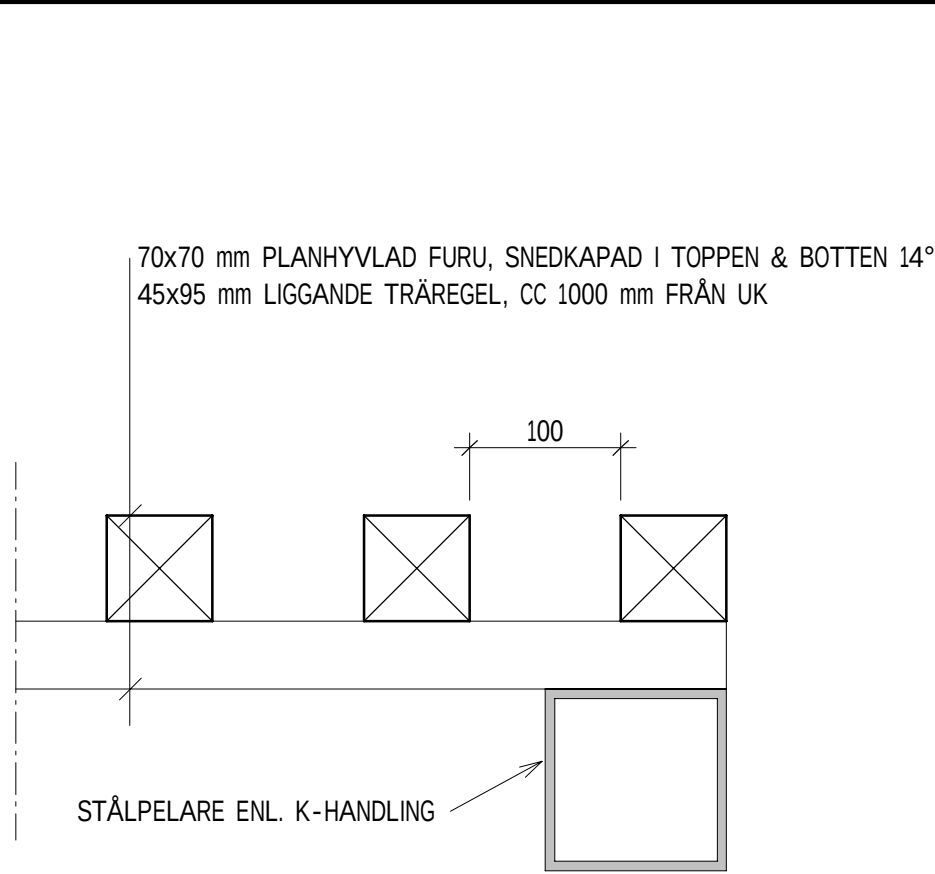

HORISONTAL PRINCIPDETALJ SPALJÉ 1
1 : 5

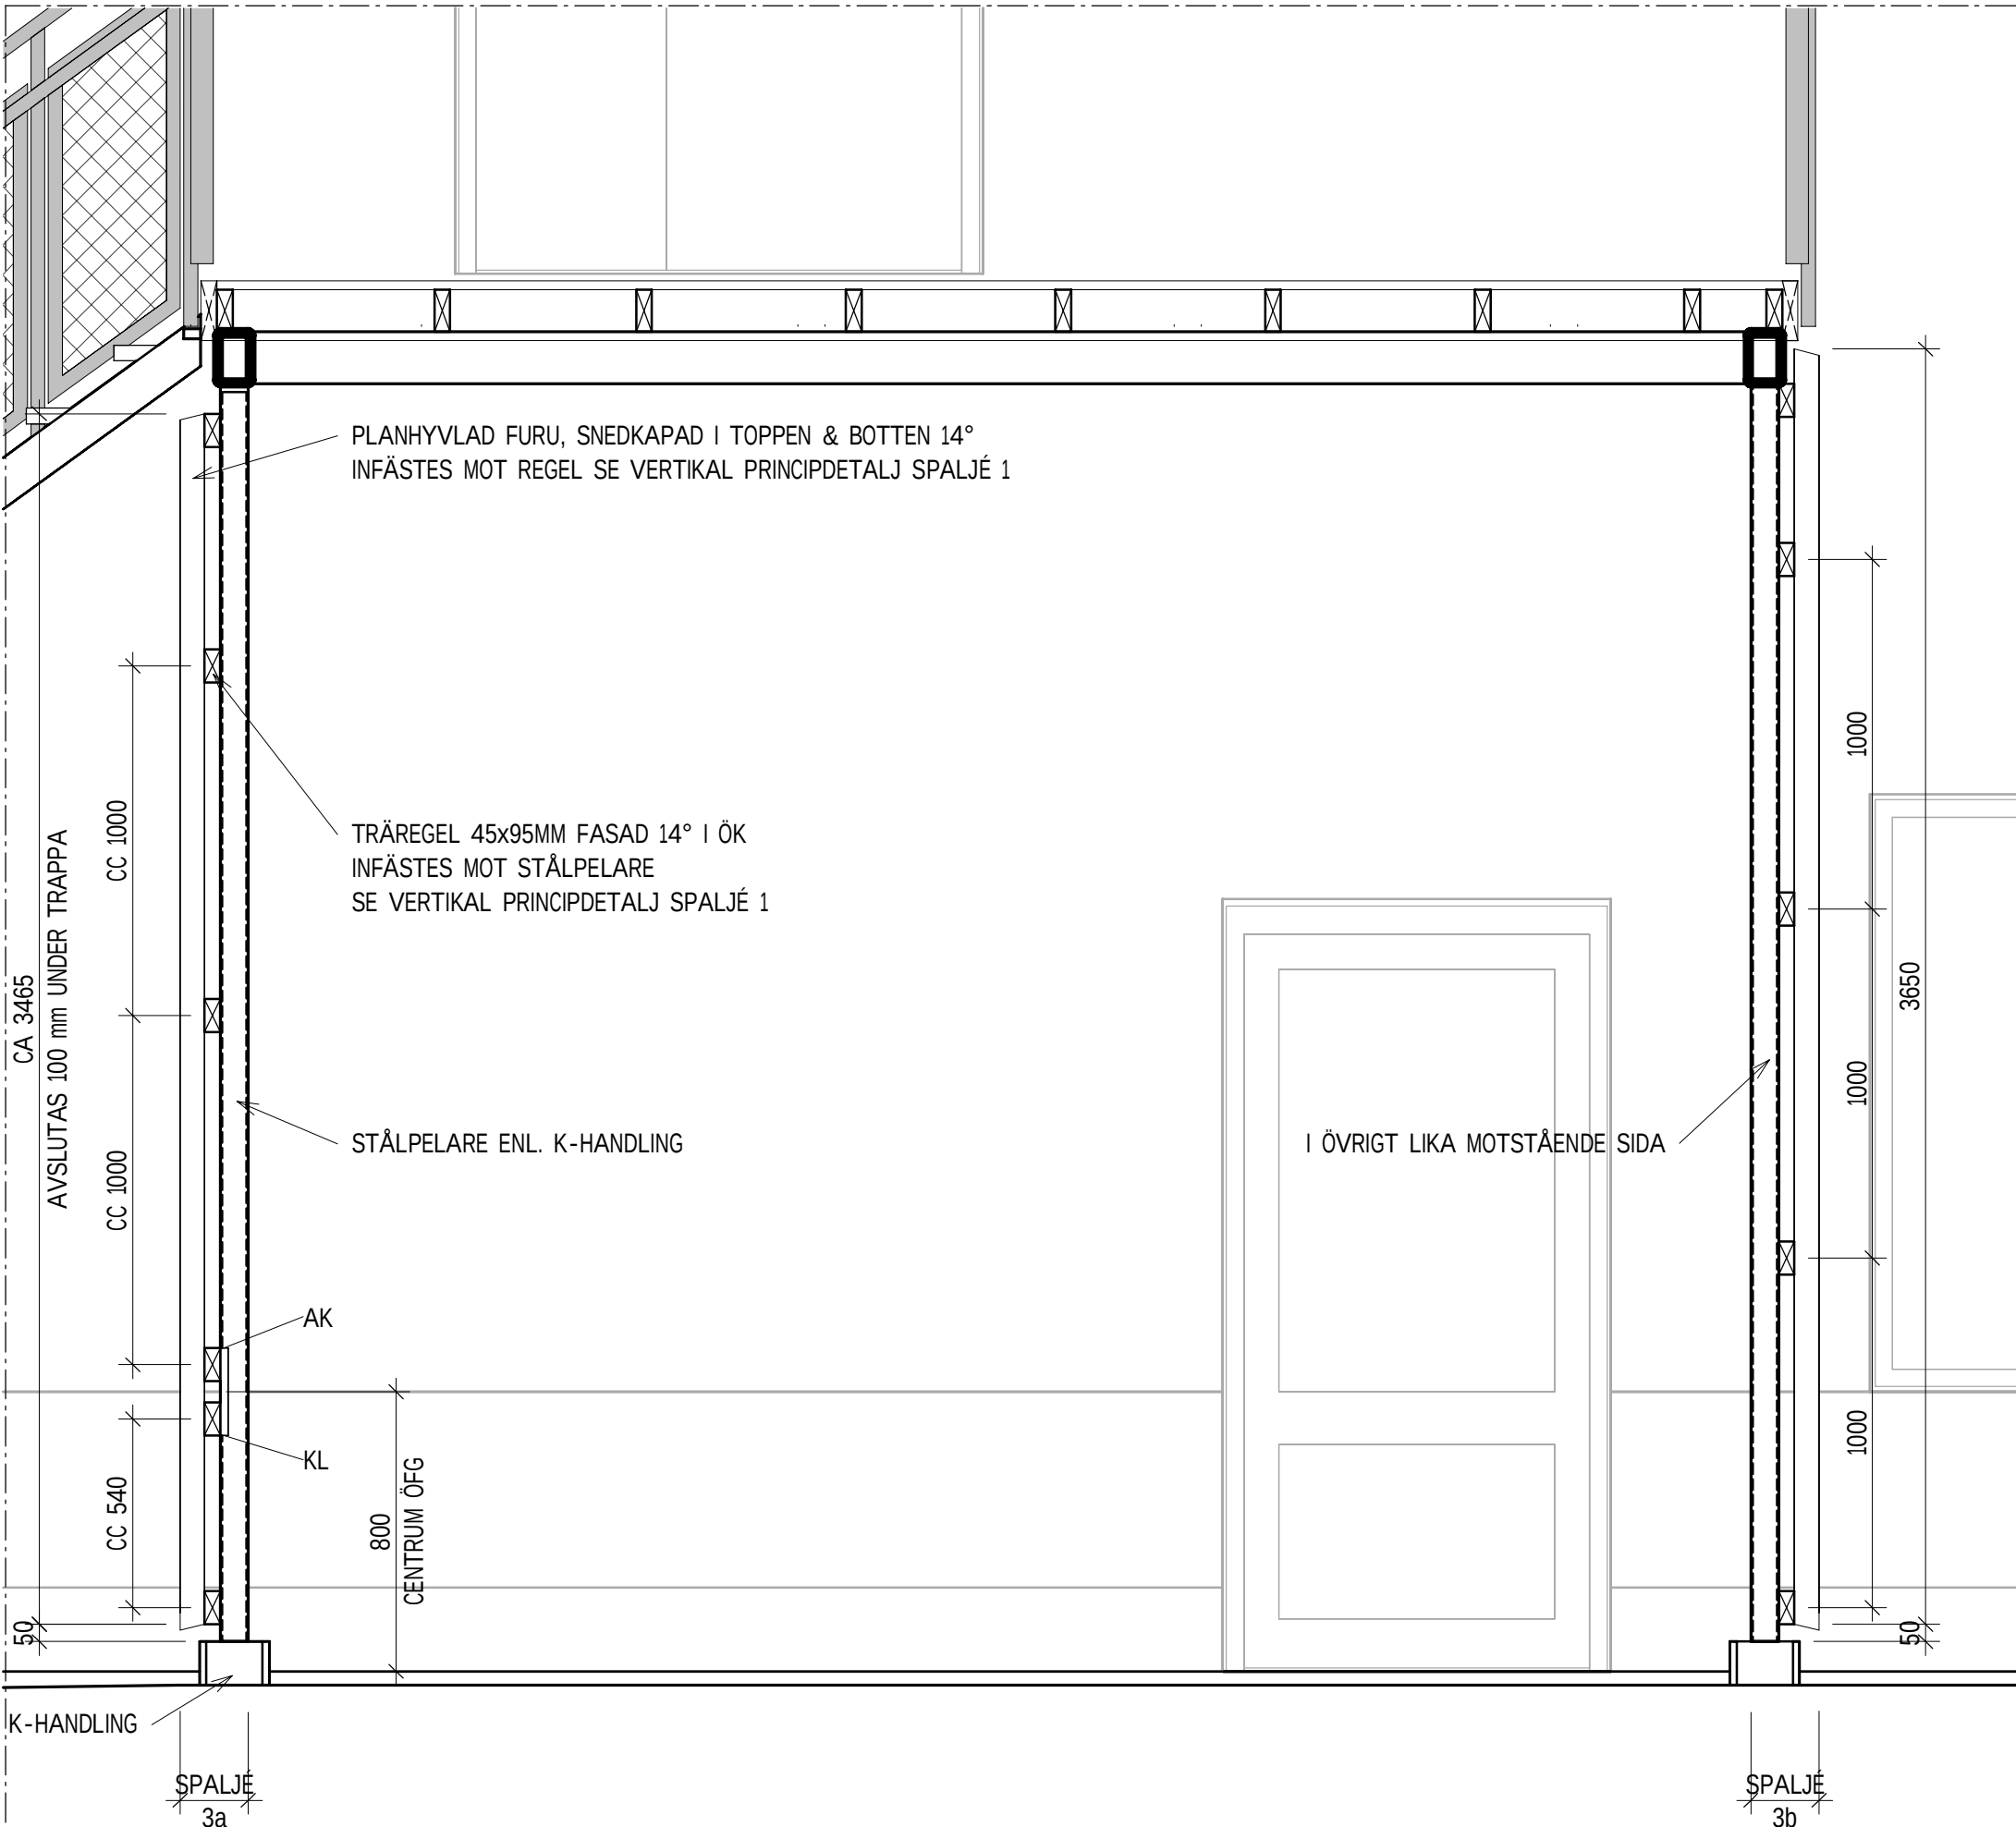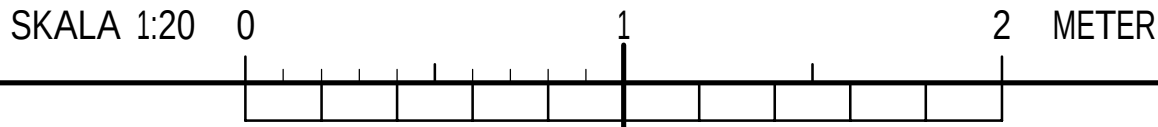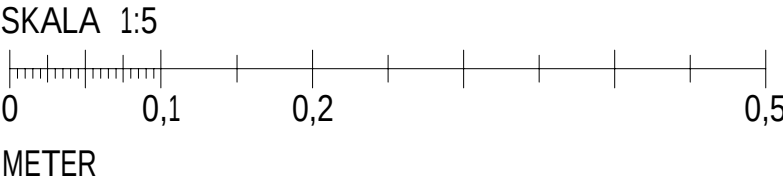

SPALJÉ 3 - SEKTION
1 : 20


FÖRKLARINGAR

Samtliga mått anges i millimeter.
Mått kontrolleras på plats innan tillverkning.

FÖRESKRIFTER

HÄNVISNINGAR

PLAN - ÖVERSIKT, BRAND A-40-1-001

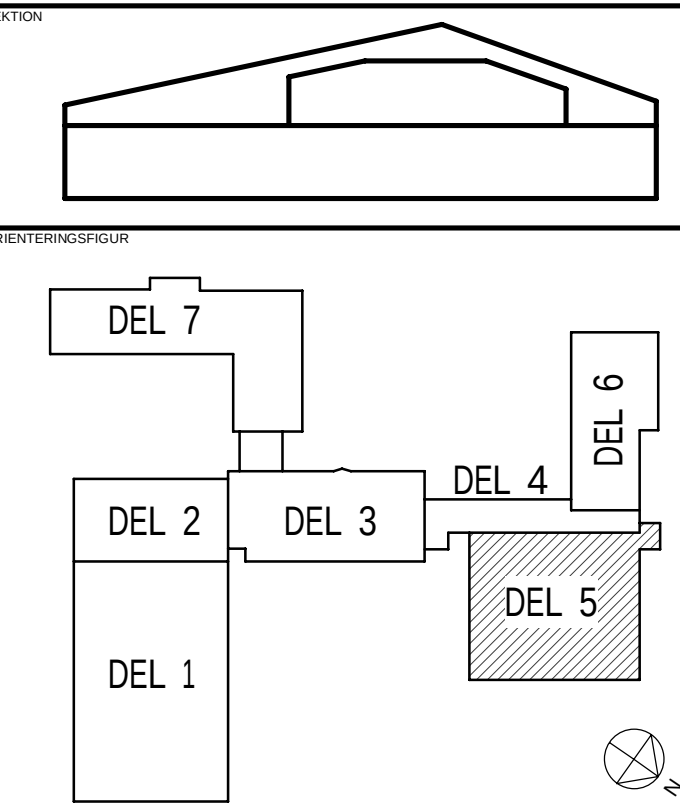

STATUS

FÖRFRÅGNINGSUNDERLAG

BYGGHANDLING

DATUM: 2024-12-20 FÖRFRÅGAD AV: T. BERGSTRÖM

BESTÄLLARE: ROBERTSFORS KOMMUN



PROJEKTNAMN

ROBERTSFORS KOMMUN

PROJEKTNUMMER: YTTRE RINGVÄGEN 4

DOKUMENTNUMMER: FORDONET 1

DISCIPLIN: NORCONSULT SVERIGE AB

UPPRORGSNUMMER: 108 83 71

TELEFON: 010 141 80 00

STYGGRAVSTYR: TOMAS BERGSTRÖM

VÄNINGSPLAN: VÄNINGSDEL: DELOMRÅDE:

SYSTEM: 45 HUSKOMPLETTERINGAR

SPECIFIKATION: SPALJÉ

UPPSTÄLLNING: SKALA: 1:20, 1:5

FORMAT: A1

DOCUMENTNUMMER: A-45-0-004